



MIKROPILOTY

PŘÍČNÝ ŘEZ P1-P1 km 0,640 000 1:25

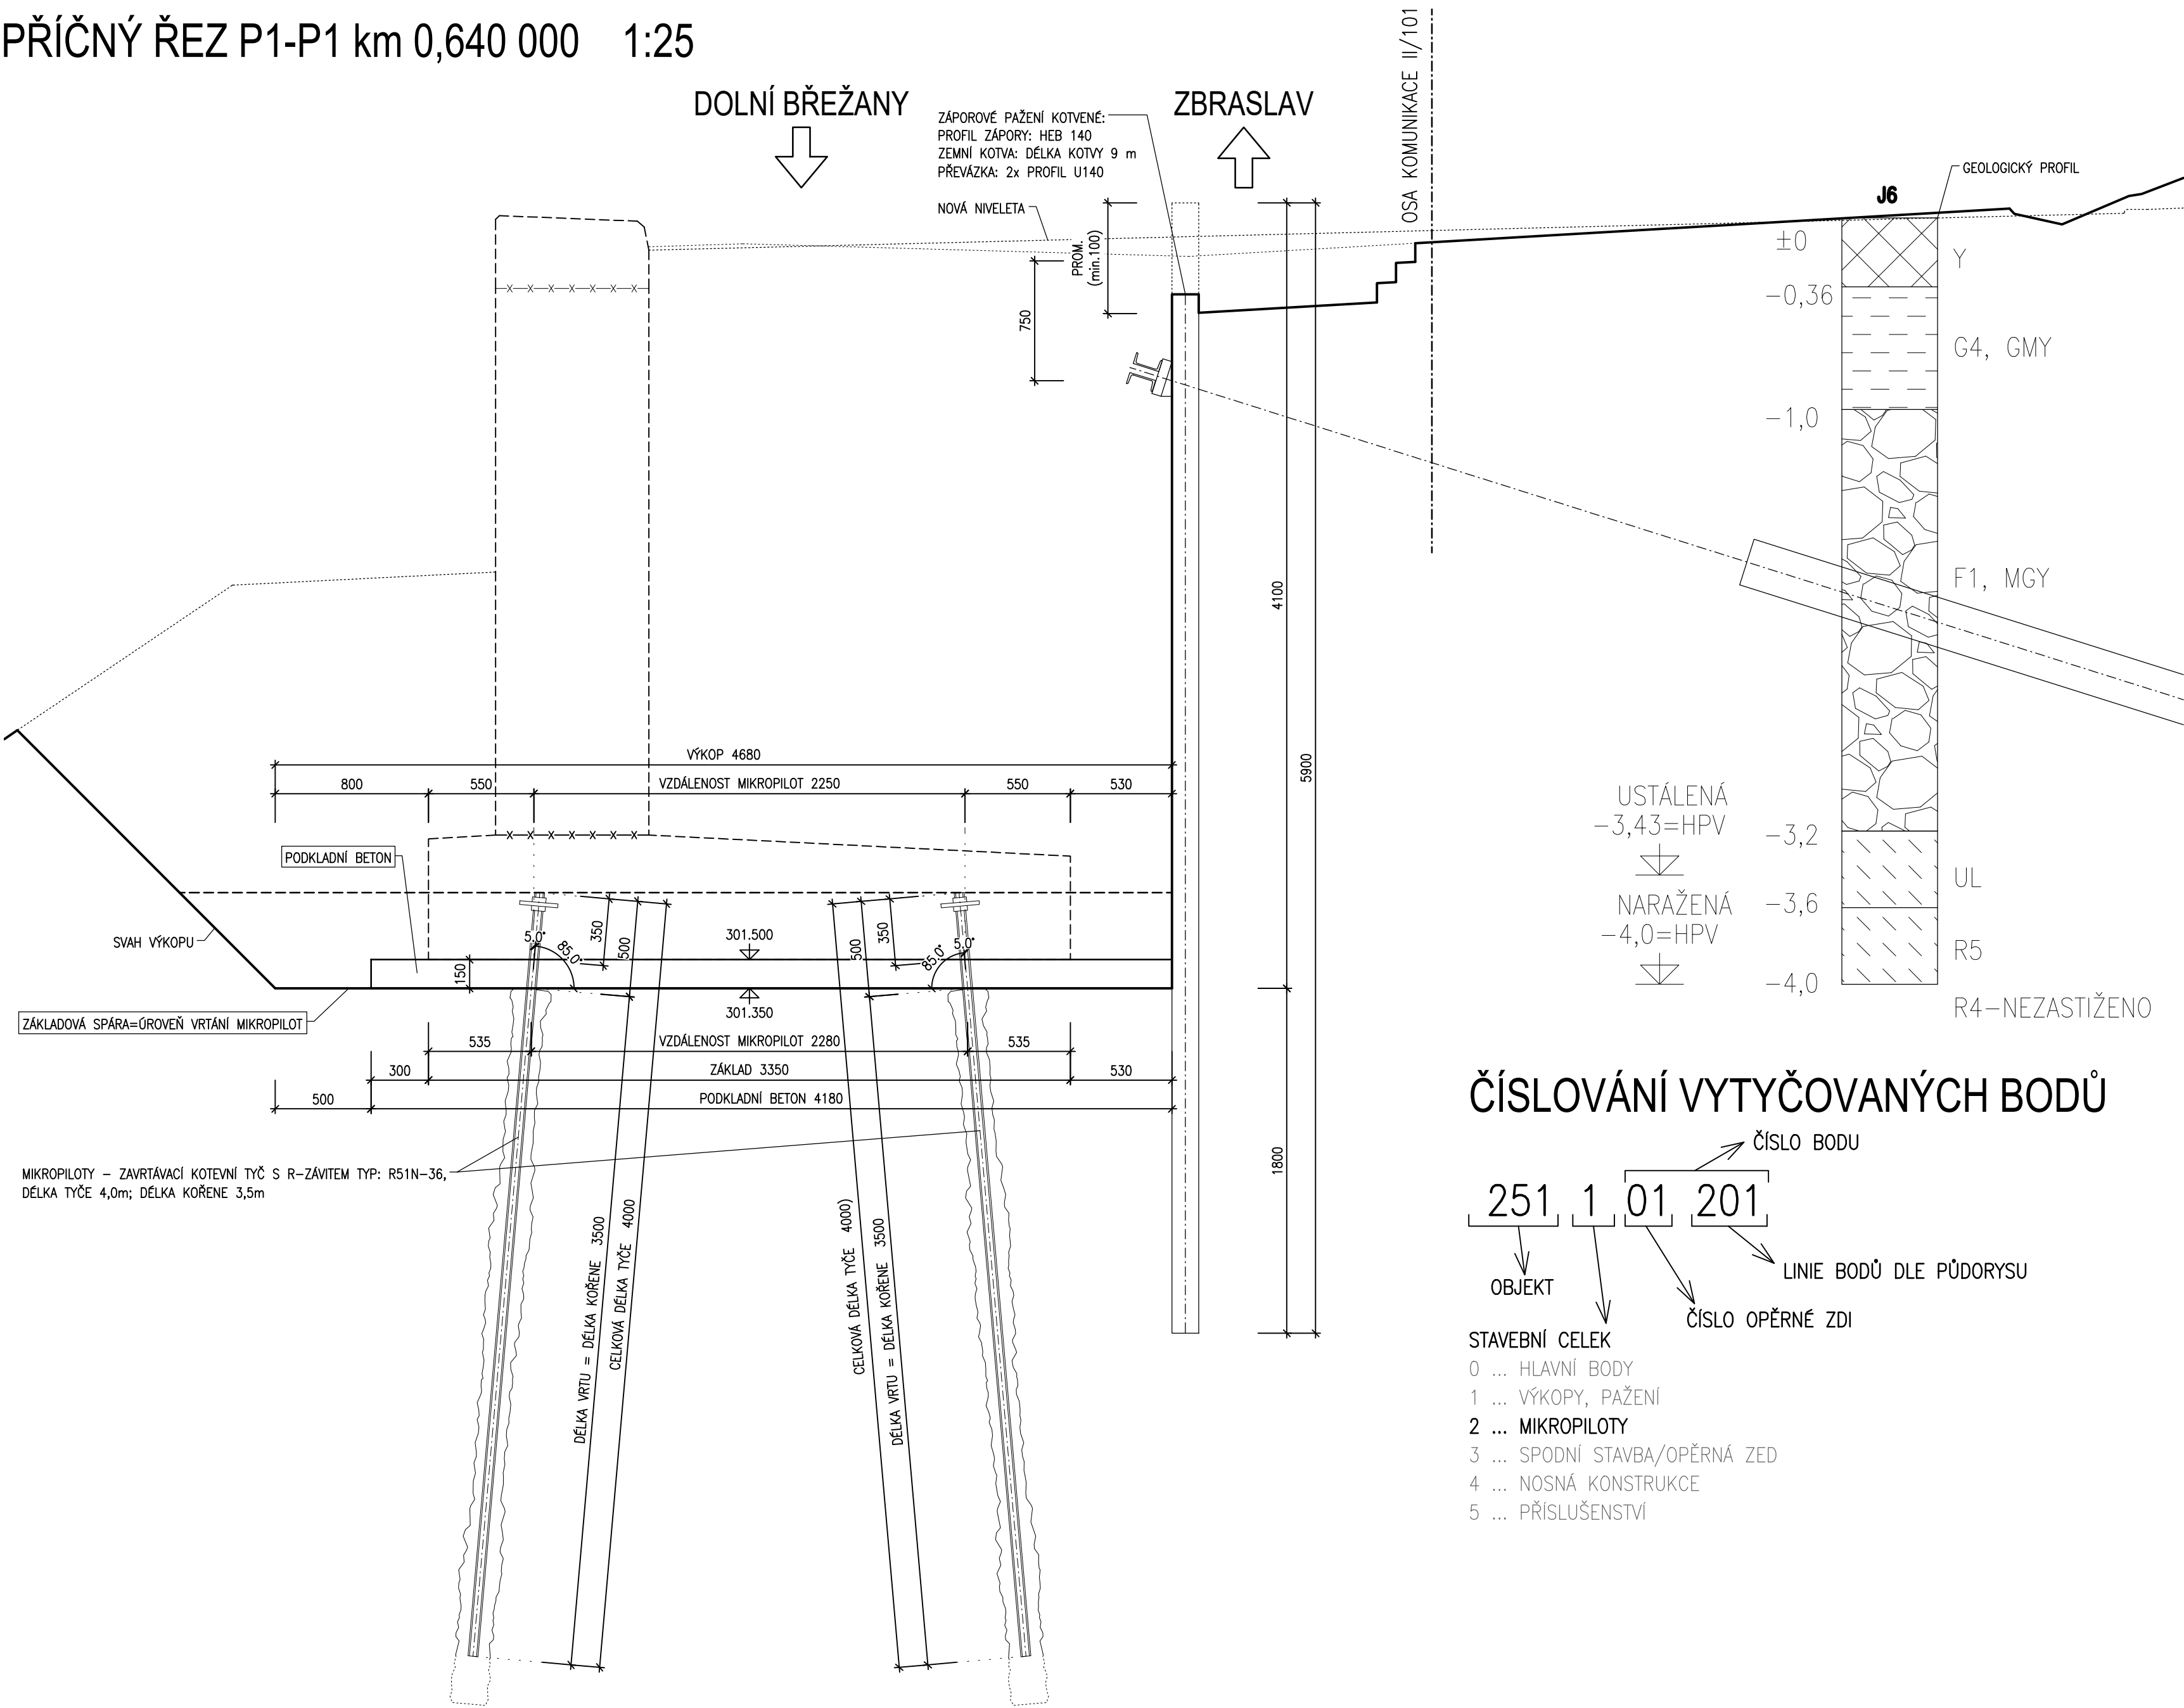

ČÍSLOVÁNÍ VYTÝČOVANÝCH BODŮ

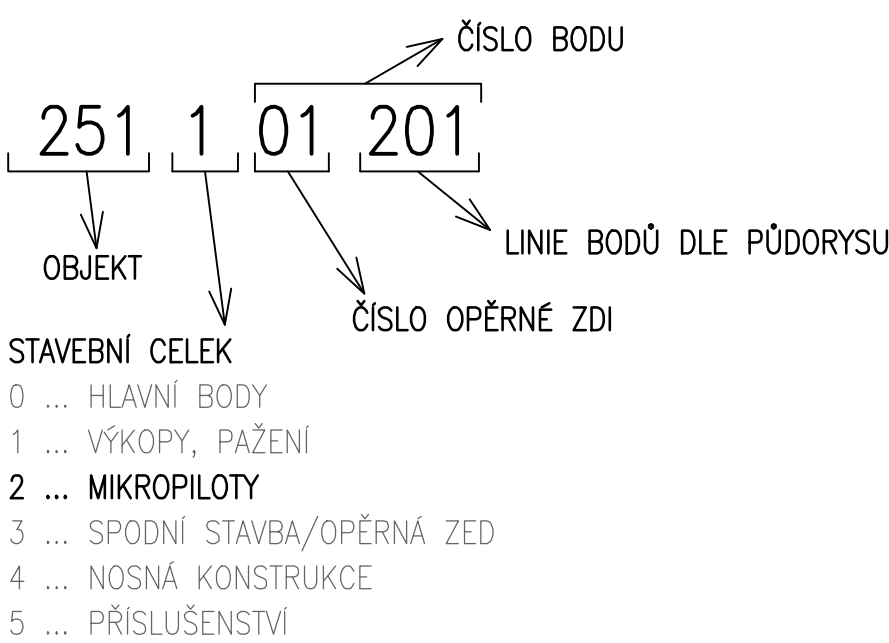

VÝKAZ MATERIÁLU

MIKROPILOTY OPĚRNÁ ZEĎ 03						
VÝKAZ MATERIÁLU						
OZN.	POPIS	DÉLKA [m]	HMOTNOST [kg/m]	POČET [ks]	DÉLKA CELKEM [m]	HMOTNOST [kg]
1	TYČ Ø51mm	4,00	7,7	1	4,000	30,80
3	PLECH 200/200,TL. 20mm	-	6,28	1	-	6,28

HMOTNOST CELKEM ... PRO 1 TYČ DL. 4.0 m	37,08 kg
---	----------

HMOTNOST CELKEM ... PRO VŠECH 32 TYČÍ	1186,56 kg
---------------------------------------	------------

POZNÁMKA:
- JE VYKÁZÁNA CELKOVÁ DÉLKA TYČE 4,0 m VČETNĚ PŘESAHU 0,35 m DO ZÁKLADU


MATERIÁL

CEMENTOVÁ SUSPENZE INJEKTAŽNÍ CEM 32,5R, C25/30

POZNÁMKY


- ZHOTOVITEL JE POVINEN PRO VŠECHNY ZEMĚMĚŘICKÉ PRÁCE POSTUPOVAT DLE TKP KAP. 1, ODS. 1.6.3.
- PRO MIKROPILOTY BUDOU POUŽITY INJEKČNÍ ZAVRTÁVACÍ KOTVNÍ TYČE SDA, TYP R51N-36
- MIKROPILOTY JSOU VYTÝČENY V ÚROVNI ZÁKLADOVÉ SPÁRY, TZN. V DOLNÍ ÚROVNI POKLADNÍHO BETONU.
- PRO PŘÍPADNÉ SPOJOVÁNÍ BUDOU POUŽITI ORIGINÁLNÍ SPOJNÍKY
- SA MOZAVRTÁVACÍ TYČ BUDE UKONČENA DESKOU 200x200x20 mm A Z OBOU STRAN STAŽENA MATICEMI
- VŠECHNY MIKROPILOTY JSOU ŠIKMÉ 5°
- PROVÁDĚNÍ MIKROPILOT MUSÍ BÝT V SOULADU S ČSN EN 14199.
- CEMENTOVÁ SUSPENZE MUSÍ MÍT FINÁLNÍ PEVNOST MIN. C25/30
- PRO ČERPÁNÍ VODY ZE DNA ZÁKLADOVÉ SPÁRY BUDOU ZBUDOVÁNY JÍMKY.

PŮDORYS 1:100

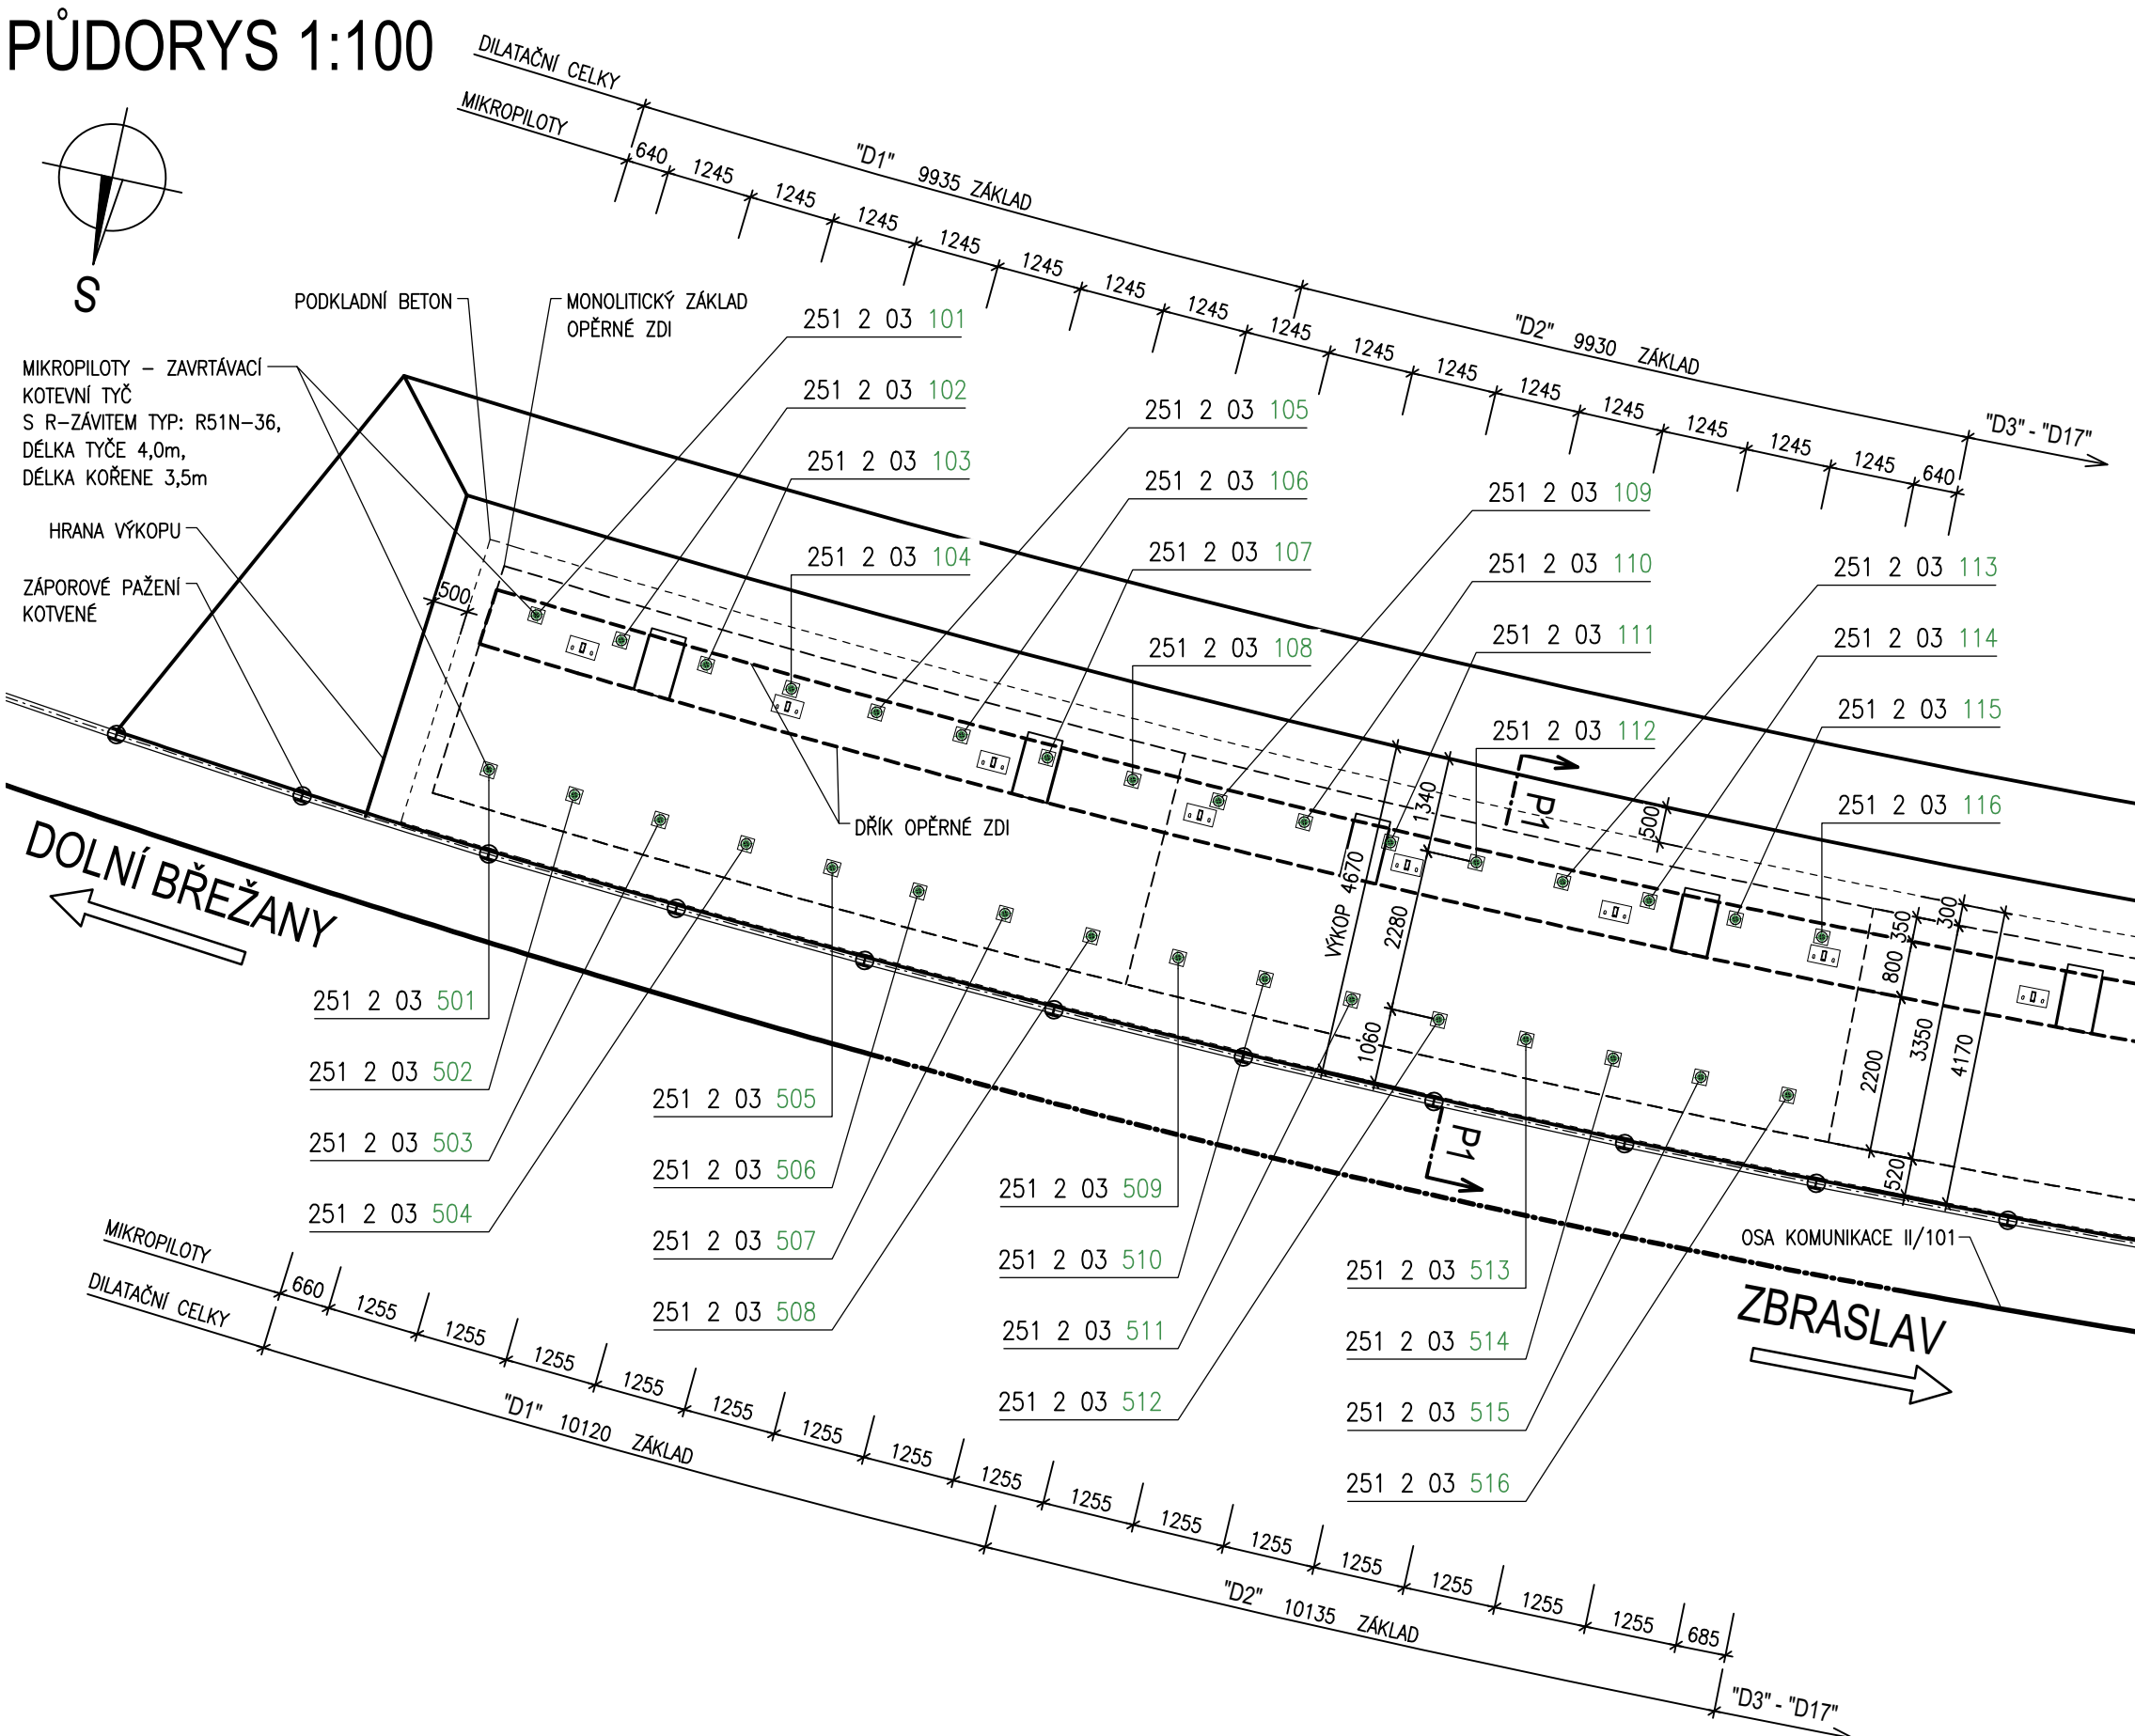


DETAIL UKONČENÍ MIKROPILOTY 1:5

POHLED

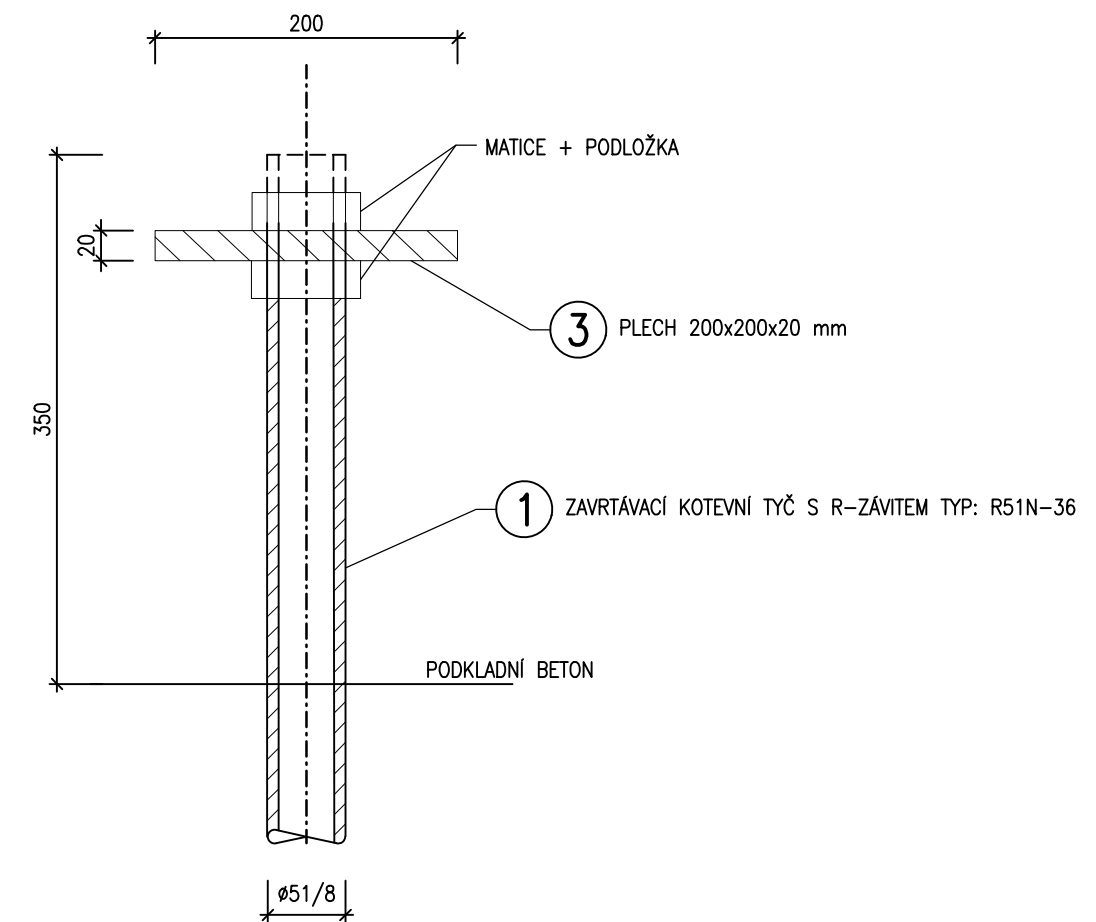

PŮDORYS

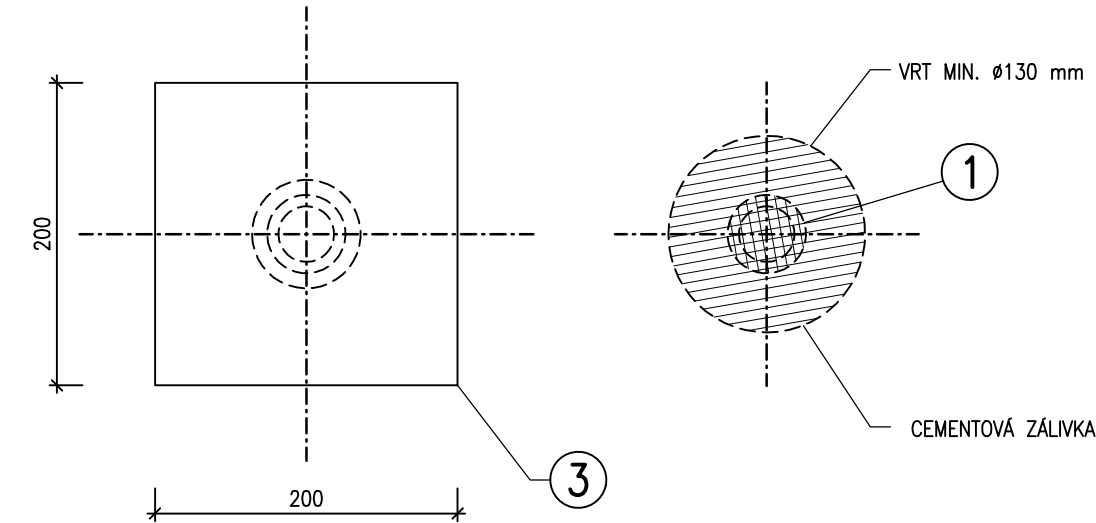

PŘEDKONCEPT

OZNAČ.	TEXT ZMĚNY - ODŮVODNĚNÍ	DATUM	PODPIS
TABULKA ZMĚN			

Název stavby	II/101 Dolní Břežany - Zbraslav	ČÍSLO OBJEKTU	SO 251.2
--------------	---------------------------------	---------------	----------

Objednatel stavby	Krajská správa a údržba silnic Středočeského kraje, příspěvková organizace Zborovská 81/11, 150 21 Praha 5-Smíchov
-------------------	--

Autorský dozor	GeoTec-GS, a.s. Chmelová 2920/6, 106 00 Praha 10
----------------	--

Technický dozor investora	TES + SGS + SGG vedoucí sdružení: TES Consulting, s.r.o. V Olšinách 2300/75, 100 00 Praha 10-Strašnice	RAZÍTKO	DATUM	PODPIS
---------------------------	--	---------	-------	--------

Zhotovitel stavby	M-SILNICE a.s. Husova 1697, 530 03 Pardubice www.msilnice.cz	RAZÍTKO	DATUM	PODPIS
-------------------	--	---------	-------	--------

Koordinátor RDS	M - PROJEKCE s. r. o. Reslova 956/13, 500 02 Hradec Králové www.m-projekce.cz	RAZÍTKO	DATUM	PODPIS
-----------------	---	---------	-------	--------

Souladnicový systém: S-JTSK	Výškový systém: Bpv
Zpracovatel stavebního objektu/části:	Projekční kancelář PRIS spol. s r.o. Osová 717/20, 625 00 Brno-Starý Lískovec www.pris.cz

Vypracoval: Ilena Syňková	Hlavní inženýr projektu: Ing. Jiří Ehrenberger	Razítko: PRIS
Odpovědný projektant: Ing. Martin Reuhla	Kontroloval: Ing. Jiří ŠRUBAŘ	PROJEKČNÍ KANCELÁŘ PRIS spol. s r. o. OSOVA 20, 625 00 BRNO
Číslo zakázky: 25139	Datum: 06/2026	

Objekt/část: SO 251.2 - OPĚRNÉ ZDI ZEĎ č. 03	Měřítko: 1:100, 1:25, 1:5	Souprava:
Příloha: MIKROPILOTY	Stupeň: RDS	Číslo přílohy: 102_MIK