



TVAR OPĚRNÉ ZDI - POHLEDY - ČÁST 1

POHLED V LÍCI B1-B1 1:50

ÚSEK "1"

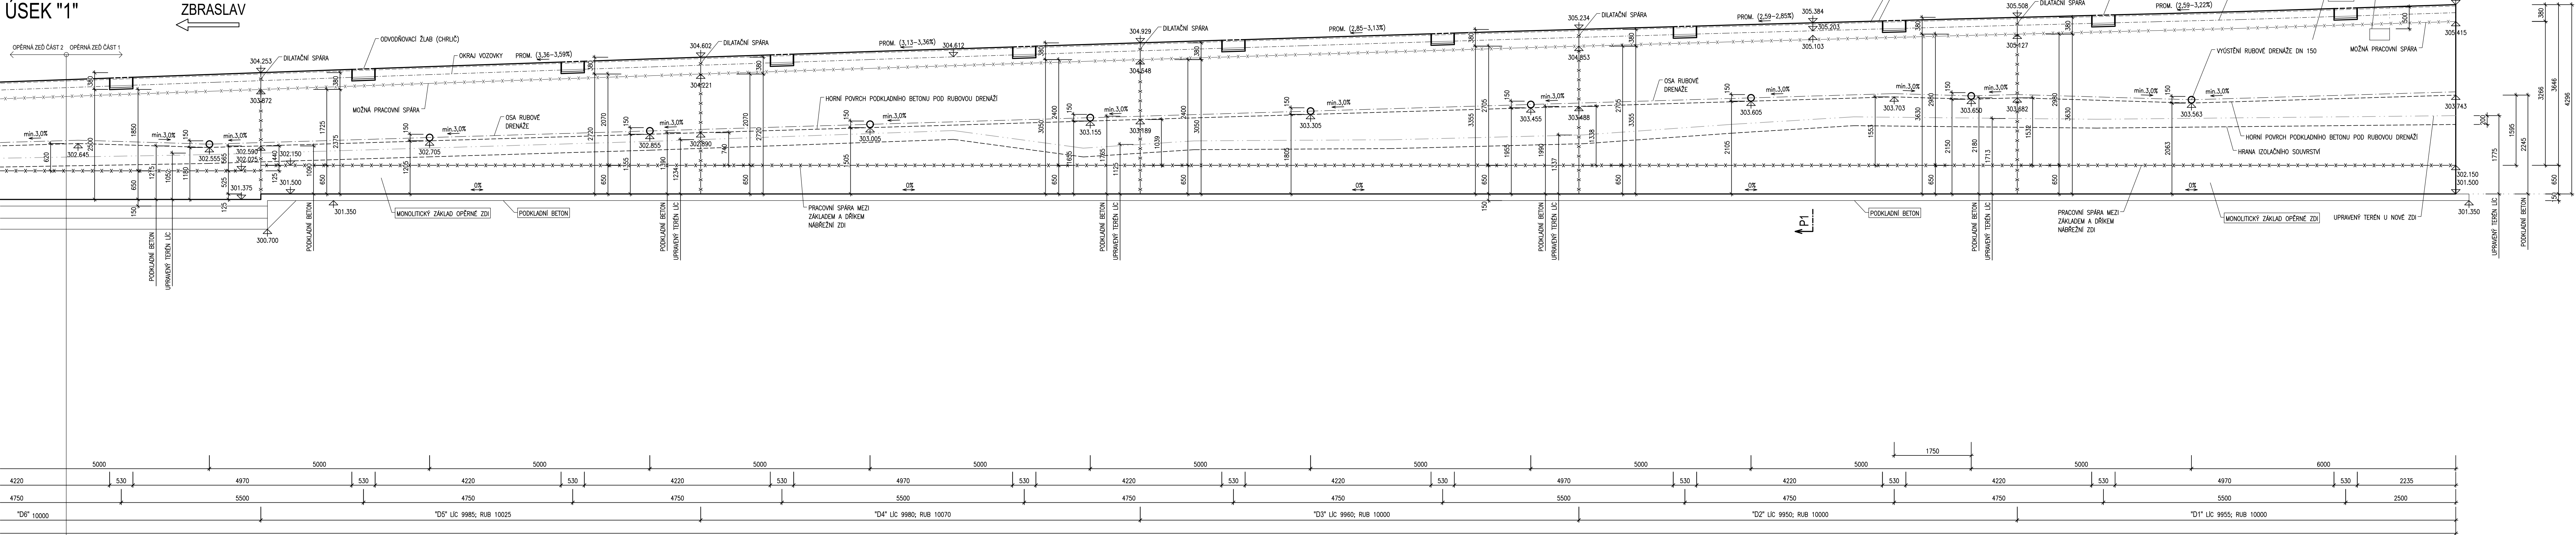

ÚSEK "2"

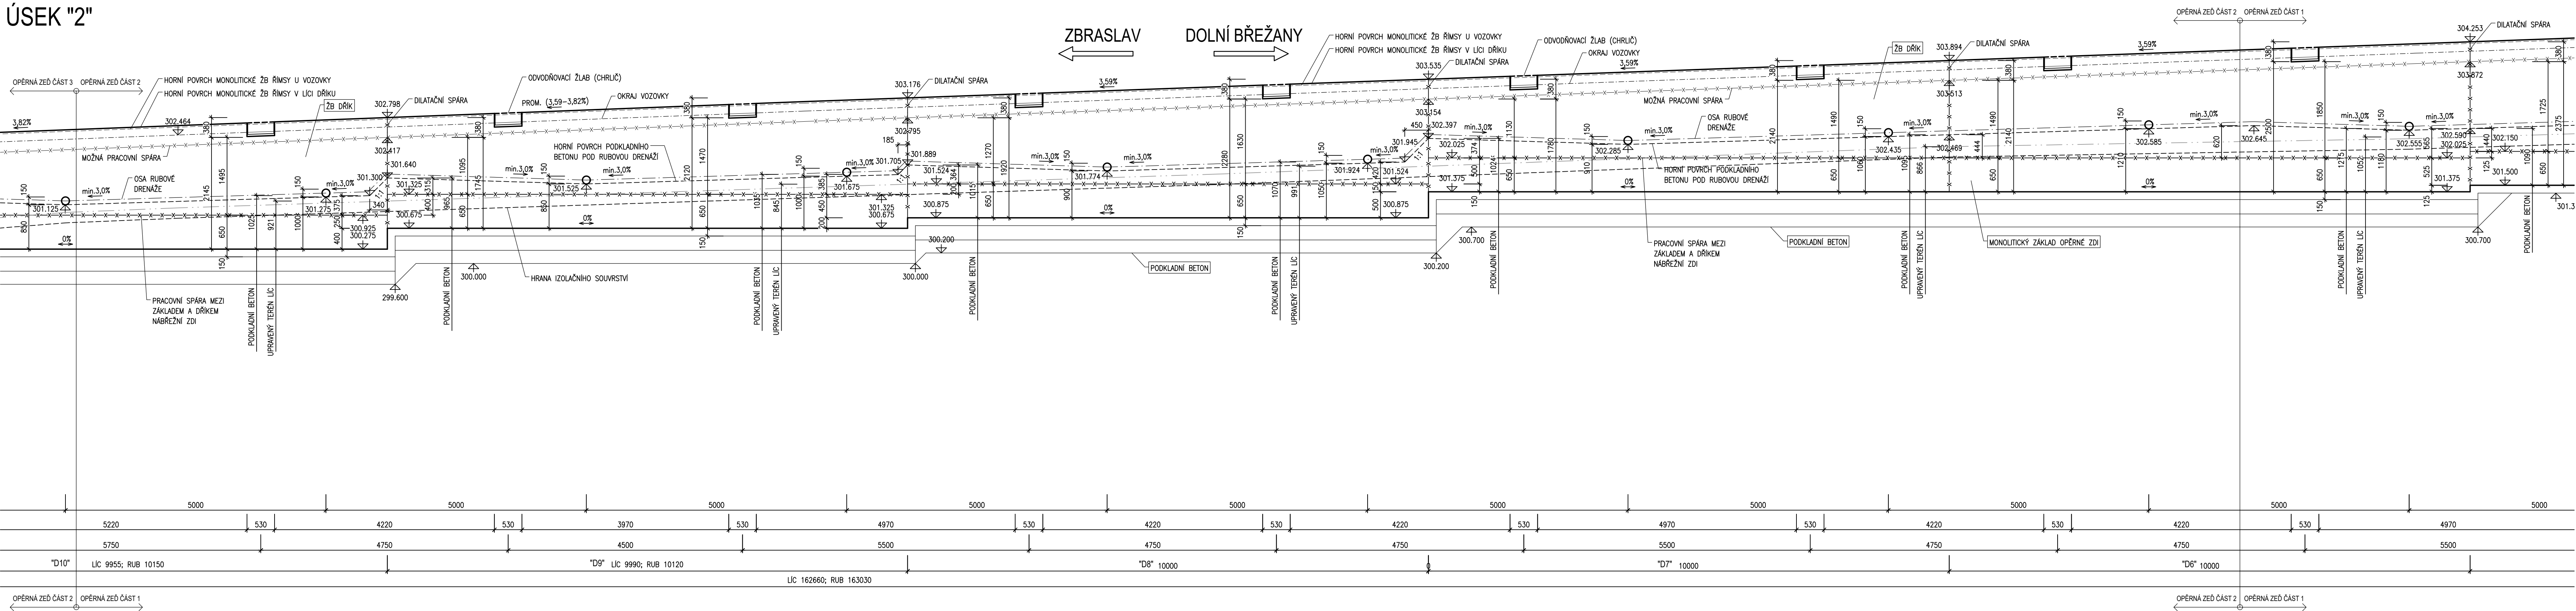

KONCEPT

|   |                         |                                                                                       |        |  |  |
|---|-------------------------|---------------------------------------------------------------------------------------|--------|--|--|
|   |                         |                                                                                       |        |  |  |
| OZNAC.   | TEXT ZMĚNY - ODŮVODNĚNÍ | DATUM                                                                                 | PODPIS |  |  |
| TABULKA ZMĚN   |                         |                                                                                       |        |  |  |
| Název stavby   |                         | ČÍSLO OBJEKTU                                                                         |        |  |  |
| II/101 Dolní Břežany - Zbraslav   |                         | SO 251.2                                                                              |        |  |  |
| Objednatel stavby   |                         |                                                                                       |        |  |  |
|  <div>Krajská správa a údržba silnic<br/>Středočeského kraje, příspěvková organizace<br/>Zborovská 611/11, 150 21 Praha 5-Smíchov</div> |                         |                                                                                       |        |  |  |
| Autorský dozor   |                         |                                                                                       |        |  |  |
|   |                         | GeoTec-GS, a.s.<br>Chmelová 2520/6, 106 00 Praha 10                                   |        |  |  |
| Technický dozor investora   |                         | RAZÍTKO                                                                               |        |  |  |
|  <div>TES + SGS + SGG<br/>vedoucí sdružení:<br/>TES Consulting, s.r.o.<br/>V Olšánské 2300/75, 100 00 Praha 10-Strašnice</div>          |                         | DATUM                                                                                 |        |  |  |
| PODPIS   |                         | PODPIS                                                                                |        |  |  |
| Zhotovitel stavby   |                         | RAZÍTKO                                                                               |        |  |  |
|  <div>M-SILNICE a.s.<br/>Husova 1697, 530 03 Pardubice<br/>www.msilnice.cz</div>                                                        |                         | DATUM                                                                                 |        |  |  |
| PODPIS   |                         | PODPIS                                                                                |        |  |  |
| Koordínátor RDS   |                         | RAZÍTKO                                                                               |        |  |  |
|  <div>M - PROJEKCE s. r.o.<br/>Restlova 956/13, 500 02 Hradec Králové<br/>www.m-projekce.cz</div>                                       |                         | DATUM                                                                                 |        |  |  |
| PODPIS   |                         | PODPIS                                                                                |        |  |  |
| Souřadnicový systém: S-JTSK   |                         |                                                                                       |        |  |  |
| Výškový systém: Bpv   |                         |                                                                                       |        |  |  |
| Zpracovatel stavebního objektu/části:   |                         |                                                                                       |        |  |  |
| Projektční kancelář PRIS spol. s r.o.<br>Osova 717/20, 625 00 Brno-Starý Lískovec<br>www.pris.cz   |                         |                                                                                       |        |  |  |
| Výpracoval:<br>Ing. Ondřej Vytásek   |                         | Razítko:                                                                              |        |  |  |
|   |                         |  |        |  |  |
| Odpovědný projektant:<br>Ing. Martin Rehnika   |                         | PROJEKČNÍ KANCELÁŘ PRIS spol. s r. o.<br>OSOVA 20, 625 00 BRNO                        |        |  |  |
|   |                         |                                                                                       |        |  |  |
| Číslo zakázky:<br>251130   |                         | Datum:<br>05/2026                                                                     |        |  |  |
| Objekt/část:   |                         | Měřítko:                                                                              |        |  |  |
| SO 251.2 - OPĚRNÉ ZDI   |                         | 1:50                                                                                  |        |  |  |
| ZED č. 03   |                         | Stupeň:                                                                               |        |  |  |
| Příloha:   |                         | RDS                                                                                   |        |  |  |
| TVAR OPĚRNÉ ZDI - POHLEDY - ČÁST 1   |                         | Číslo přílohy:                                                                        |        |  |  |
|   |                         | 103_TV1R1                                                                             |        |  |  |