



TVAR OPĚRNÉ ZDI - POHLEDY - ČÁST 2

POHLED V LÍCI B1-B1 1:50

ÚSEK "3"

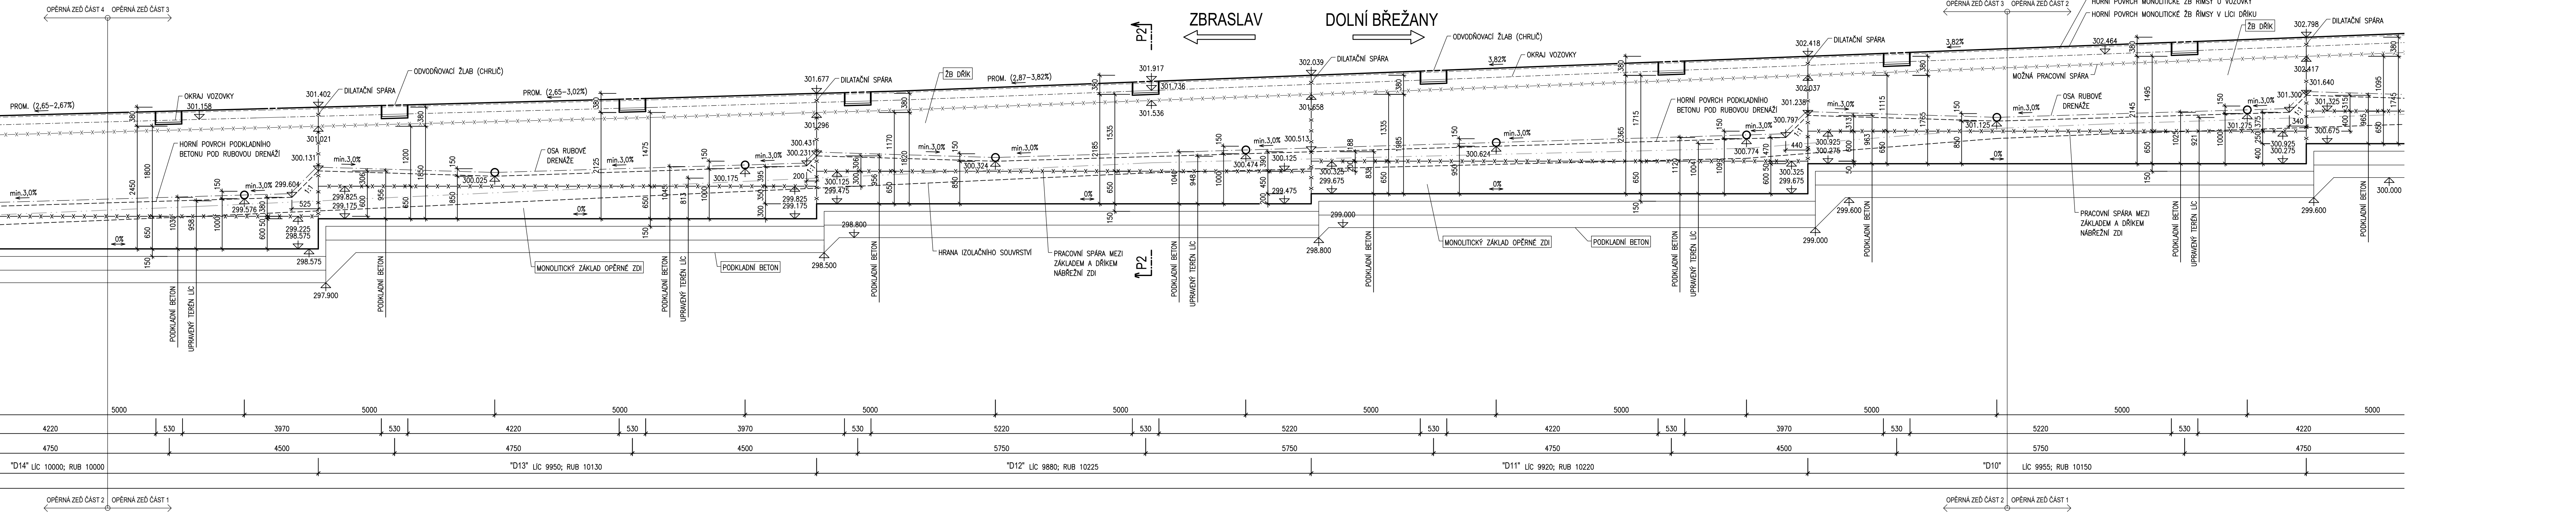

ÚSEK "4"

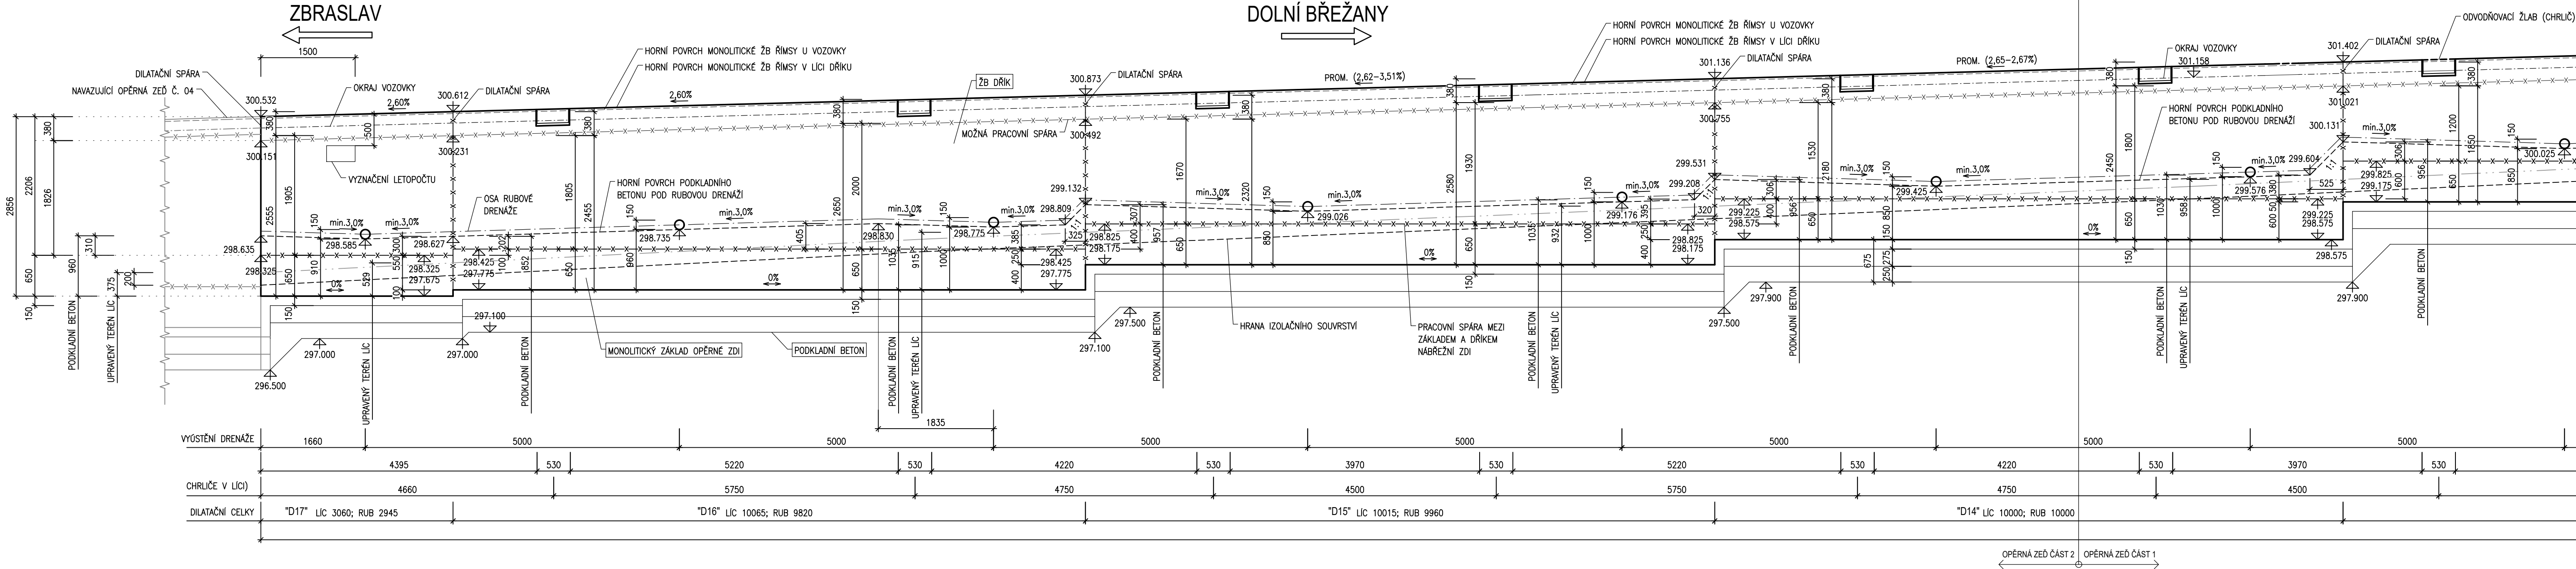

KONCEPT

OZNAČ.	TEXT ZMĚNY - ODŮVODNĚNÍ	DATUM	PODPIS
TABULKA ZMĚN			

Název stavby

II/101 Dolní Břežany - Zbraslav

ČÍSLO OBJEKTU

SO 251.2

Objednatel stavby

**Ksús**
KRAJSKÁ SPRÁVA A ÚDRŽBA SILNIC

Krajská správa a údržba silnic
Středočeského kraje, příspěvková organizace
Zborovská 81/11, 150 21 Praha 5-Smíchov

Autorský dozor

**GeoTec GS**

GeoTec-GS, a.s.
Chmelová 2920/6, 106 00 Praha 10

Technický dozor investora

**TES**
CONSULTING

TES + SGS + SGG
vedoucí sdružení:
TES Consulting, s.r.o.
V Olšinách 2300/75, 100 00 Praha 10-Stránská

RAZÍTKO

DATUM

PODPIS

Zhotovitel stavby

**M-SILNICE**

M-SILNICE a.s.
Husova 1697, 530 03 Pardubice
www.msilnice.cz

RAZÍTKO

DATUM

PODPIS

Koordinátor RDS

**M-PROJEKCE**

M - PROJEKCE s. r. o.
Reslova 956/13, 500 02 Hradec Králové
www.m-projekce.cz

RAZÍTKO

DATUM

PODPIS

Souřadnicový systém: S-JTSK

Výškový systém: Bpv

Zpracovatel stavebního objektu/části:

Projekční kancelář PRIS spol. s r.o.
Osova 717/20, 625 00 Brno-Starý Lískovec
www.pris.cz

Vypracoval: Ing. Ondřej Vytásek
Odpovědný projektant: Ing. Martin Rehnika
Číslo zakázky: 25139

Hlavní inženýr projektu: Ing. Jiří Ehrenberger
Kontroloval: Ing. Jiří ŠRUBAR
Datum: 05/2026

Razítko: **PRIS**
PROJEKČNÍ KANCELÁŘ PRIS spol. s r. o.
OSOVA 20, 625 00 BRNO

Objekt/část:

SO 251.2 - OPĚRNÉ ZDI
ZED č. 03

Měřítko: 1:50

Stupeň: RDS

Příloha: TVAR OPĚRNÉ ZDI - POHLEDY - ČÁST 2

Číslo přílohy: 104_TV2

Souprava: