



PŪDORYS 1:100 ŪSEK "1"

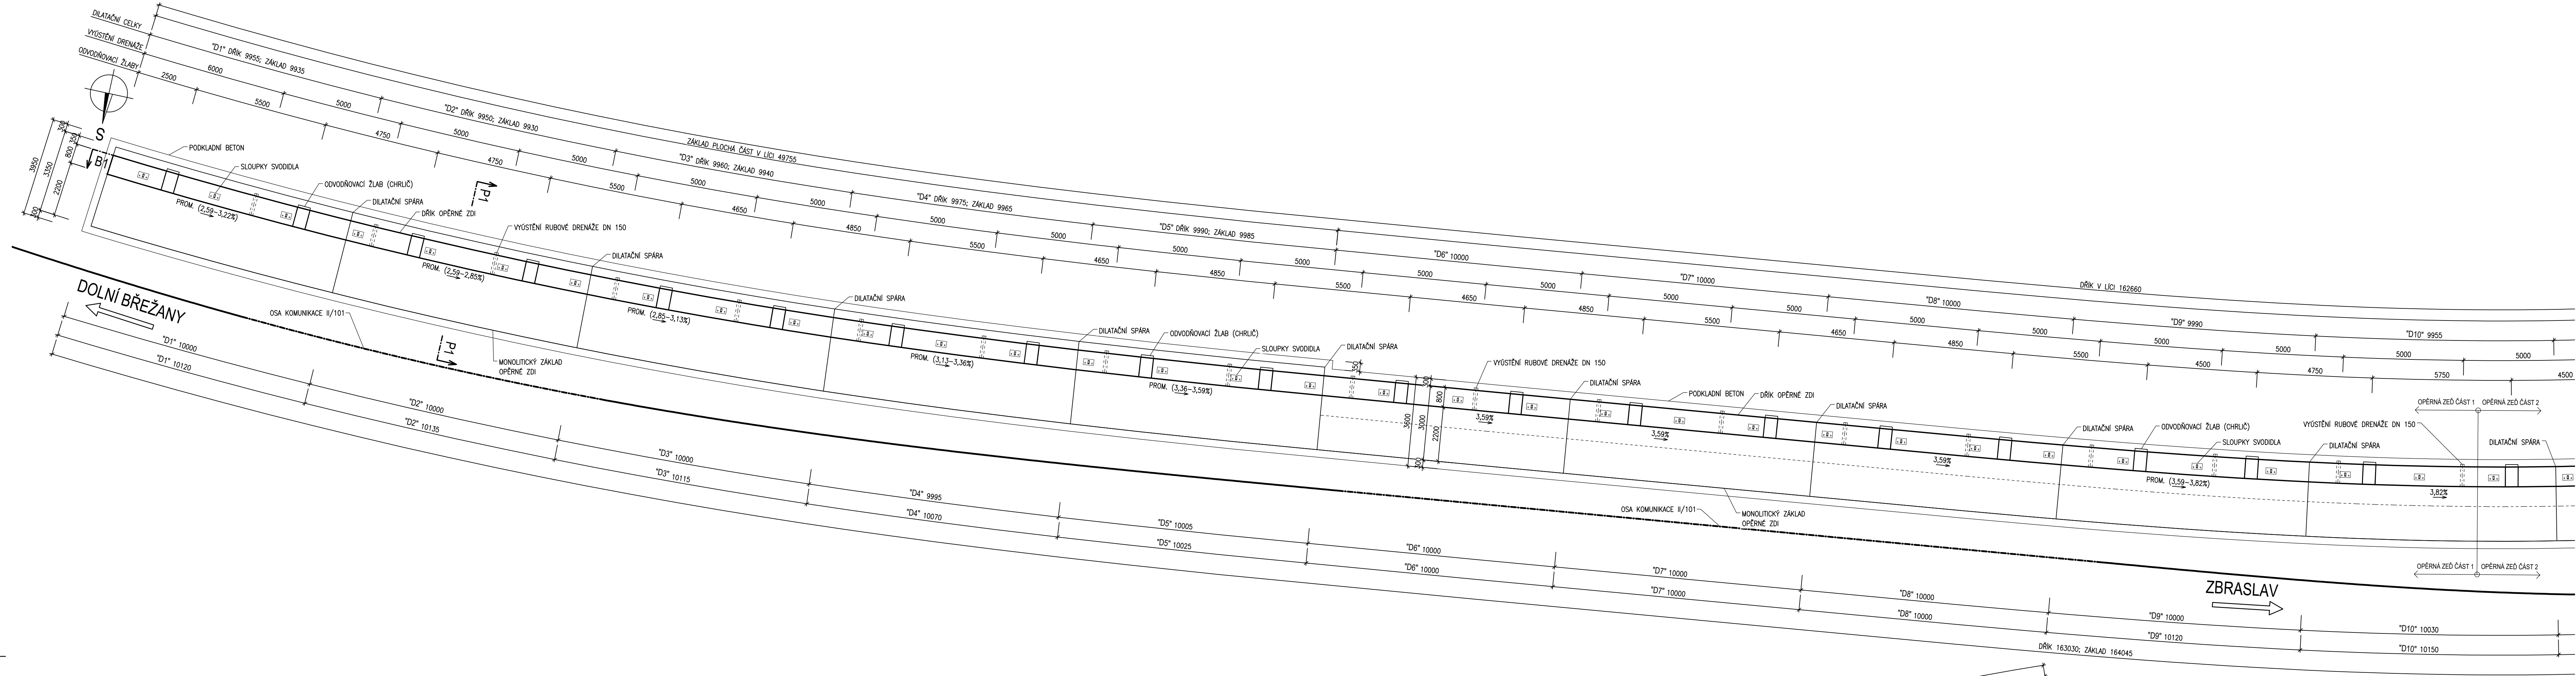

ÚSEK "2"

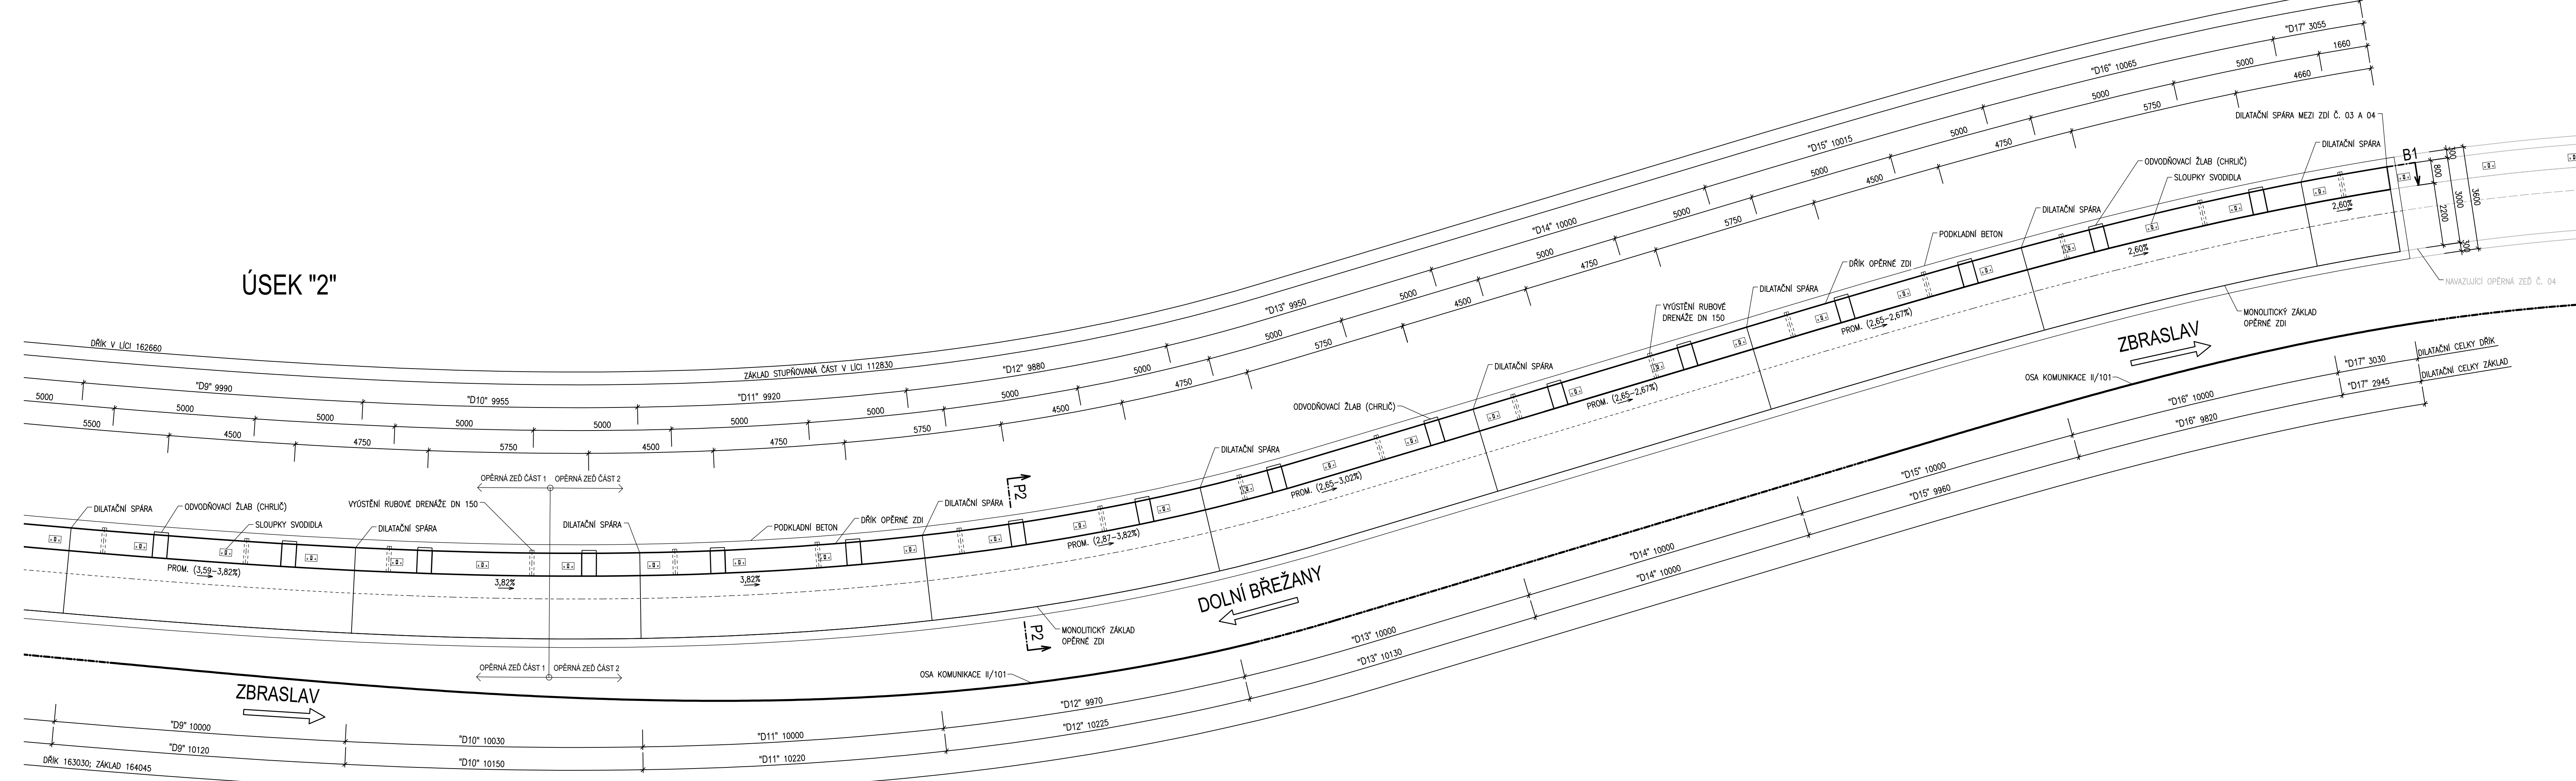

KONCEPT

OZNAČ.	TEXT ZMĚNY - ODŮVODNĚNÍ	DATUM	PODPIS
TABULKA ZMĚN			

Název stavby	II/101 Dolní Břežany - Zbraslav	ČÍSLO OBJEKTU	SO 251.2
--------------	---------------------------------	---------------	----------

Objednatel stavby

KSÚS
KRAJSKÁ SPRÁVA A PŘÍSPĚVKOVÁ ORGANIZACE

Krajská správa a údržba silnic
Středočeského kraje, příspěvková organizace
Zborovská 81/11, 150 21 Praha 5-Smíchov

Autorský dozor

GeoTec GS®

GeoTec-GS, a.s.
Chmelová 2920/6, 106 00 Praha 10

Technický dozor investora TES CONSULTING	TES + SGS + SGG vedoucí sdružení: TES Consulting, s.r.o. V Olšinách 2300/75, 100 00 Praha 10-Strašnice	RAŽITKO
		DATUM PODPIS

Zhotovitel stavby	 M-SILNICE a.s. Husova 1697, 530 03 Pardubice www.msilnice.cz	RAZÍTKO DATUM PODPIS
-------------------	---	--

Koordinátor RDS		RAZÍTKO
		
M - PROJEKCE s. r. o. Reslova 956/13, 500 02 Hradec Králové www.m-projekce.cz		
		DATUM
		PODPIS

Souřadnicový systém: S-JTSK	Výškový systém: Bpv
Zpracovatel stavebního objektu/části:	Projekční kancelář PRIS spol. s r.o. Osová 717/20, 625 00 Brno-Starý Lískovec www.pris.cz

Vypracoval: Ing. Ondřej Vytásek	Hlavní inženýr projektu: Ing. Jiří Ehrenberger	Razítko:  PROJEKČNÍ KANCELÁŘ PRIS spol. s r. o. OSOVA 20, 625 00 BRNO
Odpovědný projektant: Ing. Martin Reuhalík	Kontroloval: Ing. Jiří SRUBAR	
Číslo zakázky: 25130	Datum: 05/2026	

Objekt/část:		Měřítko:	Souprava:
SO 251.2 - OPĚRNÉ ZDI ZED č. 03		Stupeň: RDS	
Příloha:		Číslo přílohy:	
TVAR OPĚRNÉ ZDI - PŮDORYS - ČÁST 3		105_TV3	