



TVAR OPĚRNÉ ZDI - ŘEZY, DETAILS - ČÁST 4

PŘÍČNÝ ŘEZ P1-P1 km 0,640 000 1:25

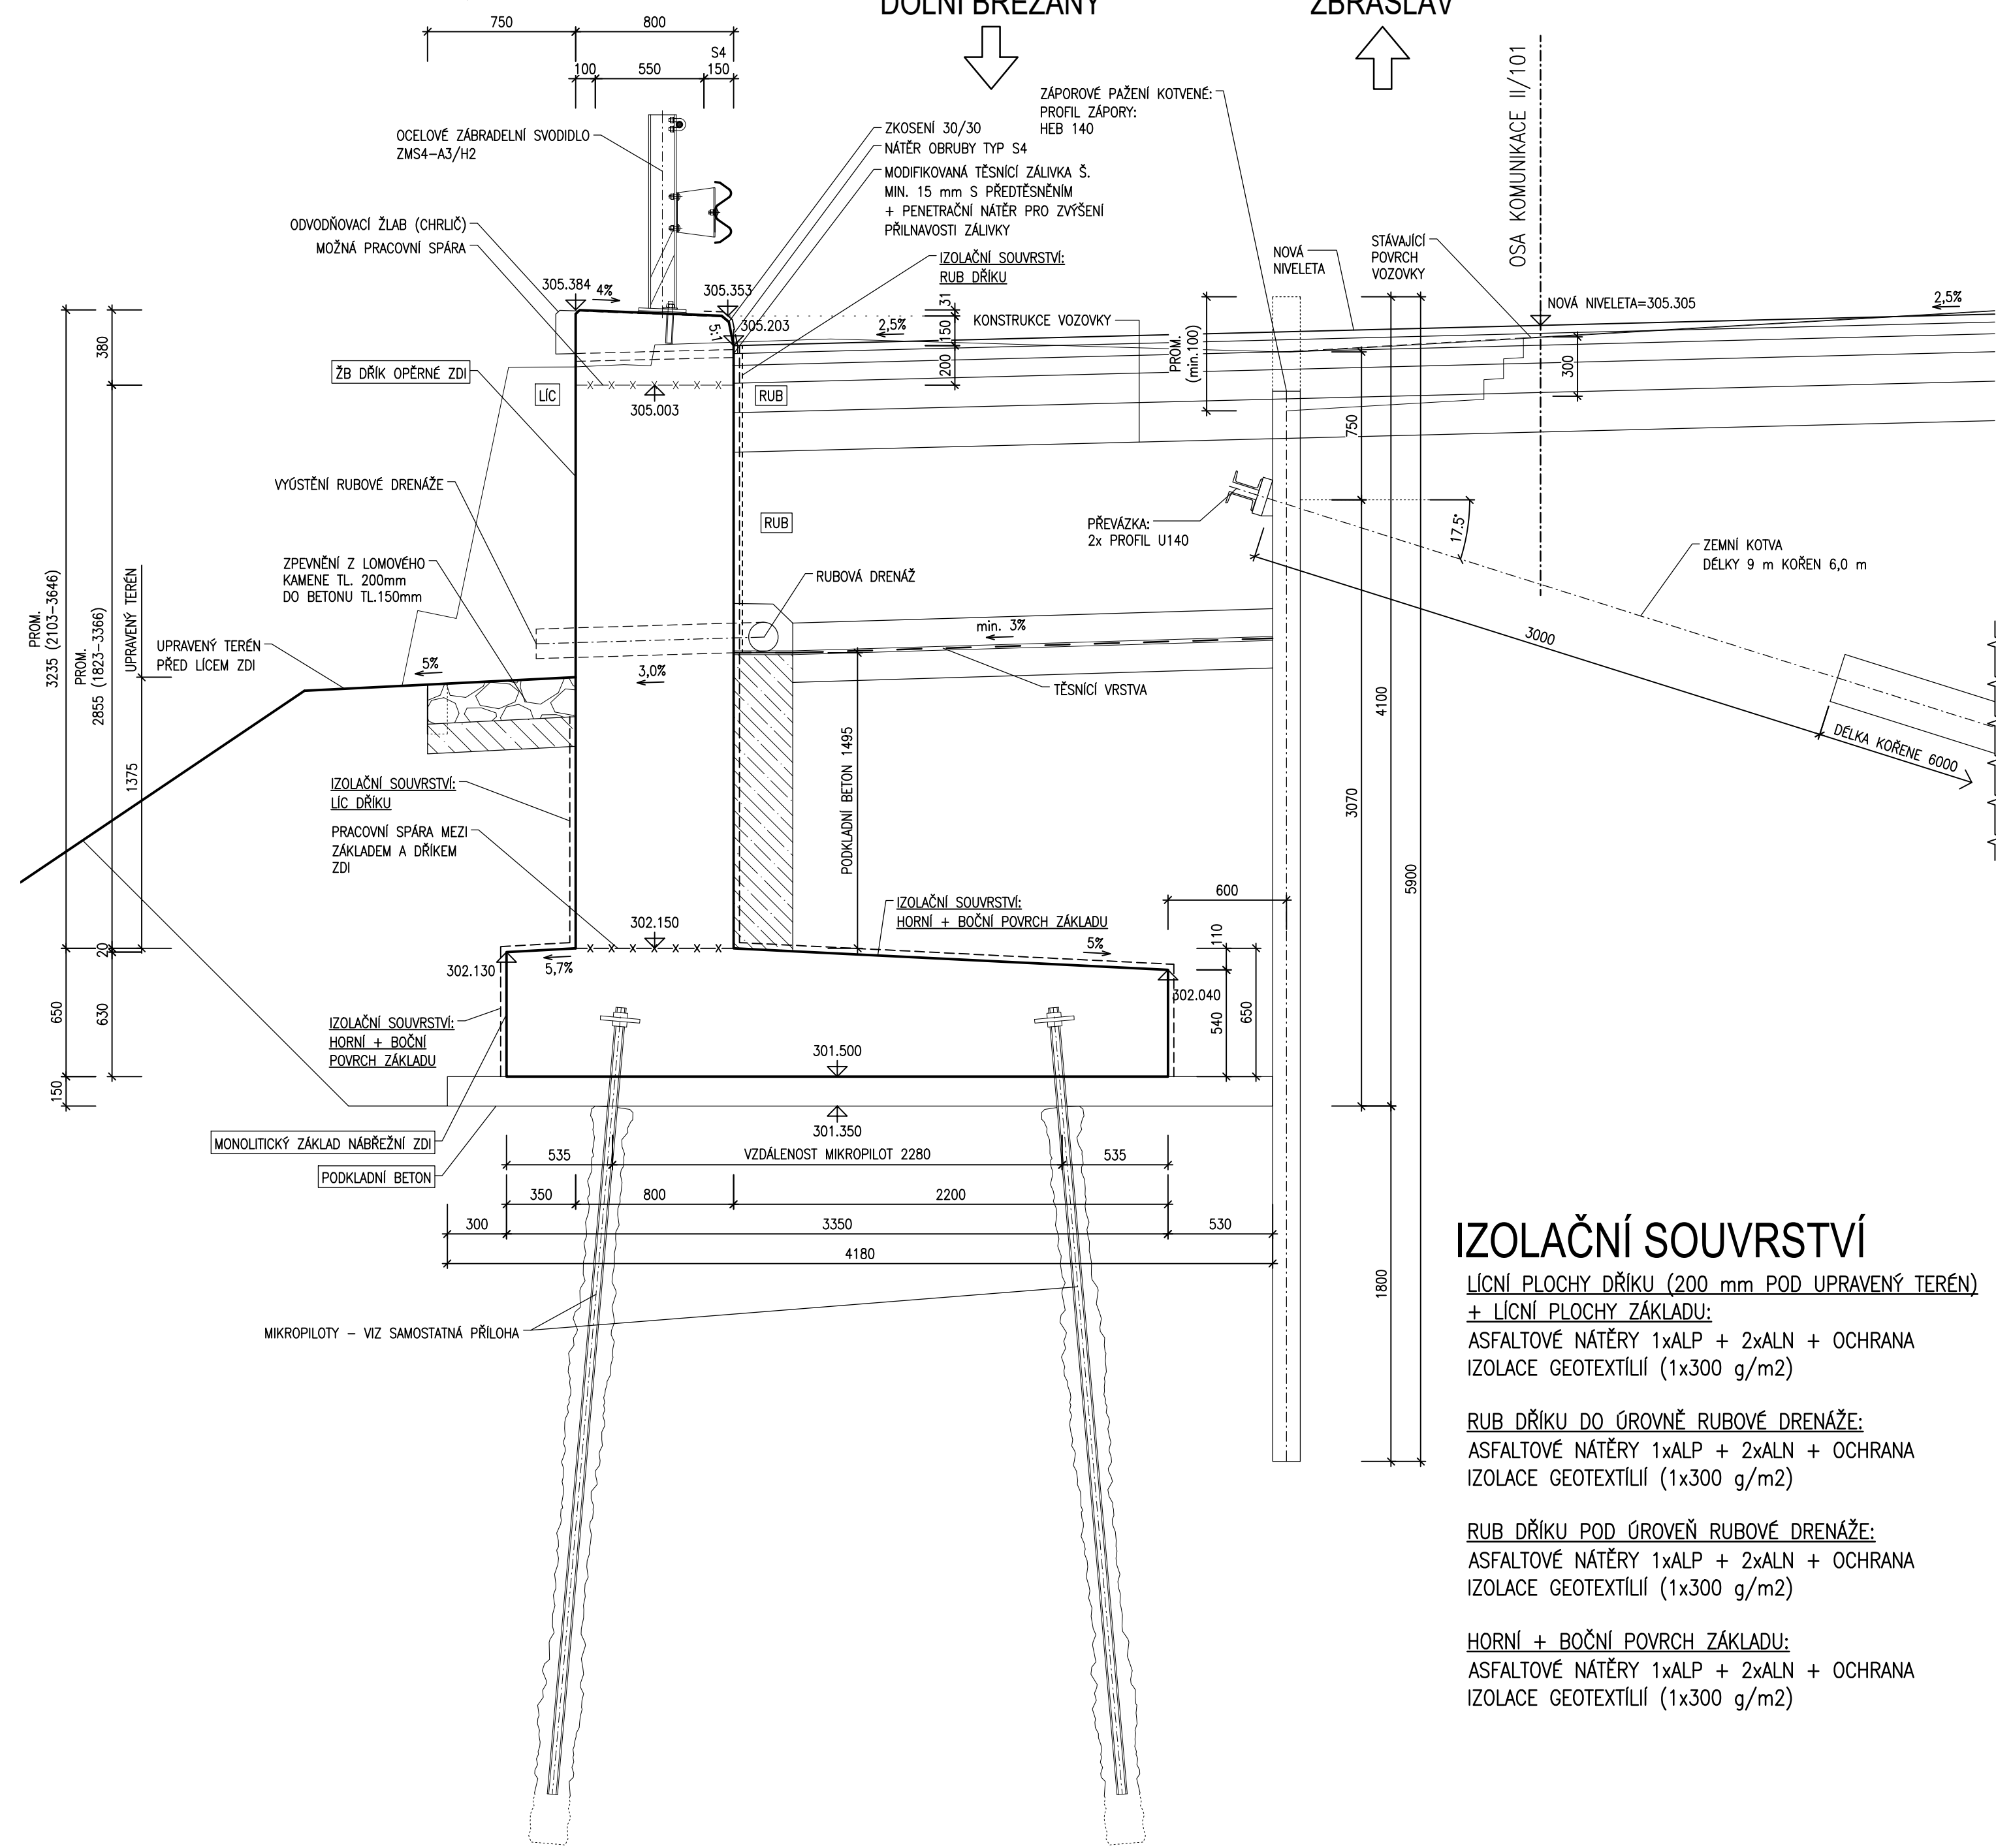


ODVODŇOVACÍ ŽLAB (CHRLIČ)

PŘÍČNÝ ŘEZ ŽLABEM 1:10

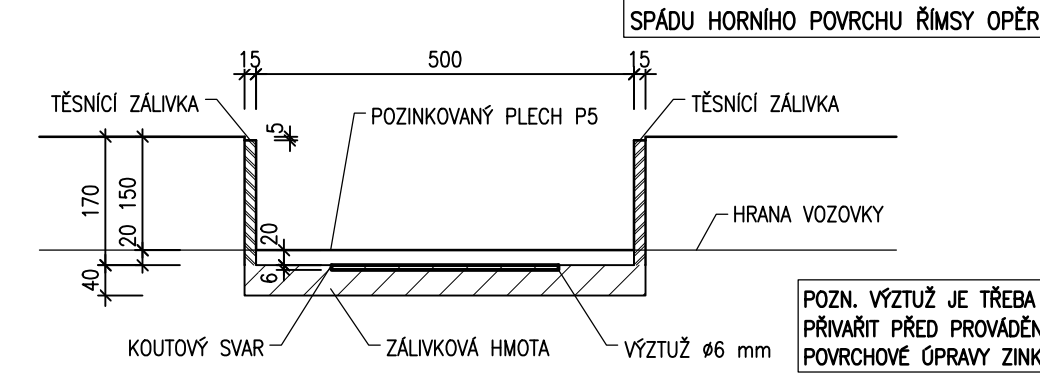


PODÉLNÝ ŘEZ ŽLABEM 1:10

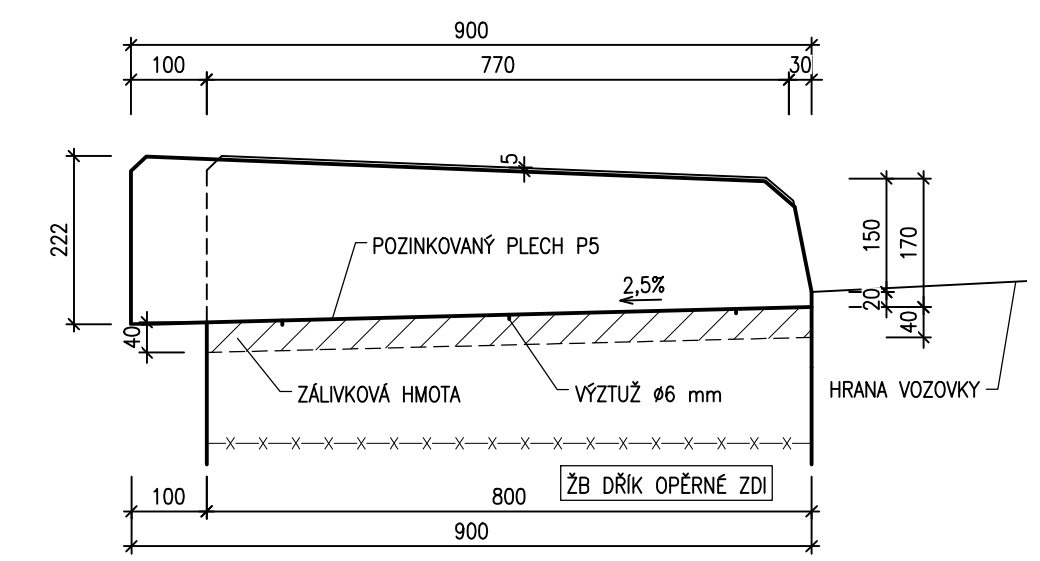

CELKEM KUSŮ CHRLIČŮ: 32 ks


ODVODŇOVACÍ ŽLAB (CHRLIČ)

PŮDORYS ŽLABU 1:25

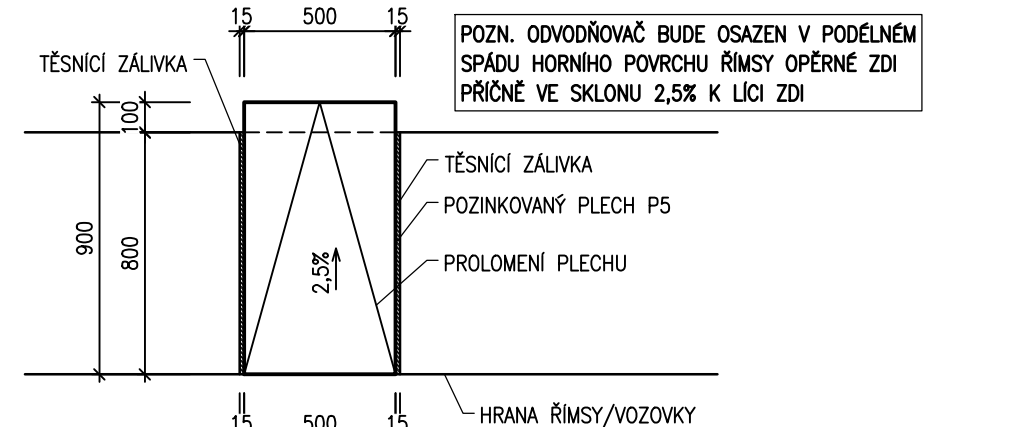


VODOROVNÁ PRACOVNÍ SPÁRA MEZI

ZÁKLADEM A DŘÍKEM 1:10

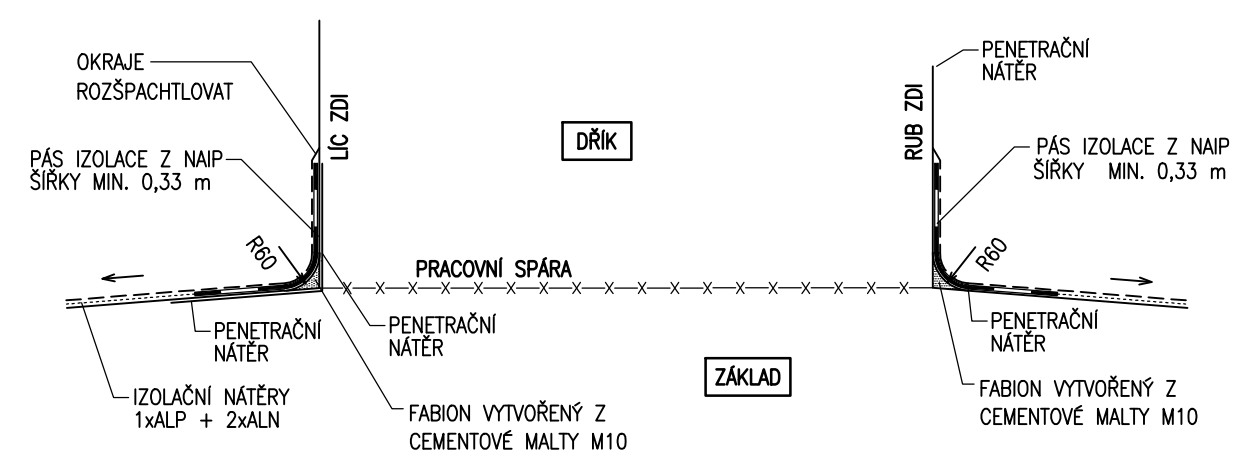


PŘÍČNÝ ŘEZ P2-P2 km 0,740 000 1:25

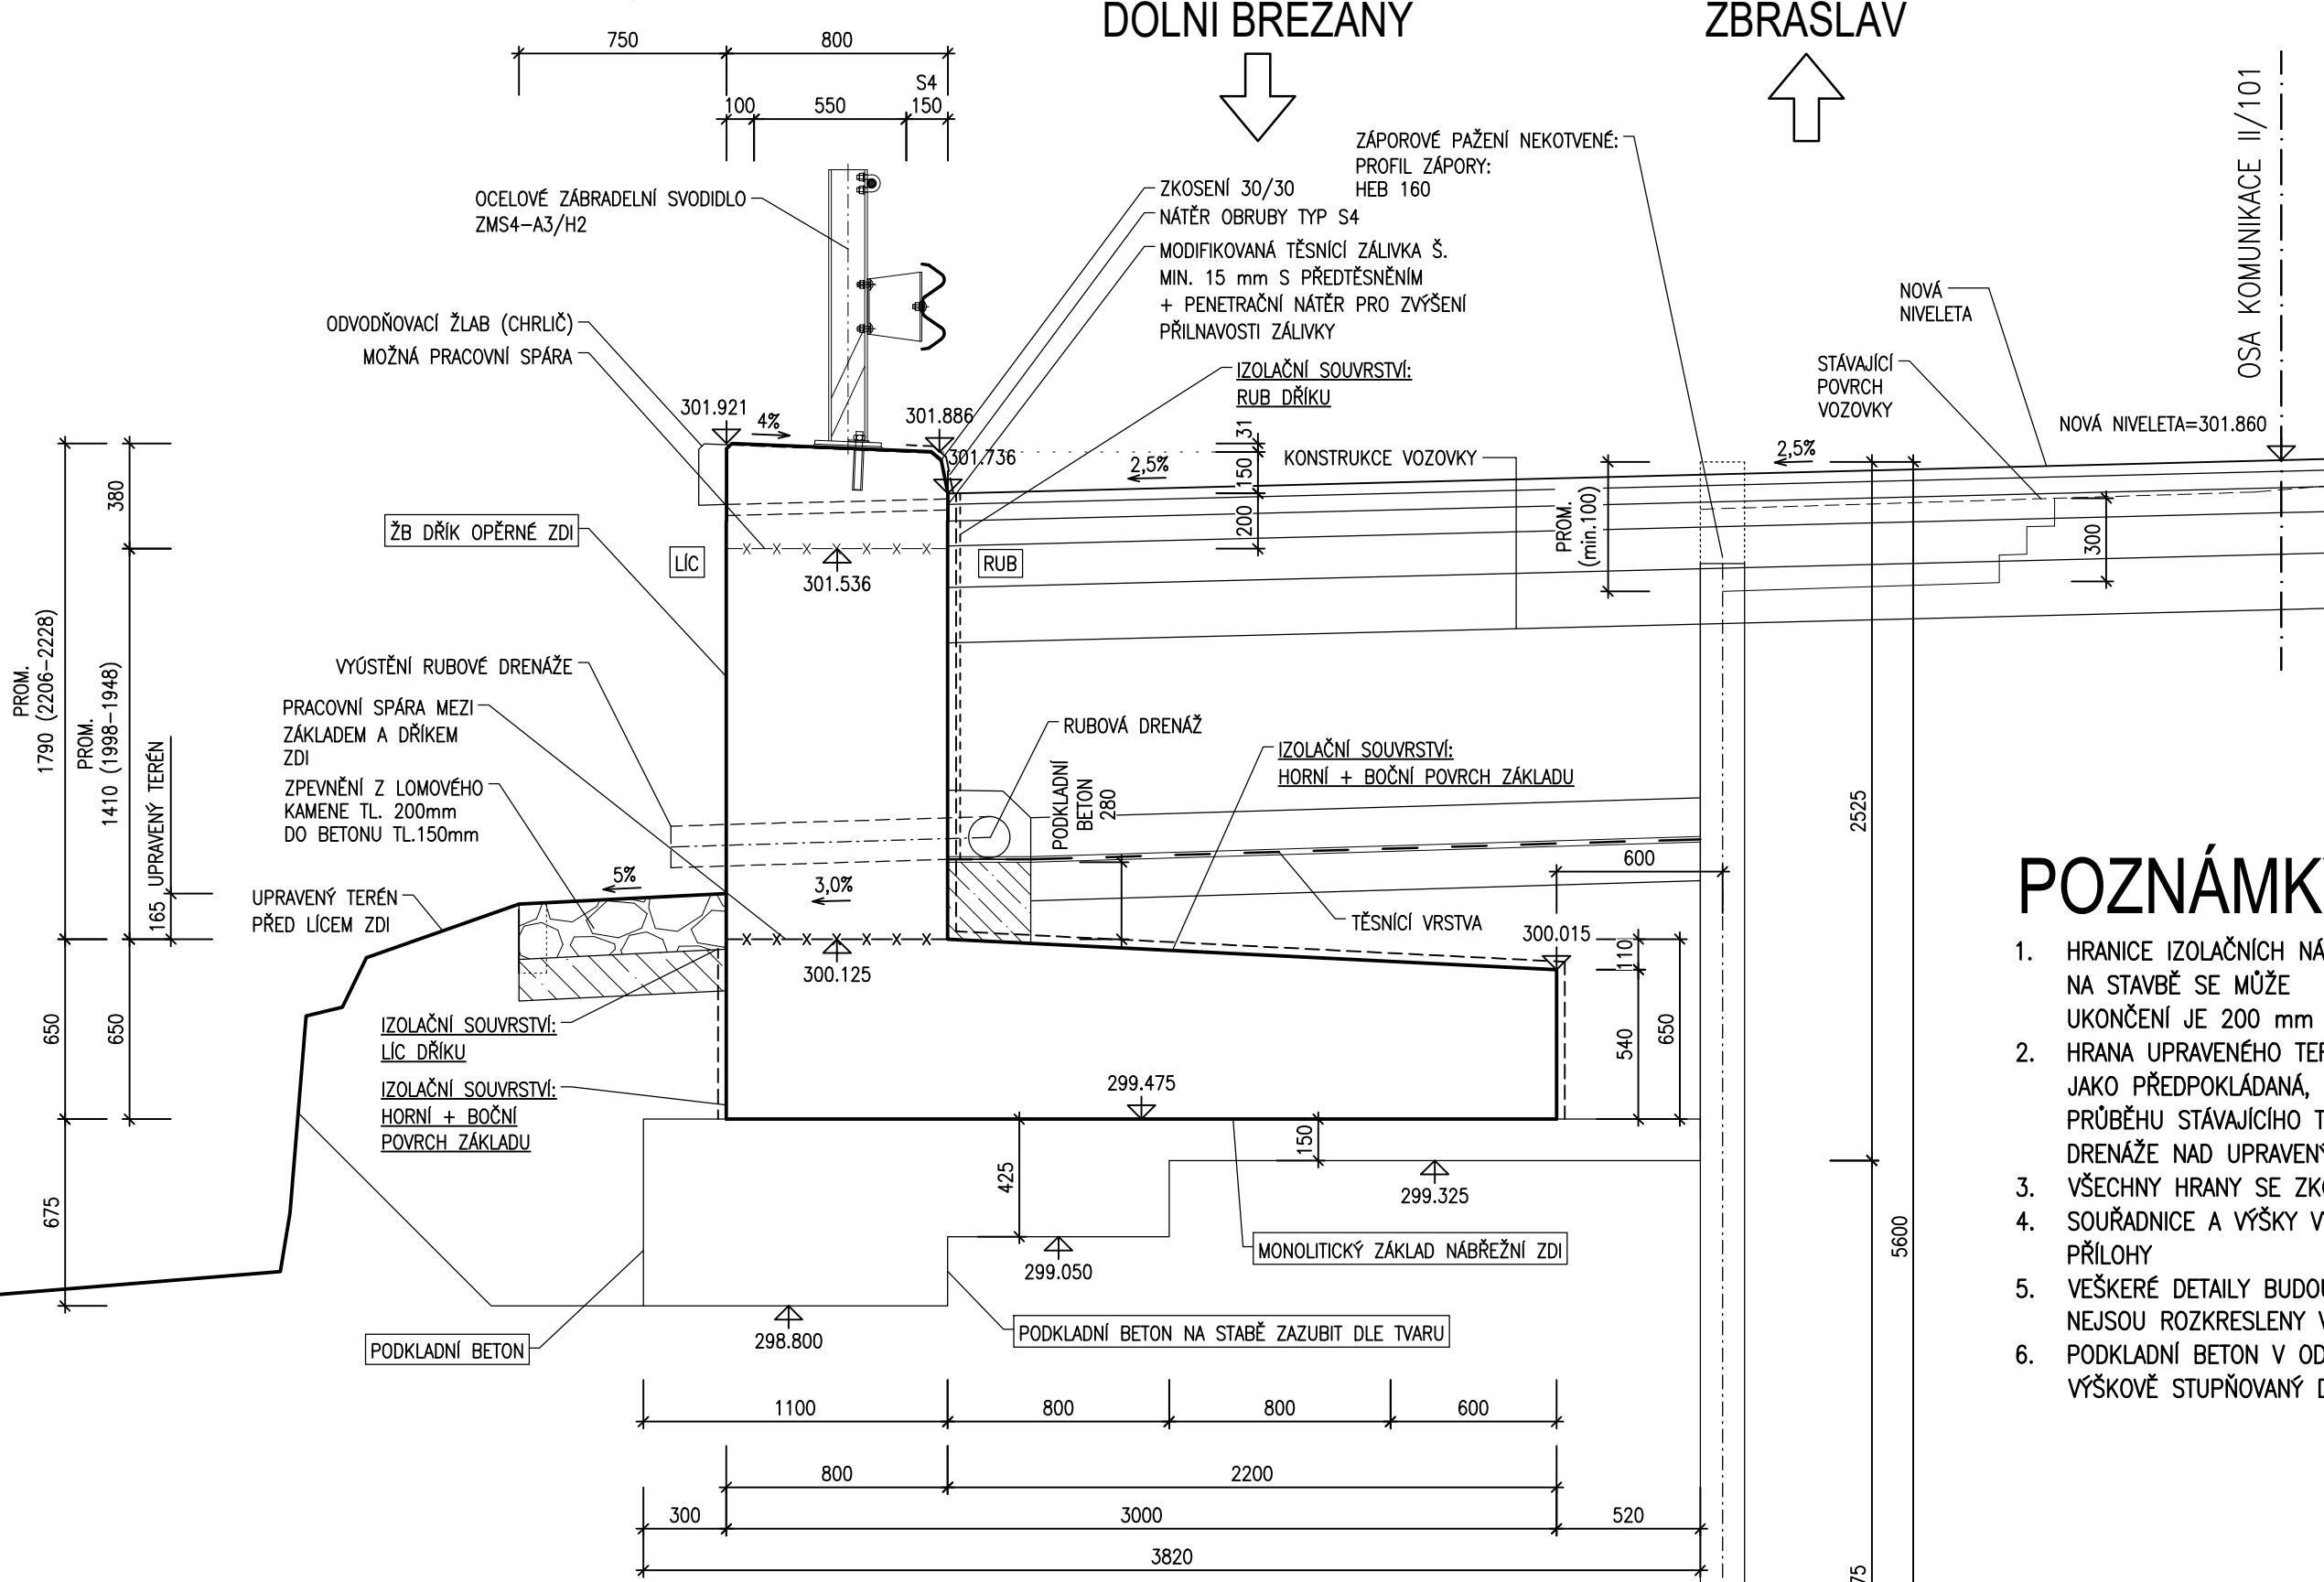


DETAIL ULOŽENÍ RUBOVÉ DRENÁŽE

ŘEZ RUBOVU DRENÁŽÍ ZA RUBEM 1:10

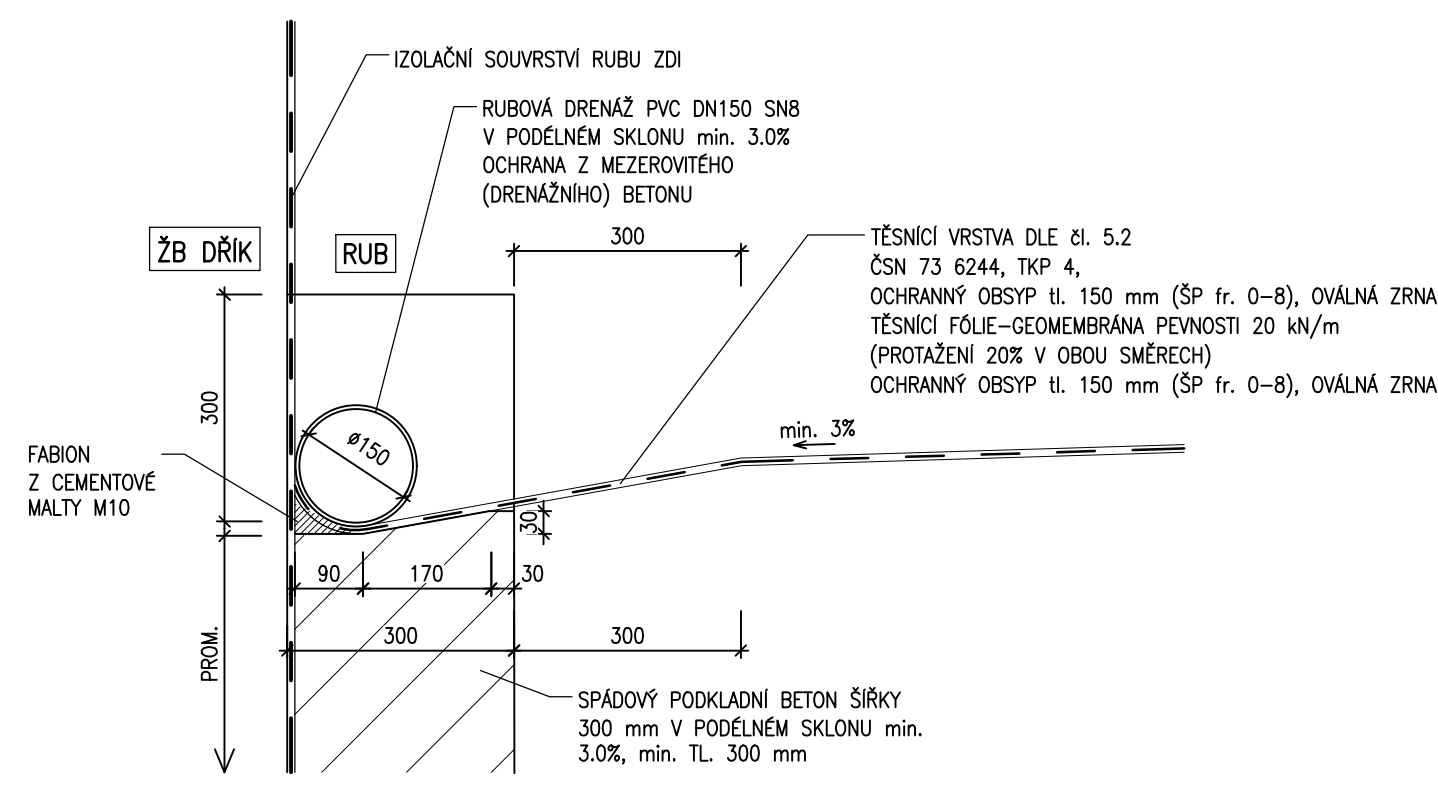


DETAIL PROSTUPU RUBOVÉ DRENÁŽE

ŘEZ DŘÍKEM ZDI 1:5

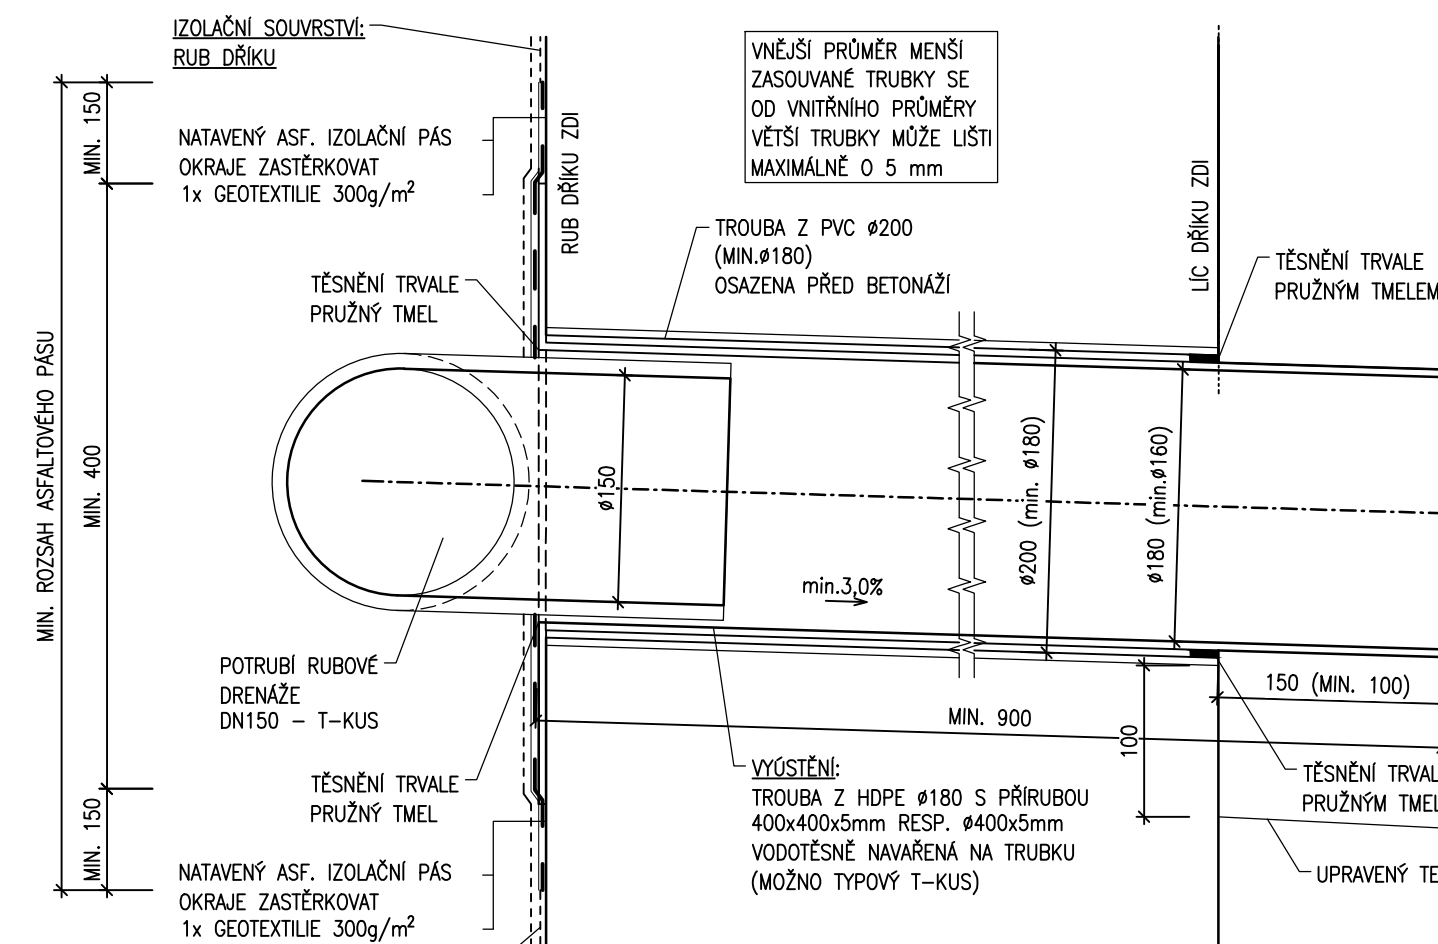


DILATAČNÍ SPÁRA 1:10

OPĚRNÁ ZEĎ - OPĚRNÁ ZEĎ

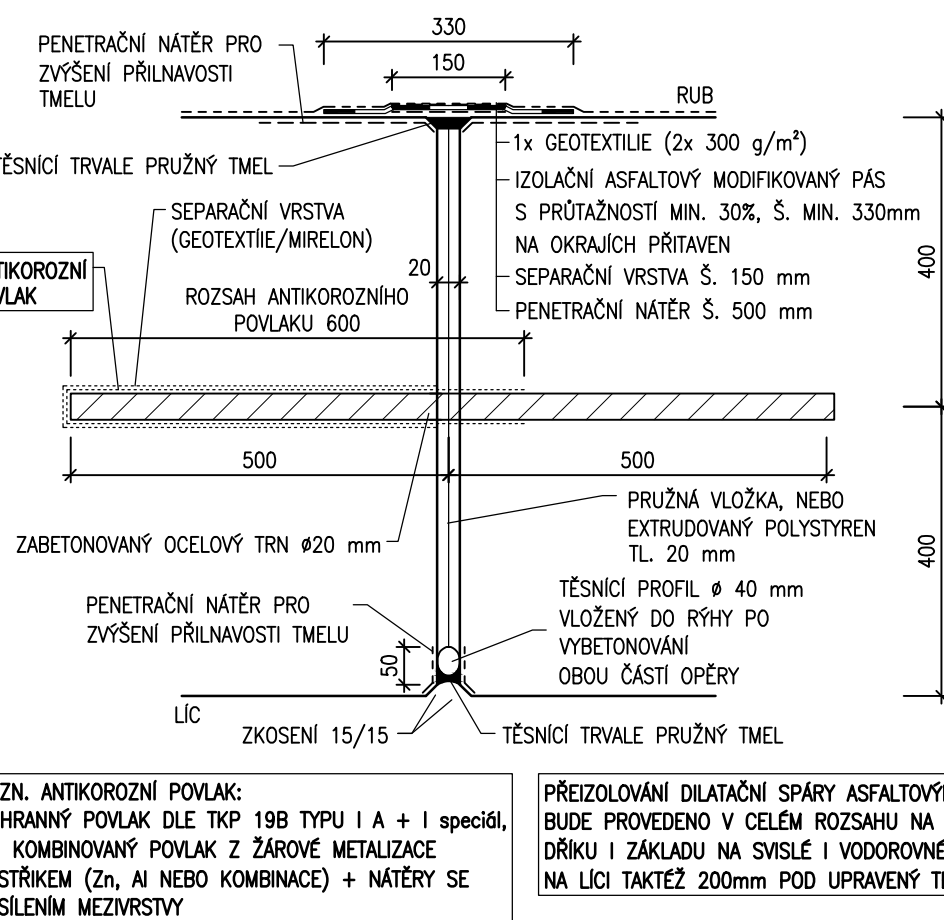


VODOROVNÁ PRACOVNÍ SPÁRA MEZI

ZÁKLADEM A DŘÍKEM 1:10

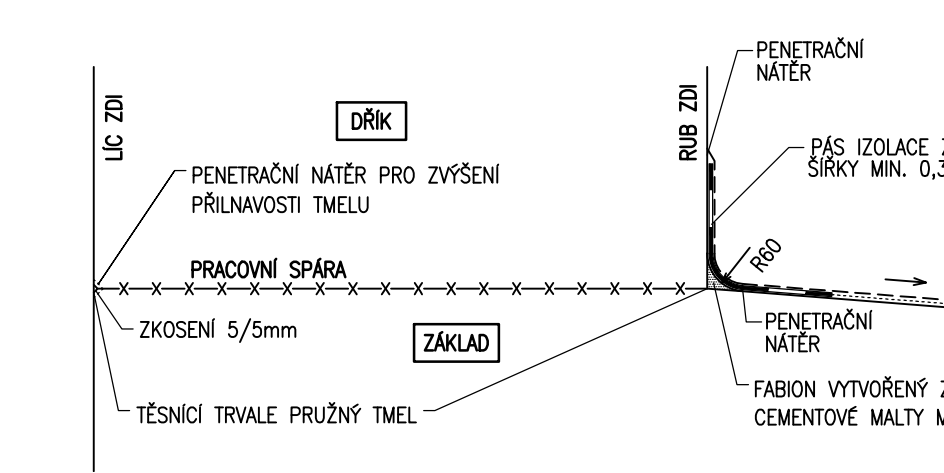

VYZNAČENÍ LETOPOČTU 1:5

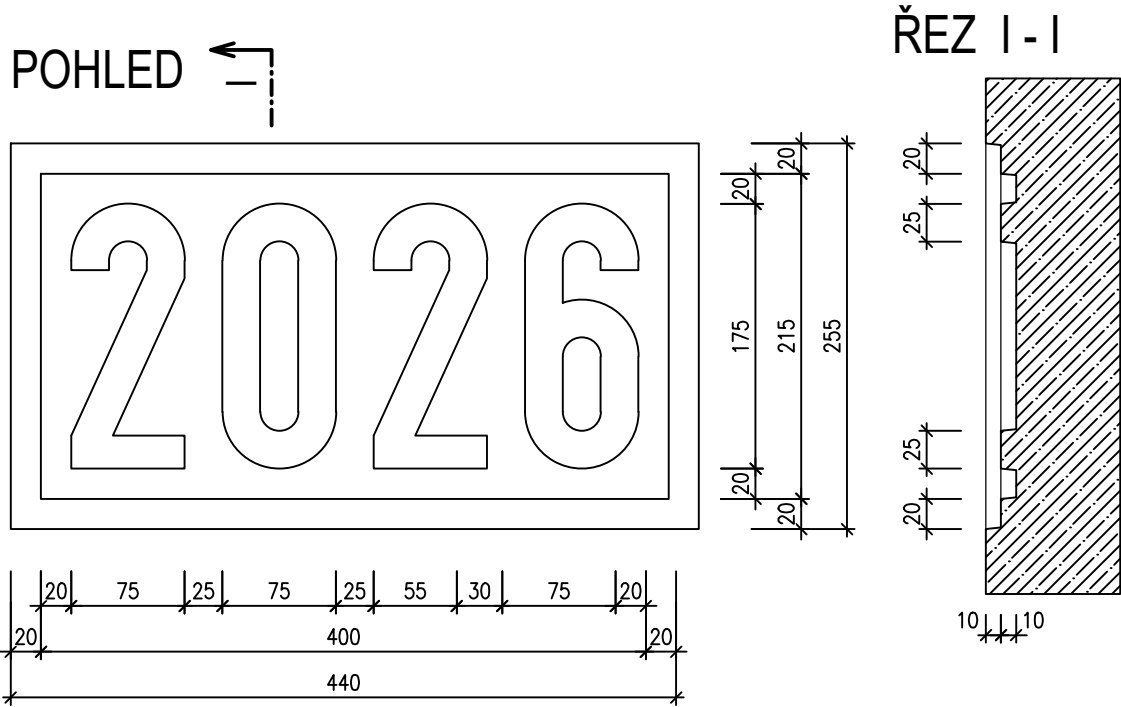

CELKEM KUSŮ LETOPOČTU: 2 ks

STAVEBNÍ MATERIÁLY

BETONY BUDOU PROVEDENY DLE ČSN EN 206	
KONSTRUKČNÍ BETONY:	
ZB ZÁKLAD	C30/37 XD2, XF2, XC2 (CZ.F.1.2) – CI 0,2; D _{max} 22 – S3
ZB DŘÍK	C30/37 XD3, XF4, XC4 (CZ.F.1.2) – CI 0,2; D _{max} 22 – S3
OSTATNÍ BETONY:	
PODKLADNÍ BETON	C12/15 X0 (CZ.F.1.2) – CI 1,0; D _{max} 22 – S3
PODKLADNÍ BETON – RUBOVÁ DRENÁŽ	C8/10 X0 (CZ.F.1.2) – CI 1,0; D _{max} 22 – S3
PODKLADNÍ BETON – SCHODIŠTĚ, DLAŽBY	C20/25 XF3, XD2 (CZ.F.1.2) – CI 0,2; D _{max} 22 – S3
BETONOVÉ PRAHY	C30/37 XF4, XD3 (CZ.F.1.2) – CI 0,2; D _{max} 22 – S3
BETONÁŘSKÁ VÝZUŽ:	
OCEL	B500B

KONCEPT

OZNAČ. TEXT ZMĚNY - ODŮVODNĚNÍ		DATUM	PODPIS
TABULKA ZMĚN			
Název stavby		ČÍSLO OBJEKTU	
II/101 Dolní Břežany - Zbraslav		SO 251.2	
Objednatel stavby			
Ksús Krajská správa a údržba silnic Středočeského kraje, příspěvková organizace Zborovská 81/11, 150 21 Praha 5-Smíchov			
Autorský dozor			
GeoTec GS		GeoTec-GS, a.s. Chmelová 2920/6, 106 00 Praha 10	
Technický dozor investora			
TES CONSULTING		TES + SGS + SGG vedoucí sdružení: TES Consulting, s.r.o. V Olšinách 2300/75, 100 00 Praha 10-Štrašnice	
Zhotovitel stavby			
M-SILNICE		M-SILNICE a.s. Husova 1697, 530 03 Pardubice www.msilnice.cz	
Koordínátor RDS			
M - PROJEKCE		M - PROJEKCE s. r. o. Reslova 956/13, 500 02 Hradec Králové www.m-projekce.cz	

Souladníkový systém: S-JTSK		Výškový systém: Bpv	
Zpracovatel stavebního objektu/části:		Projektční kancelář PRIS spol. s r.o. Osova 717/20, 625 00 Brno-Starý Lískovec www.pris.cz	
Vypracoval: Ing. Ondřej Vytásek		Hlavní inženýr projektu: Ing. Jiří Ehrenberger	
Odpovědný projektant: Ing. Martin Reuhla		Kontroloval: Ing. Jiří ŠRUBAR	
Číslo zakázky: 25139		Datum: 05/2026	
Objekt/část: SO 251.2 - OPĚRNÉ ZDI ZEĎ č. 03		Měřítko: 1:25, 1:10, 1:5	
Příloha:		Stupeň: RDS	
TVAR OPĚRNÉ ZDI - ŘEZY, DETAILS - ČÁST 4		Číslo přílohy: 106_TV94	