



VÝZTUŽ OPĚRNÉ ZDI - POHLEDY, ŘEZY - ČÁST 1


POHLED V LÍCI B1-B1 1:50
DILATAČNÍ CELEK "D3" - "D8"

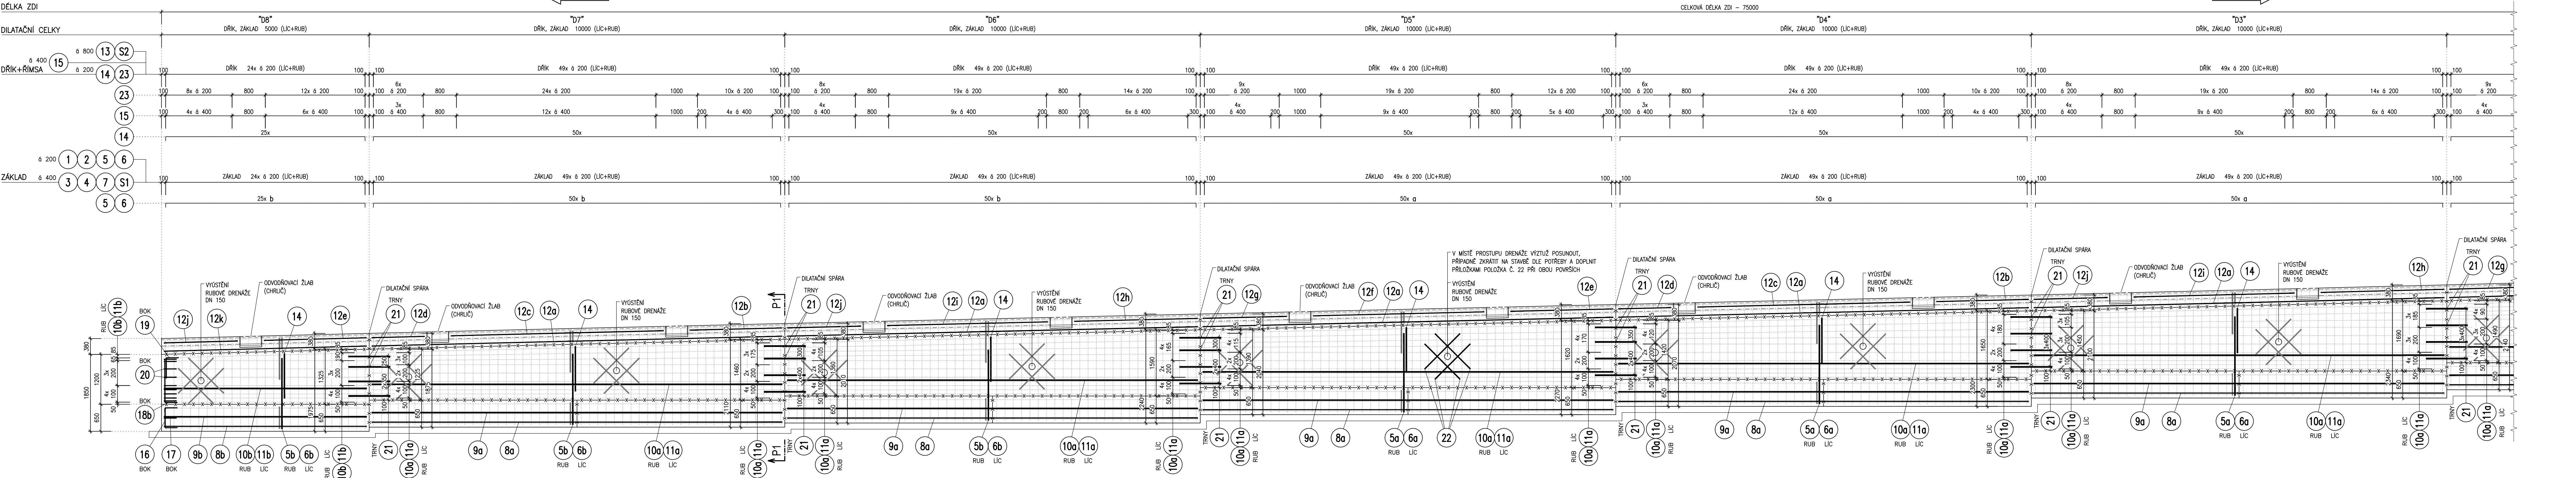


DILATAČNÍ CELEK "D1" - "D2"

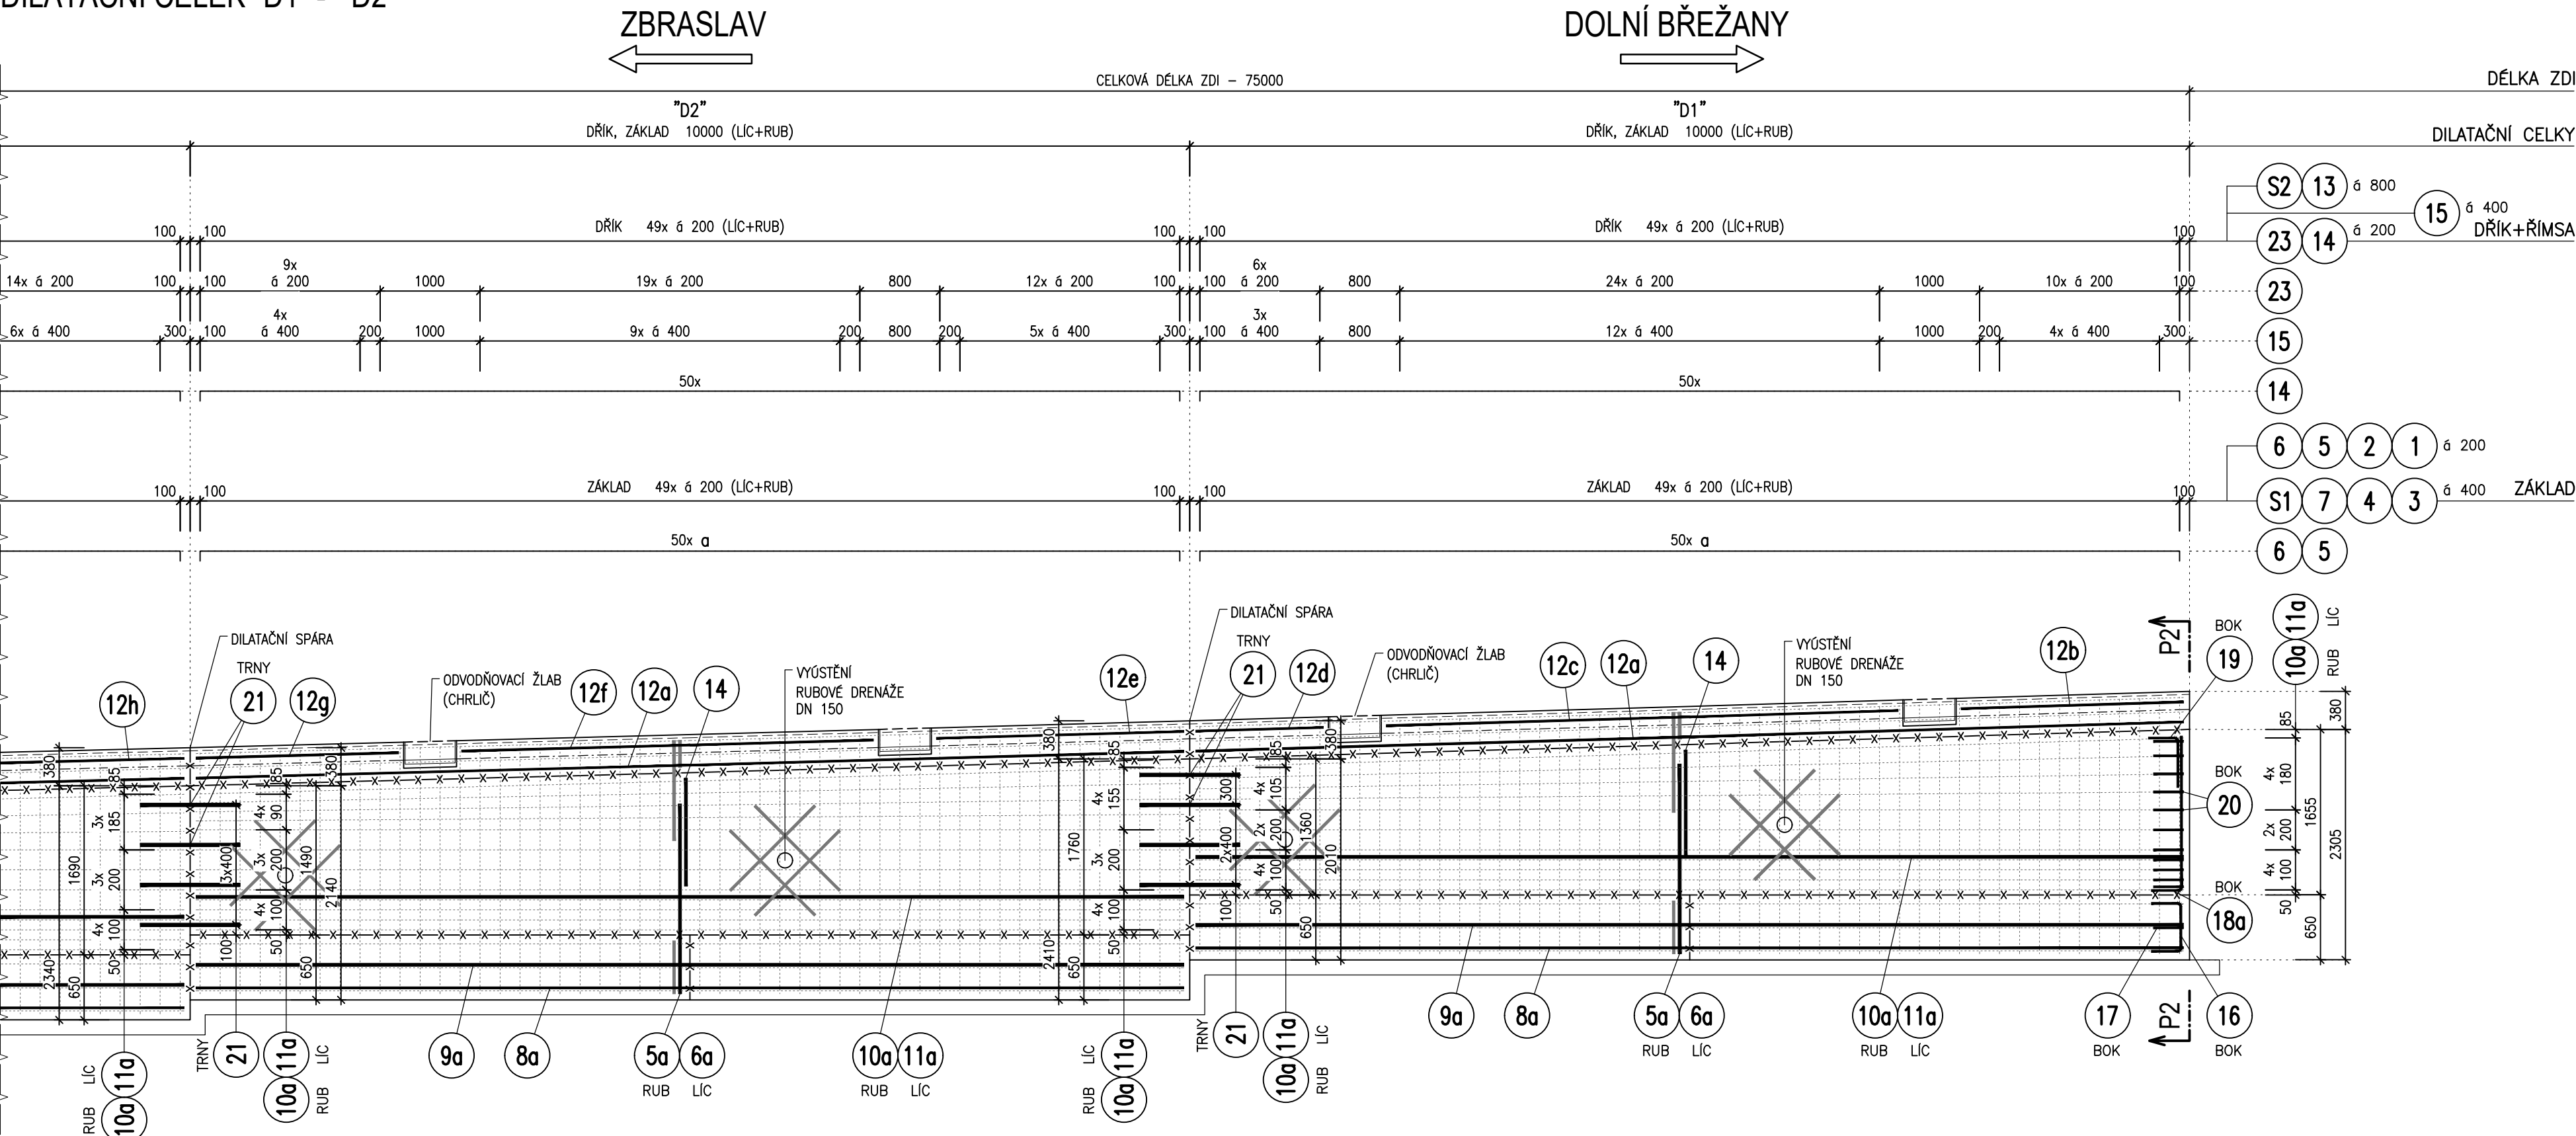

PŘÍČNÝ ŘEZ P1-P1 1:25

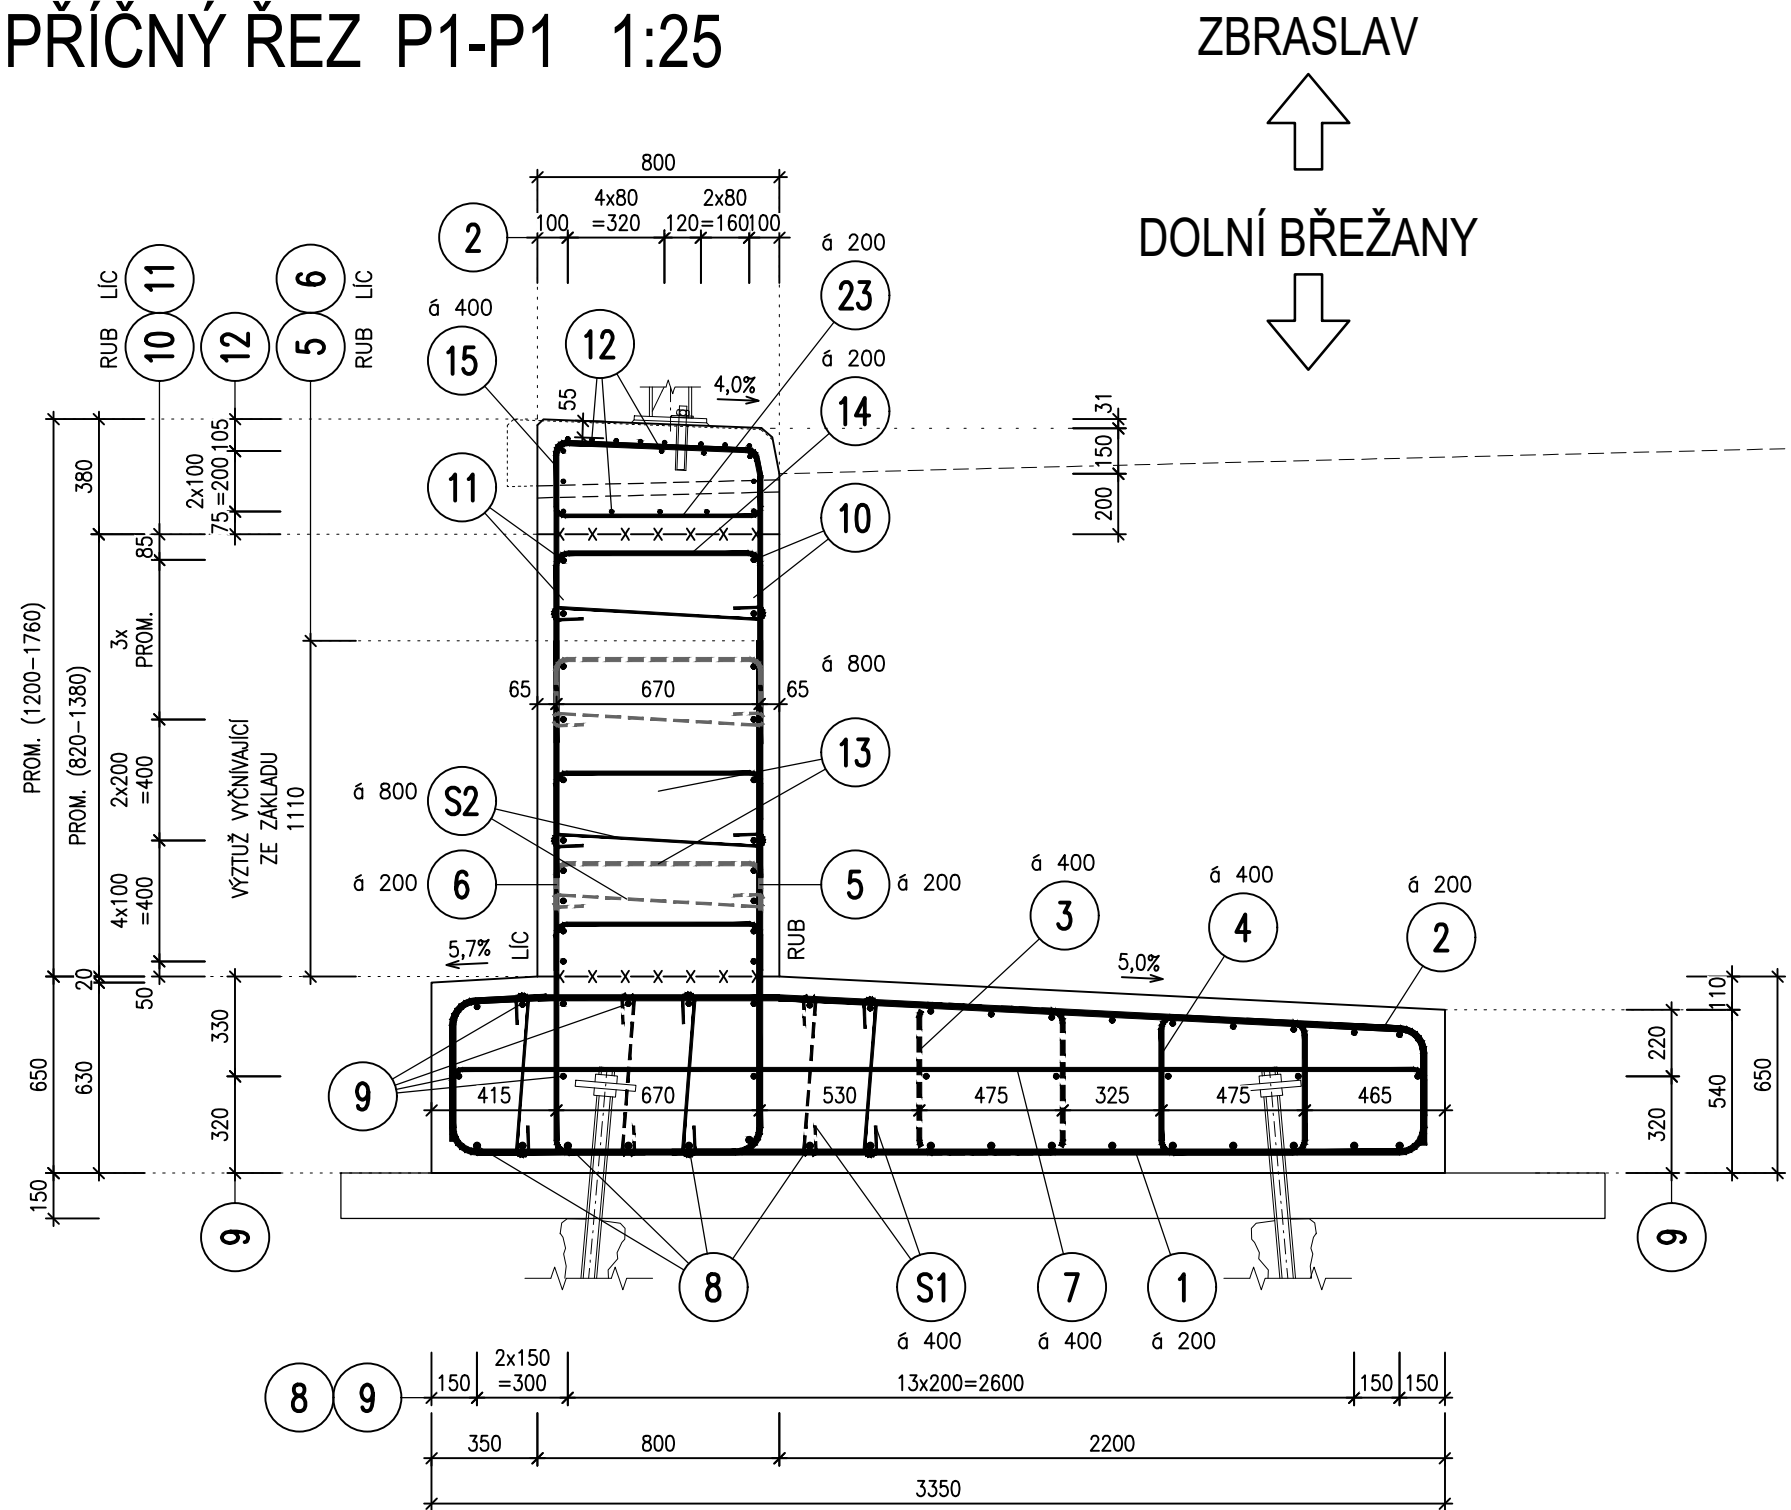

POHLED P2-P2 1:50

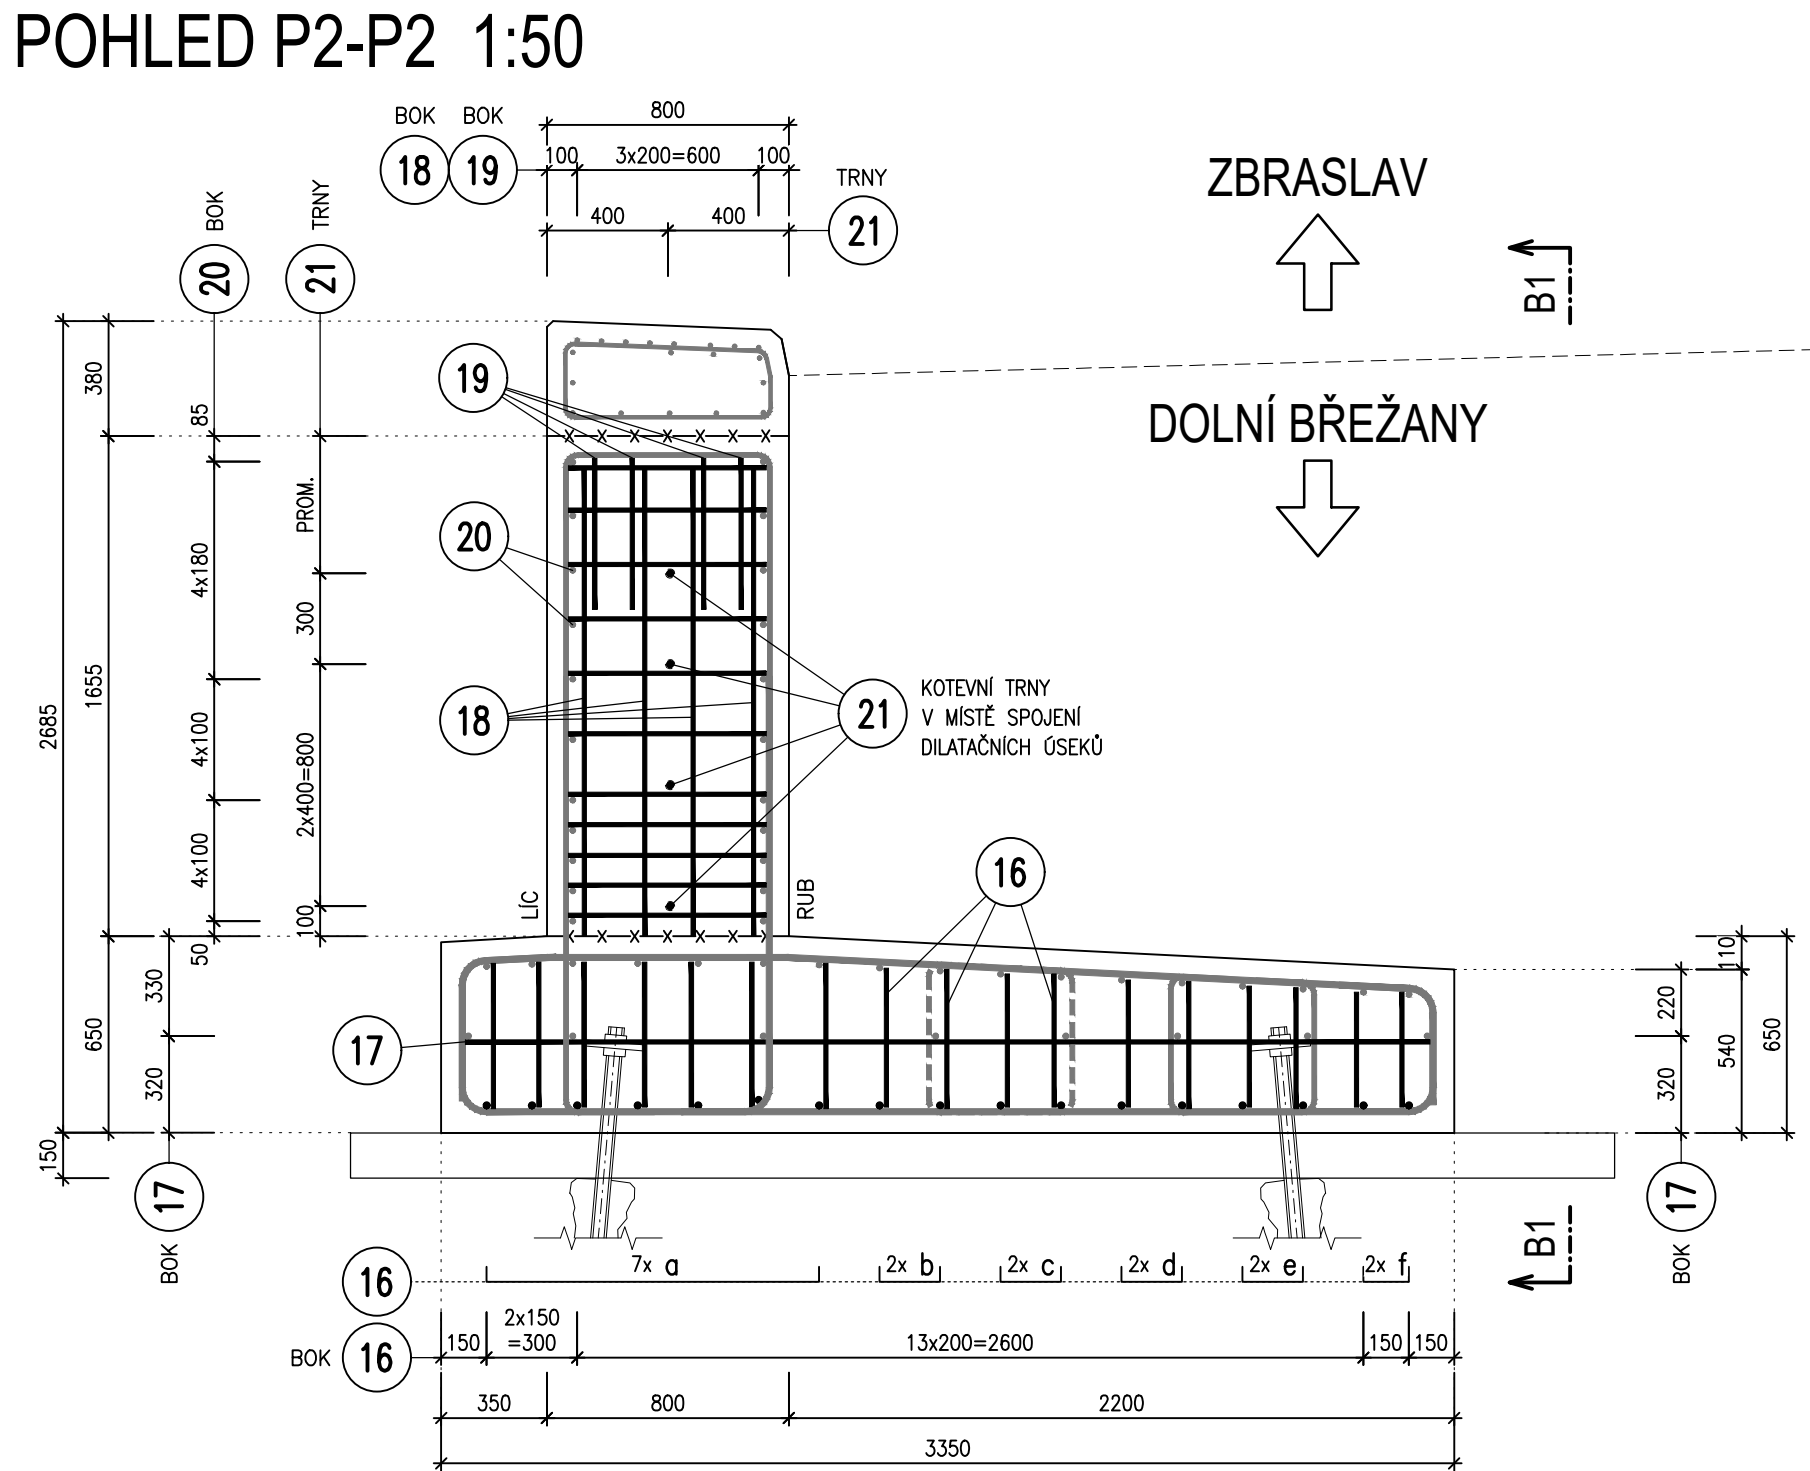

PŘEDKONCEPT			
OZNAČ.	TEXT ZMĚNY - ODŮVODNĚNÍ	DATUM	PODPIS
TABULKA ZMĚN			
Název stavby		ČÍSLO OBJEKTU	
II/101 Dolní Břežany - Zbraslav		SO 251.2	
Objednatel stavby			
 Krajská správa a údržba silnic Středočeského kraje, příspěvková organizace Zborovská 811/11, 150 21 Praha 5-Smíchov			
Autorský dozor			
		GeoTec-GS, a.s. Chmelová 2920/6, 106 00 Praha 10	
Technický dozor investora		RAZÍTKO	
		TES + SGS + SGG vedoucí sdružení: TES Consulting, s.r.o. V Olšánské 2300/75, 100 00 Praha 10-Strašnice	
Datum		PODPIS	
Zhotovitel stavby		RAZÍTKO	
		M-SILNICE a.s. Husova 1697, 530 03 Pardubice www.msilnice.cz	
Datum		PODPIS	
Koordinační RDS		RAZÍTKO	
		M - PROJEKCE s. r. o. Restlova 956/13, 500 02 Hradec Králové www.m-projeke.cz	
Datum		PODPIS	
Souřadnicový systém: S-JTSK		Výškový systém: Bpv	
Zpracovatel stavebního objektu/části:			
Projektovací kancelář PRIS spol. s r.o. Osova 717/20, 625 00 Brno-Starý Lískovec www.pris.cz			
Výpracoval:		Razítko:	
Iona Syňková			
Odpovědný projektant:		Hlavní inženýr projektu:	
Ing. Martin Rehnika		Ing. Jiří Ehrenberger	
Kontroloval:		Kontrola:	
Ing. Jiří ŠRUBAR		Ing. Jiří ŠRUBAR	
Číslo zakázky:		Datum:	
25-122-02		03/2026	
Objekt/část:		Měřítko:	
SO 251.2 - OPĚRNÉ ZDI		1:50; 1:25	
ZED č. 05		Stupeň:	
Příloha:		S	
VÝZTUŽ OPĚRNÉ ZDI - POHLEDY, ŘEZY - ČÁST 1		Číslo přílohy:	
		107_VOZ1	