



# MIKROPILOTY


PŮDORYS 1:100

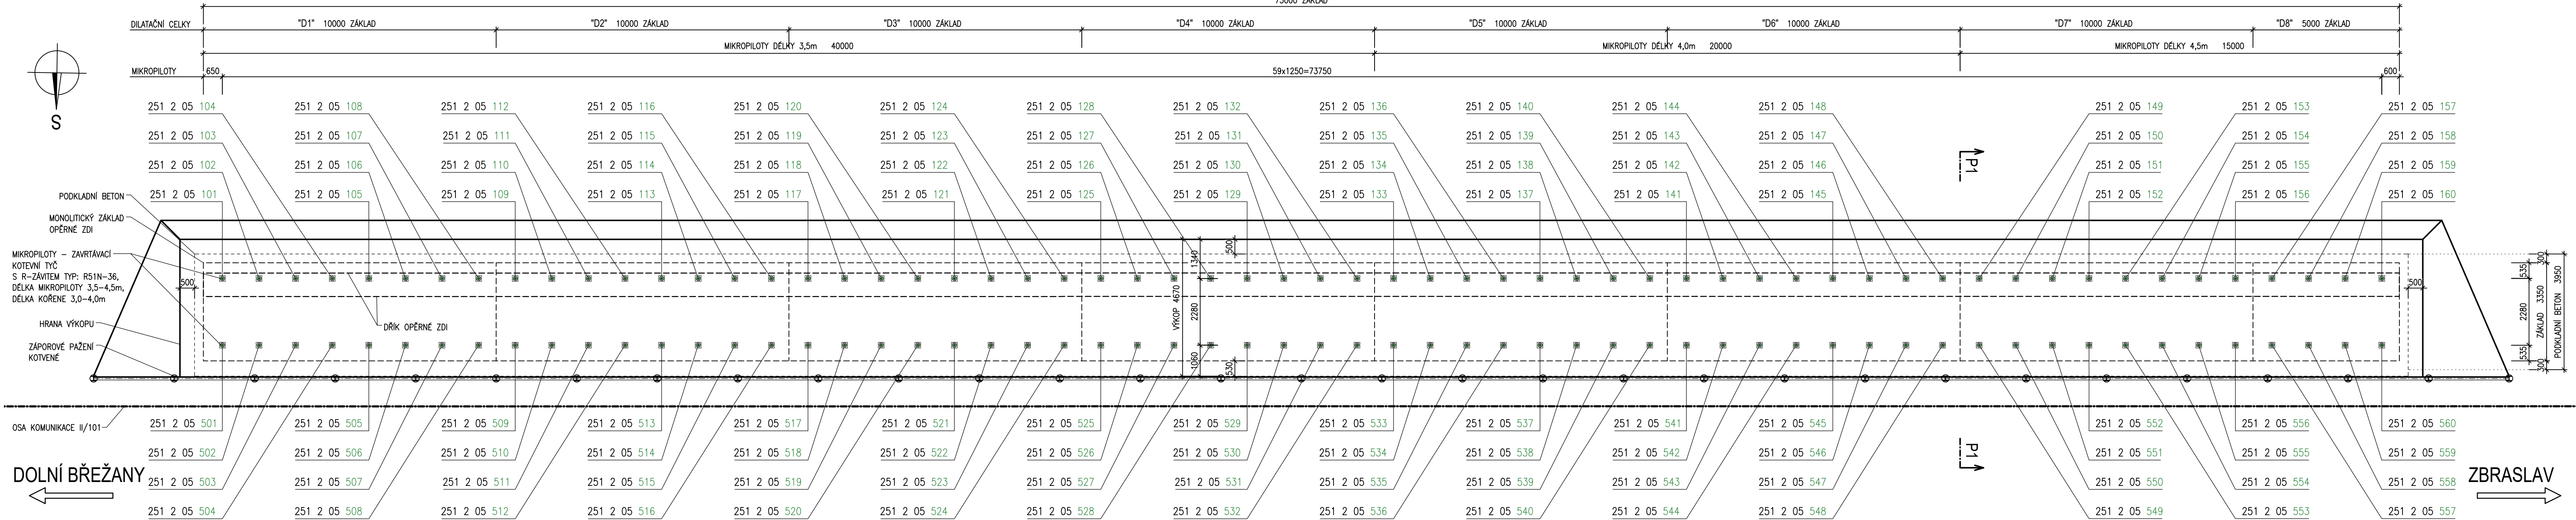


PŘÍČNÝ ŘEZ P1-P1 km 1,060 000 1:25

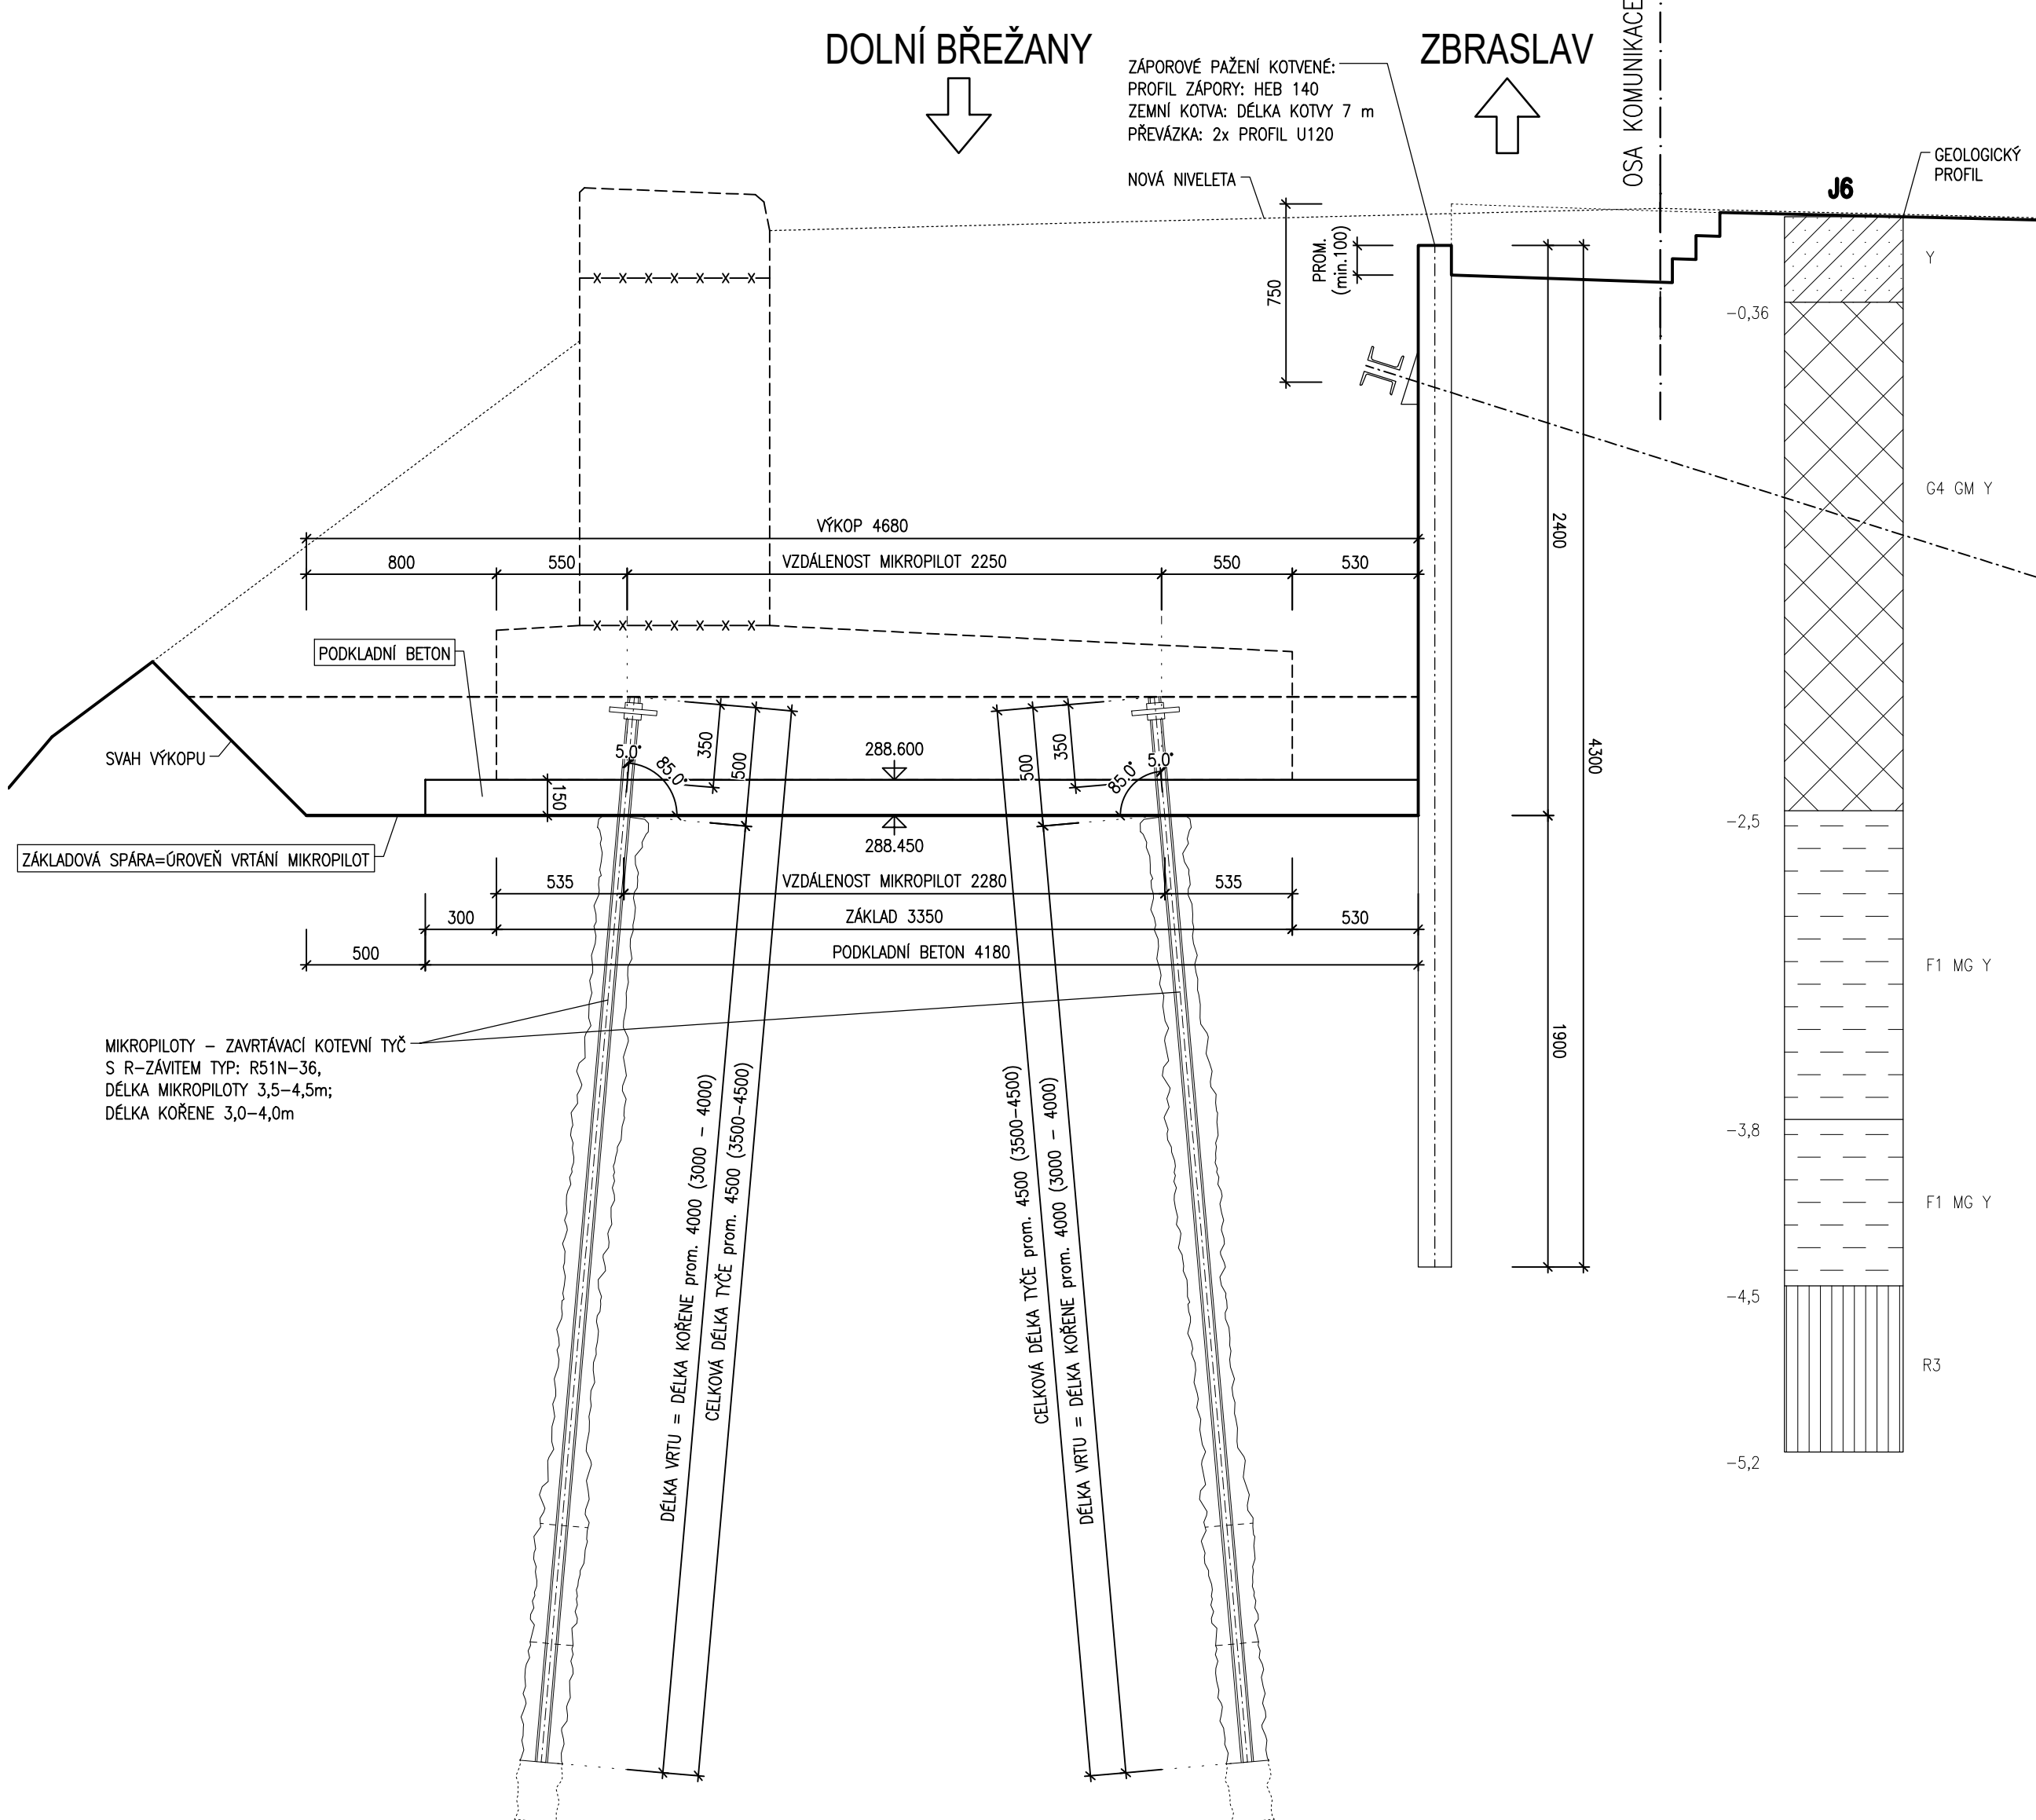


DETAIL UKONČENÍ MIKROPILOTY 1:5

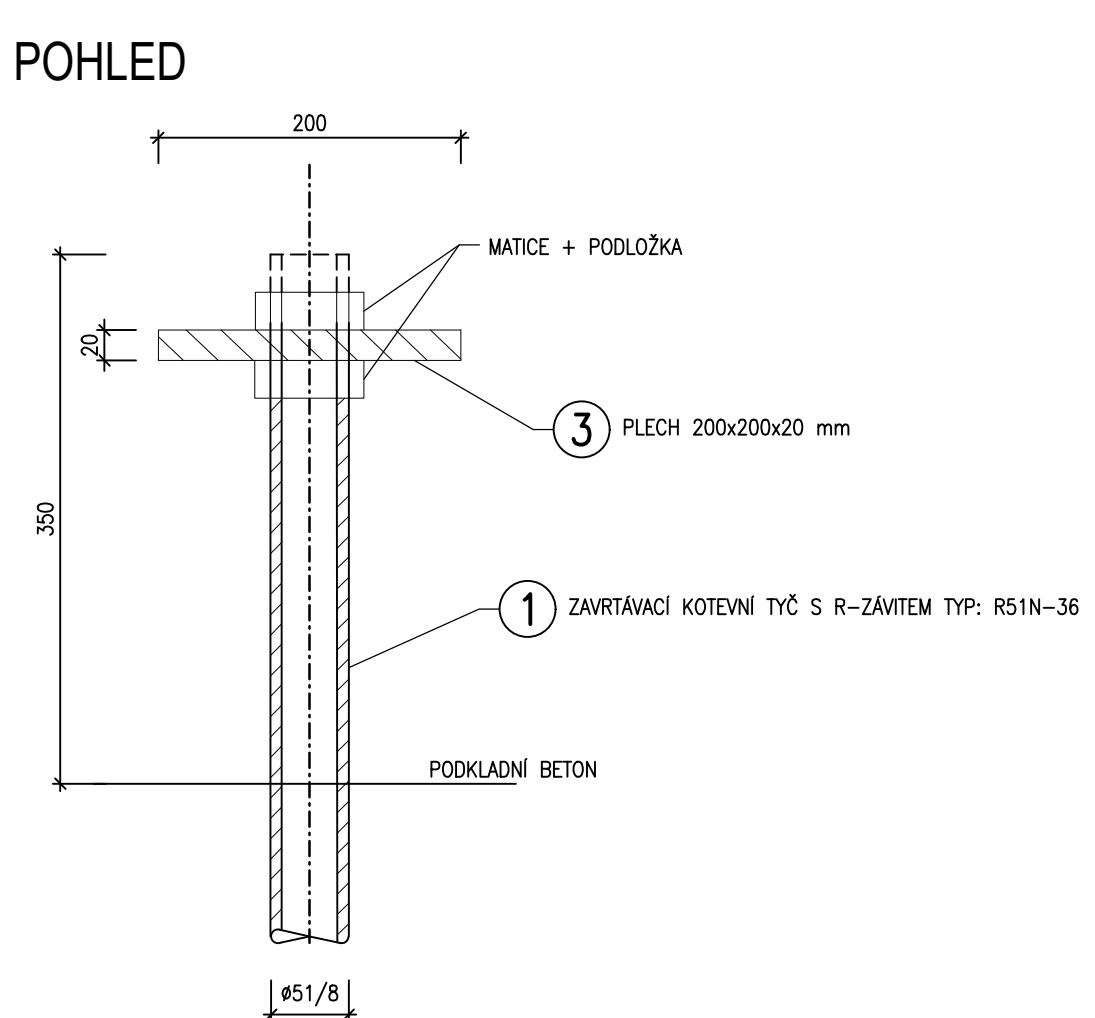

PŮDORYS

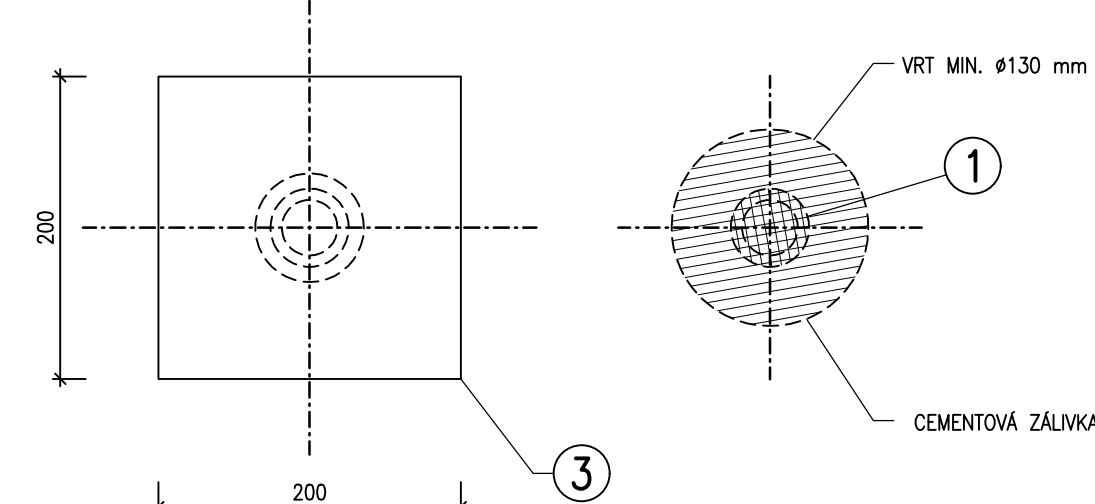

ŘEZ V KOŘENOVÉ ČÁSTI

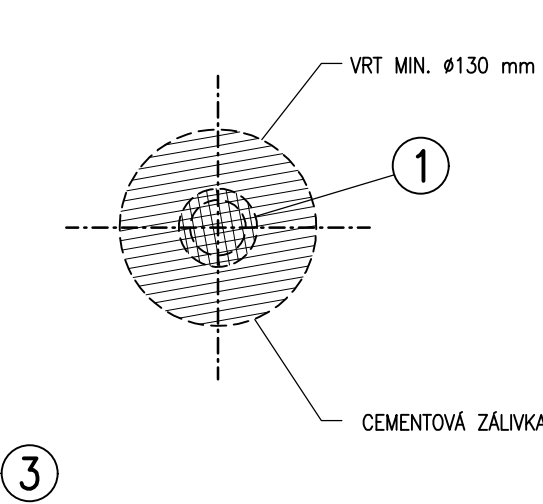


SEZNAM SOUŘADNIC

Vytčení mikropilot

| Opěrná zed č. 5 - mikropiloty |             |              |            |             |                         |                    |                 |                                |        | SO 251.2_05        |
|-------------------------------|-------------|--------------|------------|-------------|-------------------------|--------------------|-----------------|--------------------------------|--------|--------------------|
| RADA BODŮ 05                  |             |              |            |             |                         |                    |                 |                                |        |                    |
| ČÁST                          | Označ. bodu | Číslo bodu   | SOUŘADNICE |             | VÝŠKA HLAVY MIKROPILOTY | CELKOVÁ DÉLKA TYČE | VÝŠKA PATY TYČE | VÝŠKA V ÚROVNI ZAKLADOVÉ SPÁRY | ODKLON | Poznámky           |
|                               |             |              | Y [m]      | X [m]       |                         |                    |                 |                                |        |                    |
| LICOVÁ STRANA                 | 101         | 251 2 05 101 | 743539.055 | 1056872.575 | 290.250                 | 3.50               | 286.76          | 289.750                        | 5      | DILATAČNÍ CELEK D1 |
|                               | 102         | 251 2 05 102 | 743540.305 | 1056872.565 | 290.250                 | 3.50               | 286.76          | 289.750                        | 5      |                    |
|                               | 103         | 251 2 05 103 | 743541.555 | 1056872.615 | 290.250                 | 3.50               | 286.76          | 289.750                        | 5      |                    |
|                               | 104         | 251 2 05 104 | 743542.805 | 1056872.636 | 290.250                 | 3.50               | 286.76          | 289.750                        | 5      |                    |
|                               | 105         | 251 2 05 105 | 743544.055 | 1056872.656 | 290.250                 | 3.50               | 286.76          | 289.750                        | 5      |                    |
|                               | 106         | 251 2 05 106 | 743545.304 | 1056872.676 | 290.250                 | 3.50               | 286.76          | 289.750                        | 5      |                    |
|                               | 107         | 251 2 05 107 | 743546.554 | 1056872.696 | 290.250                 | 3.50               | 286.76          | 289.750                        | 5      |                    |
|                               | 108         | 251 2 05 108 | 743547.804 | 1056872.716 | 290.250                 | 3.50               | 286.76          | 289.750                        | 5      |                    |
|                               | 109         | 251 2 05 109 | 743549.054 | 1056872.736 | 289.850                 | 3.50               | 286.36          | 289.350                        | 5      |                    |
|                               | 110         | 251 2 05 110 | 743550.304 | 1056872.756 | 289.850                 | 3.50               | 286.36          | 289.350                        | 5      |                    |
| LICOVÁ STRANA                 | 111         | 251 2 05 111 | 743551.554 | 1056872.776 | 289.850                 | 3.50               | 286.36          | 289.350                        | 5      | DILATAČNÍ CELEK D2 |
|                               | 112         | 251 2 05 112 | 743552.803 | 1056872.796 | 289.850                 | 3.50               | 286.36          | 289.350                        | 5      |                    |
|                               | 113         | 251 2 05 113 | 743554.053 | 1056872.816 | 289.850                 | 3.50               | 286.36          | 289.350                        | 5      |                    |
|                               | 114         | 251 2 05 114 | 743555.303 | 1056872.836 | 289.850                 | 3.50               | 286.36          | 289.350                        | 5      |                    |
|                               | 115         | 251 2 05 115 | 743556.553 | 1056872.856 | 289.850                 | 3.50               | 286.36          | 289.350                        | 5      |                    |
|                               | 116         | 251 2 05 116 | 743557.803 | 1056872.876 | 289.850                 | 3.50               | 286.36          | 289.350                        | 5      |                    |
|                               | 117         | 251 2 05 117 | 743559.053 | 1056872.896 | 289.650                 | 3.50               | 286.16          | 289.150                        | 5      |                    |
|                               | 118         | 251 2 05 118 | 743560.303 | 1056872.916 | 289.650                 | 3.50               | 286.16          | 289.150                        | 5      |                    |
|                               | 119         | 251 2 05 119 | 743561.552 | 1056872.936 | 289.650                 | 3.50               | 286.16          | 289.150                        | 5      |                    |
|                               | 120         | 251 2 05 120 | 743562.802 | 1056872.956 | 289.650                 | 3.50               | 286.16          | 289.150                        | 5      |                    |
| LICOVÁ STRANA                 | 121         | 251 2 05 121 | 743564.052 | 1056872.976 | 289.650                 | 3.50               | 286.16          | 289.150                        | 5      | DILATAČNÍ CELEK D3 |
|                               | 122         | 251 2 05 122 | 743565.302 | 1056872.996 | 289.650                 | 3.50               | 286.16          | 289.150                        | 5      |                    |
|                               | 123         | 251 2 05 123 | 743566.552 | 1056873.016 | 289.650                 | 3.50               | 286.16          | 289.150                        | 5      |                    |
|                               | 124         | 251 2 05 124 | 743567.802 | 1056873.036 | 289.650                 | 3.50               | 286.16          | 289.150                        | 5      |                    |
|                               | 125         | 251 2 05 125 | 743569.051 | 1056873.056 | 289.450                 | 3.50               | 285.96          | 288.950                        | 5      |                    |
|                               | 126         | 251 2 05 126 | 743570.301 | 1056873.076 | 289.450                 | 3.50               | 285.96          | 288.950                        | 5      |                    |
|                               | 127         | 251 2 05 127 | 743571.551 | 1056873.096 | 289.450                 | 3.50               | 285.96          | 288.950                        | 5      |                    |
|                               | 128         | 251 2 05 128 | 743572.801 | 1056873.116 | 289.450                 | 3.50               | 285.96          | 288.950                        | 5      |                    |
|                               | 129         | 251 2 05 129 | 743574.051 | 1056873.136 | 289.450                 | 3.50               | 285.96          | 288.950                        | 5      |                    |
|                               | 130         | 251 2 05 130 | 743575.301 | 1056873.156 | 289.450                 | 3.50               | 285.96          | 288.950                        | 5      |                    |
| LICOVÁ STRANA                 | 131         | 251 2 05 131 | 743576.550 | 1056873.176 | 289.450                 | 3.50               | 285.96          | 288.950                        | 5      | DILATAČNÍ CELEK D4 |
|                               | 132         | 251 2 05 132 | 743577.800 | 1056873.196 | 289.450                 | 3.50               | 285.96          | 288.950                        | 5      |                    |
|                               | 133         | 251 2 05 133 | 743579.050 | 1056873.216 | 289.250                 | 4.00               | 285.27          | 288.750                        | 5      |                    |
|                               | 134         | 251 2 05 134 | 743580.300 | 1056873.236 | 289.250                 | 4.00               | 285.27          | 288.750                        | 5      |                    |
|                               | 135         | 251 2 05 135 | 743581.550 | 1056873.256 | 289.250                 | 4.00               | 285.27          | 288.750                        | 5      |                    |
|                               | 136         | 251 2 05 136 | 743582.800 | 1056873.276 | 289.250                 | 4.00               | 285.27          | 288.750                        | 5      |                    |
|                               | 137         | 251 2 05 137 | 743584.049 | 1056873.296 | 289.250                 | 4.00               | 285.27          | 288.750                        | 5      |                    |
|                               | 138         | 251 2 05 138 | 743585.299 | 1056873.316 | 289.250                 | 4.00               | 285.27          | 288.750                        | 5      |                    |
|                               | 139         | 251 2 05 139 | 743586.549 | 1056873.336 | 289.250                 | 4.00               | 285.27          | 288.750                        | 5      |                    |
|                               | 140         | 251 2 05 140 | 743587.799 | 1056873.356 | 289.250                 | 4.00               | 285.27          | 288.750                        | 5      |                    |
| LICOVÁ STRANA                 | 141         | 251 2 05 141 | 743589.049 | 1056873.376 | 289.050                 | 4.00               | 285.07          | 288.550                        | 5      | DILATAČNÍ CELEK D5 |
|                               | 142         | 251 2 05 142 | 743590.299 | 1056873.396 | 289.050                 | 4.00               | 285.07          | 288.550                        | 5      |                    |
|                               | 143         | 251 2 05 143 | 743591.548 | 1056873.416 | 289.050                 | 4.00               | 285.07          | 288.550                        | 5      |                    |
|                               | 144         | 251 2 05 144 | 743592.798 | 1056873.436 | 289.050                 | 4.00               | 285.07          | 288.550                        | 5      |                    |
|                               | 145         | 251 2 05 145 | 743594.048 | 1056873.456 | 289.050                 | 4.00               | 285.07          | 288.550                        | 5      |                    |
|                               | 146         | 251 2 05 146 | 743595.298 | 1056873.476 | 289.050                 | 4.00               | 285.07          | 288.550                        | 5      |                    |
|                               | 147         | 251 2 05 147 | 743596.548 | 1056873.496 | 289.050                 | 4.00               | 285.07          | 288.550                        | 5      |                    |
|                               | 148         | 251 2 05 148 | 743597.798 | 1056873.516 | 289.050                 | 4.00               | 285.07          | 288.550                        | 5      |                    |
|                               | 149         | 251 2 05 149 | 743599.048 | 1056873.536 | 288.850                 | 4.50               | 284.47          | 288.450                        | 5      |                    |
|                               | 150         | 251 2 05 150 | 743600.297 | 1056873.556 | 288.850                 | 4.50               | 284.47          | 288.450                        | 5      |                    |
| LICOVÁ STRANA                 | 151         | 251 2 05 151 | 743601.547 | 1056873.576 | 288.850                 | 4.50               | 284.47          | 288.450                        | 5      | DILATAČNÍ CELEK D6 |
|                               | 152         | 251 2 05 152 | 743602.797 | 1056873.596 | 288.850                 | 4.50               | 284.47          | 288.450                        | 5      |                    |
|                               | 153         | 251 2 05 153 | 743604.047 | 1056873.616 | 288.850                 | 4.50               | 284.47          | 288.450                        | 5      |                    |
|                               | 154         | 251 2 05 154 | 743605.297 | 1056873.636 | 288.850                 | 4.50               | 284.47          | 288.450                        | 5      |                    |
|                               | 155         | 251 2 05 155 | 743606.547 | 1056873.656 | 288.850                 | 4.50               | 284.47          | 288.450                        | 5      |                    |
|                               | 156         | 251 2 05 156 | 743607.797 | 1056873.676 | 288.850                 | 4.50               | 284.47          | 288.450                        | 5      |                    |
|                               | 157         | 251 2 05 157 | 743609.046 | 1056873.696 | 288.850                 | 4.50               | 284.47          | 288.450                        | 5      |                    |
|                               | 158         | 251 2 05 158 | 743610.296 | 1056873.716 | 288.850                 | 4.50               | 284.47          | 288.450                        | 5      |                    |
|                               | 159         | 251 2 05 159 | 743611.546 | 1056873.736 | 288.850                 | 4.50               | 284.47          | 288.450                        | 5      |                    |
|                               | 160         | 251 2 05 160 | 743612.796 | 1056873.756 | 288.850                 | 4.50               | 284.47          | 288.450                        | 5      |                    |

ČÍSLOVÁNÍ VYTÝČOVANÝCH BODŮ

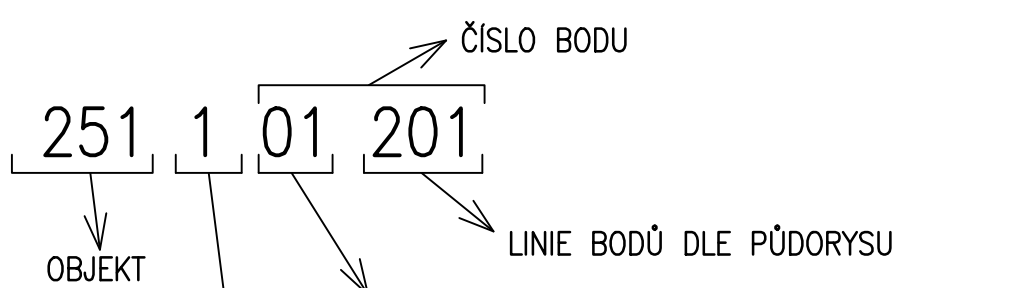

STAVEBNÍ CELEK

- 0 ... HLAVNÍ BODY
- 1 ... VÝKOPY, PAŽENÍ
- 2 ... MIKROPILOTY
- 3 ... SPODNÍ STAVBA/OPĚRNÁ ZED
- 4 ... NOSNÁ KONSTRUKCE
- 5 ... PŘÍSLUŠENSTVÍ

MATERIÁL

CEMENTOVÁ SUSPENZE

POZNÁMKY

- ZHOTOVITEL JE POVINEN PRO VŠECHNY ZEMĚMĚŘICKÉ PRÁCE POSTUPOVAT DLE TKP KAP. 1, ODS. 1.6.3.
- PRO MIKROPILOTY BUDOU POUŽITY INJEKČNÍ ZAVRTÁVACÍ KOTVENÍ TYČE SDA, TYP R51N-36.
- MIKROPILOTY JSOU VYTÝČENY V ÚROVNI ZAKLADOVÉ SPÁRY, TZN. V DOLNÍ ÚROVNI PODKLADNÍHO BETONU.
- PRO PÍPAČNÉ SPOJOVÁNÍ BUDOU POUŽITI ORIGINÁLNÍ SPOJNÍKY.
- SA MOZAVATÁVACÍ TYČ BUDE UKONČENÁ DESKOU 200x200x20 mm A Z OBOU STRAN STAŽENA MATICEMI
- VŠECHNY MIKROPILOTY JSOU ŠIKMÉ 5°
- PROVÁDĚNÍ MIKROPILOT MUŽI BYTI V SOULADU S ČSN EN 14199.
- CEMENTOVÁ SUSPENZE MUSÍ MÍT FINÁLNÍ PĚNOST MÍN. C25/30
- PRO ČERPÁNÍ VODY ZE DNA ZAKLADOVÉ SPÁRY BUDOU ZBUDOVÁVANY JMKY.
- DÉLKA SAMOZAVRTNÉ TYČE BUDE MINIMÁLNĚ 3,5-4,5m, DÉLKA MIKROPILOTY S OHLEDEM NA POUŽITÍ ZTRACENÉ VRTACÍ KORUNKY BUDE DLE ZVYKLOSTI DODAVATELE.

INJEKTAŽNÍ CEM 32,5R, C25/30

ZBRASLAV

VÝKAZ MATERIÁLU

MIKROPILOTY OPĚRNÁ ZEĎ 05

VÝKAZ MATERIÁLU

| OZN. | POPIS                  | DÉLKA [m] | HMOTNOST [kg/m] | POČET [ks] | DÉLKA CELKEM [m] | HMOTNOST [kg] |
|------|------------------------|-----------|-----------------|------------|------------------|---------------|
| 1    | TYČ Ø51mm              | 3.50      | 7.7             | 1          | 3.500            | 26.95         |
| 3    | PLECH 200/200,TL. 20mm | -         | 6.28            | 1          | -                | 6.28          |

HMOTNOST CELKEM ... PRO 1 TYČ DL. 3,5 m

33.23 kg

HMOTNOST CELKEM ... PRO VŠECH 64 TYČÍ

2126.72 kg

POZNÁMKY:

- JE VÝKÁZANA CELKOVÁ DÉLKA TYČE 3,5 m VČETNÉ PŘESAHU 0,35 m DO ZÁKLADU

MIKROPILOTY OPĚRNÁ ZEĎ 05

VÝKAZ MATERIÁLU

| OZN. | POPIS                  | DÉLKA [m] | HMOTNOST [kg/m] | POČET [ks] | DÉLKA CELKEM [m] | HMOTNOST [kg] |
|------|------------------------|-----------|-----------------|------------|------------------|---------------|
| 1    | TYČ Ø51mm              | 4.00      | 7.7             | 1          | 4.000            | 30.80         |
| 3    | PLECH 200/200,TL. 20mm | -         | 6.28            | 1          | -                | 6.28          |

HMOTNOST CELKEM ... PRO 1 TYČ DL. 4.0 m

37.08 kg

HMOTNOST CELKEM ... PRO VŠECH 32 TYČÍ

1186.56 kg

POZNÁMKY:

- JE VÝKÁZANA CELKOVÁ DÉLKA TYČE 4,0 m VČETNÉ PŘESAHU 0,35 m DO ZÁKLADU

MIKROPILOTY OPĚRNÁ ZEĎ 05

VÝKAZ MATERIÁLU

| OZN. | POPIS                  | DÉLKA [m] | HMOTNOST [kg/m] | POČET [ks] | DÉLKA CELKEM [m] | HMOTNOST [kg] |
|------|------------------------|-----------|-----------------|------------|------------------|---------------|
| 1    | TYČ Ø51mm              | 4.50      | 7.7             | 1          | 4.500            | 34.65         |
| 3    | PLECH 200/200,TL. 20mm | -         | 6.28            | 1          | -                | 6.28          |

HMOTNOST CELKEM ... PRO 1 TYČ DL. 4.5 m

40.93 kg

HMOTNOST CELKEM ... PRO VŠECH 24 TYČÍ

982.32 kg

POZNÁMKY:

- JE VÝKÁZANA CELKOVÁ DÉLKA TYČE 4,5 m VČETNÉ PŘESAHU 0,35 m DO ZÁKLADU

PŘEDKONCEPT

|                   |  |                                                                            |  |               |  |          |  |        |  |
|-------------------|--|----------------------------------------------------------------------------|--|---------------|--|----------|--|--------|--|
| OZNAC.            |  | TEXT ZMĚNY - ODŮVODNĚNÍ                                                    |  | TABULKA ZMĚN  |  | DATUM    |  | PODPIS |  |
| Název stavby      |  | II/101 Dolní Břežany - Zbraslav                                            |  | ČÍSLO OBJEKTU |  | SO 251.2 |  |        |  |
| Objednatel stavby |  | Krajská správa a údržba silnic Středočeského kraje, příspěvková organizace |  |               |  |          |  |        |  |