



TVAR OPĚRNÉ ZDI - POHLED - ČÁST 1.

POHLED V LÍCI B1-B1 1:50
DILATAČNÍ CELEK "D4" - "D8"

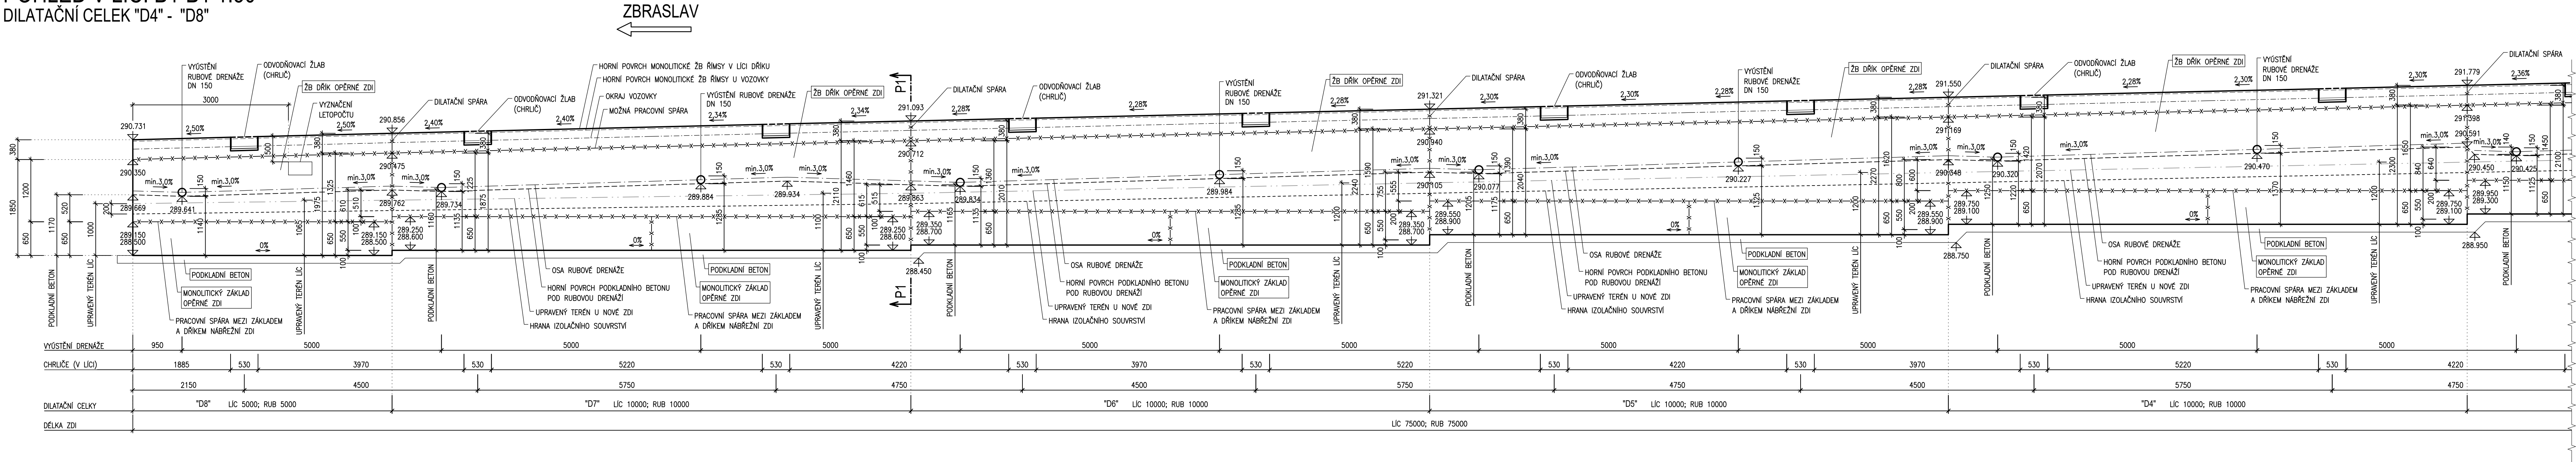

DILATAČNÍ CELEK "D1" - "D3"

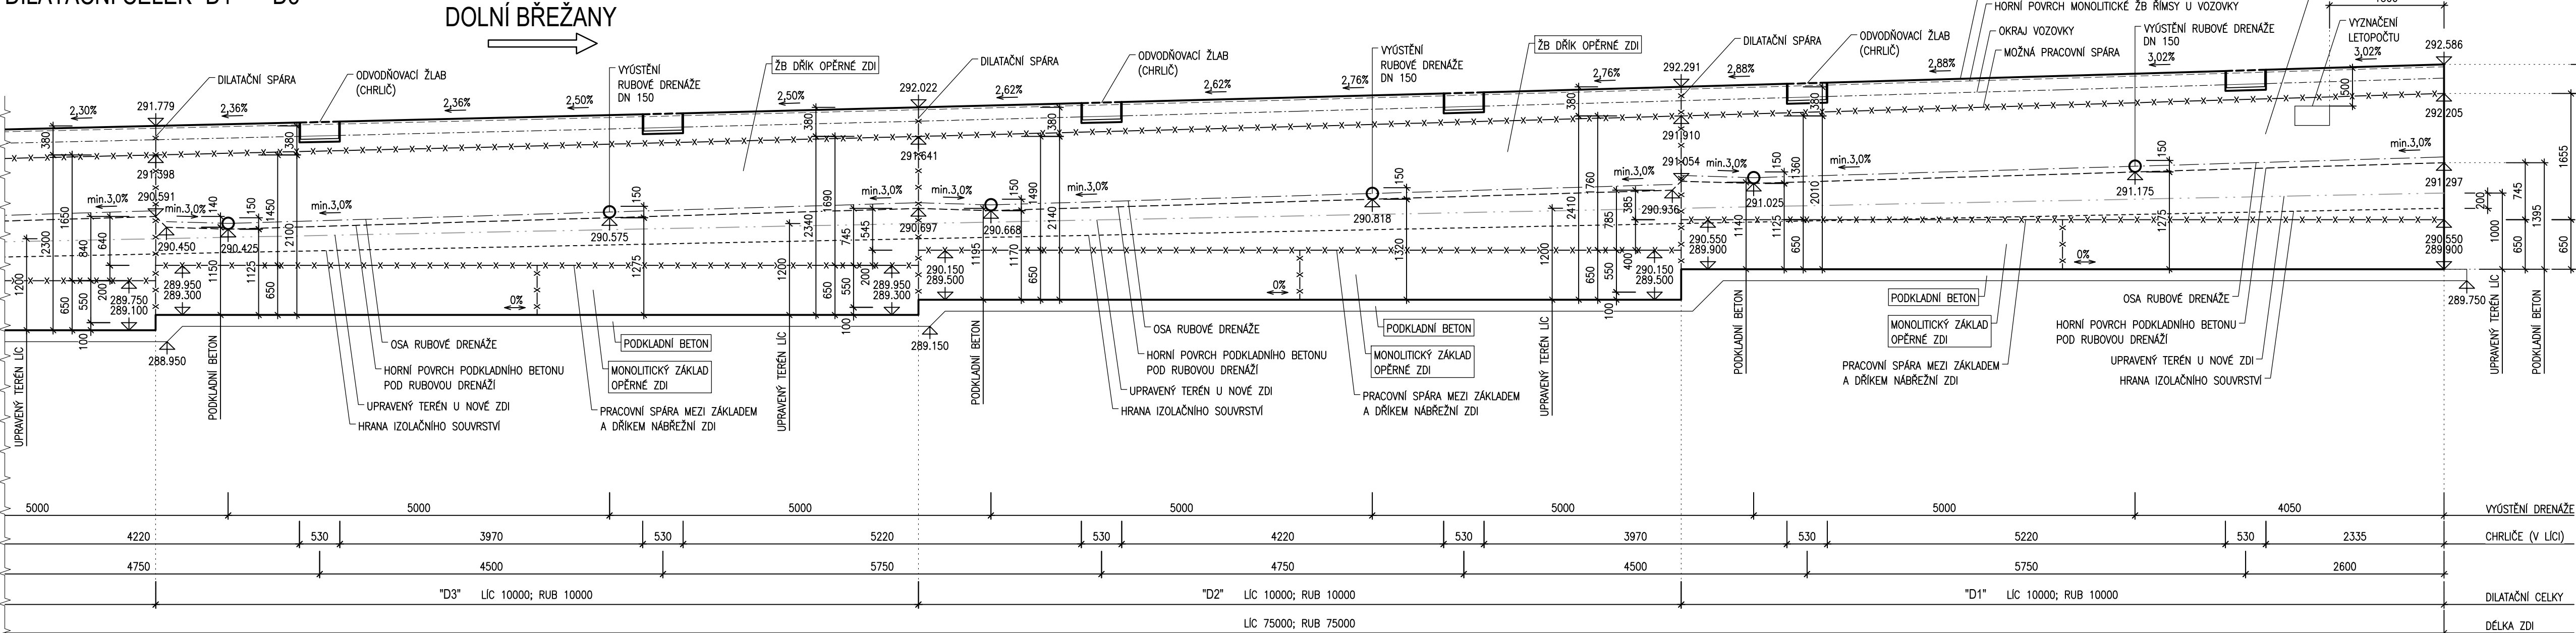

PŘEDKONCEPT

OZNAČ.		TEXT ZMĚNY - ODŮVODNĚNÍ	DATUM
		TABULKA ZMĚN	PODPIS
Název stavby		ČÍSLO OBJEKTU	
II/101 Dolní Břežany - Zbraslav		SO 251.2	
Objednatel stavby			
		Krajská správa a údržba silnic Středočeského kraje, příspěvková organizace Zborovská 811/11, 150 21 Praha 5-Smíchov	
Autorský dozor			
		GeoTec-GS, a.s. Chmelova 2920/6, 106 00 Praha 10	
Technický dozor investora		RAZÍTKO	
		TES + SGS + SGG vedoucí sdružení: TES Consulting, s.r.o. V Olšinách 2300/75, 100 00 Praha 10-Strašnice	
		DATUM	
		PODPIS	
Zhotovitel stavby		RAZÍTKO	
		M-SILNICE a.s. Husova 1697, 530 03 Pardubice www.msilnice.cz	
		DATUM	
		PODPIS	
Koordinator RDS		RAZÍTKO	
		M - PROJEKCE s. r. o. Reslova 956/13, 500 02 Hradec Králové www.m-projekce.cz	
		DATUM	
		PODPIS	
Souřadnicový systém: S-JTSK		Výškový systém: Bpv	
Zpracovatel stavebního objektu/části:			
Projektční kancelář PRIS spol. s r.o. Osova 717/20, 625 00 Brno-Starý Lískovec www.pris.cz			
Vypracoval: Ilona Synková		Hlavní inženýr projektu: Ing. Jiří Ehrenberger	
Odpovědný projektant: Ing. Martin Řehulka		Kontroloval: Ing. Jiří ŠRUBAR	
Číslo zakázky: 25-122-02		Datum: 06/2026	
Objekt/část:		Razítko:	
SO 251.2 - OPĚRNÉ ZDI ZED č. 05		 PROJEKČNÍ KANCELÁŘ PRIS spol. s r. o. OSOVA 20, 625 00 BRNO	
Příloha:		Měřítko: 1:50	
TVAR OPĚRNÉ ZDI - POHLED - ČÁST 1.		Stupeň: RDS	
		Číslo přílohy: 104_TVR1	
		Souprava:	