TVAR OPĚRNÉ ZDI - PŮDORYS, ŘEZ, DETAILY - ČÁST 2.

PŮDORYS 1:100

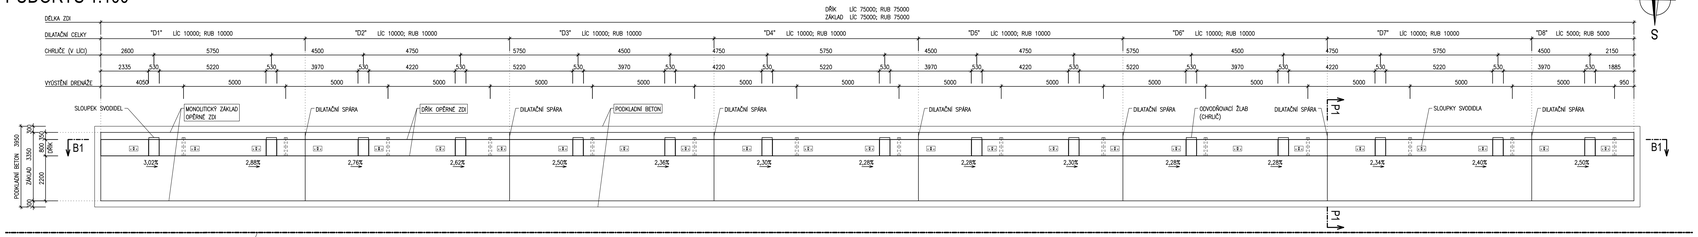

DOLNÍ BŘEŽANY

OSA KOMUNIKACE II/101

ZBRASLAV

PŘÍČNÝ ŘEZ P1-P1 km 1,060 000 1:25

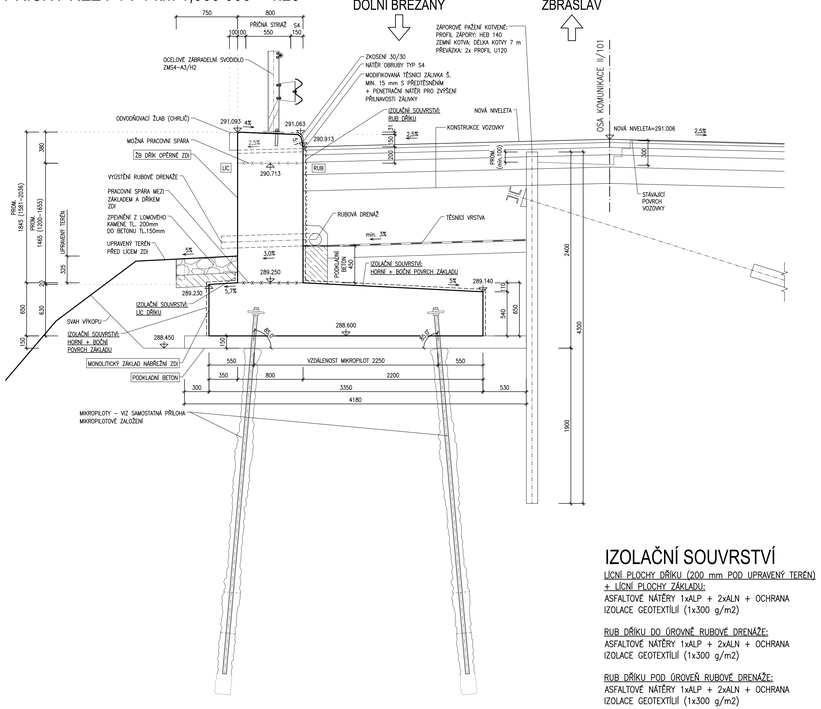

DETAIL PROSTUPU RUBOVÉ DRENÁŽE

ŘEZ DŘÍKEM ZDI 1:5

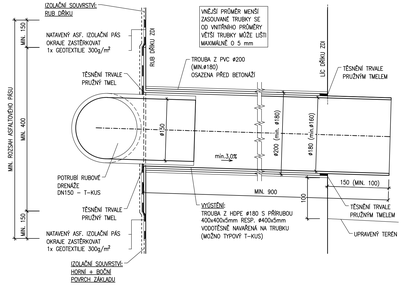

DILATAČNÍ SPÁRA 1:10

OPĚRNÁ ZEĎ - OPĚRNÁ ZEĎ

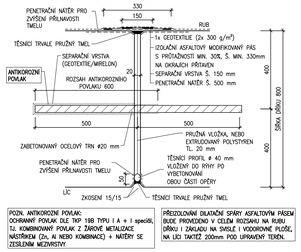

IZOLAČNÍ SOUVRSTVÍ

LÍCNÍ PLOCHY DŘÍKU (200 mm POD UPRAVENÝ TERÉN) + LÍCNÍ PLOCHY ZÁKLADU:
ASFALTOVÉ NÁTĚRY 1xALP + 2xALN + OCHRANA IZOLACE GEOTEXTILIÍ (1x300 g/m2)

RUB DŘÍKU DO ÚROVNĚ RUBOVÉ DRENÁŽE:
ASFALTOVÉ NÁTĚRY 1xALP + 2xALN + OCHRANA IZOLACE GEOTEXTILIÍ (1x300 g/m2)

RUB DŘÍKU POD ÚROVEŇ RUBOVÉ DRENÁŽE:
ASFALTOVÉ NÁTĚRY 1xALP + 2xALN + OCHRANA IZOLACE GEOTEXTILIÍ (1x300 g/m2)

HORNÍ + BOČNÍ POVRCH ZÁKLADU:
ASFALTOVÉ NÁTĚRY 1xALP + 2xALN + OCHRANA IZOLACE GEOTEXTILIÍ (1x300 g/m2)

DETAIL ULOŽENÍ RUBOVÉ DRENÁŽE

ŘEZ RUBOVU DRENÁŽÍ ZA RUBEM 1:10

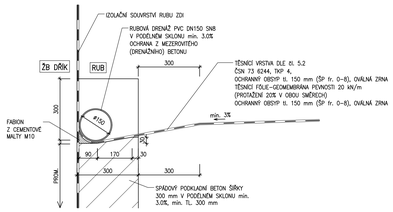

VODOROVNÁ PRACOVNÍ SPÁRA MEZI ZÁKLADEM A DŘÍKEM 1:10

POZNÁMKY

1. HRANICE IZOLAČNÍCH NÁTĚRŮ JE VYKRESLENA JAKO PŘEDPOKLÁDANÁ, NA STAVBĚ SE MŮŽE UPRAVIT DLE SKUTEČNÉHO DOSYPÁNÍ SVAHU. UKONČENÍ JE 200 mm POD UPRAVENÝM TERÉNEM.
2. HRANA UPRAVENÉHO TERÉNU U LÍCE OPĚRNÉ ZDI JE VYKRESLENA JAKO PŘEDPOKLÁDANÁ, NA STAVBĚ SE MŮŽE UPRAVIT DLE SKUTEČNÉHO PRŮBĚHU STÁVAJÍCÍHO TERÉNU S OHLEDEM NA VÝSTŘELNÍ RUBOVÉ DRENÁŽE NAD UPRAVENÝ TERÉN
3. VŠECHNY HRANY SE ZKOSÍ 20/20, POKUD NENÍ UVEDENO JINAK
4. SOUŘADNICE A VÝŠKY VYTYČENÍ OPĚRNÉ ZDI JE SOUČÁSTÍ SAMOSTATNÉ PŘÍLOHY
5. VEŠKERÉ DETAILY BUDOU PROVEDENY DLE PŘÍSLUŠNÝCH VL, POKUD NEJSOU ROZKRESLENY V PROJEKTOVÉ DOKUMENTACI

VYZNAČENÍ LETOPOČTU 1:5

POHLED

ŘEZ I - I

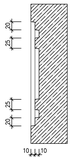

CELKEM KUSŮ LETOPOČTŮ: 2 ks

ODVODŇOVACÍ ŽLAB (CHRLIČ)

PŘÍČNÝ ŘEZ ŽLABEM 1:10

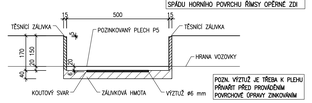

PODÉLNÝ ŘEZ ŽLABEM 1:10

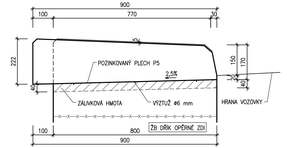

ODVODŇOVACÍ ŽLAB (CHRLIČ)

PŮDORYS ŽLABU 1:25

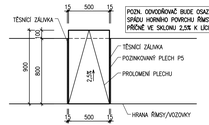

CELKEM KUSŮ CHRLIČŮ: 15 ks

STAVEBNÍ MATERIÁLY

BETONY BUDOU PROVEDENY DLE ČSN EN 206

KONSTRUKČNÍ BETONY:

ŽB ZÁKLAD	**C30/37** XD2, XF2 ,XC2 (CZ,F.1.2) – Cl 0,2; D_{max} 22 – S3	
ŽB DŘÍK	**C30/37** XD3, XF4, XC4 (CZ,F.1.2) – Cl 0,2; D_{max} 22 – S3	

OSTATNÍ BETONY:

PODKLADNÍ BETON	**C12/15** X0	(CZ,F.1.2) – Cl 1,0; D_{max} 22 – S3
PODKLADNÍ BETON – RUBOVÁ DRENÁŽ	**C8/10** X0	(CZ,F.1.2) – Cl 1,0; D_{max} 22 – S3
PODKLADNÍ BETON – SCHODIŠTĚ, DLAŽBY	**C20/25** XF3, XD2	(CZ,F.1.2) – Cl 0,2; D_{max} 22 – S3
BETONOVÉ PRAHY	**C30/37** XF4, XD3	(CZ,F.1.2) – Cl 0,2; D_{max} 22 – S3

BETONÁŘSKÁ VÝZTUŽ:

OCEL **B500B**

PRACOVNÍ, DILATAČNÍ SPÁRY A TĚSNĚNÍ

PENETRAČNÍ NÁTĚR

– KOMPONENTNÍ AKTIVAČNÍ NÁTĚR NA BÁZI EPOXIDU – POLYURETANOVÁ PRYSKYŘICE
– OBJEMOVÁ HMOTNOST 0,9 kg/l
– VISKOZITA 10–15 MPa.s
– BOD VZPLANUTÍ < 21 °C

TĚSNÍCÍ TMEL dle ČSN EN ISO 11600 (F-25-HM-M1p), barva šedá

– F – stavební (konstrukční) tmel
– 25 – třída tmelu dle tab.1
– HM – dle sekantového modulu tažnosti vysokomodulový
– M1p – tmel zkoušen na podkladní maltě s penetrací

Tmel musí vyhovovat požadavků dle ČSN EN ISO 11600 tab.3 a tab.4.
Pro těsnění je navržena elastická 1-komponentní tmelící hmota:

– báze tmelu	polyuretanová vytvrzující vzdušnou vlhkostí
– objemová hmotnost	~1,3 kg/l
– mez protažení	cca. 400%
– pevnost v tahu	1,5 N/ mm2
– pevnost v roztržení	7 N/mm2
– modul pružnosti E	~0,6 N/ mm2 (po 28 dnech) při teplotě –20 °C
– tepelná odolnost	– 40 °C až + 80 °C
– tvrdost Shore A	35

PŘEDKONCEPT

OZNAČ.	TEXT ZMĚNY - ODVODNĚNÍ	DATUM	PODPIS
	TABULKA ZMĚN		

Název stavby: II/101 Dolní Břežany - Zbraslav
Číslo objektu: SO 251.2

Objednatel stavby: Krajská správa a údržba silnic Středočeského kraje, příspěvková organizace, Zborovská 81/11, 150 21 Praha 5-Smíchov

Autorský dozor: GeoTec-GS, a.s., Chmelová 2920/6, 106 00 Praha 10

Technický dozor investora: TES + SGS + SGG, vedoucí sdružení: TES Consulting, s.r.o., V Olšinách 2300/75, 100 00 Praha 10-Strašnice

Zhotovitel stavby: M-SILNICE a.s., Husova 1697, 530 03 Pardubice, www.msilnice.cz

Koordinátor BOZP: M - PROJEKCE s. r.o., Resslova 956/13, 500 02 Hradec Králové, www.m-projekce.cz

Souřadnicový systém: S-JTSK; Výškový systém: Bpv

Zpracovatel stavebního objektu/části: Projekční kancelář PRIS spol. s r.o., Osová 717/20, 625 00 Brno-Starý Lískovec, www.pris.cz

Vypracoval: Ilona Synková		Hlavní inženýr projektu: Ing. Jiří Ehrenberger	Razítko: PROJEKČNÍ KANCELÁŘ PRIS spol. s r.o. OSOVÁ 20, 625 00 BRNO
Odpovědný projektant: Ing. Martin Řehulka		Kontroloval: Ing. Jiří ŠRUBAŘ	
Číslo zakázky: 25-122-02		Datum: 06/2026	

Objekt/část: SO 251.2 - OPĚRNÉ ZDI ZEĎ č. 05	Měřítko: 1:100; 1:25; 1:5	Soupravo:
	Stupeň: RDS	
Příloha: TVAR OPĚRNÉ ZDI - PŮDORYS, ŘEZ, DETAILY - ČÁST 2.	Číslo přílohy: 105_TVR2	