



VYTYČENÍ OPĚRNÉ ZDI  
PŮDORYS 1:100

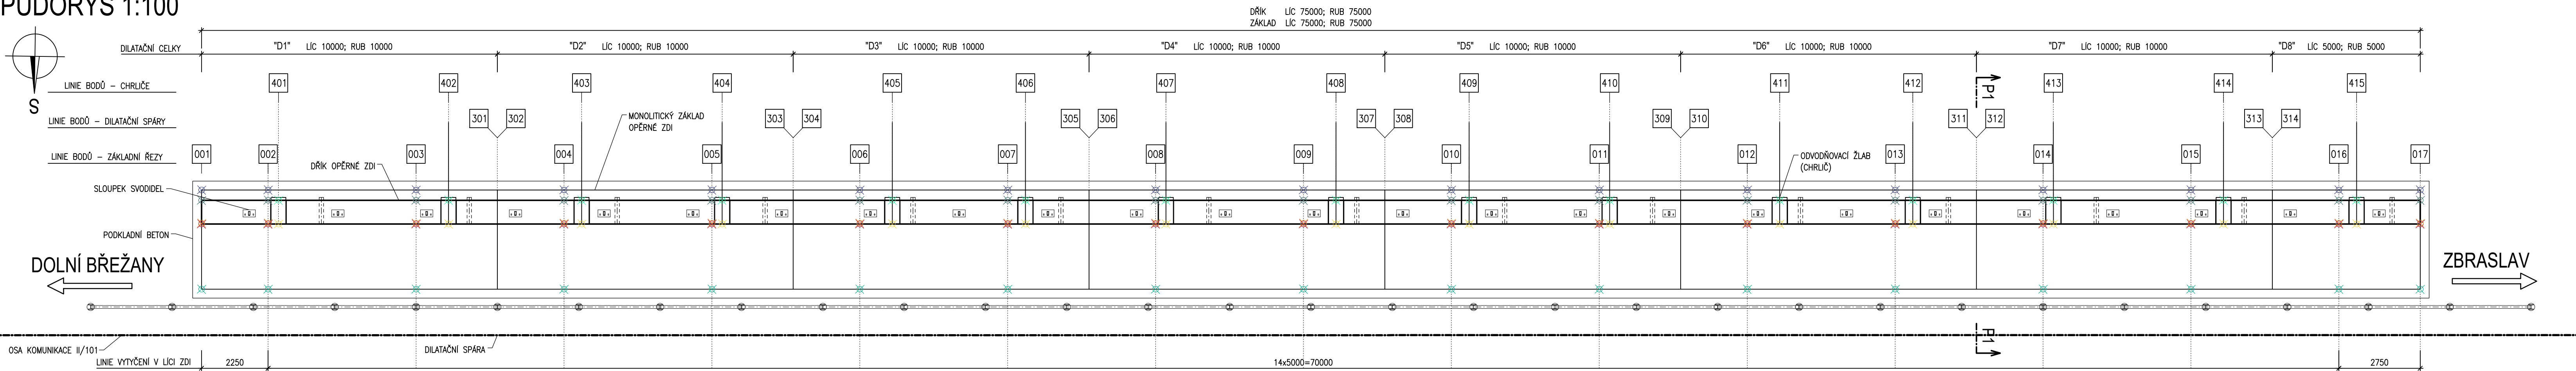

SCHEMA ČÍSLOVÁNÍ BODŮ P1-P1 1:25

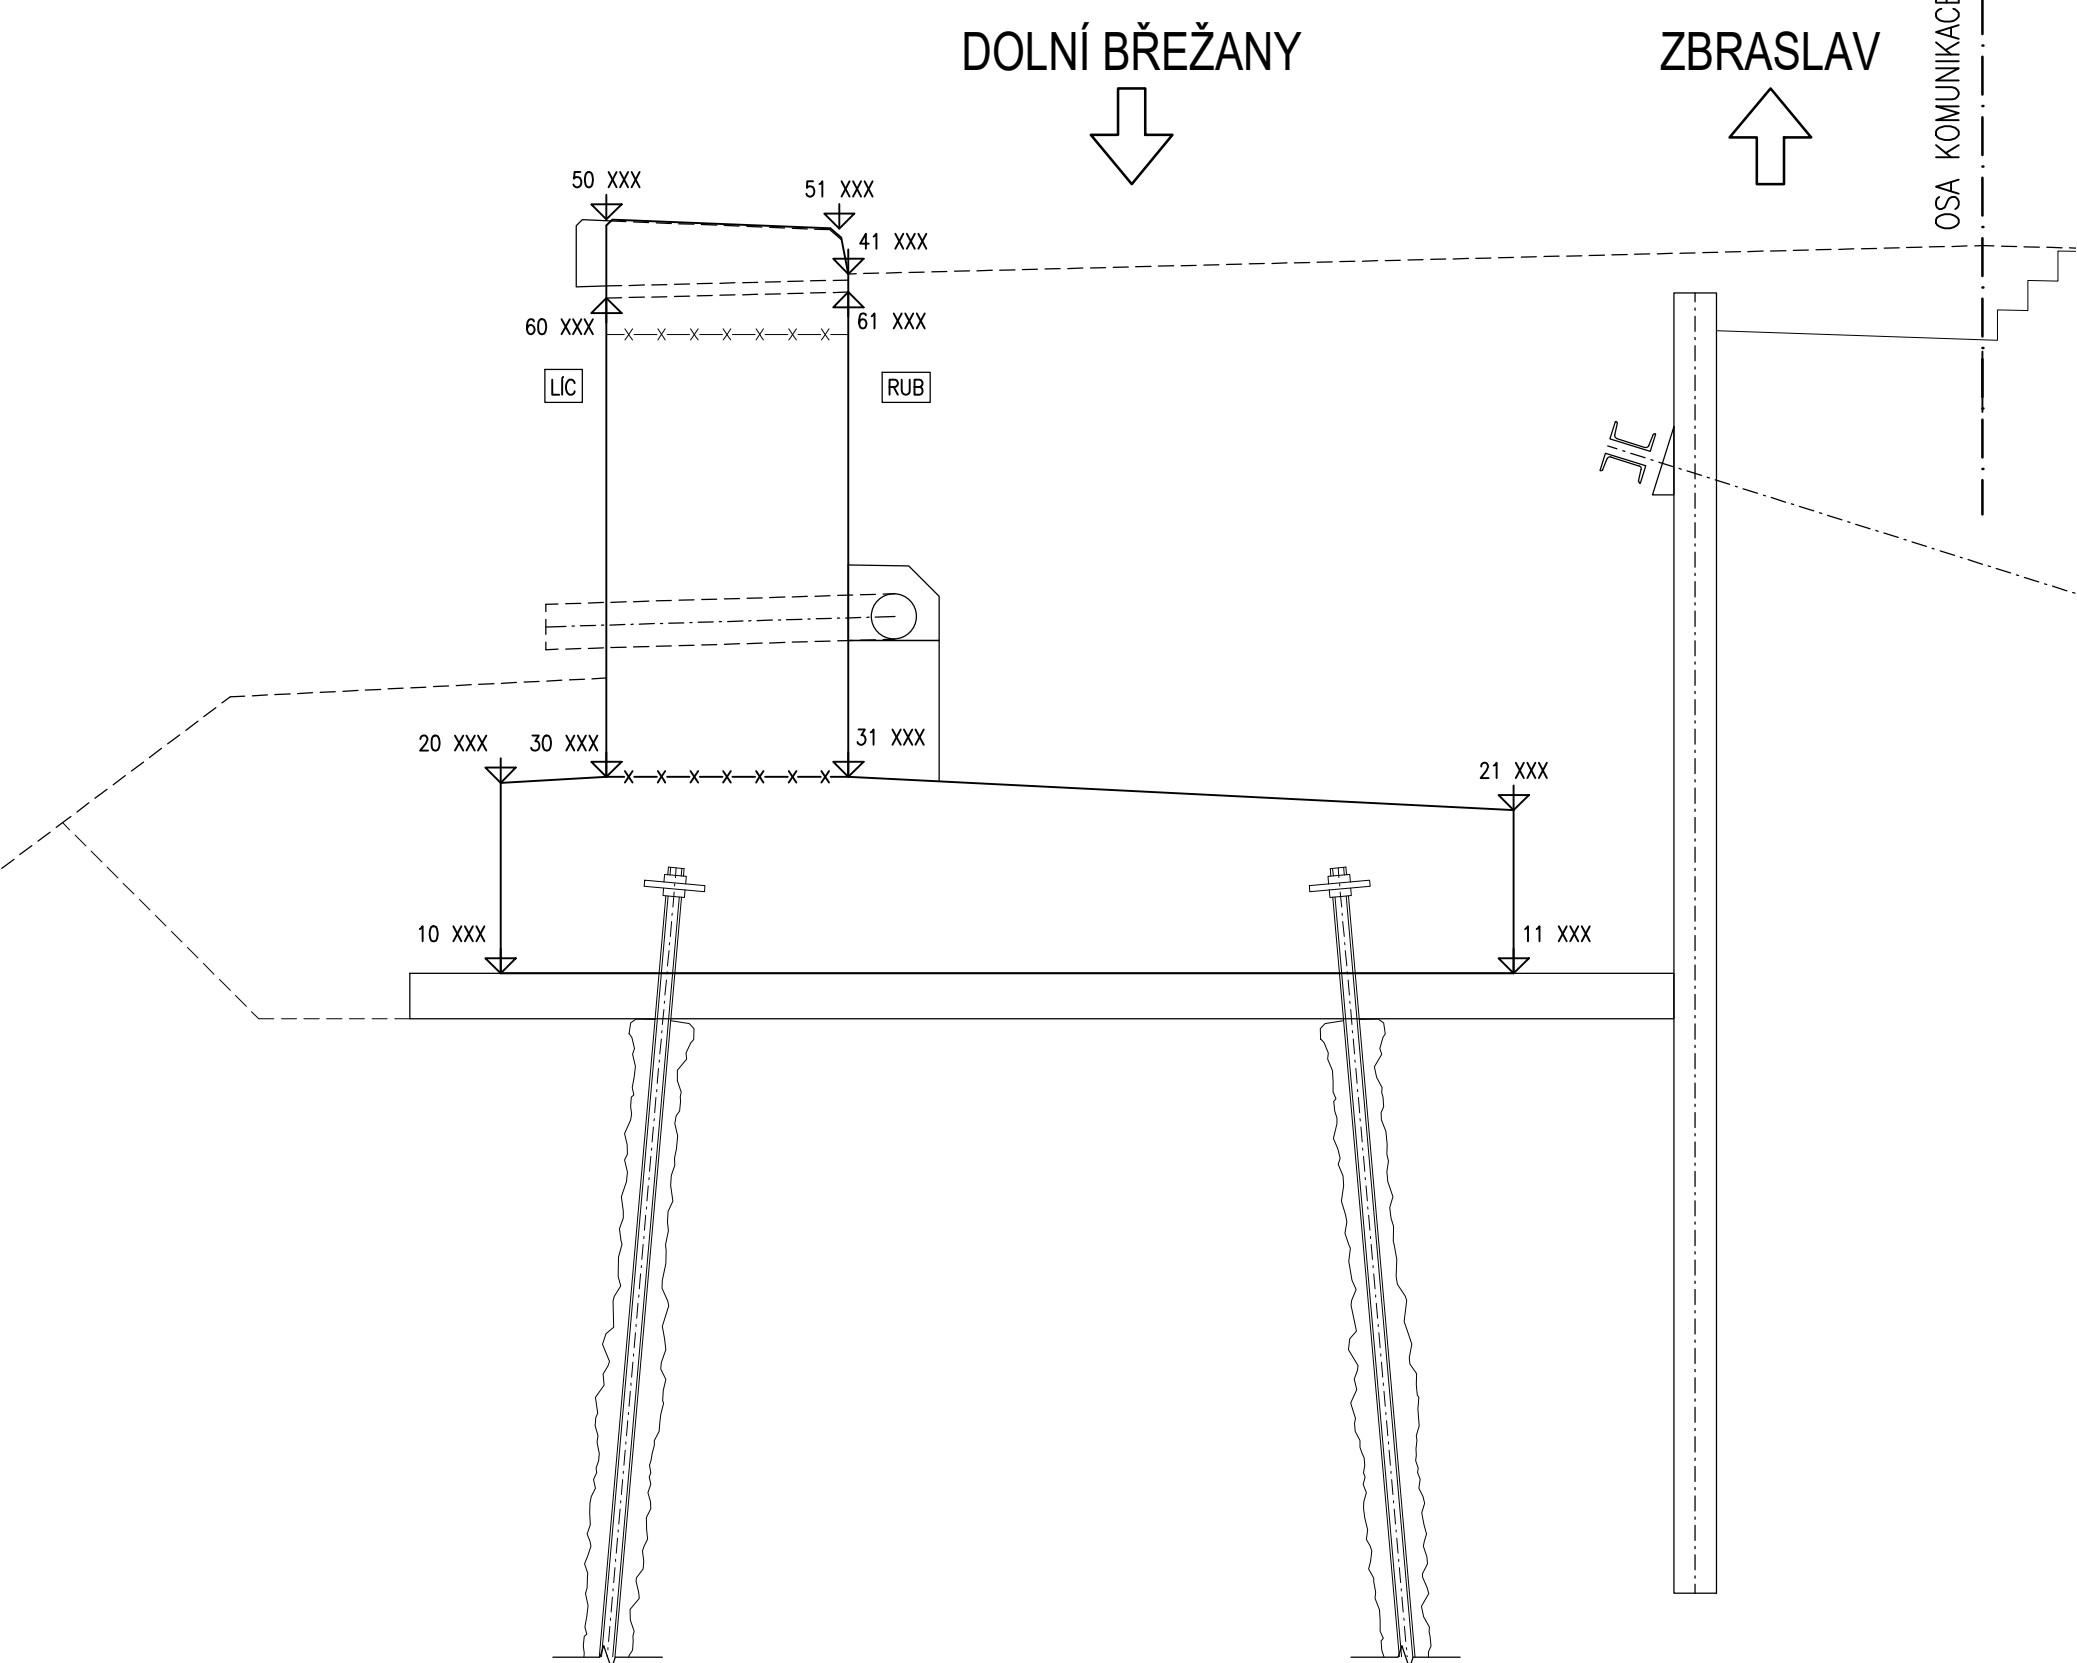

SEZNAM SOUŘADNIC

| Vytyčení tvaru opěrné zdi        |                          |                 |                |             |
|----------------------------------|--------------------------|-----------------|----------------|-------------|
| Opěrná zeď č. 5 - vytyčení tvaru |                          |                 |                |             |
| OPĚRNÁ ZED' 05                   |                          |                 |                |             |
| RADA BODŮ                        | Označ. Bodu dle půdorysu | Číslo bodu      | SOUŘADNICE     | Poznámky    |
|                                  |                          |                 | Y [m]<br>X [m] |             |
| 60                               | 401                      | 251 3 05 60 401 | 743541.002     | 1056872.794 |
|                                  | 402                      | 251 3 05 60 402 | 743546.751     | 1056872.886 |
|                                  | 403                      | 251 3 05 60 403 | 743551.251     | 1056872.958 |
|                                  | 404                      | 251 3 05 60 404 | 743556.000     | 1056873.034 |
|                                  | 405                      | 251 3 05 60 405 | 743561.749     | 1056873.126 |
|                                  | 406                      | 251 3 05 60 406 | 743566.249     | 1056873.199 |
|                                  | 407                      | 251 3 05 60 407 | 743570.998     | 1056873.275 |
|                                  | 408                      | 251 3 05 60 408 | 743576.747     | 1056873.367 |
|                                  | 409                      | 251 3 05 60 409 | 743581.247     | 1056873.439 |
|                                  | 410                      | 251 3 05 60 410 | 743585.996     | 1056873.515 |
|                                  | 411                      | 251 3 05 60 411 | 743591.745     | 1056873.608 |
|                                  | 412                      | 251 3 05 60 412 | 743596.245     | 1056873.680 |
|                                  | 413                      | 251 3 05 60 413 | 743600.994     | 1056873.756 |
|                                  | 414                      | 251 3 05 60 414 | 743606.744     | 1056873.848 |
|                                  | 415                      | 251 3 05 60 415 | 743611.243     | 1056873.920 |

| Vytyčení tvaru opěrné zdi        |                          |                 |                |             |
|----------------------------------|--------------------------|-----------------|----------------|-------------|
| Opěrná zeď č. 5 - vytyčení tvaru |                          |                 |                |             |
| OPĚRNÁ ZED' 05                   |                          |                 |                |             |
| RADA BODŮ                        | Označ. Bodu dle půdorysu | Číslo bodu      | SOUŘADNICE     | Poznámky    |
|                                  |                          |                 | Y [m]<br>X [m] |             |
| 61                               | 401                      | 251 3 05 61 401 | 743541.015     | 1056871.994 |
|                                  | 402                      | 251 3 05 61 402 | 743546.754     | 1056872.086 |
|                                  | 403                      | 251 3 05 61 403 | 743551.263     | 1056872.158 |
|                                  | 404                      | 251 3 05 61 404 | 743556.013     | 1056872.234 |
|                                  | 405                      | 251 3 05 61 405 | 743561.762     | 1056872.327 |
|                                  | 406                      | 251 3 05 61 406 | 743566.262     | 1056872.399 |
|                                  | 407                      | 251 3 05 61 407 | 743571.011     | 1056872.475 |
|                                  | 408                      | 251 3 05 61 408 | 743576.760     | 1056872.567 |
|                                  | 409                      | 251 3 05 61 409 | 743581.260     | 1056872.639 |
|                                  | 410                      | 251 3 05 61 410 | 743586.009     | 1056872.715 |
|                                  | 411                      | 251 3 05 61 411 | 743591.758     | 1056872.808 |
|                                  | 412                      | 251 3 05 61 412 | 743596.258     | 1056872.880 |
|                                  | 413                      | 251 3 05 61 413 | 743600.997     | 1056872.956 |
|                                  | 414                      | 251 3 05 61 414 | 743606.746     | 1056873.048 |
|                                  | 415                      | 251 3 05 61 415 | 743611.256     | 1056873.120 |

| Vytyčení tvaru opěrné zdi        |                          |                 |                              |             |
|----------------------------------|--------------------------|-----------------|------------------------------|-------------|
| Opěrná zeď č. 5 - vytyčení tvaru |                          |                 |                              |             |
| OPĚRNÁ ZED' 05                   |                          |                 |                              |             |
| RADA BODŮ                        | Označ. Bodu dle půdorysu | Číslo bodu      | SOUŘADNICE                   | Poznámky    |
|                                  |                          |                 | Y [m]<br>X [m]<br>Z [m.n.m.] |             |
| 10                               | 001                      | 251 3 05 10 001 | 743538.397                   | 1056873.102 |
|                                  | 002                      | 251 3 05 10 002 | 743540.647                   | 1056873.138 |
|                                  | 003                      | 251 3 05 10 003 | 743545.646                   | 1056873.218 |
|                                  | 004                      | 251 3 05 10 004 | 743550.645                   | 1056873.298 |
|                                  | 005                      | 251 3 05 10 005 | 743555.645                   | 1056873.379 |
|                                  | 006                      | 251 3 05 10 006 | 743560.644                   | 1056873.459 |
|                                  | 007                      | 251 3 05 10 007 | 743565.643                   | 1056873.539 |
|                                  | 008                      | 251 3 05 10 008 | 743570.643                   | 1056873.619 |
|                                  | 009                      | 251 3 05 10 009 | 743575.642                   | 1056873.699 |
|                                  | 010                      | 251 3 05 10 010 | 743580.641                   | 1056873.779 |
|                                  | 011                      | 251 3 05 10 011 | 743585.641                   | 1056873.860 |
|                                  | 012                      | 251 3 05 10 012 | 743590.640                   | 1056873.940 |
|                                  | 013                      | 251 3 05 10 013 | 743595.639                   | 1056874.020 |
|                                  | 014                      | 251 3 05 10 014 | 743600.639                   | 1056874.100 |
|                                  | 015                      | 251 3 05 10 015 | 743605.638                   | 1056874.180 |
| 20                               | 016                      | 251 3 05 20 016 | 743610.638                   | 1056874.261 |
|                                  | 017                      | 251 3 05 20 017 | 743615.637                   | 1056874.341 |
|                                  | 018                      | 251 3 05 20 018 | 743620.636                   | 1056874.421 |
|                                  | 019                      | 251 3 05 20 019 | 743625.635                   | 1056874.501 |
|                                  | 020                      | 251 3 05 20 020 | 743630.634                   | 1056874.581 |
|                                  | 021                      | 251 3 05 20 021 | 743635.633                   | 1056874.661 |
|                                  | 022                      | 251 3 05 20 022 | 743640.632                   | 1056874.741 |
|                                  | 023                      | 251 3 05 20 023 | 743645.631                   | 1056874.821 |
|                                  | 024                      | 251 3 05 20 024 | 743650.630                   | 1056874.901 |
|                                  | 025                      | 251 3 05 20 025 | 743655.629                   | 1056874.981 |
|                                  | 026                      | 251 3 05 20 026 | 743660.628                   | 1056875.061 |
|                                  | 027                      | 251 3 05 20 027 | 743665.627                   | 1056875.141 |
|                                  | 028                      | 251 3 05 20 028 | 743670.626                   | 1056875.221 |
|                                  | 029                      | 251 3 05 20 029 | 743675.625                   | 1056875.301 |
|                                  | 030                      | 251 3 05 20 030 | 743680.624                   | 1056875.381 |

| Vytyčení tvaru opěrné zdi        |                          |                 |                              |             |
|----------------------------------|--------------------------|-----------------|------------------------------|-------------|
| Opěrná zeď č. 5 - vytyčení tvaru |                          |                 |                              |             |
| OPĚRNÁ ZED' 05                   |                          |                 |                              |             |
| RADA BODŮ                        | Označ. Bodu dle půdorysu | Číslo bodu      | SOUŘADNICE                   | Poznámky    |
|                                  |                          |                 | Y [m]<br>X [m]<br>Z [m.n.m.] |             |
| 11                               | 001                      | 251 3 05 11 001 | 743538.450                   | 1056869.752 |
|                                  | 002                      | 251 3 05 11 002 | 743540.700                   | 1056869.788 |
|                                  | 003                      | 251 3 05 11 003 | 743545.700                   | 1056869.869 |
|                                  | 004                      | 251 3 05 11 004 | 743550.699                   | 1056869.949 |
|                                  | 005                      | 251 3 05 11 005 | 743555.698                   | 1056870.029 |
|                                  | 006                      | 251 3 05 11 006 | 743560.698                   | 1056870.109 |
|                                  | 007                      | 251 3 05 11 007 | 743565.697                   | 1056870.189 |
|                                  | 008                      | 251 3 05 11 008 | 743570.696                   | 1056870.270 |
|                                  | 009                      | 251 3 05 11 009 | 743575.696                   | 1056870.350 |
|                                  | 010                      | 251 3 05 11 010 | 743580.695                   | 1056870.430 |
|                                  | 011                      | 251 3 05 11 011 | 743585.694                   | 1056870.510 |
|                                  | 012                      | 251 3 05 11 012 | 743590.694                   | 1056870.590 |
|                                  | 013                      | 251 3 05 11 013 | 743595.693                   | 1056870.670 |
|                                  | 014                      | 251 3 05 11 014 | 743600.693                   | 1056870.751 |
|                                  | 015                      | 251 3 05 11 015 | 743605.692                   | 1056870.831 |
| 21                               | 016                      | 251 3 05 21 016 | 743610.691                   | 1056870.911 |
|                                  | 017                      | 251 3 05 21 017 | 743615.690                   | 1056870.991 |
|                                  | 018                      | 251 3 05 21 018 | 743620.689                   | 1056871.071 |
|                                  | 019                      | 251 3 05 21 019 | 743625.688                   | 1056871.151 |
|                                  | 020                      | 251 3 05 21 020 | 743630.687                   | 1056871.231 |
|                                  | 021                      | 251 3 05 21 021 | 743635.686                   | 1056871.311 |
|                                  | 022                      | 251 3 05 21 022 | 743640.685                   | 1056871.391 |
|                                  | 023                      | 251 3 05 21 023 | 743645.684                   | 1056871.471 |
|                                  | 024                      | 251 3 05 21 024 | 743650.683                   | 1056871.551 |
|                                  | 025                      | 251 3 05 21 025 | 743655.682                   | 1056871.631 |
|                                  | 026                      | 251 3 05 21 026 | 743660.681                   | 1056871.711 |
|                                  | 027                      | 251 3 05 21 027 | 743665.680                   | 1056871.791 |
|                                  | 028                      | 251 3 05 21 028 | 743670.679                   | 1056871.871 |
|                                  | 029                      | 251 3 05 21 029 | 743675.678                   | 1056871.951 |
|                                  | 030                      | 251 3 05 21 030 | 743680.677                   | 1056872.031 |

| Vytyčení tvaru opěrné zdi        |                          |                 |                              |             |
|----------------------------------|--------------------------|-----------------|------------------------------|-------------|
| Opěrná zeď č. 5 - vytyčení tvaru |                          |                 |                              |             |
| OPĚRNÁ ZED' 05                   |                          |                 |                              |             |
| RADA BODŮ                        | Označ. Bodu dle půdorysu | Číslo bodu      | SOUŘADNICE                   | Poznámky    |
|                                  |                          |                 | Y [m]<br>X [m]<br>Z [m.n.m.] |             |
| 20                               | 001                      | 251 3 05 20 001 | 743538.397                   | 1056873.102 |
|                                  | 002                      | 251 3 05 20 002 | 743540.647                   | 1056873.138 |
|                                  | 003                      | 251 3 05 20 003 | 743545.646                   | 1056873.218 |
|                                  | 004                      | 251 3 05 20 004 | 743550.645                   | 1056873.298 |
|                                  | 005                      | 251 3 05 20 005 | 743555.645                   | 1056873.379 |
|                                  | 006                      | 251 3 05 20 006 | 743560.644                   | 1056873.459 |
|                                  | 007                      | 251 3 05 20 007 | 743565.643                   | 1056873.539 |
|                                  | 008                      | 251 3 05 20 008 | 743570.643                   | 1056873.619 |
|                                  | 009                      | 251 3 05 20 009 | 743575.642                   | 1056873.699 |
|                                  | 010                      | 251 3 05 20 010 | 743580.641                   | 1056873.779 |
|                                  | 011                      | 251 3 05 20 011 | 743585.641                   | 1056873.860 |
|                                  | 012                      | 251 3 05 20 012 | 743590.640                   | 1056873.940 |
|                                  | 013                      | 251 3 05 20 013 | 743595.639                   | 1056874.020 |
|                                  | 014                      | 251 3 05 20 014 | 743600.639                   | 1056874.100 |
|                                  | 015                      | 251 3 05 20 015 | 743605.638                   | 1056874.180 |
| 30                               | 016                      | 251 3 05 30 016 | 743610.638                   | 1056874.261 |
|                                  | 017                      | 251 3 05 30 017 | 743615.637                   | 1056874.341 |
|                                  | 018                      | 251 3 05 30 018 | 743620.636                   | 1056874.421 |
|                                  | 019                      | 251 3 05 30 019 | 743625.635                   | 1056874.501 |
|                                  | 020                      | 251 3 05 30 020 | 743630.634                   | 1056874.581 |
|                                  | 021                      | 251 3 05 30 021 | 743635.633                   | 1056874.661 |
|                                  | 022                      | 251 3 05 30 022 | 743640.632                   | 1056874.741 |
|                                  | 023                      | 251 3 05 30 023 | 743645.631                   | 1056874.821 |
|                                  | 024                      | 251 3 05 30 024 | 743650.630                   | 1056874.901 |
|                                  | 025                      | 251 3 05 30 025 | 743655.629                   | 1056874.981 |
|                                  | 026                      | 251 3 05 30 026 | 743660.628                   | 1056875.061 |
|                                  | 027                      | 251 3 05 30 027 | 743665.627                   | 1056875.141 |
|                                  | 028                      | 251 3 05 30 028 | 743670.626                   | 1056875.221 |
|                                  | 029                      | 251 3 05 30 029 | 743675.625                   | 1056875.301 |
|                                  | 030                      | 251 3 05 30 030 | 743680.624                   | 1056875.381 |

| Vytyčení tvaru opěrné zdi        |                          |                 |                                       | SO 251.2_05 |         |
|----------------------------------|--------------------------|-----------------|---------------------------------------|-------------|---------|
| Opěrná zeď č. 5 - vytyčení tvaru |                          |                 |                                       |             |         |
| OPĚRNÁ ZED' 05                   |                          |                 |                                       |             |         |
| ŘÁDA BODŮ                        | Označ. Bodu dle půdorysu | Číslo bodu      | SOUŘADNICE                            | Poznámky    |         |
|                                  |                          |                 | Y<br>[m]<br>X<br>[m]<br>Z<br>[m.n.m.] |             |         |
| 21                               | 001                      | 251 3 05 21 001 | 743538.450                            | 1056869.752 | 290.440 |
|                                  | 002                      | 251 3 05 21 002 | 743540.700                            | 1056869.788 | 290.440 |
|                                  | 003                      | 251 3 05 21 003 | 743545.700                            | 1056869.869 | 290.440 |
|                                  | 004                      | 251 3 05 21 004 | 743550.699                            | 1056869.949 | 290.040 |
|                                  | 005                      | 251 3 05 21 005 | 743555.698                            | 1056870.029 | 290.040 |
|                                  | 006                      | 251 3 05 21 006 | 743560.698                            | 1056870.109 | 289.840 |
|                                  | 007                      | 251 3 05 21 007 | 743565.697                            | 1056870.189 | 289.840 |
|                                  | 008                      | 251 3 05 21 008 | 743570.696                            | 1056870.270 | 289.640 |
|                                  | 009                      | 251 3 05 21 009 | 743575.696                            | 1056870.350 | 289.640 |
|                                  | 010                      | 251 3 05 21 010 | 743580.695                            | 1056870.430 | 289.440 |
|                                  | 011                      | 251 3 05 21 011 | 743585.694                            | 1056870.510 | 289.440 |
|                                  | 012                      | 251 3 05 21 012 | 743590.694                            | 1056870.590 | 289.240 |
|                                  | 013                      | 251 3 05 21 013 | 743595.693                            | 1056870.670 | 289.240 |
|                                  | 014                      | 251 3 05 21 014 | 743600.693                            | 1056870.751 | 289.140 |
|                                  | 015                      | 251 3 05 21 015 | 743605.692                            | 1056870.831 | 289.140 |
| 31                               | 016                      | 251 3 05 31 016 | 743610.691                            | 1056870.911 | 289.040 |
|                                  | 017                      | 251 3 05 31 017 | 743615.691                            | 1056870.955 | 289.040 |
|                                  | 301                      | 251 3 05 31 301 | 743584.448                            | 1056869.913 | 290.440 |
|                                  | 302                      | 251 3 05 31 302 | 743586.699                            | 1056869.913 | 290.040 |
|                                  | 303                      | 251 3 05 31 303 | 743588.448                            | 1056870.073 | 290.040 |
|                                  | 304                      | 251 3 05 31 304 | 743588.448                            | 1056870.073 | 289.840 |
| 31                               | 305                      | 251 3 05 31 305 | 743588.447                            | 1056870.233 | 289.840 |
|                                  | 306                      | 251 3 05 31 306 | 743588.447                            | 1056870.233 | 289.640 |
|                                  | 307                      | 251 3 05 31 307 | 743578.446                            | 1056870.394 | 289.640 |
|                                  | 308                      | 251 3 05 31 308 | 743578.445                            | 1056870.394 | 289.440 |
|                                  | 309                      | 251 3 05 31 309 | 743588.444                            | 1056870.554 | 289.440 |
|                                  | 310                      | 251 3 05 31 310 | 743588.444                            | 1056870.554 | 289.240 |
| 31                               | 311                      | 251 3 05 31 311 | 743598.443                            | 1056870.715 | 289.240 |
|                                  | 312                      | 251 3 05 31 312 | 743598.443                            | 1056870.715 | 289.140 |
|                                  | 313                      | 251 3 05 31 313 | 743608.442                            | 1056870.875 | 289.140 |
|                                  | 314                      | 251 3 05 31 314 | 743608.442                            | 1056870.875 | 289.040 |