



DILATAČNÍ CELEK "D1" - "D19"

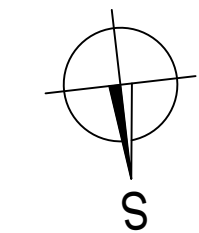

DOLNÍ BŘEŽANY

DILATAČNÍ CELEK "D20" - "D34"

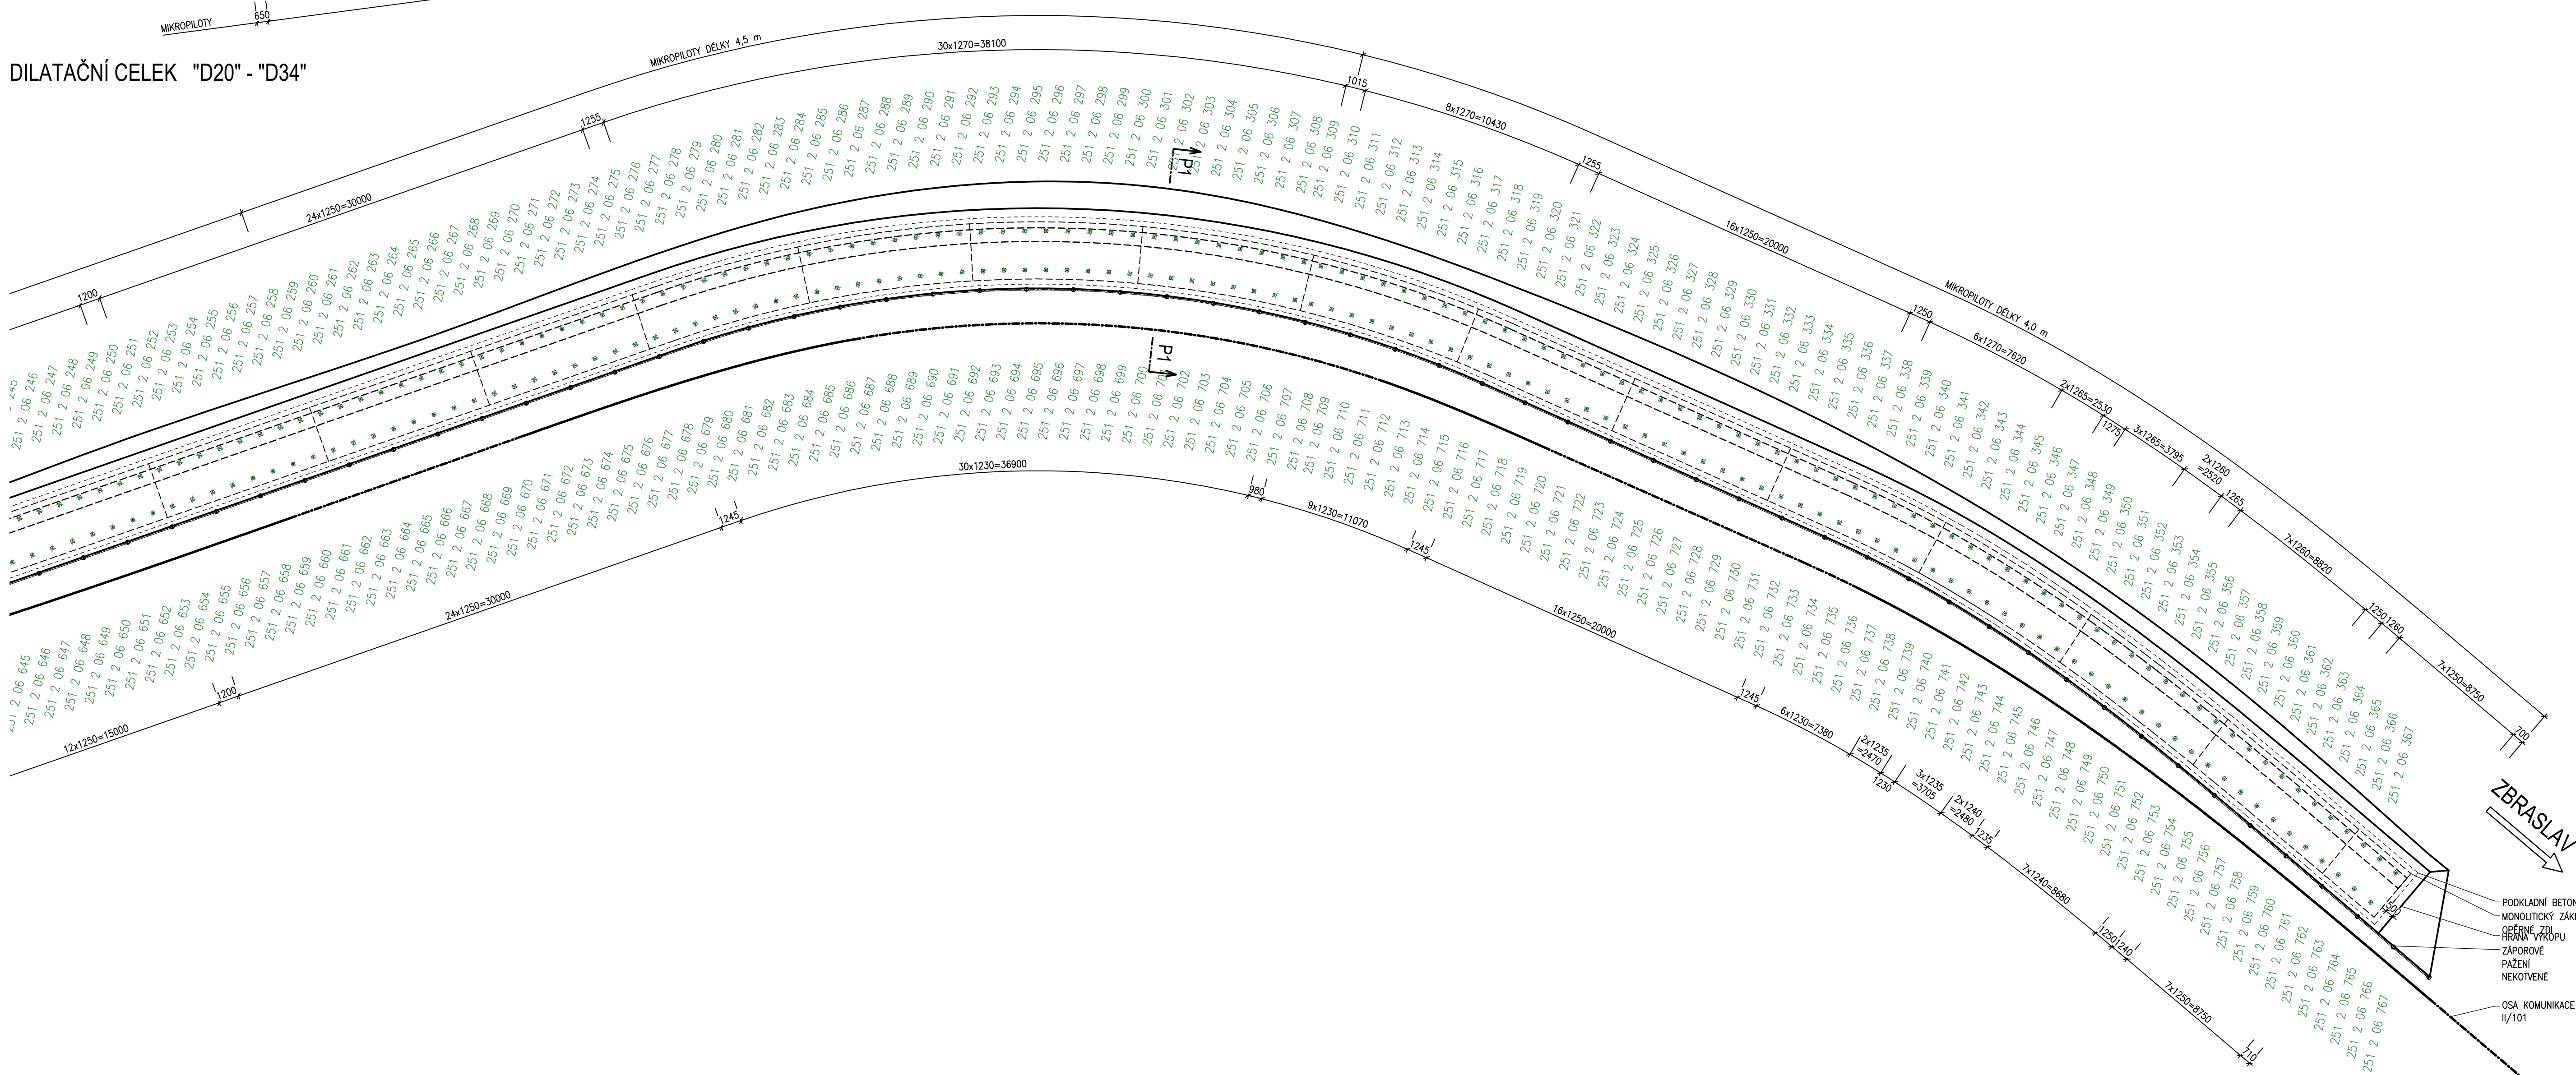

PŘEDKONCEPT

OZNAČ.	TEXT ZMĚNY - ODŮVODNĚNÍ	DATUM	PODPIS
TABULKA ZMĚN			

Název stavby	II/101 Dolní Břežany - Zbraslav	ČÍSLO OBJEKTU	SO 251.2
--------------	---------------------------------	---------------	----------

Objednatel stavby

KSÚS
KRAJSKÁ SPRÁVA A ÚDRŽBA SILNIC

Krajská správa a údržba silnic
Středočeského kraje, příspěvková organizace
Zborovská 81/11, 150 21 Praha 5-Smíchov

Autorský dozor

GeoTec GS®

GeoTec-GS, a.s.
Chmelová 2920/6, 106 00 Praha 10

Technický dozor investora TES CONSULTING	TES + SGS + SGG vedoucí sdružení: TES Consulting, s.r.o. V Olšinách 2300/75, 100 00 Praha 10-Strašnice	RAŽITKO DATUM PODPIS
--	---	--

Zhotovitel stavby		RAZÍTKO
	M-SILNICE a.s. Husova 1697, 530 03 Pardubice www.msilnice.cz	DATUM PODPIS

Koordinátor RDS  M - PROJEKCE	M - PROJEKCE s. r. o. Reslova 956/13, 500 02 Hradec Králové www.m-projekce.cz	RAZÍTKO
Datum:		DATUM PODPIS

Souřadnicový systém: S-JTSK

Projekční kancelář PRIS spol. s r.o.
Osova 717/20, 625 00 Brno-Starý Lískovec
www.pris.cz

Výškový systém: Bpv

Vypracoval: Ilena Šynková	Hlavní inženýr projektu: Ing. Jiří Ehrenberger	Razítko:  PROJEKČNÍ KANCELÁŘ PRIS spol. s r. o. OSOVA 20, 625 00 BRNO
Odpovědný projektant: Ing. Martin Reuňka	Kontrolýr: Ing. Jiří ŠRUBAR	
Číslo zakázky: 25-122-02	Datum: 06/2026	

Objekt/zást: SO 251.2 - OPĚRNÉ ZDI ZED č. 06	Měřítko:	1:200	Souprava:
	Stupeň:	RDS	
Příloha: MIKROPILOTY - PŮDORYS, VYTÝČENÍ - ČÁST 1	Číslo přílohy: 103_MIK1		