



MIKROPILOTY - ŘEZY, VÝKAZY - ČÁST 2.

PŘÍČNÝ ŘEZ P1-P1 km 1,340 000 1:25

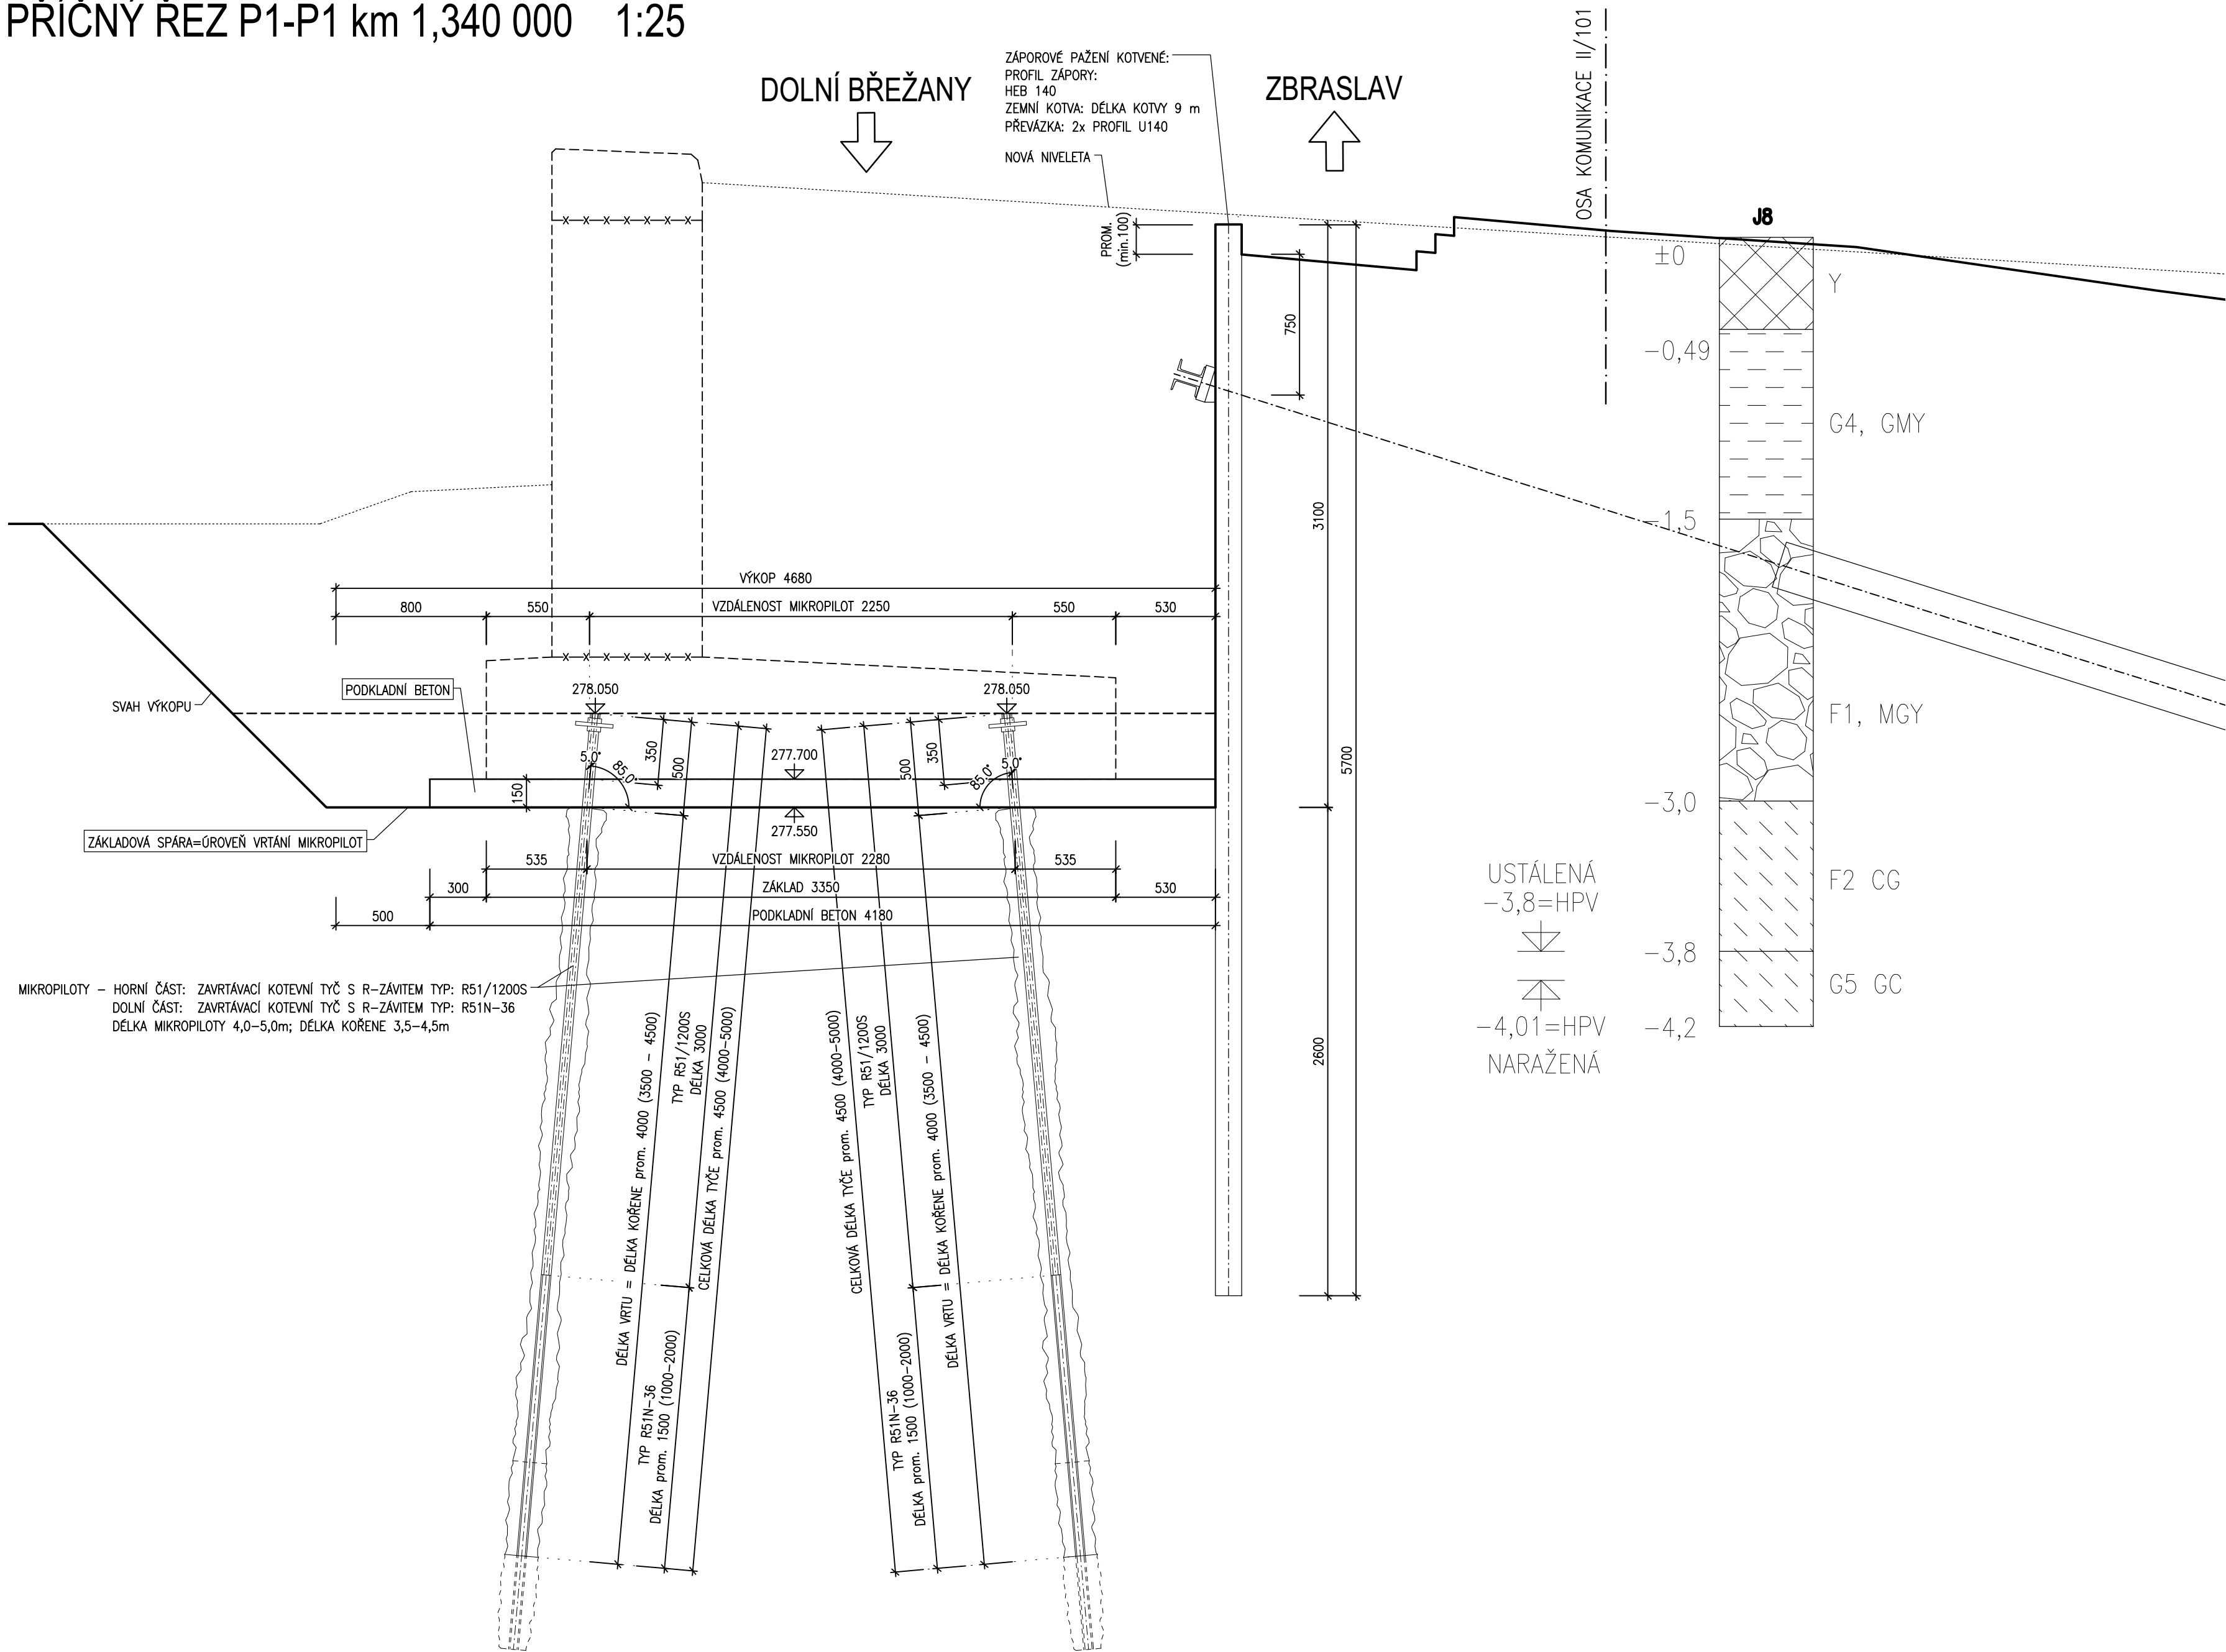


DETAIL UKONČENÍ MIKROPILOTY 1:5


POHLED

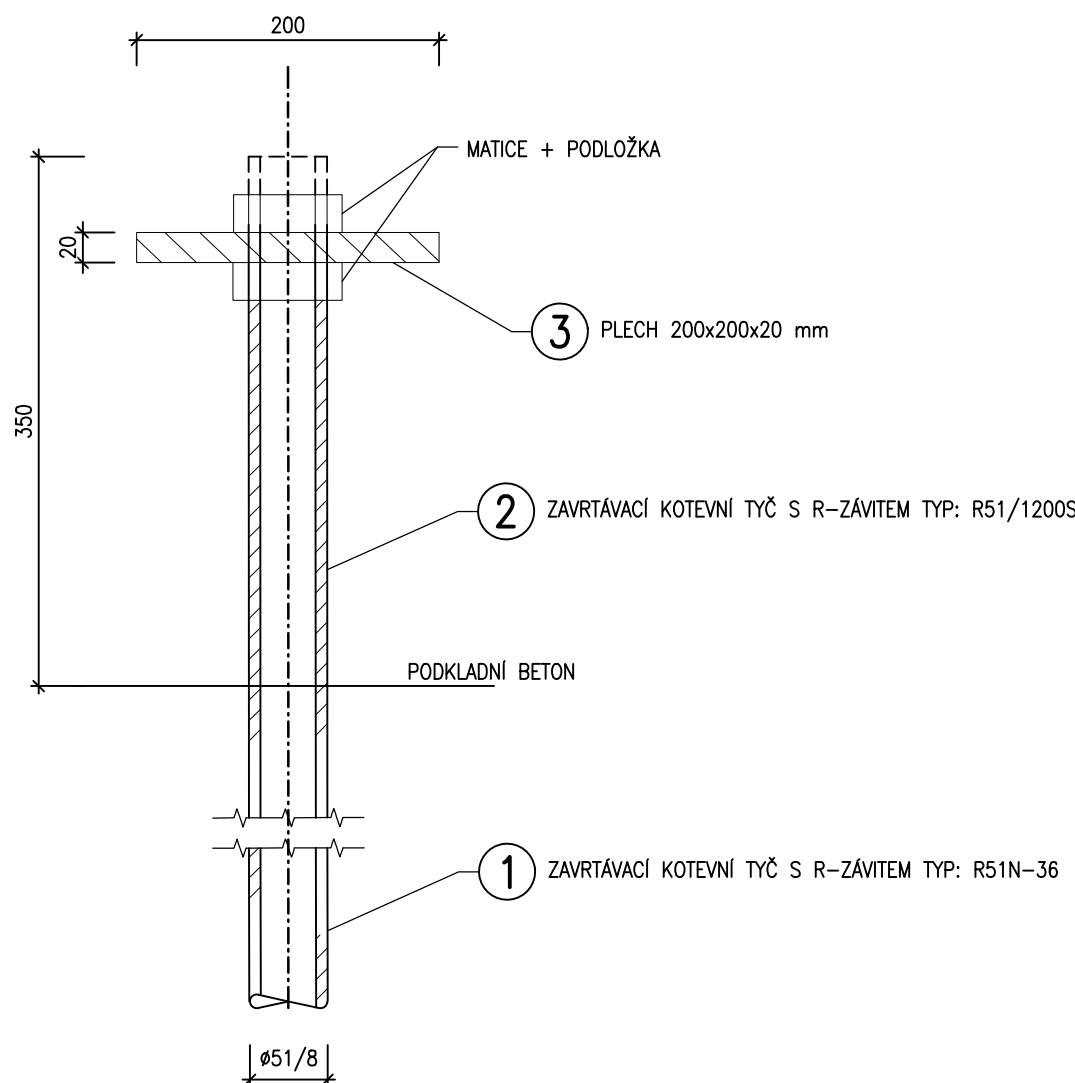

PŮDORYS

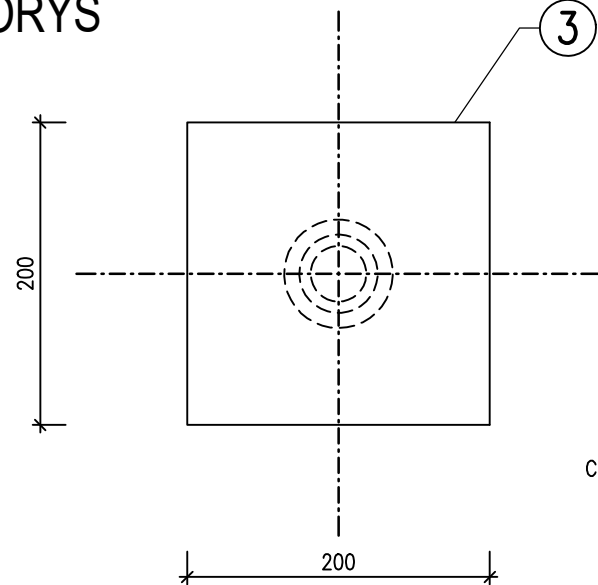

ŘEZ V KOŘENOVÉ ČÁSTI

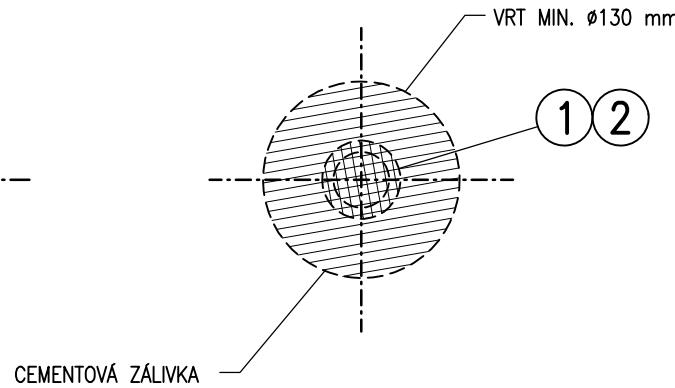

VÝKAZ MATERIÁLU

MIKROPILOTY OPĚRNÁ ZEĎ 06

VÝKAZ MATERIÁLU

OZN.	POPIS	DÉLKA [m]	HMOTNOST [kg/m]	POČET [ks]	DÉLKA CELKEM [m]	HMOTNOST [kg]
1	TYČ Ø51mm, TYP: R51N-36	2,00	7,7	1	2,000	15,40
2	TYČ Ø51mm, TYP: R51/1200S	3,00	14,7	1	3,000	44,10
3	PLECH 200/200, TL 20mm	-	6,28	1	-	6,28

HMOTNOST CELKEM ... PRO 1 TYČ DL. 5.0 m	65,78 kg
---	----------

HMOTNOST CELKEM ... PRO VŠECH 320 TYČÍ	21049,60 kg
--	-------------

POZNÁMKA:

- JE VYKÁZÁNA CELKOVÁ DÉLKA TYČE 5,0 m VČETNĚ PŘESAHU 0,35 m DO ZÁKLADU

MIKROPILOTY OPĚRNÁ ZEĎ 06

VÝKAZ MATERIÁLU

OZN.	POPIS	DÉLKA [m]	HMOTNOST [kg/m]	POČET [ks]	DÉLKA CELKEM [m]	HMOTNOST [kg]
1	TYČ Ø51mm, TYP: R51N-36	1,50	7,7	1	1,500	11,55
2	TYČ Ø51mm, TYP: R51/1200S	3,00	14,7	1	3,000	44,10
3	PLECH 200/200, TL 20mm	-	6,28	1	-	6,28

HMOTNOST CELKEM ... PRO 1 TYČ DL. 4.5 m	61,93 kg
---	----------

HMOTNOST CELKEM ... PRO VŠECH 96 TYČÍ	5945,28 kg
---------------------------------------	------------

POZNÁMKA:

- JE VYKÁZÁNA CELKOVÁ DÉLKA TYČE 4,5 m VČETNĚ PŘESAHU 0,35 m DO ZÁKLADU

MIKROPILOTY OPĚRNÁ ZEĎ 06

VÝKAZ MATERIÁLU

OZN.	POPIS	DÉLKA [m]	HMOTNOST [kg/m]	POČET [ks]	DÉLKA CELKEM [m]	HMOTNOST [kg]
1	TYČ Ø51mm, TYP: R51N-36	1,00	7,7	1	1,000	7,70
2	TYČ Ø51mm, TYP: R51/1200S	3,00	14,7	1	3,000	44,10
3	PLECH 200/200, TL 20mm	-	6,28	1	-	6,28

HMOTNOST CELKEM ... PRO 1 TYČ DL. 4.0 m	58,08 kg
---	----------

HMOTNOST CELKEM ... PRO VŠECH 118 TYČÍ	6853,44 kg
--	------------

POZNÁMKA:

- JE VYKÁZÁNA CELKOVÁ DÉLKA TYČE 4,0 m VČETNĚ PŘESAHU 0,35 m DO ZÁKLADU


MATERIÁL

CEMENTOVÁ SUSPENZE INJEKTAŽNÍ CEM 32,5R, C25/30

POZNÁMKY

- ZHOTOVITEL JE POVINEN PRO VŠECHNY ZEMĚMĚŘICKÉ PRÁCE POSTUPOVAT DLE TKP KAP. 1, ODS. 1.6.3.
- PRO MIKROPILOTY BUDOU POUŽITY INJEKČNÍ ZAVRTÁVACÍ KOTEVNÍ TYČE SDA, TYP R51N-36 A R51/1200S
- MIKROPILOTY JSOU VYTÝČENY V ÚROVNI ZÁKLADOVÉ SPÁRY, TZN. V DOLNÍ ÚROVNI PODKLADNÍHO BETONU.
- PRO PÍPADNÉ SPOJOVÁNÍ BUDOU POUŽITI ORIGINALNÍ SPOJNÍKY
- SAMOZAVRTÁVACÍ TYČ BUDE UKONČENÁ DESKOU 200x200x20 mm A Z OBOU STRAN STAŽENA MATICEMI
- VŠECHNY MIKROPILOTY JSOU ŠIKMÉ 5°
- PROVÁDĚNÍ MIKROPILOT MUSÍ BÝT V SOULADU S ČSN EN 14199.
- CEMENTOVÁ SUSPENZE MUSÍ MÍT FINÁLNÍ PEVNOST MIN. C25/30
- PRO ČERPÁNÍ VODY ZE DNA ZÁKLADOVÉ SPÁRY BUDOU ZBUDOVÁNY JÍMKY.
- DÉLKA SAMOZAVRTNÉ TYČE BUDE MINIMÁLNĚ 5m, DÉLKA MIKROPILOTY S OHLEDEM NA POUŽITÍ ZTRACENÉ VRTACÍ KORUNKY BUDE DLE ZVYKLOSTÍ DODAVATELE.

ČÍSLOVÁNÍ VYTÝČOVANÝCH BODŮ

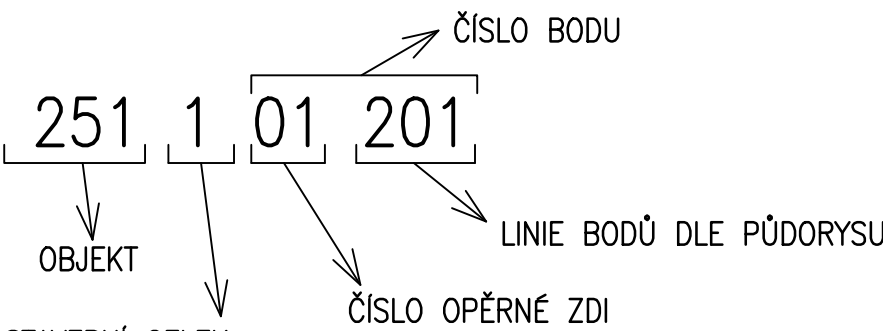

STAVEBNÍ CELEK

- 0 ... HLAVNÍ BODY
- 1 ... VÝKOPY, PAŽENÍ
- 2 ... MIKROPILOTY
- 3 ... SPODNÍ STAVBA/OPĚRNÁ ZED
- 4 ... NOSNÁ KONSTRUKCE
- 5 ... PŘÍSLUŠENSTVÍ

PŘEDKONCEPT

OZNAČ.	TEXT ZMĚNY - ODŮVODNĚNÍ	DATUM	PODPIS
TABULKA ZMĚN			

Název stavby	II/101 Dolní Břežany - Zbraslav	ČÍSLO OBJEKTU	SO 251.2
--------------	---------------------------------	---------------	----------

Objednatel stavby	Krajská správa a údržba silnic Středočeského kraje, příspěvková organizace Zbrovovská 81/11, 150 21 Praha 5-Smíchov		
-------------------	---	--	--

Autorský dozor	GeoTec-GS, a.s. Chmelová 2920/6, 106 00 Praha 10		
----------------	--	--	--

Technický dozor investora	TES + SGS + SGG vedoucí sdružení: TES Consulting, s.r.o. V Olšánách 2300/75, 100 00 Praha 10-Strašnice	RAZÍTKO	DATUM	PODPIS
---------------------------	---	---------	-------	--------

Zhotovitel stavby	M-SILNICE a.s. Husova 1697, 530 03 Pardubice www.m-silnice.cz	RAZÍTKO	DATUM	PODPIS
-------------------	---	---------	-------	--------

Koordinátor RDS	M - PROJEKCE s. r.o. Reslova 956/13, 500 02 Hradec Králové www.m-projekce.cz	RAZÍTKO	DATUM	PODPIS
-----------------	--	---------	-------	--------

Souřadnicový systém: S-JTSK Výškový systém: Bpv

Zpracovatel stavebního objektu/části:	Projekční kancelář PRIS spol. s r.o. Osová 717/20, 625 00 Brno-Starý Lískovec www.pris.cz		
---------------------------------------	---	--	--

Vypracoval: Ilona Synková	Hlavní inženýr projektu: Ing. Jiří Ehrenberger	Razítko: PROJEKČNÍ KANCELÁŘ PRIS spol. s r. o. OSOVÁ 20, 625 00 BRNO
Odpovědný projektant: Ing. Martin Reuhla	Kontroloval: Ing. Jiří ŠRUBAŘ	
Číslo zakázky: 25-122-02	Datum: 06/2026	

Objekt/část:	SO 251.2 - OPĚRNÉ ZDI ZEĎ č. 06	Měřítko:	1:25; 1:5	Souprava:
Příloha:	MIKROPILOTY - ŘEZY, VÝKAZY - ČÁST 2.	Stupeň:	RDS	
		Číslo přílohy:	104_MIK2	