



VYTÝČENÍ OPĚRNÉ ZDI - PŮDORYS - ČÁST 1

PŮDORYS 1:100


DILATAČNÍ CELEK "D1" - "D11"

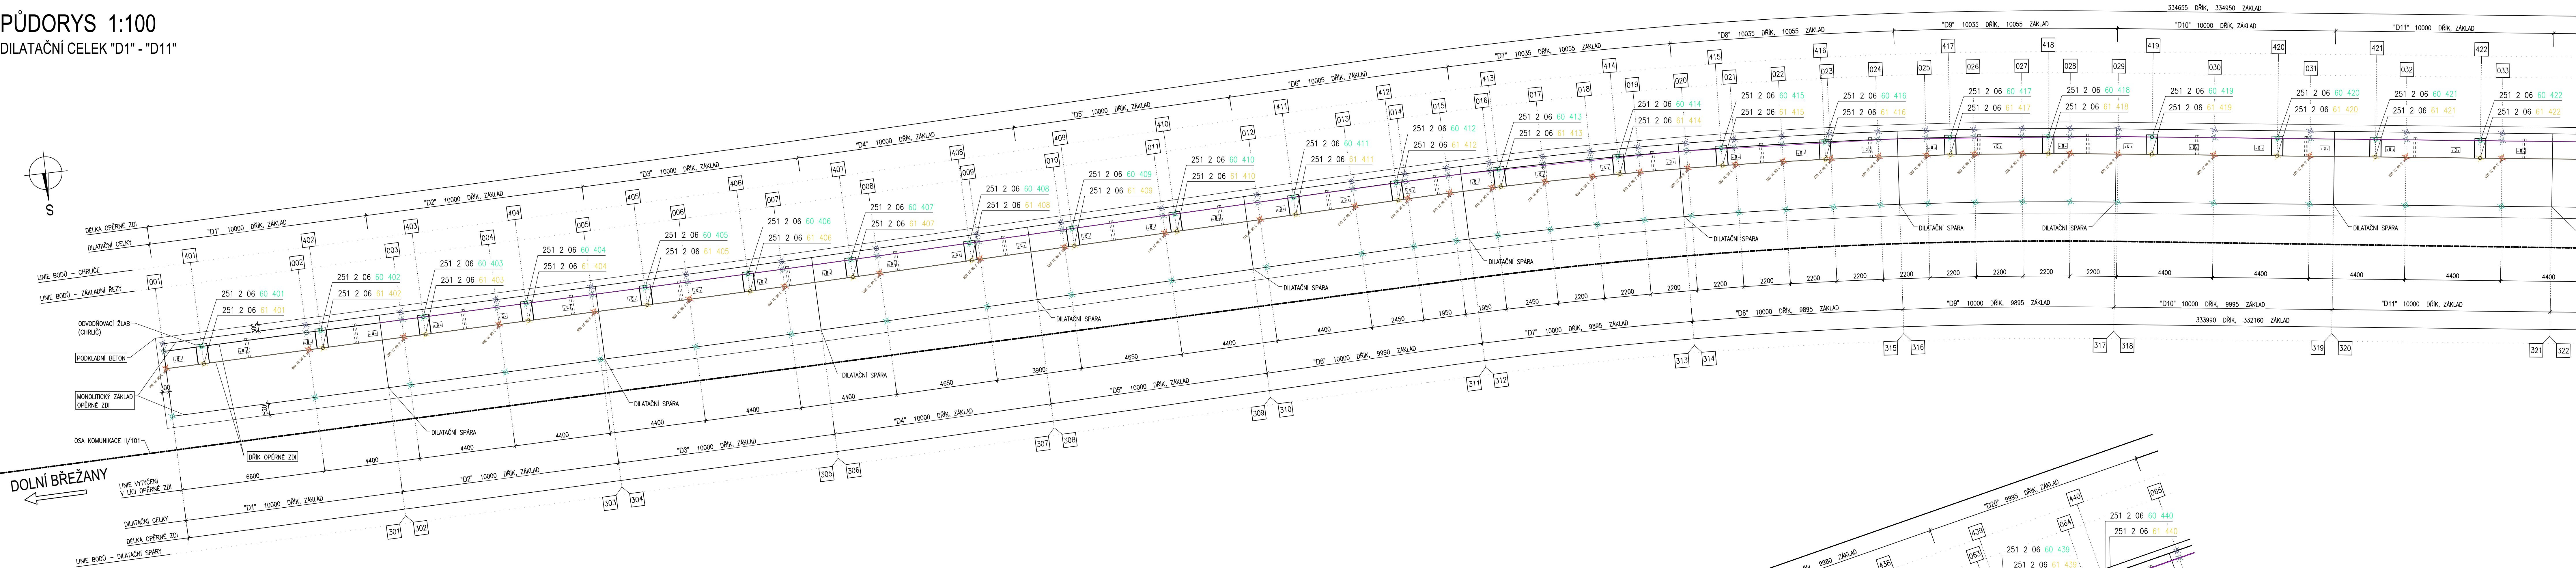

DILATAČNÍ CELEK "D11" - "D20"

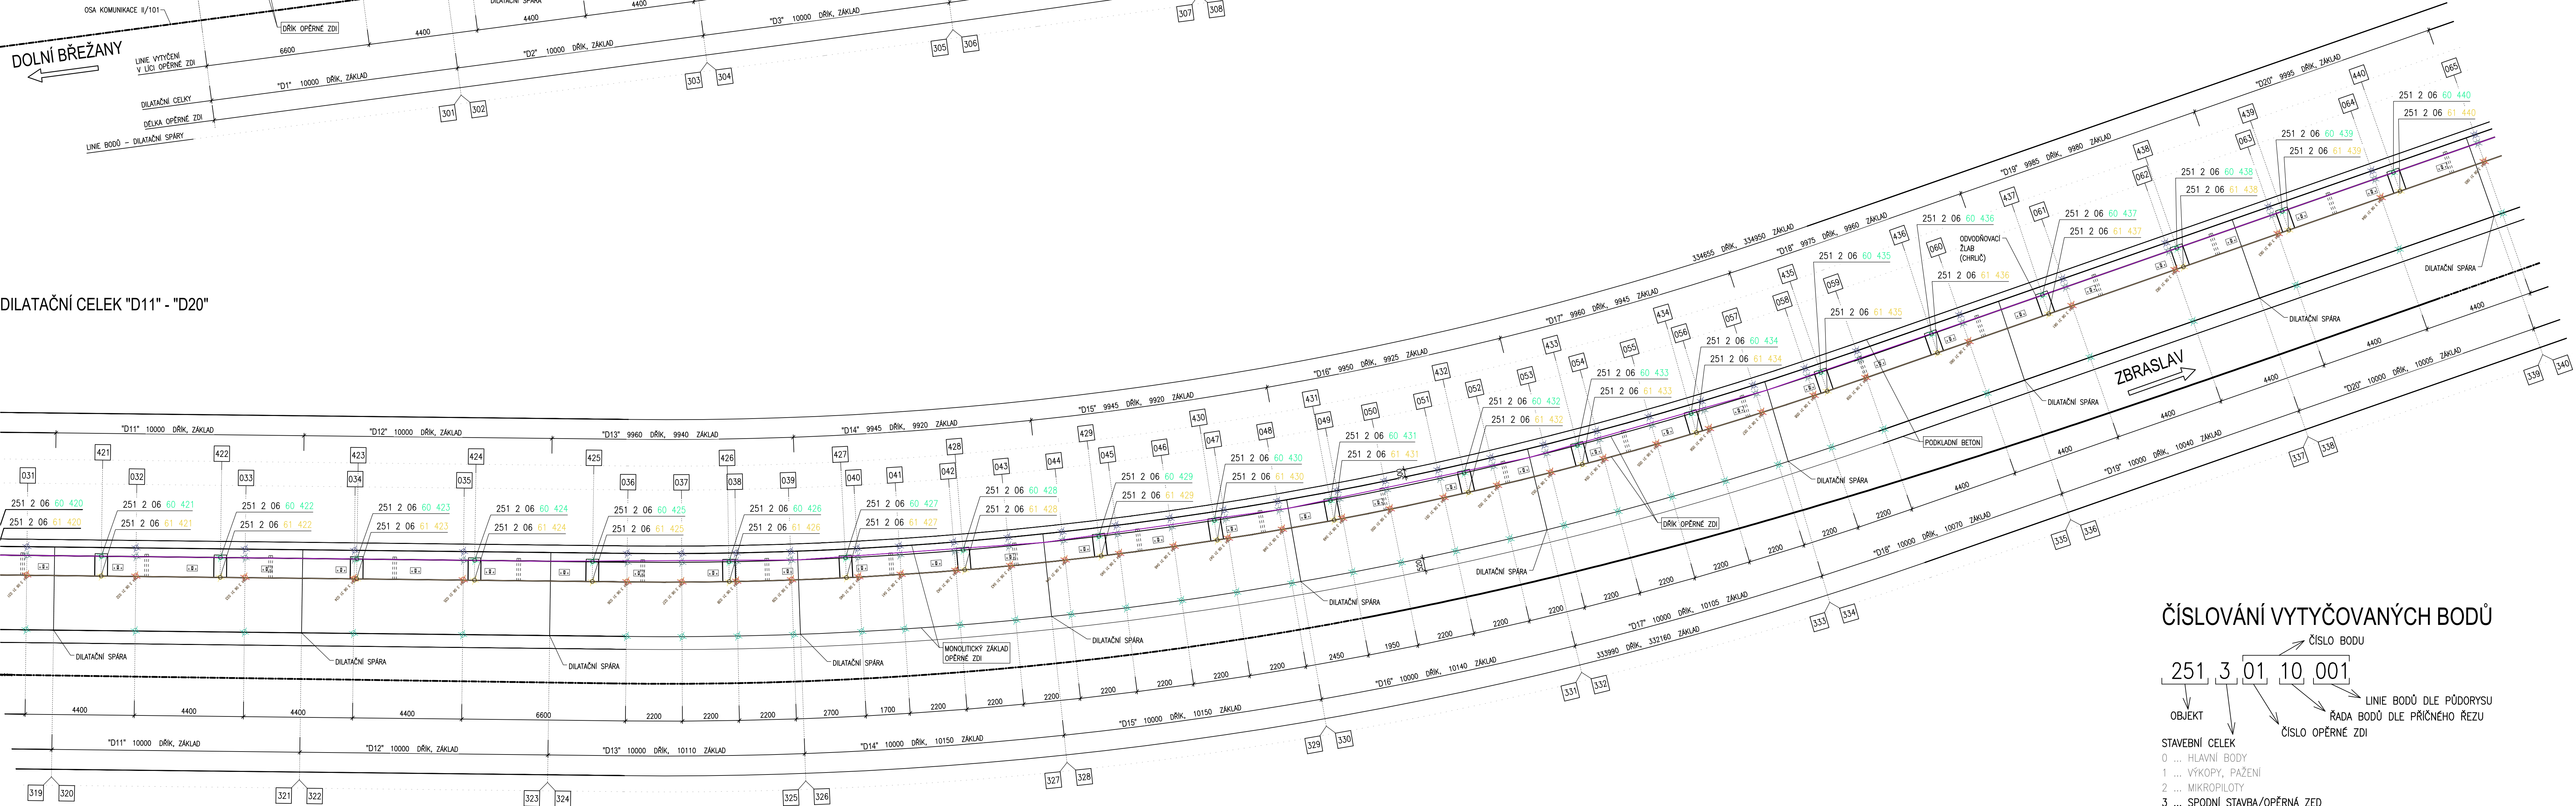

ČÍSLOVÁNÍ VYTÝČOVANÝCH BODŮ

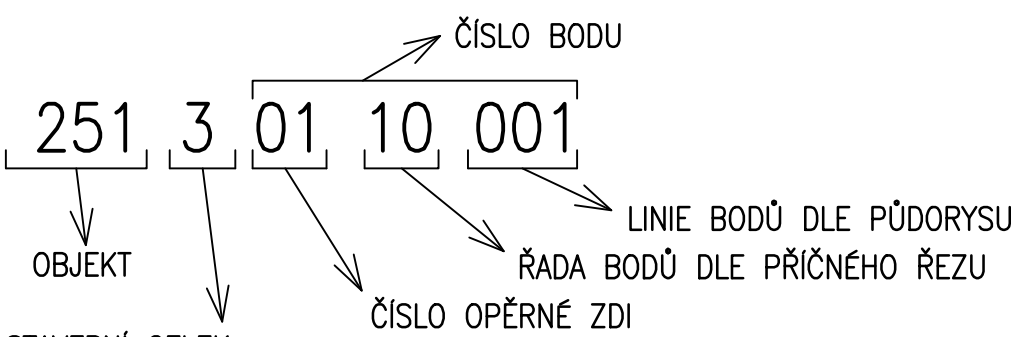

- STAVEBNÍ CELEK
- 0 ... HLAVNÍ BODY
 - 1 ... VÝKOPY, PAŽENÍ
 - 2 ... MİKROPILOTY
 - 3 ... SPODNÍ STAVBA/OPĚRNÁ ZED
 - 4 ... NOSNÁ KONSTRUKCE
 - 5 ... PŘÍSLUŠENSTVÍ

PŘEDKONCEPT			
OZNAC.		TEXT ZMĚNY - ODŮVODNĚNÍ	TABULKA ZMĚN
OZNAC.		DATUM	PODPIS
Název stavby		ČÍSLO OBJEKTU	
II/101 Dolní Břežany - Zbraslav		SO 251.2	
Objednatel stavby			
		Krajská správa a údržba silnic Středočeského kraje, příspěvková organizace Zborovská 611/11, 150 21 Praha 5-Smíchov	
Autorský dozor			
		GeoTec-GS, a.s. Chmelová 2920/6, 106 00 Praha 10	
Technický dozor investora		RAZÍTKO	
		TES + SGS + SGG vedoucí sdružení: TES Consulting, s.r.o. V Olšánské 2300/75, 100 00 Praha 10-Strašnice	
		DATUM	PODPIS
Zhotovitel stavby		RAZÍTKO	
		M-SILNICE a.s. Husova 1697, 530 03 Pardubice www.msilnice.cz	
		DATUM	PODPIS
Koordínátor RDS		RAZÍTKO	
		M - PROJEKCE s. r.o. Restlova 956/13, 500 02 Hradec Králové www.m-projeke.cz	
		DATUM	PODPIS
Souřadnicový systém: S-JTSK		Výškový systém: Bpv	
Zpracovatel stavebního objektu/části:			
Projektovní kancelář PRIS spol. s r.o. Osova 717/20, 625 00 Brno-Starý Lískovec www.pris.cz			
Vyracoval: Ing. Ondřej Vytásek		Hlavní inženýr projektu: Ing. Jiří Ehrenberger	
Odpovědný projektant: Ing. Martin Rehnika		Kontroloval: Ing. Jiří ŠRUBAŘ	
Číslo zakázky: 25-122-02		Datum: 06/2026	
Objekt/část:		Měřítko:	
SO 251.2 - OPĚRNÉ ZDI		1:100	
ZED č. 06		Stupeň:	
		RDS	
Příloha:		Číslo přílohy:	
VYTÝČENÍ OPĚRNÉ ZDI - PŮDORYS - ČÁST 1		113_VYT1	