

VYTÝČENÍ OPĚRNÉ ZDI - PŮDORYS, ŘEZ - ČÁST 2

PŮDORYS 1:100

DILATAČNÍ CELEK "D20" - "D29"



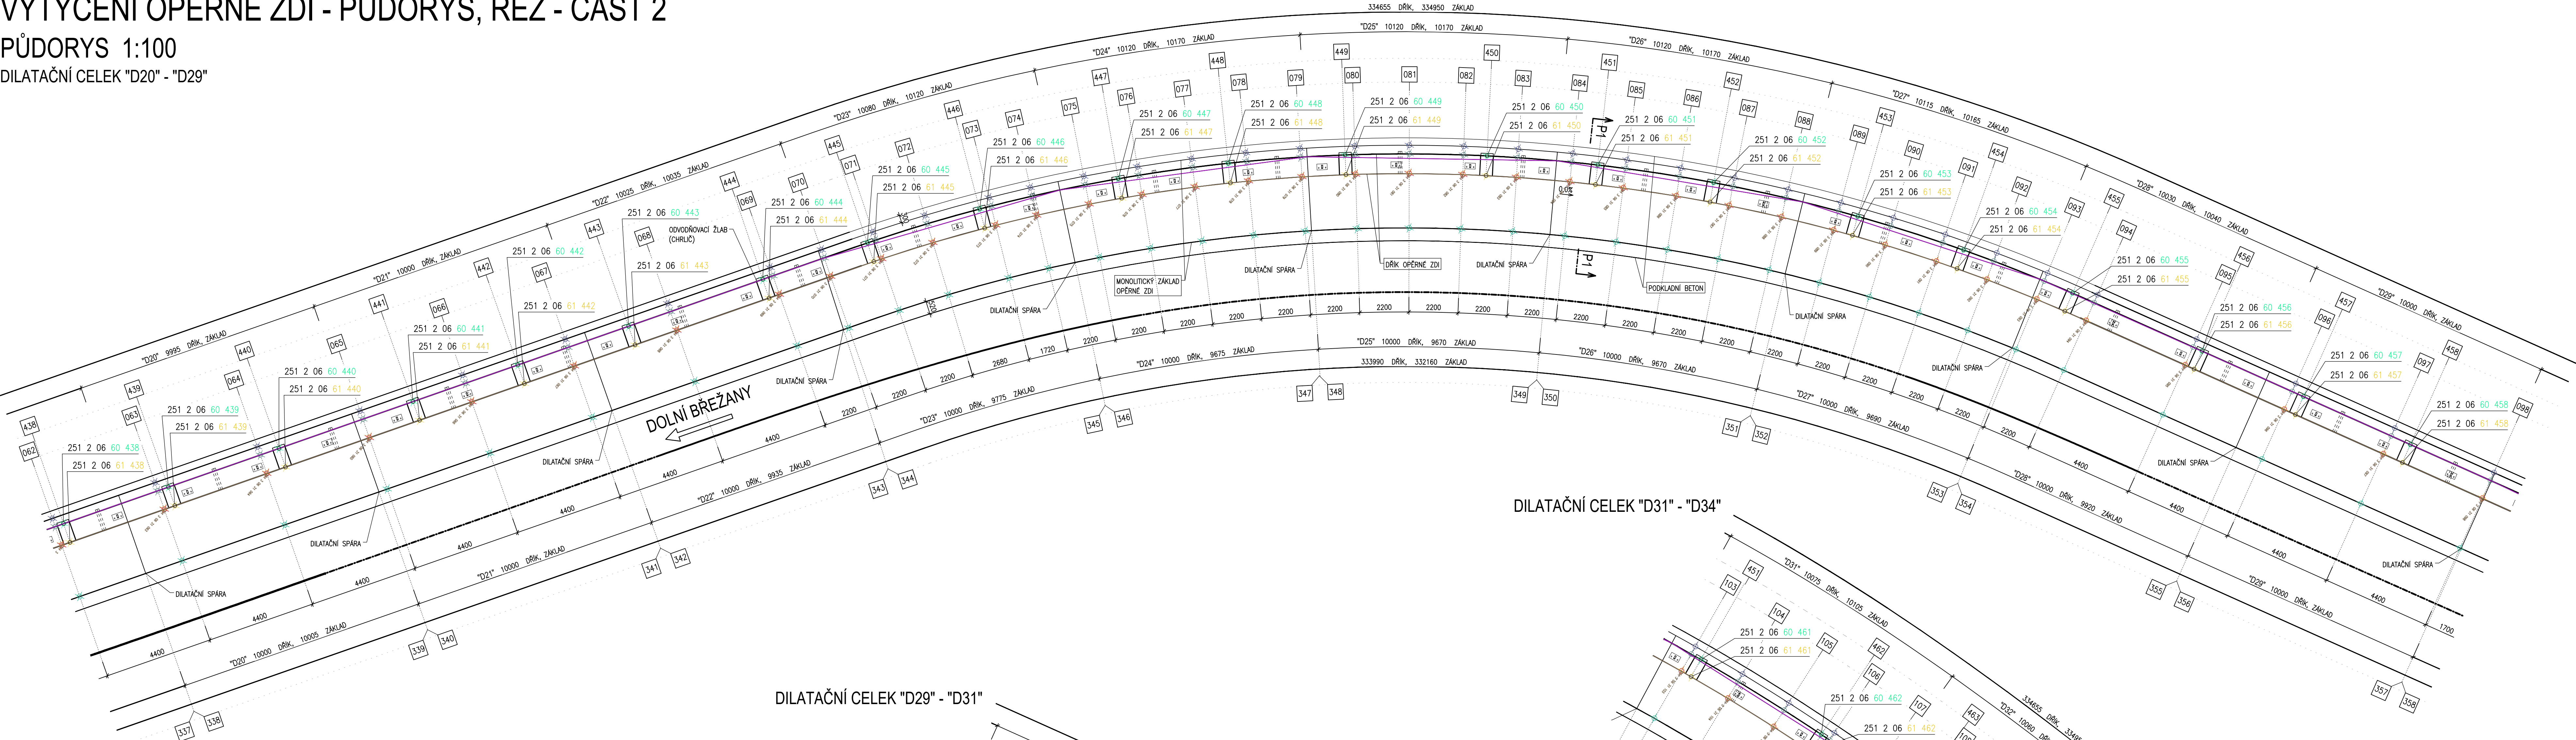


SCHÉMA ČÍSLOVÁNÍ BODŮ P1-P1 1:25

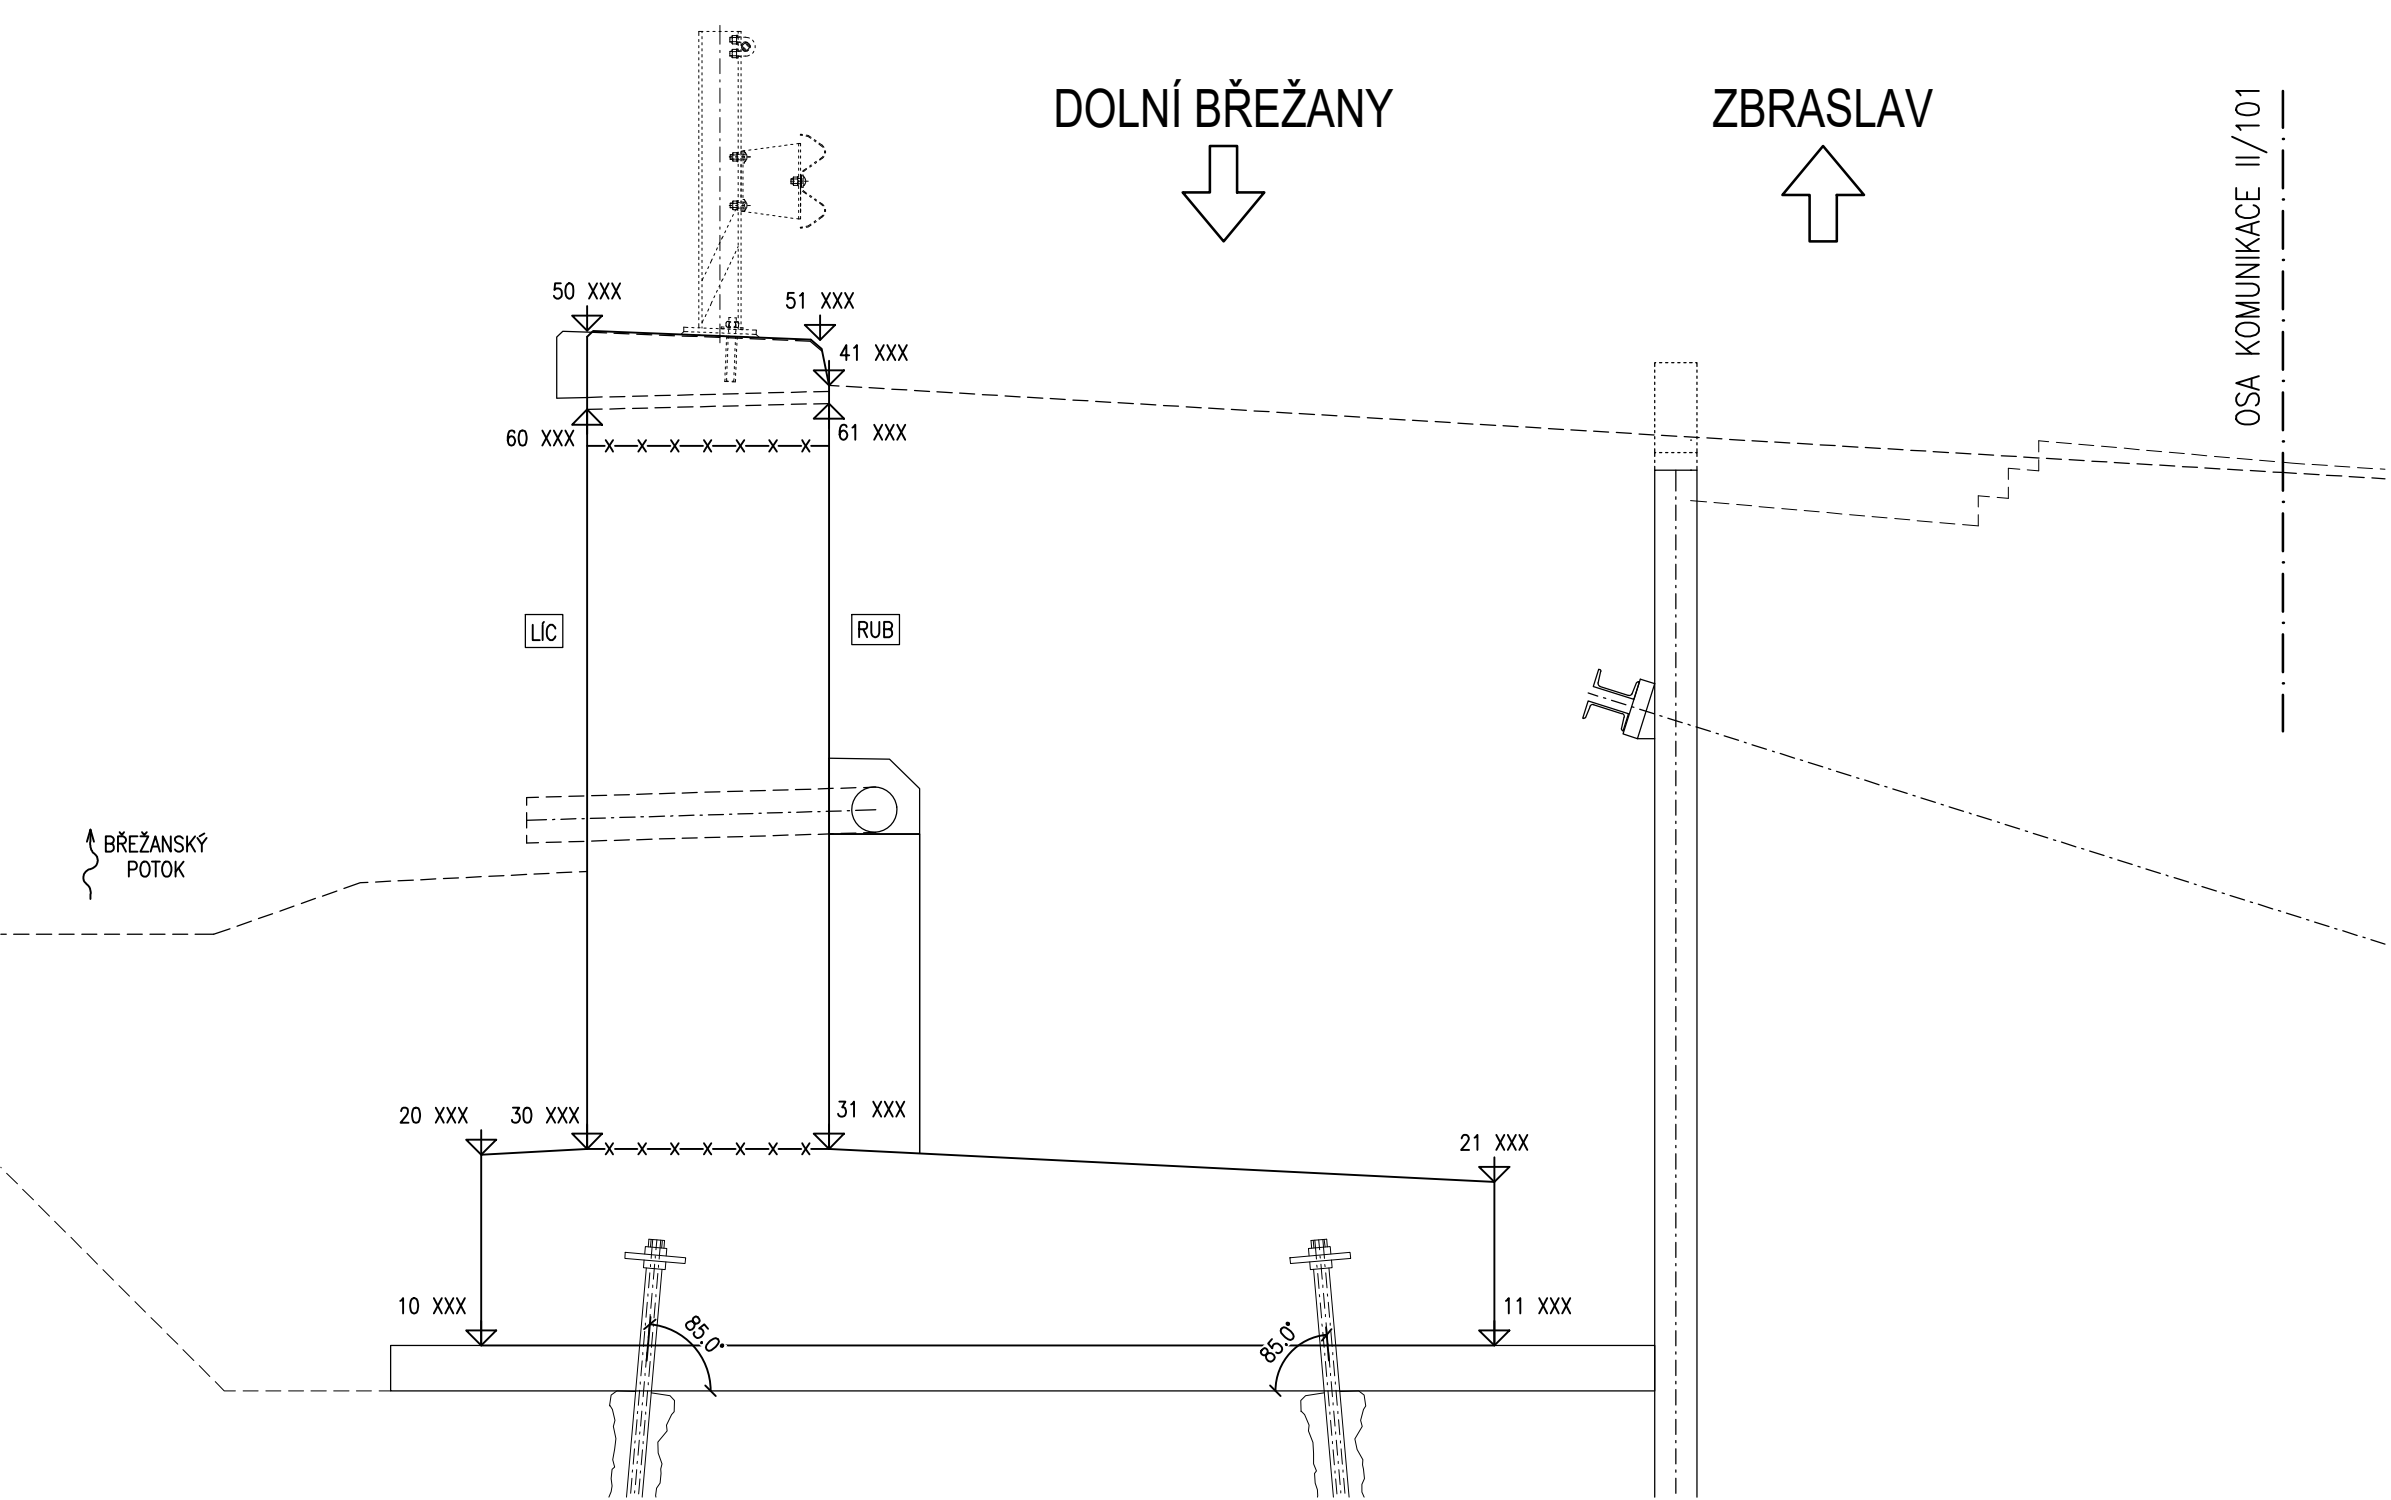

ČÍSLOVÁNÍ VYTÝČOVANÝCH BODŮ

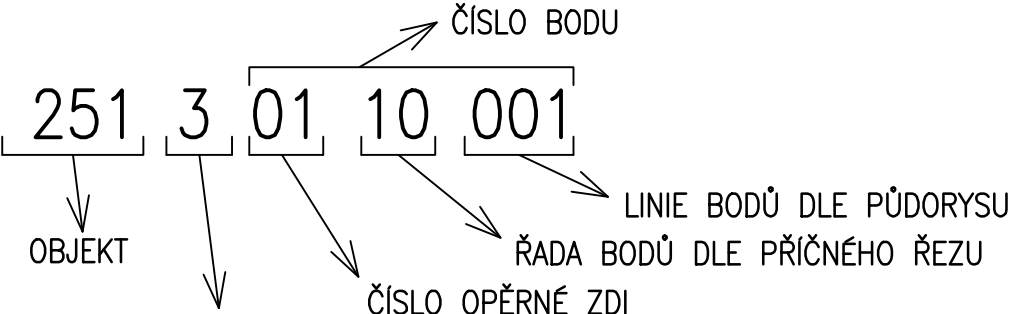


- STAVEBNÍ CELEK
- 0 ... HLAVNÍ BODY
 - 1 ... VÝKOPY, PAŽENÍ
 - 2 ... MIKROPILOTY
 - 3 ... SPODNÍ STAVBA/OPĚRNÁ ZED
 - 4 ... NOSNÁ KONSTRUKCE
 - 5 ... PŘÍSLUŠENSTVÍ

POZNÁMKY

- ZHOTOVITEL JE POVINEN PRO VEŠKERÝ ZEMĚMĚŘICKÉ PRÁCE POSTUPOVAT DLE TKP KAP. 1, ODS. 1.6.3.
- ZÁKLADNÍ LINIE JE VYTÝČENA PO 2,2m; RESPEKTIVĚ PO 4,4m V LÍCI ZDI
- ČÍSLOVNÍ BODŮ VYTÝČENÍ JE VE SMĚRU STAVBY

DILATAČNÍ CELEK "D29" - "D31"

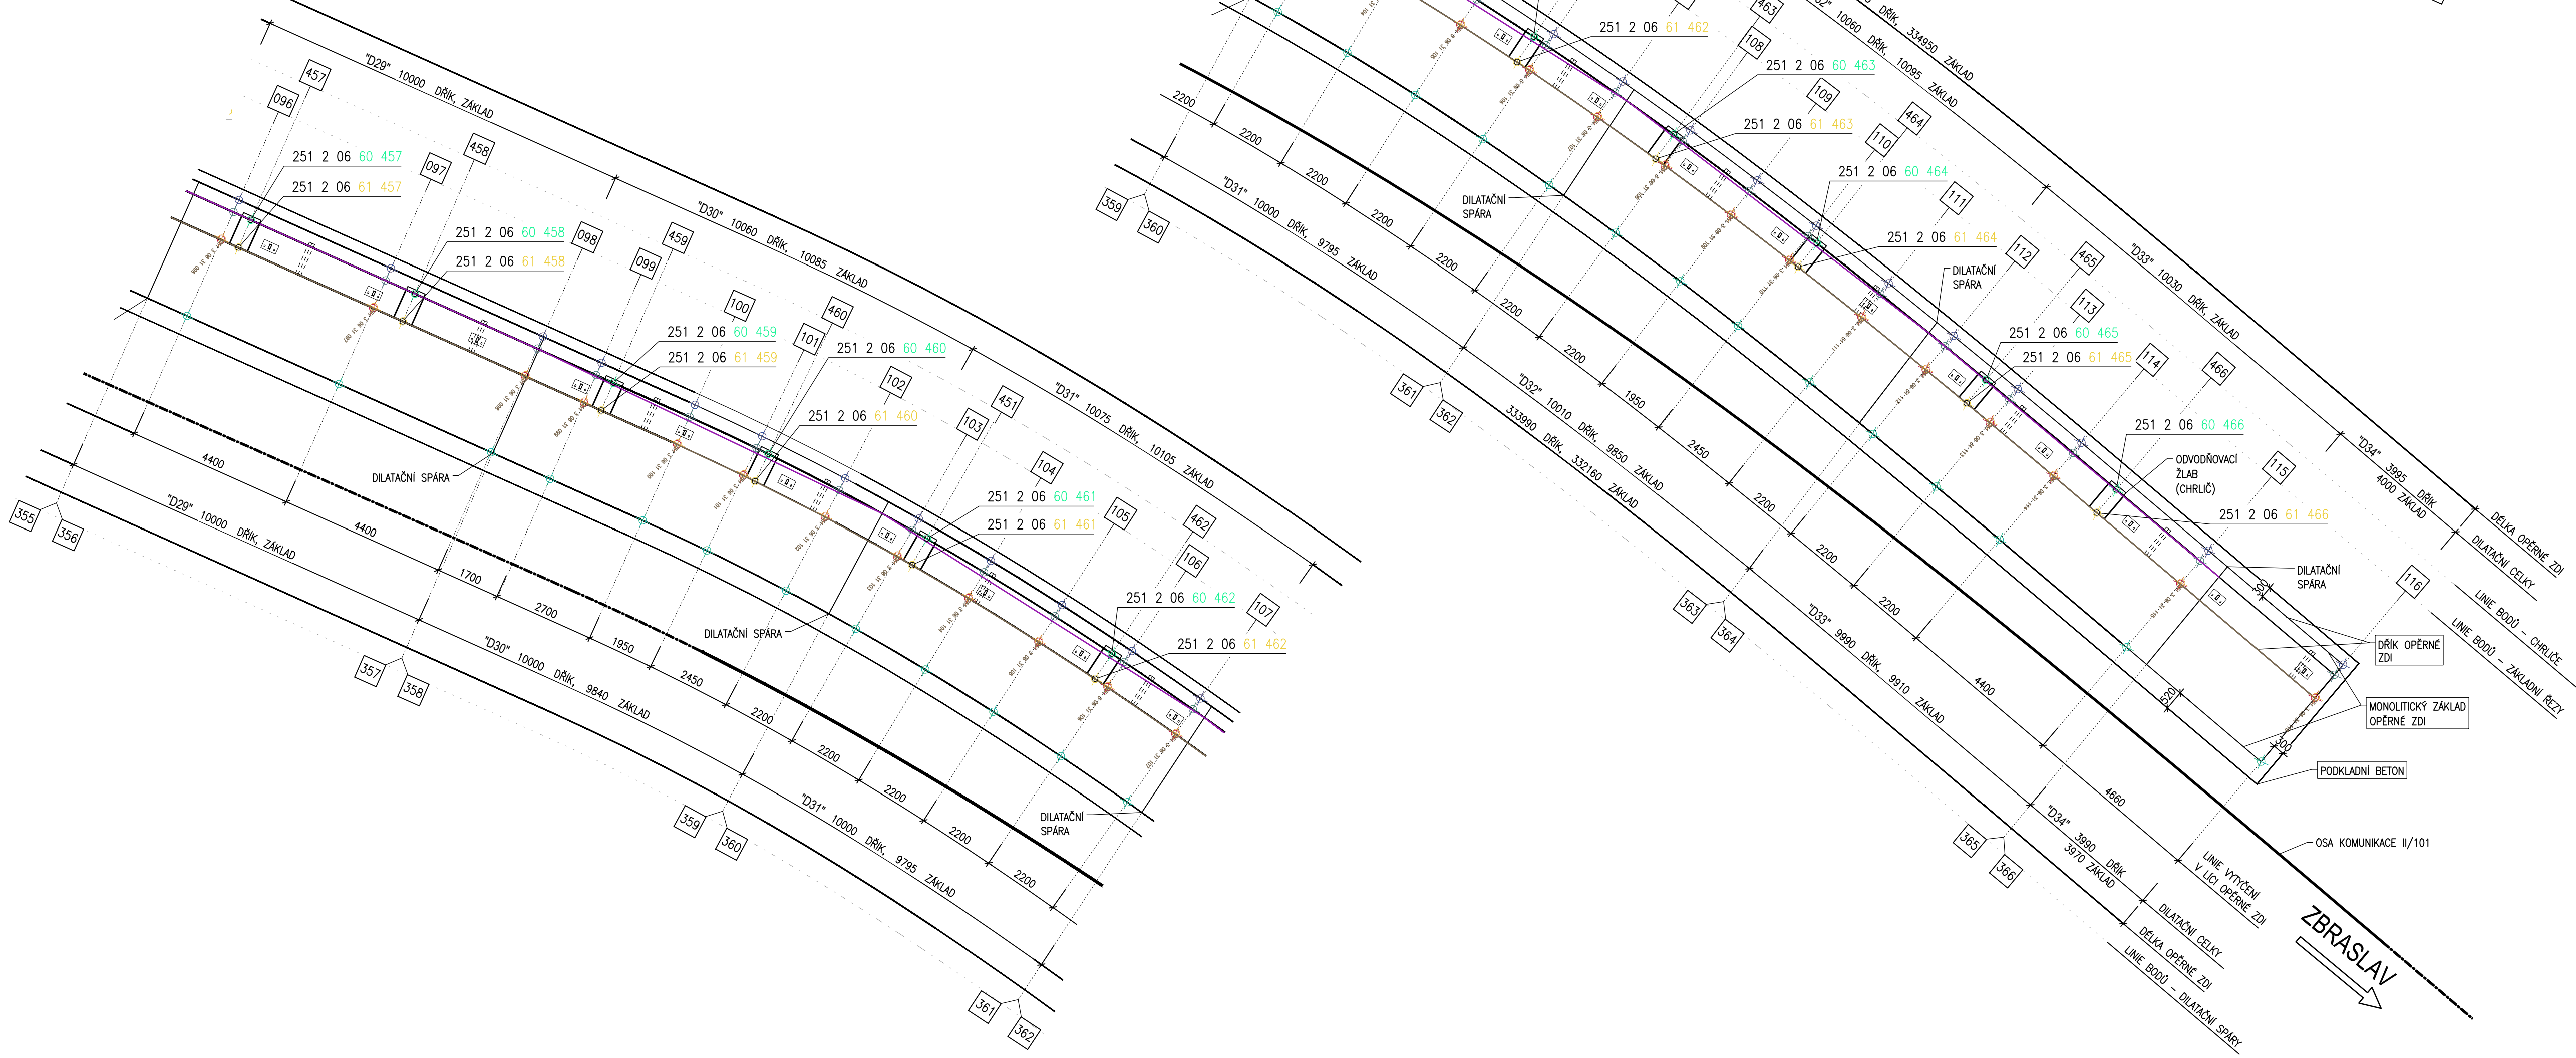

PŘEDKONCEPT

OZNAČ. TEXT ZMĚNY - ODŮVODNĚNÍ		DATUM	
TABULKA ZMĚN		PODPIS	
Název stavby		ČÍSLO OBJEKTU	
II/101 Dolní Břežany - Zbraslav		SO 251.2	
Objednatel stavby			
		Krajská správa a údržba silnic Středočeského kraje, příspěvková organizace Zborovská 611/11, 150 21 Praha 5-Smíchov	
Autorský dozor			
		GeoTec-GS, a.s. Chmelová 2920/6, 106 00 Praha 10	
Technický dozor investora		RAZÍTKO	
		TES + SGS + SGG vedoucí sdružení: TES Consulting, s.r.o. V Olšánské 2300/75, 100 00 Praha 10-Strašnice	
Datum		PODPIS	
Zhotovitel stavby		RAZÍTKO	
		M-SILNICE a.s. Husova 1697, 530 03 Pardubice www.msilnice.cz	
Datum		PODPIS	
Koordinační RDS		RAZÍTKO	
		M - PROJEKCE s. r. o. Reslova 956/13, 500 02 Hradec Králové www.m-projekce.cz	
Datum		PODPIS	
Souřadnicový systém: S-JTSK		Výškový systém: Bpv	
Zpracovatel stavebního objektu/části:			
Projekční kancelář PRIS spol. s r. o. Osova 717/20, 625 00 Brno-Starý Lískovec www.pris.cz			
Vyracoval:		Razítko:	
Ing. Ondřej Vytásek 			
Odpovědný projektant:		PROJEKČNÍ KANCELÁŘ PRIS spol. s r. o.	
Ing. Martin Reutka 		OSOVA 20, 625 00 BRNO	
Číslo zakázky:			
25-122-02			
Objekt/část:		Měřítko:	
SO 251.2 - OPĚRNÉ ZDI		1:100	
ZED č. 06		Stupeň:	
Příloha:		RDS	
VYTÝČENÍ OPĚRNÉ ZDI - PŮDORYS, ŘEZ - ČÁST 2		Číslo přílohy:	
		114_VYT2	