

VÝZTUŽ OPĚRNÉ ZDI

PRÍČNÝ ŘEZ P1-P1 1:25



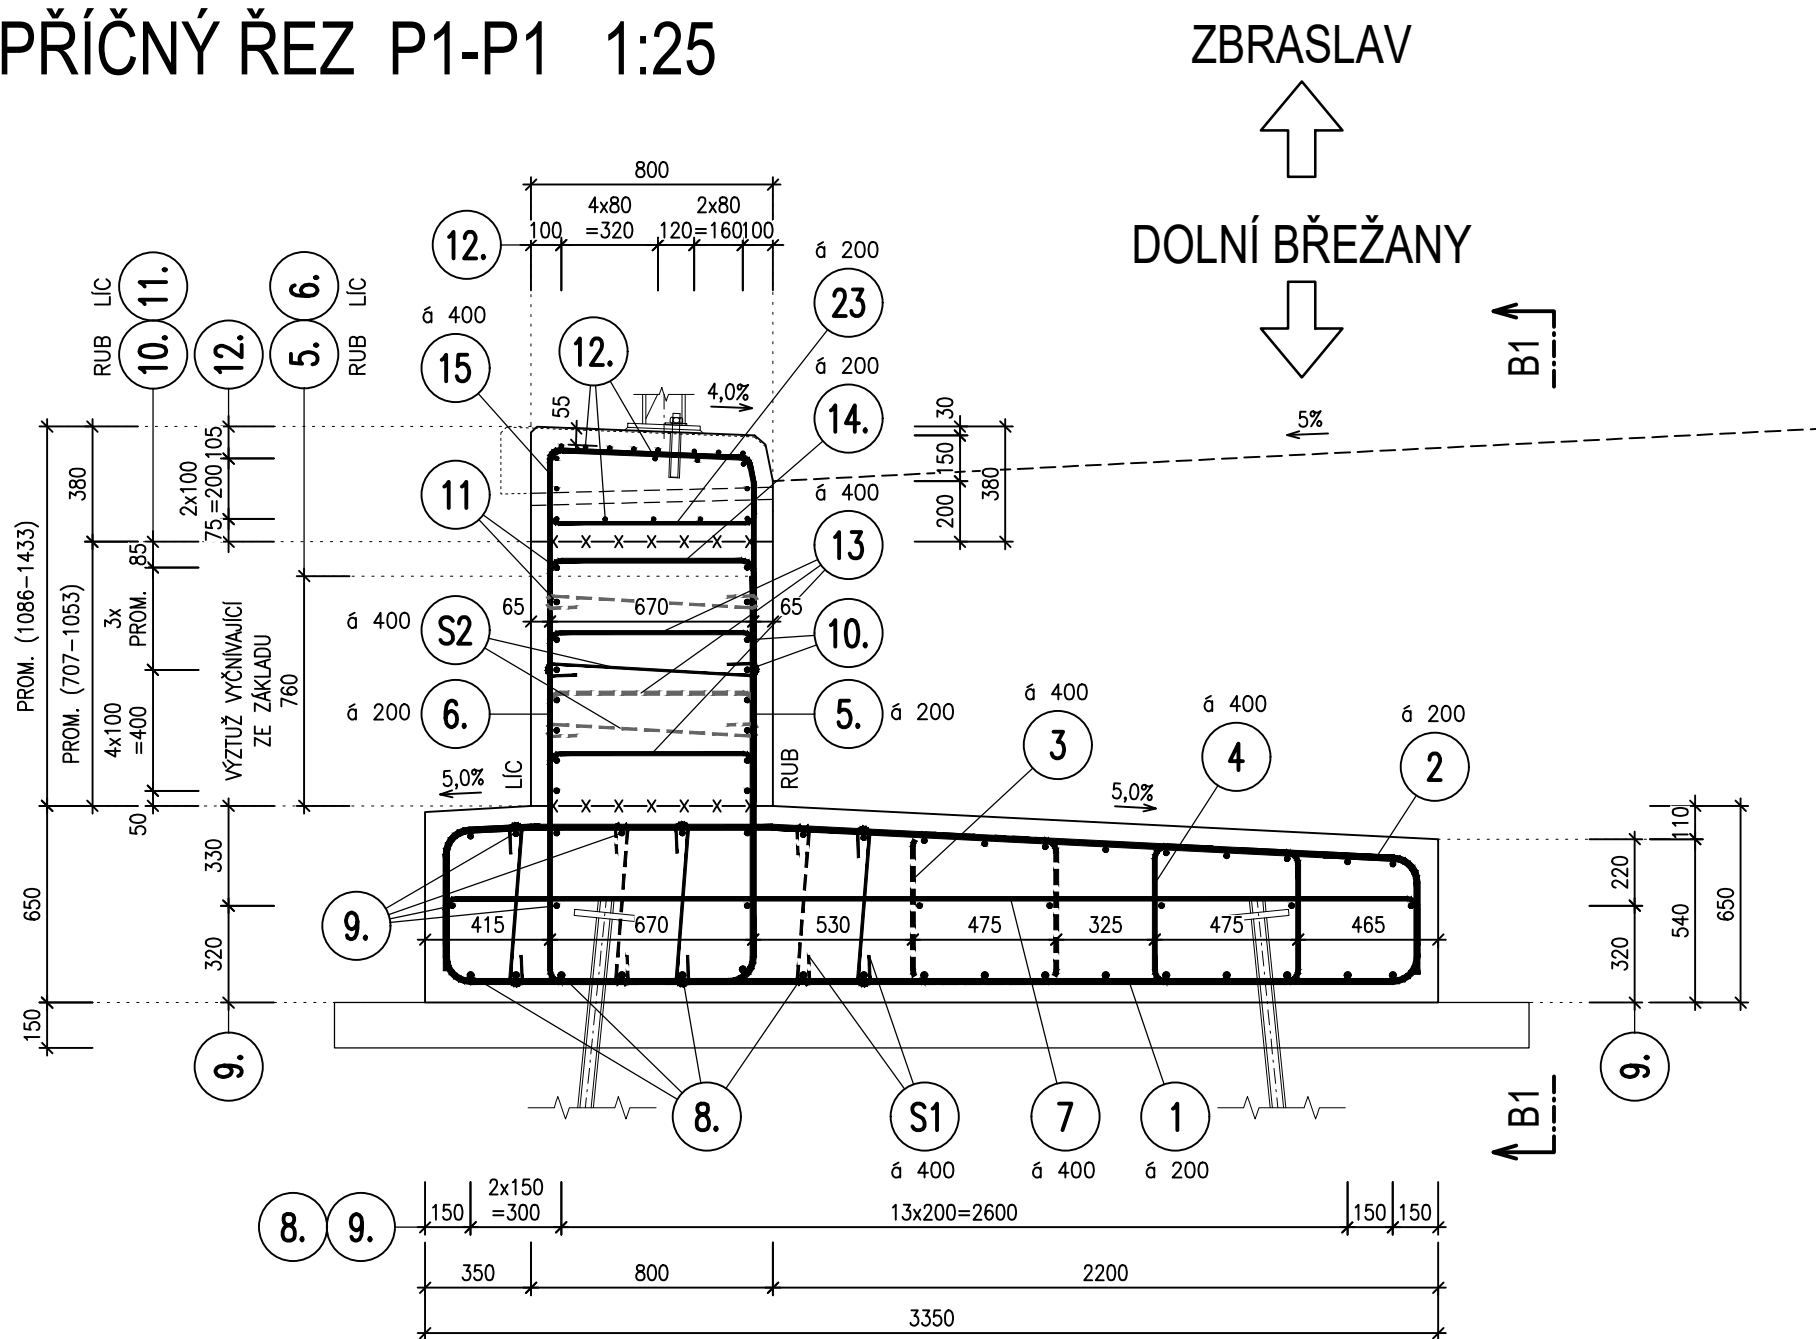


SCHÉMA VÝZTUŽE 1:25

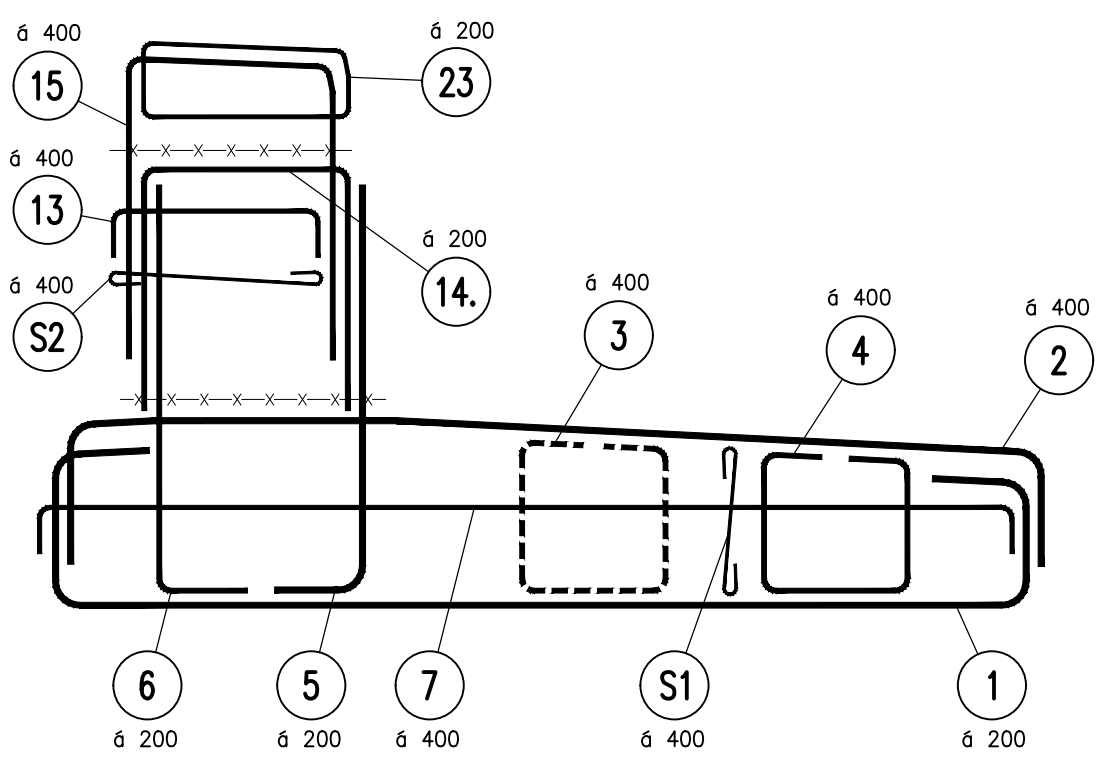


VÝTAH VÝZTUŽE - ZÁKLAD 1:25

VÝZTUŽ KÓTOVÁNA NA VNĚJŠÍ OBRSY

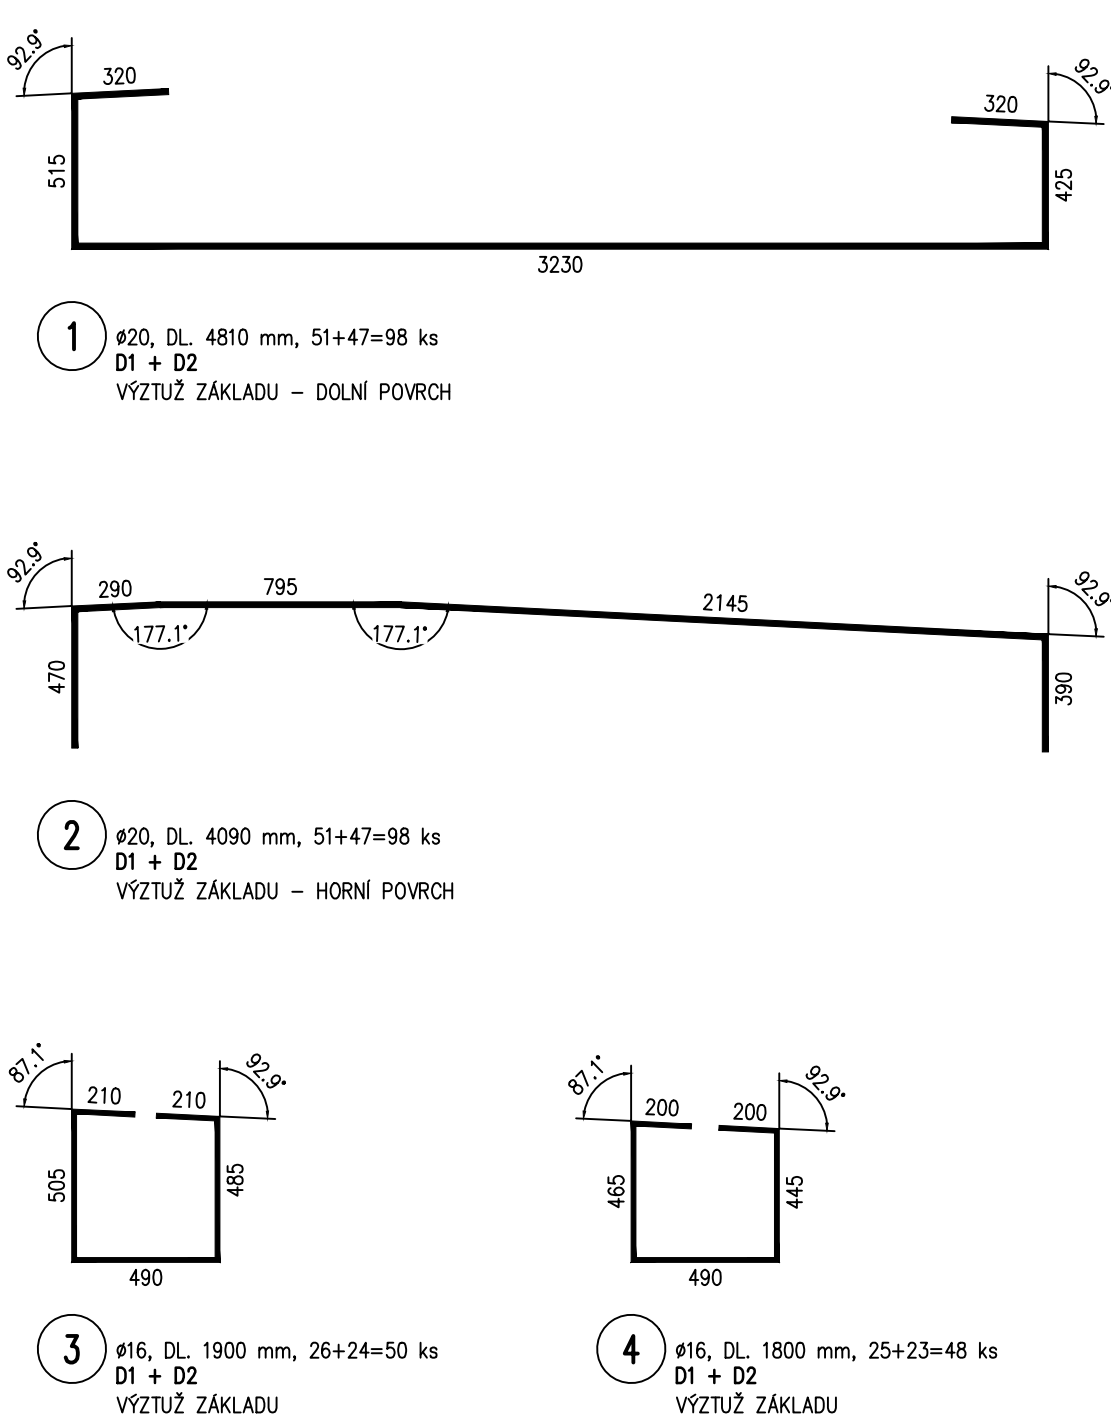


POHLED P2-P2 1:50

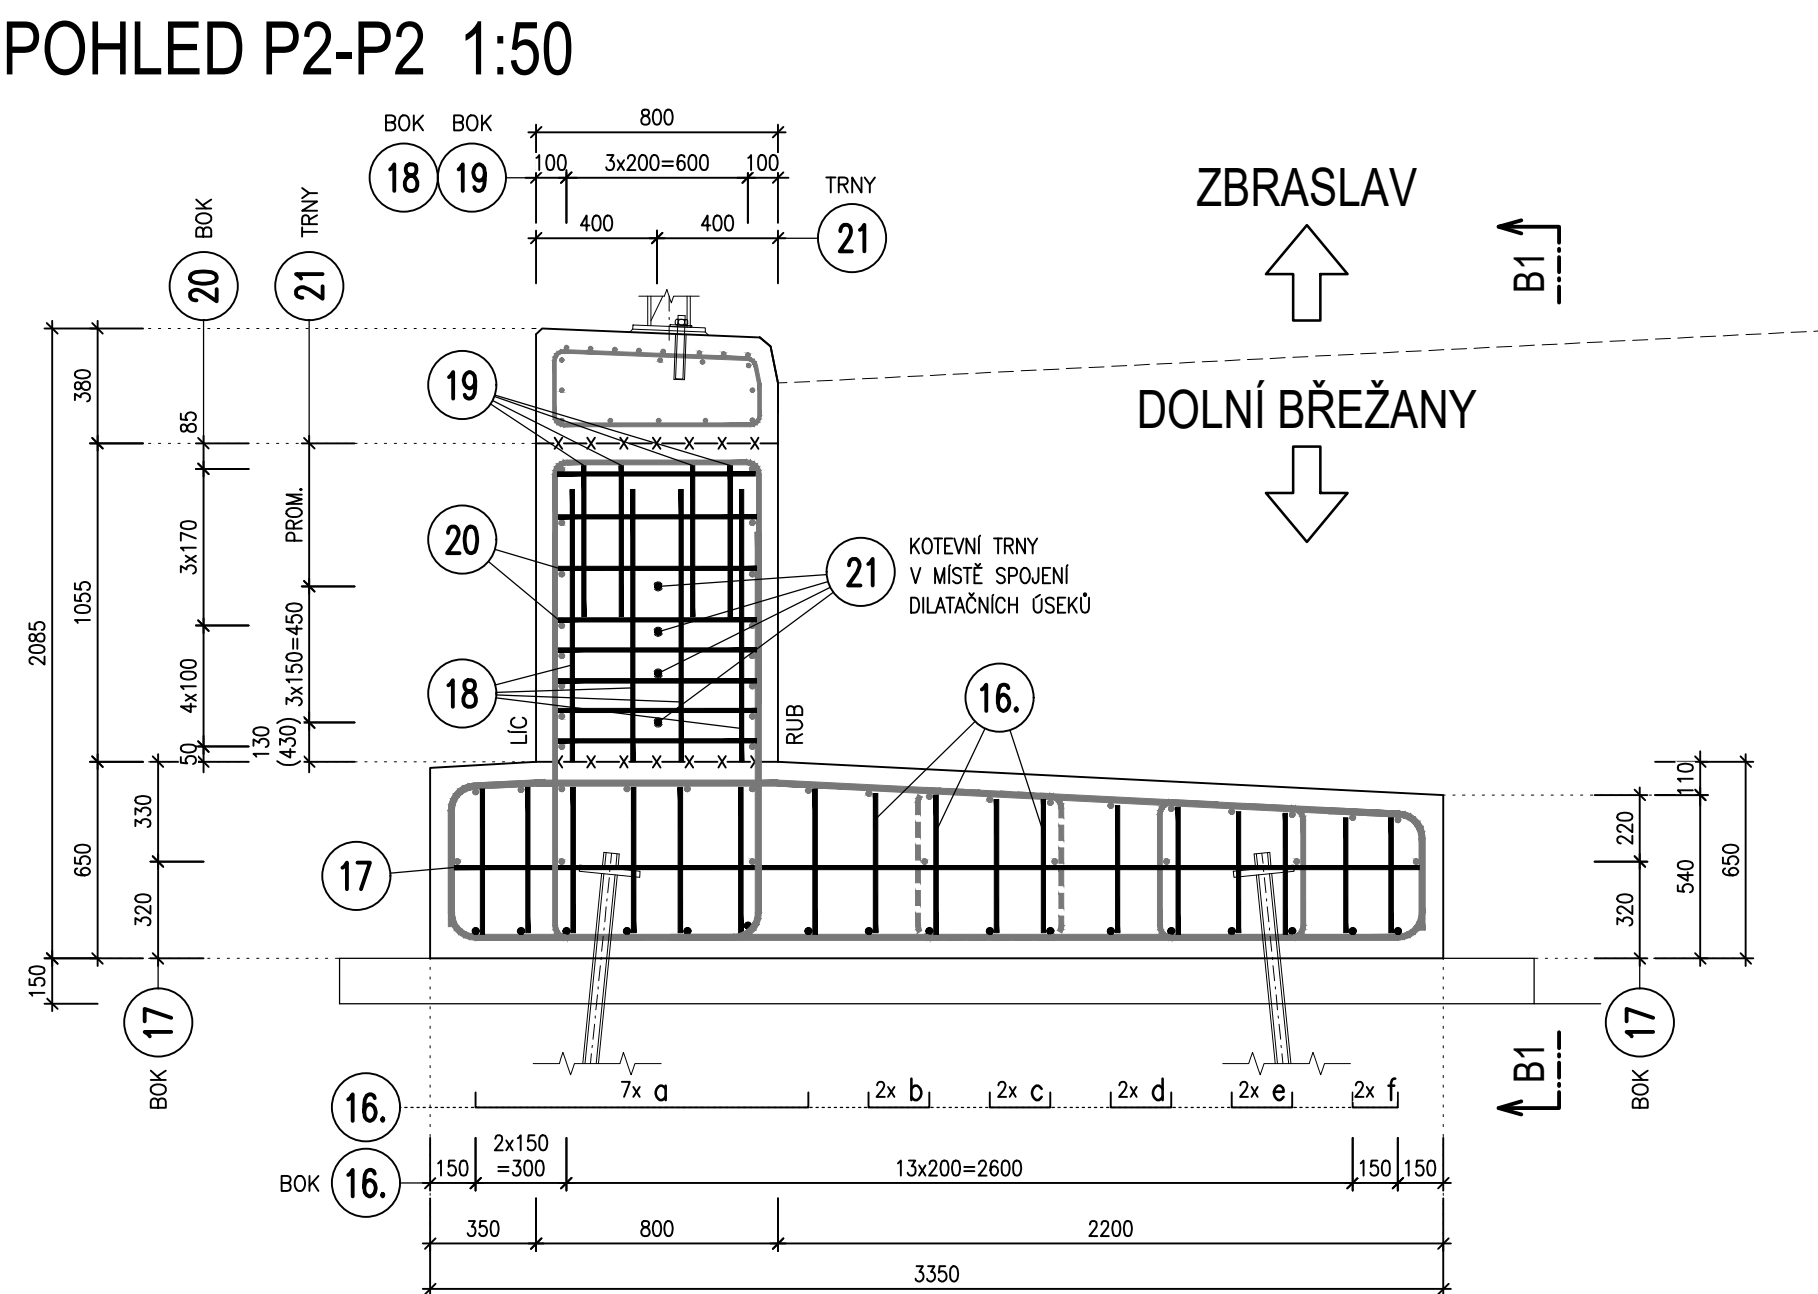


VÝTAH VÝZTUŽE - DŘÍK 1:25

VÝZTUŽ KÓTOVÁNA NA VNĚJŠÍ OBRSY

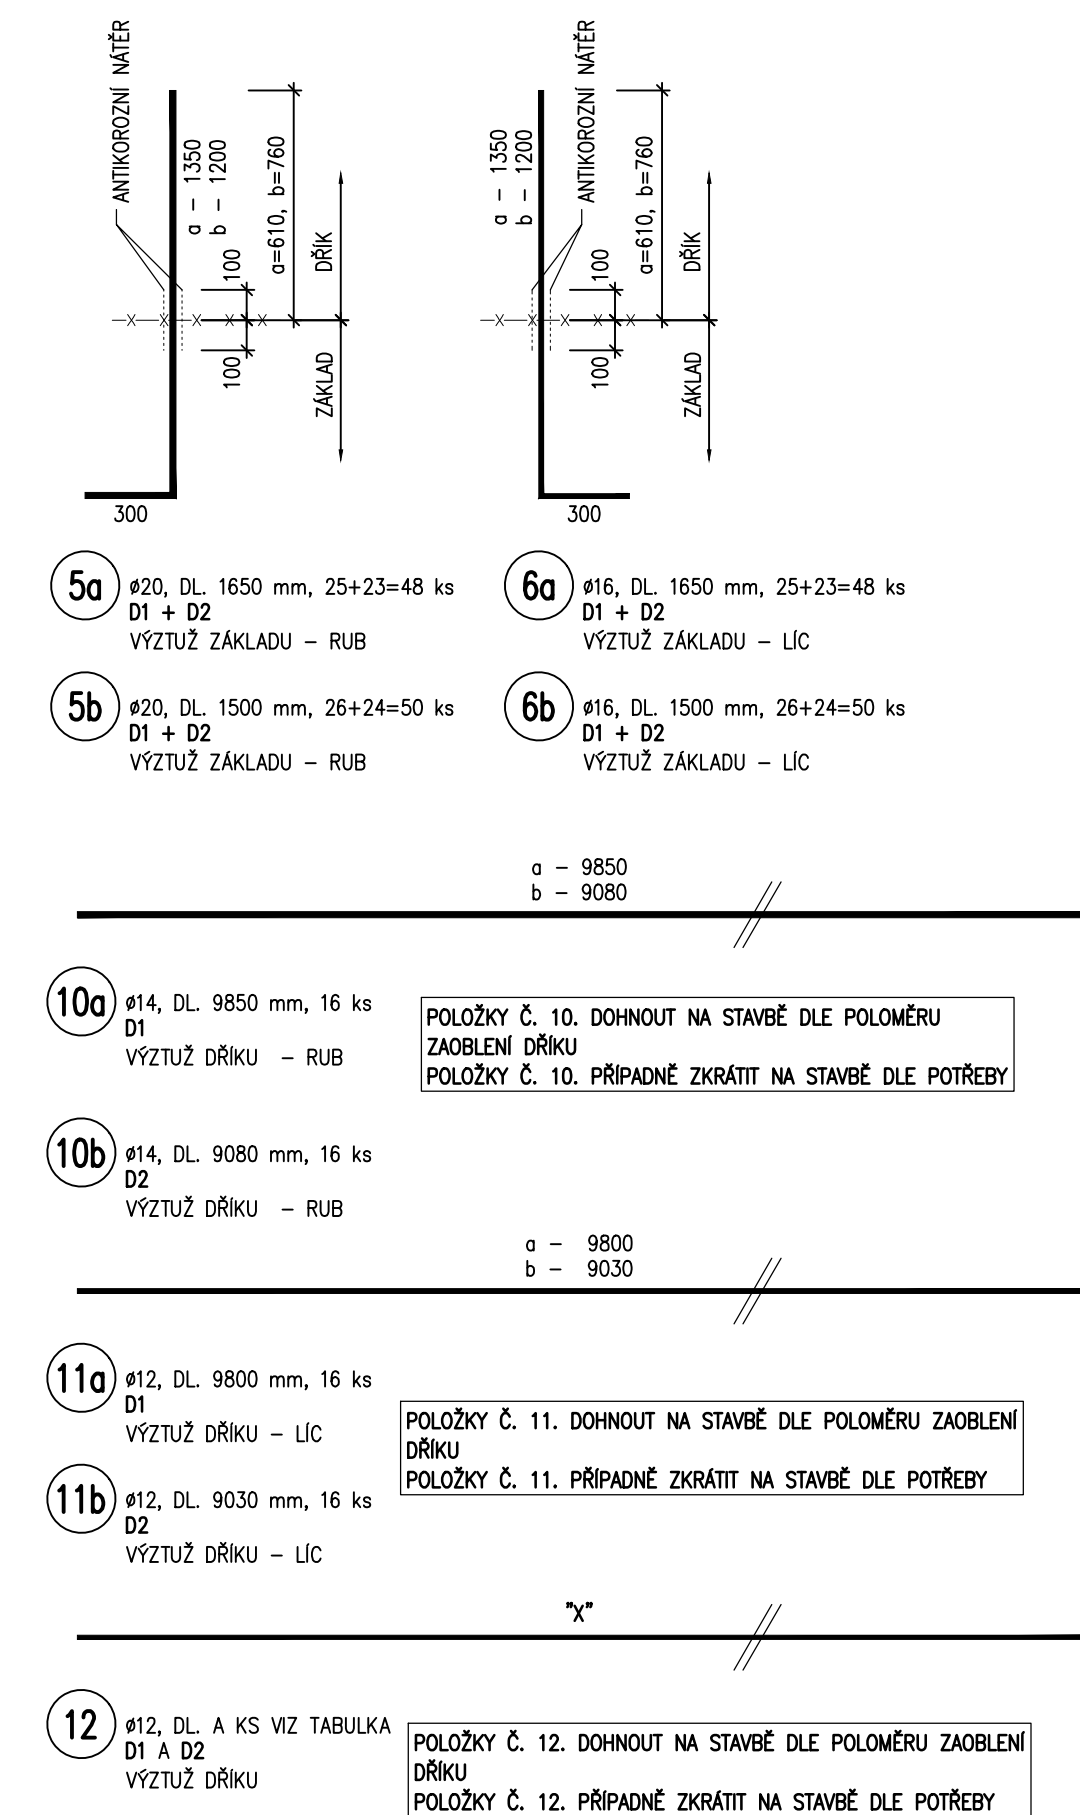

OZN.	X	Délka	Počet	Dilatační
		celkem	celkem	usek
	[mm]	[mm]	[ks]	[ozn.]
12a	9850	9850	5	D1
12b	1600	1600	28	D1, D2
12c	4560	4560	14	D1
12d	2340	2340	14	D1
12e	9080	9080	5	D2
12f	4370	4370	14	D2
12g	1800	1800	14	D2
CELKEM			322430	mm

POHLED V LÍCI B1-B1 1:50

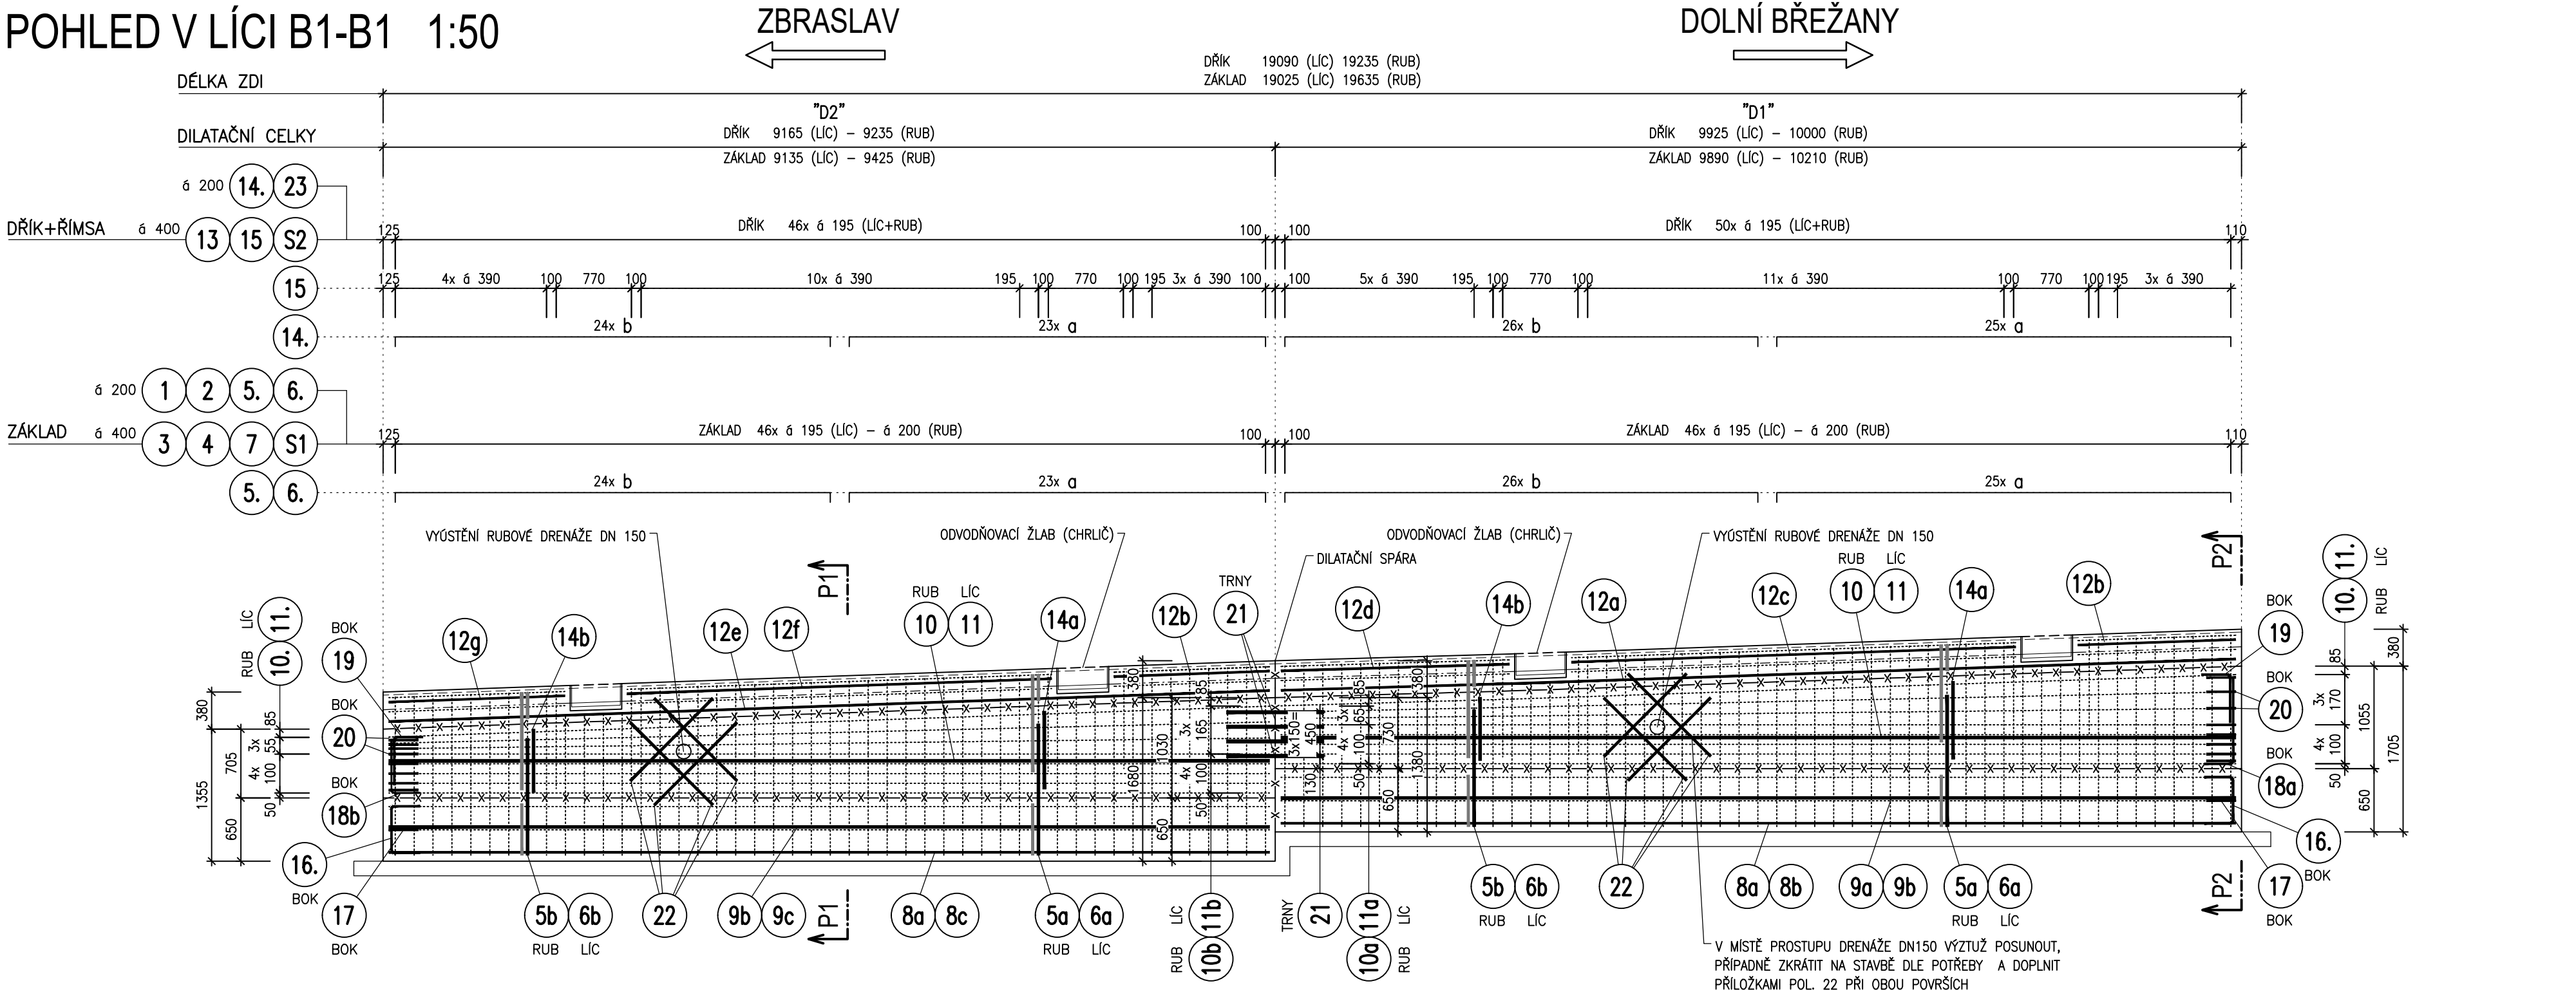


VÝKAZ VÝZTUŽE - ZÁKLAD

OZN.	Φ [mm]	DĚLKA 1ks [mm]	ks	DĚLKA DLE Φ [m]			
				Φ 12	Φ 14	Φ 16	Φ 20
1	20	4810	98				471,38
2	20	4090	98				400,82
3	16	1900	50			95,00	
4	16	1800	48			86,40	
7	10	3550	50				
8a	20	7000	38				266,00
8b	20	4200	19				79,80
8c	20	3400	19				64,60
9a	14	7000	62		434,00		
9b	14	4000	31		124,00		
9c	14	3200	31		99,20		
16	10	35520	1				
17	10	3800	2				
S1	8	660	246				
DĚLKA DLE Φ CELKEM			[m]	0,00	657,20	181,40	1282,60
HMOTNOST DLE Φ 1bm			[kg]	0,888	1,208	1,578	2,466
HMOTNOST DLE Φ CELKEM			[kg]	0,00	794,17	286,31	3163,08
HMOTNOST CELKEM			[kg]		4444		

VÝKAZ VÝZTUŽE - DŘÍK

OZN.	φ	DĚLKA		ks	DĚLKA DLE φ [m]			
	[mm]	1ks [mm]			φ 8	φ 12	φ 16	φ 20
5a	20	1650	48					79,20
5b	20	1500	50					75,00
6a	16	1650	48				79,20	
6b	16	1500	50				75,00	
10a	14	9850	16					
10b	14	9080	16					
11a	12	9800	16			156,80		
11b	12	9030	16			144,48		
12	12	322430	1			322,43		
13	14	1000	171					
14a	14	2300	48					
14b	14	2000	50					
15	16	2650	86				227,90	
18a	10	1200	4					
18b	10	850	4					
19	10	800	8					
20	10	1250	16					
21	20	1000	4					4,00
22	16	1200	16				19,20	
23	12	2150	94			202,10		
S2	8	940	171		160,74			
DĚLKA DLE φ CELKEM				[m]	160,74	825,81	401,30	158,20
HMOTNOST DLE φ 1bm				[kg]	0,395	0,888	1,578	2,466
HMOTNOST DLE φ CELKEM				[kg]	63,43	733,17	633,39	390,14
HMOTNOST CELKEM				[kg]	2668			

VÝKAZ VÝZTUŽE CELKEM: 7112 kg

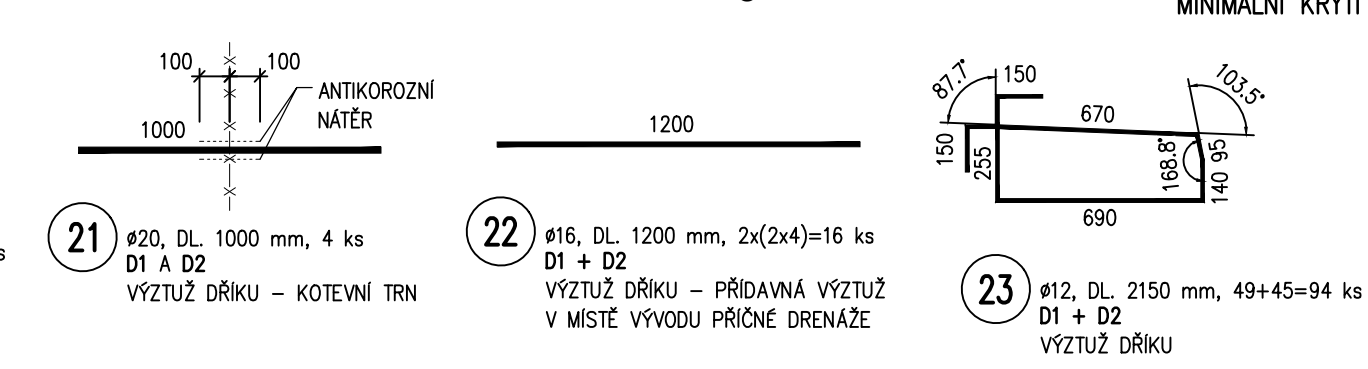

STAVEBNÍ MATERIÁLY

BETONY BUDOU PRAVEDENY DLE ČSN EN 206

CONSTRUKČNÍ BETONY:

ZB ZÁKLAD

ZB DŘÍK

OSTATNÍ BETONY:

PODKLADNÍ BETON

BETONÁRSKÁ VÝZTUŽ:

OCEL

B500B

NEJMENŠÍ PRŮMĚR TRNU d, PRO OHÝBÁNÍ

DLE ČSN EN 1992-1-1

Průměr prutu

φ ≤ 16mm

φ > 16mm

4φ

7φ

≥ 10φ

≥ 70mm

φ

φ

POZNÁMKY

- ZA ÚČELEM DOKONALÉHO PROBETONOVÁNÍ KONSTRUKCE NENÍ PŘÍPUSTNÉ, ABY MEZERA MEZI SOUBĚŽNÝMI POLOŽKAMI BYLA MENŠÍ NEŽ 35 mm.
- PRO PŘÍPADNÉ SVAŘOVÁNÍ VÝZTUŽE PLATÍ TP 193
- STYKOVANÁ VÝZTUŽ BUDE ULOŽENA NA SRAZ

KONCEPT

OZNAČ.	TEXT ZMĚNY - ODŮVODNĚNÍ	DATUM	PODPIS
TABULKA ZMĚN			

Název stavby	II/101 Dolní Břežany - Zbraslav	ČÍSLO OBJEKTU	SO 251.2
--------------	---------------------------------	---------------	----------

Objednatel stavby	Krásná správa a údržba silnic Středočeského kraje, příspěvková organizace Zborovská 811/1, 150 21 Praha 5-Smíchov
-------------------	---

Autorský dozor	GeoTec GS, a.s. Chmelová 2920/6, 106 00 Praha 10
----------------	--

Technický dozor investora	TES + SGS + SGG vedoucí sdružení: TES Consulting, s.r.o. V Olšanské 2300/75, 100 00 Praha 10-Strašnice	RAZITKO	DATUM	PODPIS
---------------------------	--	---------	-------	--------

Zhotovitel stavby	M-SILNICE a.s. Husova 1697, 530 03 Pardubice www.msilnice.cz	RAZITKO	DATUM	PODPIS
-------------------	--	---------	-------	--------

Koordinátor RDS	M - PROJEKCE s. r. o. Reslova 956/13, 500 02 Hradec Králové www.m-projekce.cz	RAZITKO	DATUM	PODPIS
-----------------	---	---------	-------	--------

Soutěžní systém: S-JTSK	Výškový systém: Bpv
-------------------------	---------------------

Zpracovatel stavebního objektu:Část:	Projekční kancelář PRIS spol. s r.o. Osová 717/20, 625 00 Brno-Starý Lískovec www.pris.cz
--------------------------------------	---

Vypracoval: Irena Synková Odpovědný projektant: Ing. Martin Reuhla Číslo zadání: 25-122-02	Hlavní inženýr projektu: Ing. Jiří Ehrenberger Kontroloval: Ing. Jiří ŠRUBAR Datum: 06/2026	Razítko: PRIS PROJEKČNÍ KANCELÁŘ PRIS spol. s r.o. OSOVÁ 20, 625 00 BRNO
--	---	--

Objekt:Část:	SO 251.2 - OPĚRNÉ ZDI ZEĎ č. 07	Měřítko: 1:50, 1:25	Souprava:
Příloha:	VÝZTUŽ OPĚRNÉ ZDI	Stupeň: RDS	Číslo přílohy: 106_VOZ