


VÝZTUŽ OPĚRNÉ ZDI

PŘÍČNÝ ŘEZ P1-P1 1:25

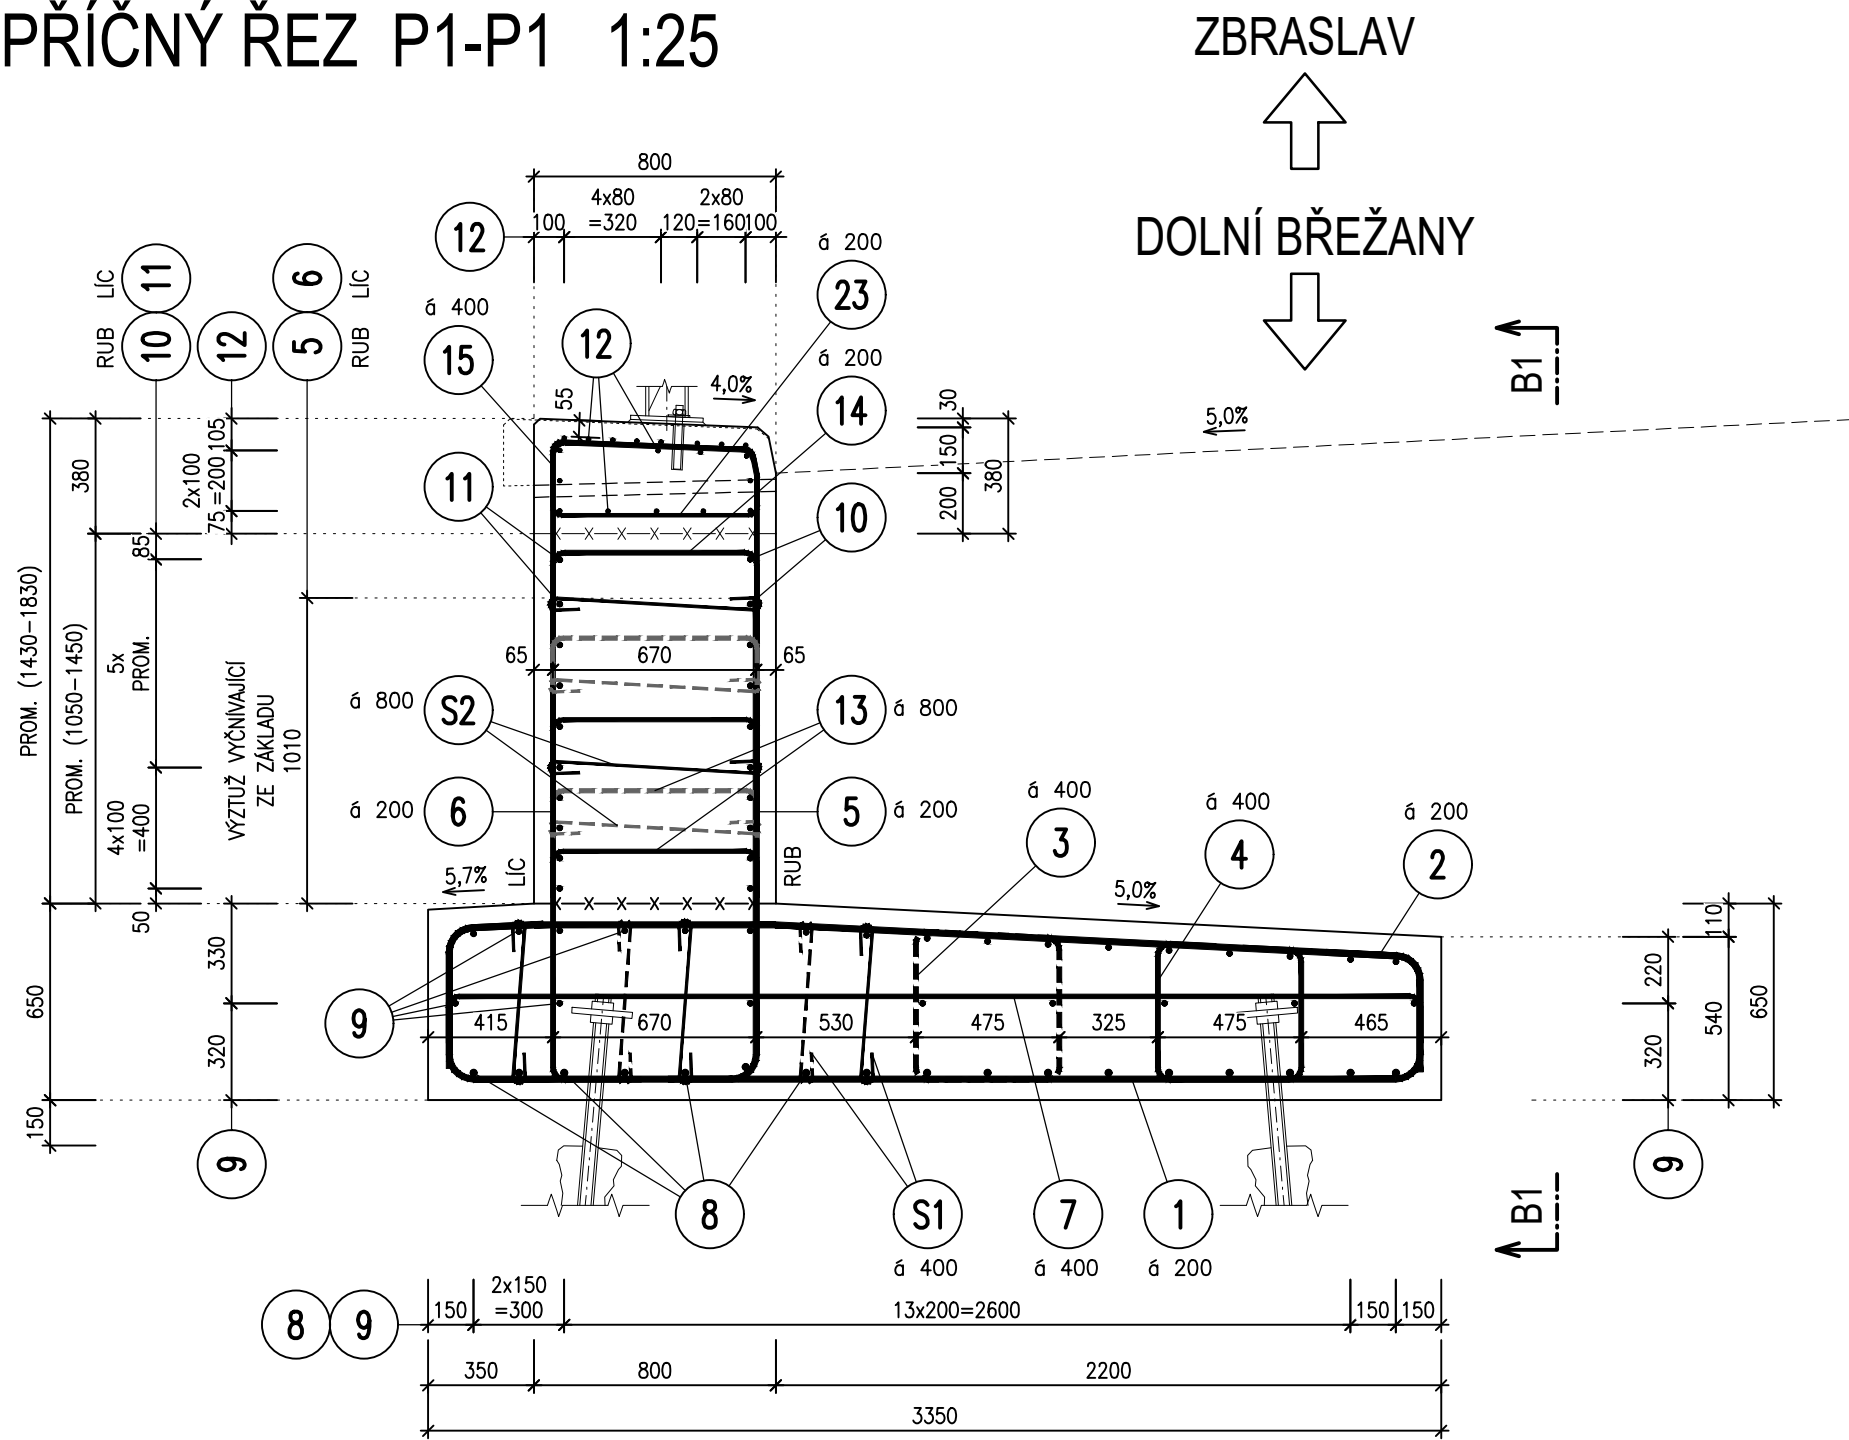

POHLED P2-P2 1:50



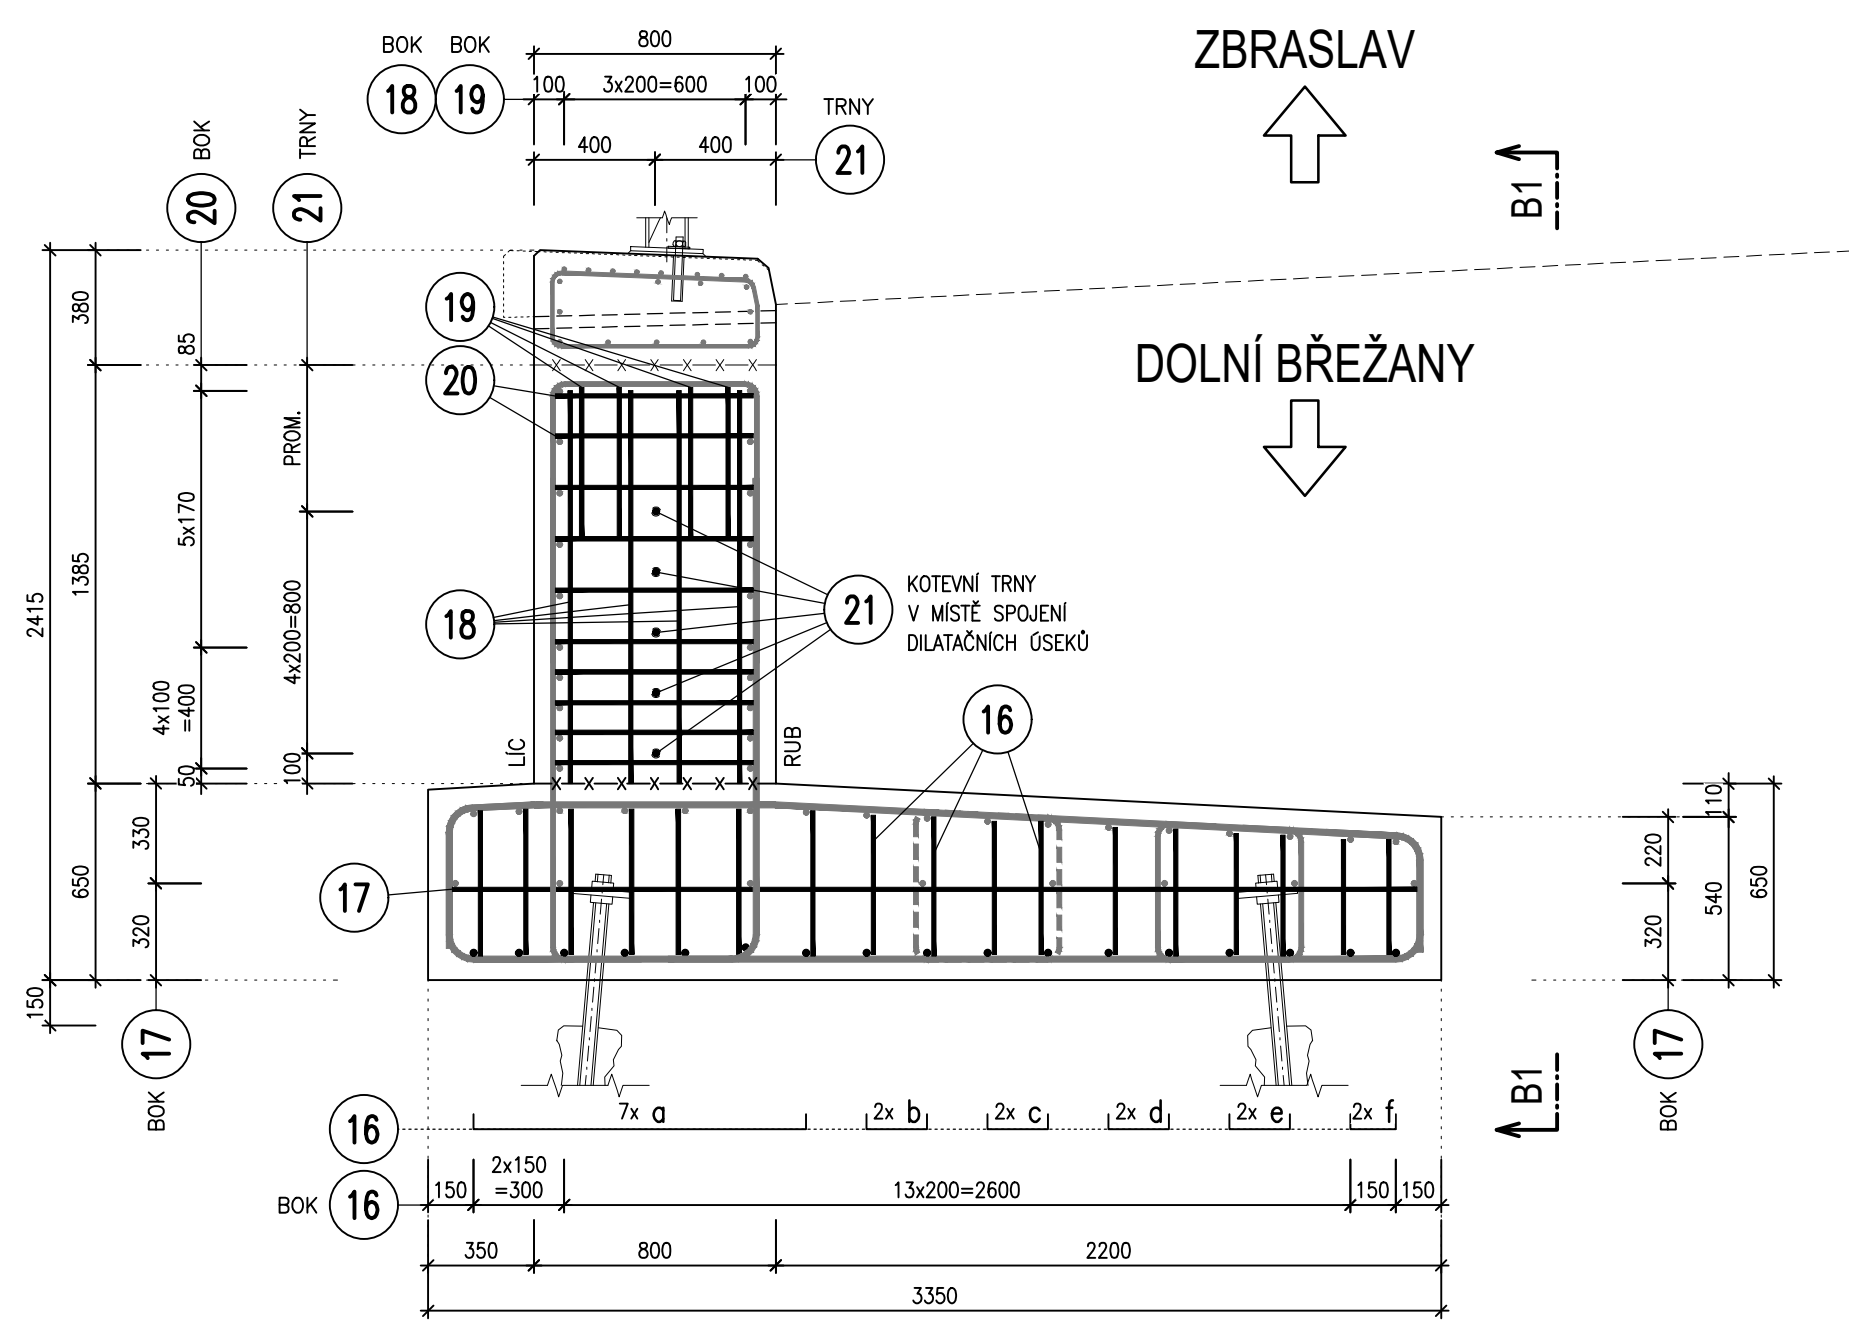


SCHÉMA VÝZTUŽE 1:25

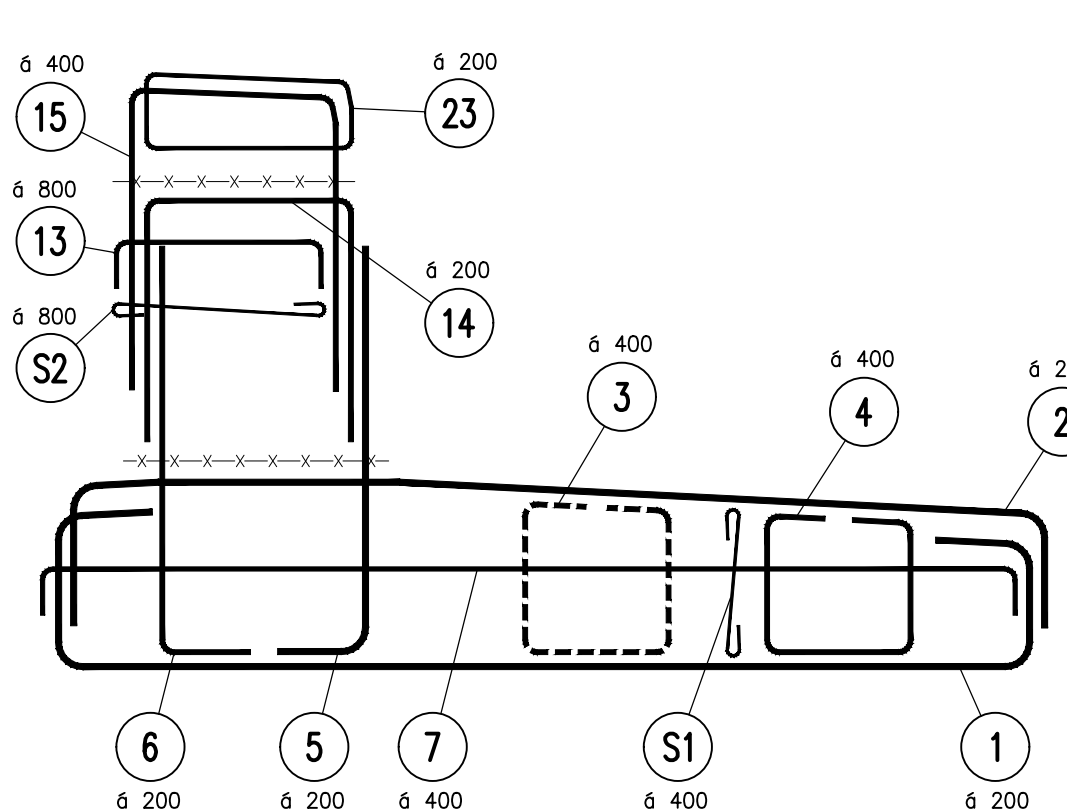


POHLED V LÍCI B1-B1 1:50

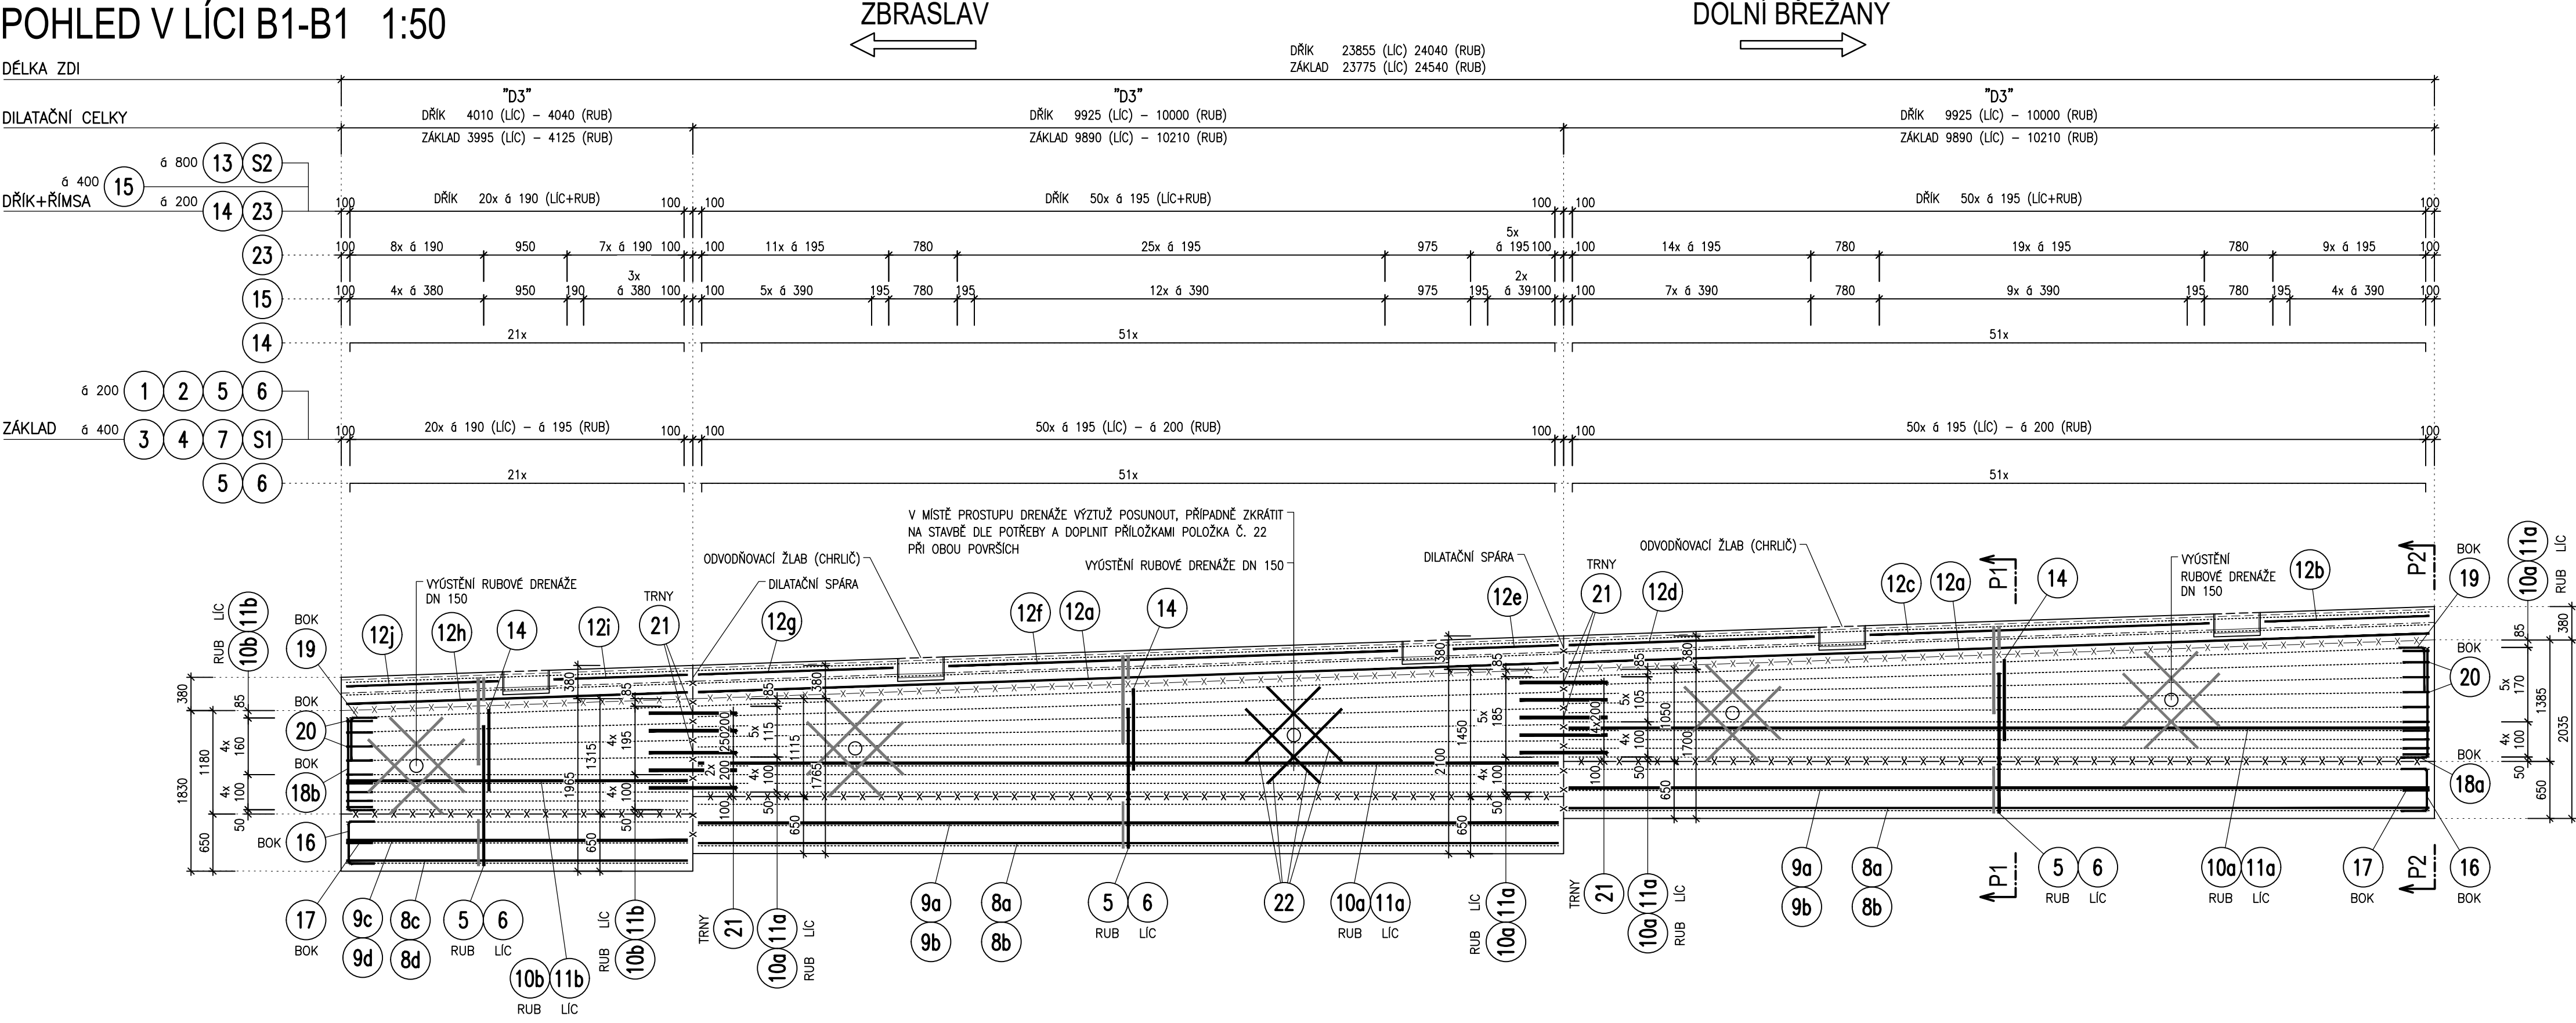

VÝTAH VÝZTUŽE - ZÁKLAD 1:25

VÝZTUŽ KÓTOVÁNA NA VNĚJŠÍ OBRYŠ

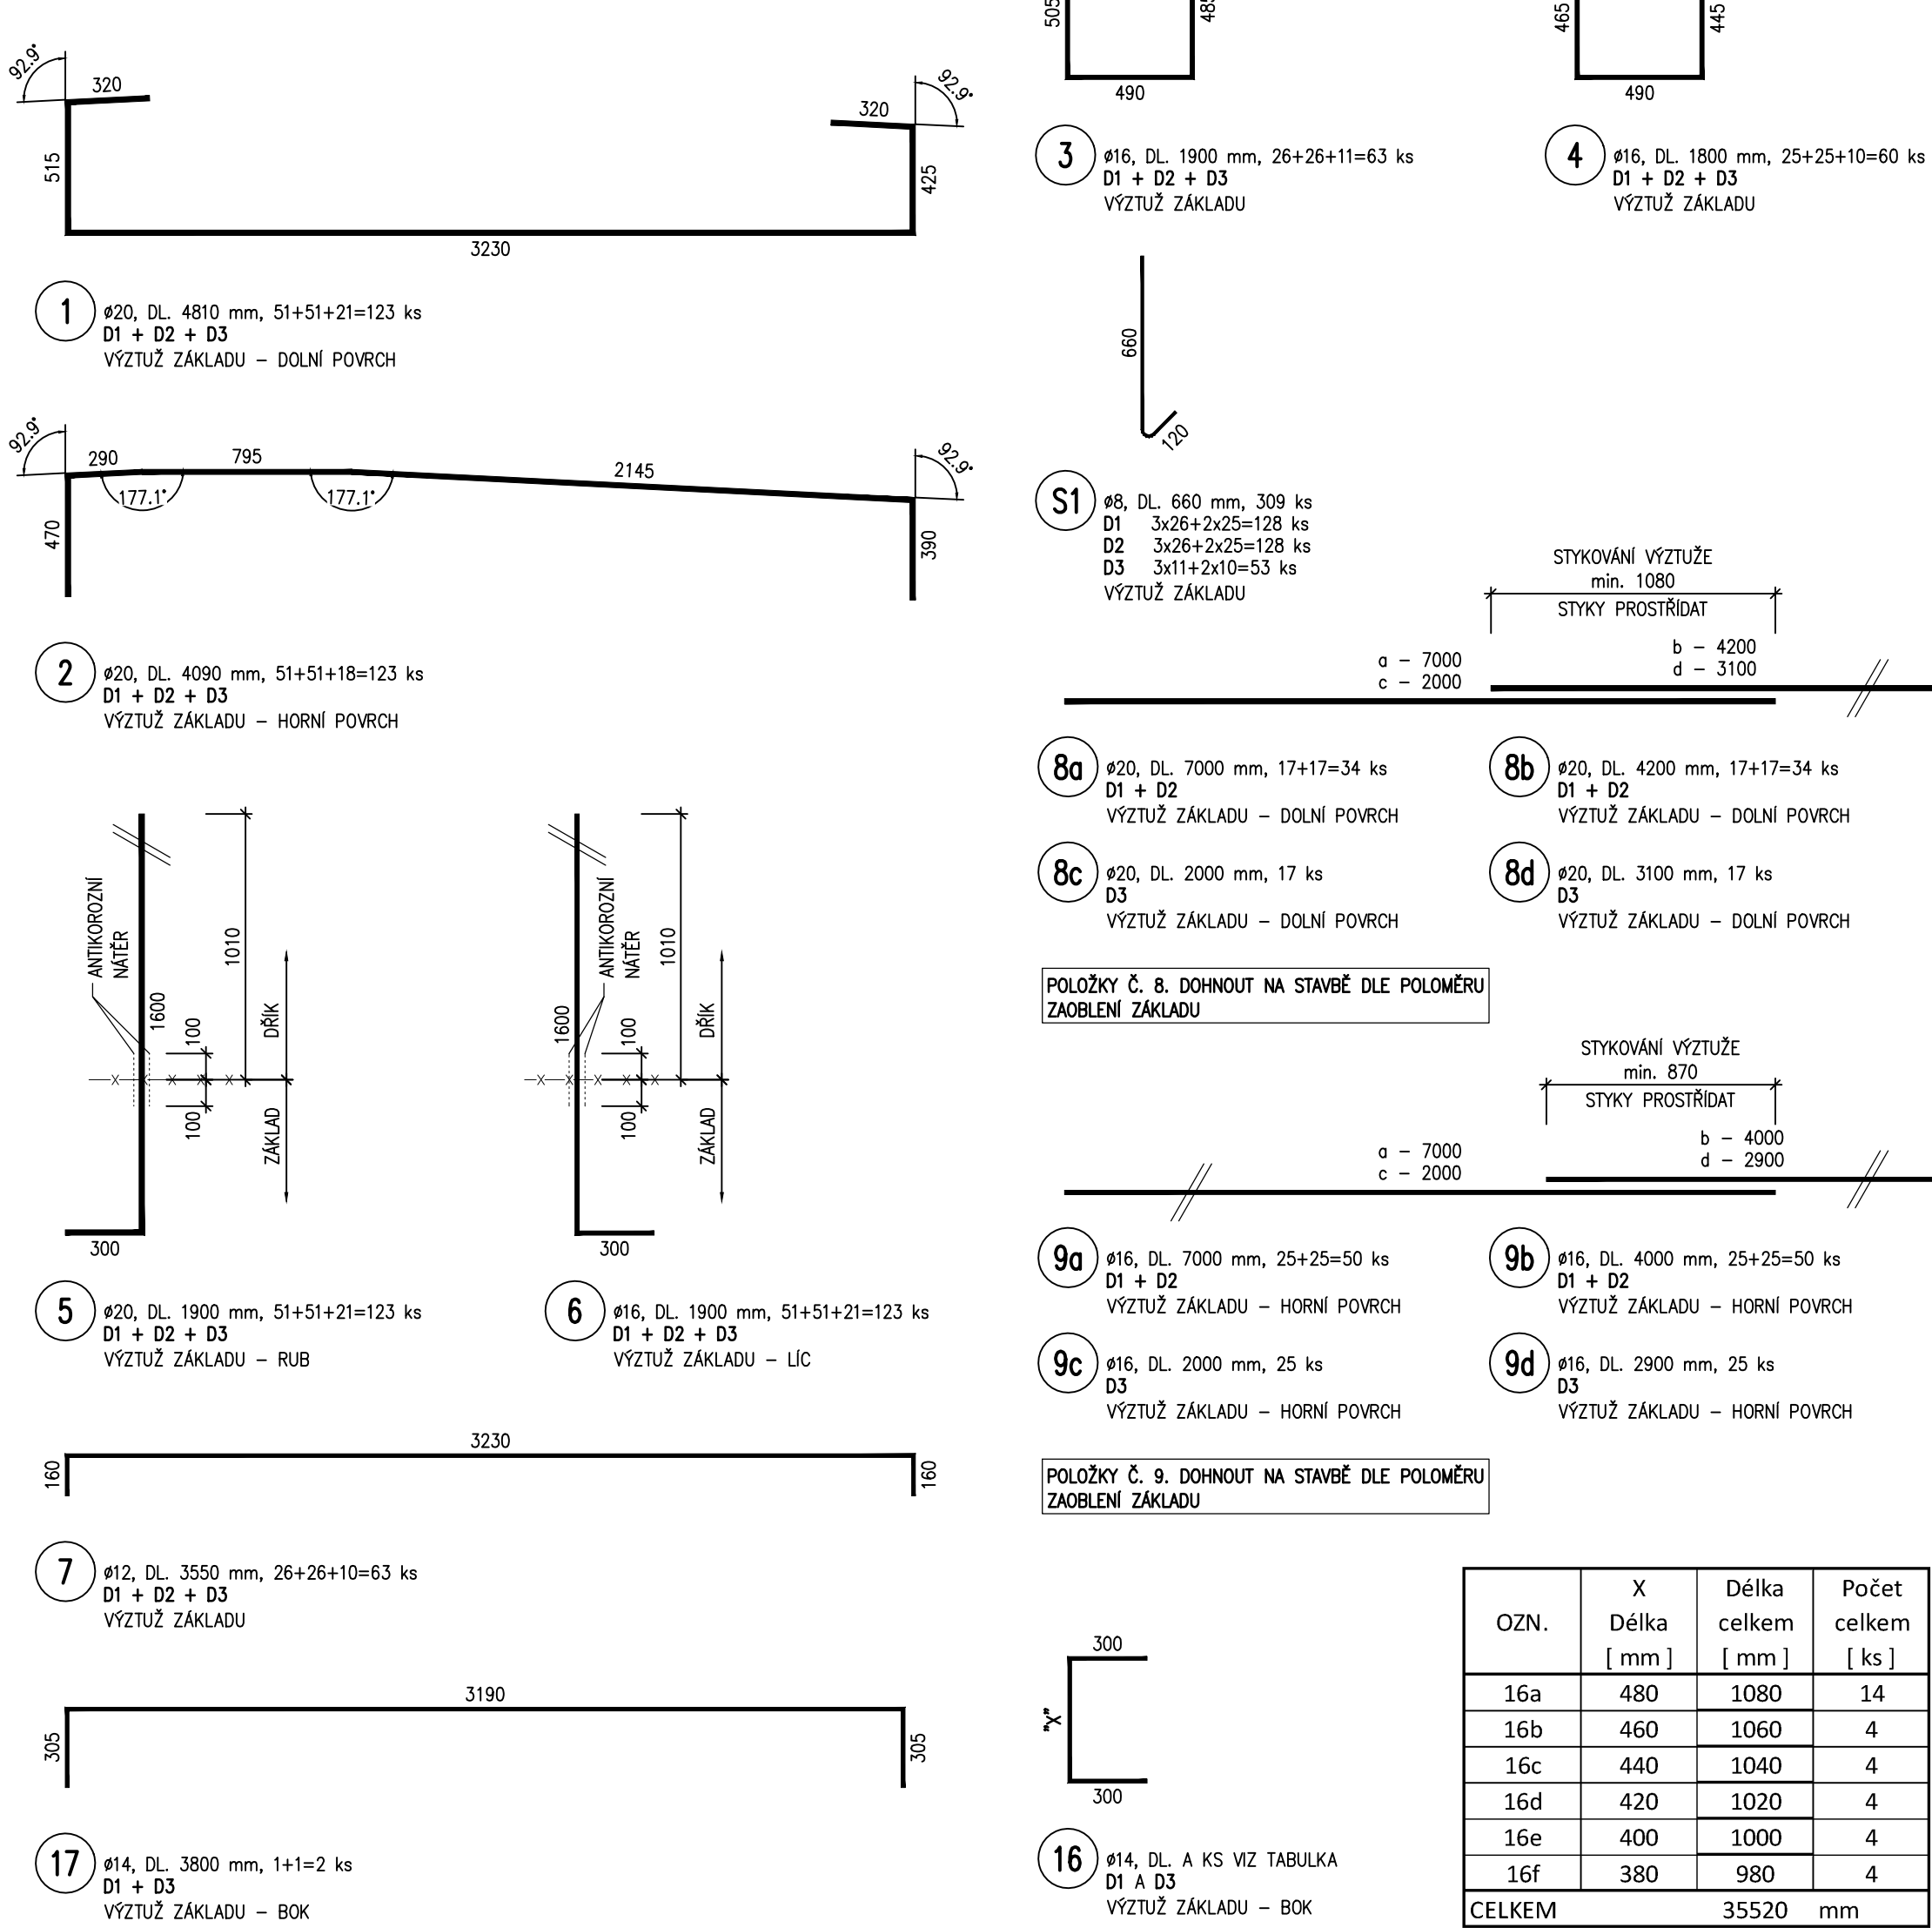

VÝTAH VÝZTUŽE - DŘÍK 1:25

VÝZTUŽ KÓTOVÁNA NA VNĚJŠÍ OBRYŠ


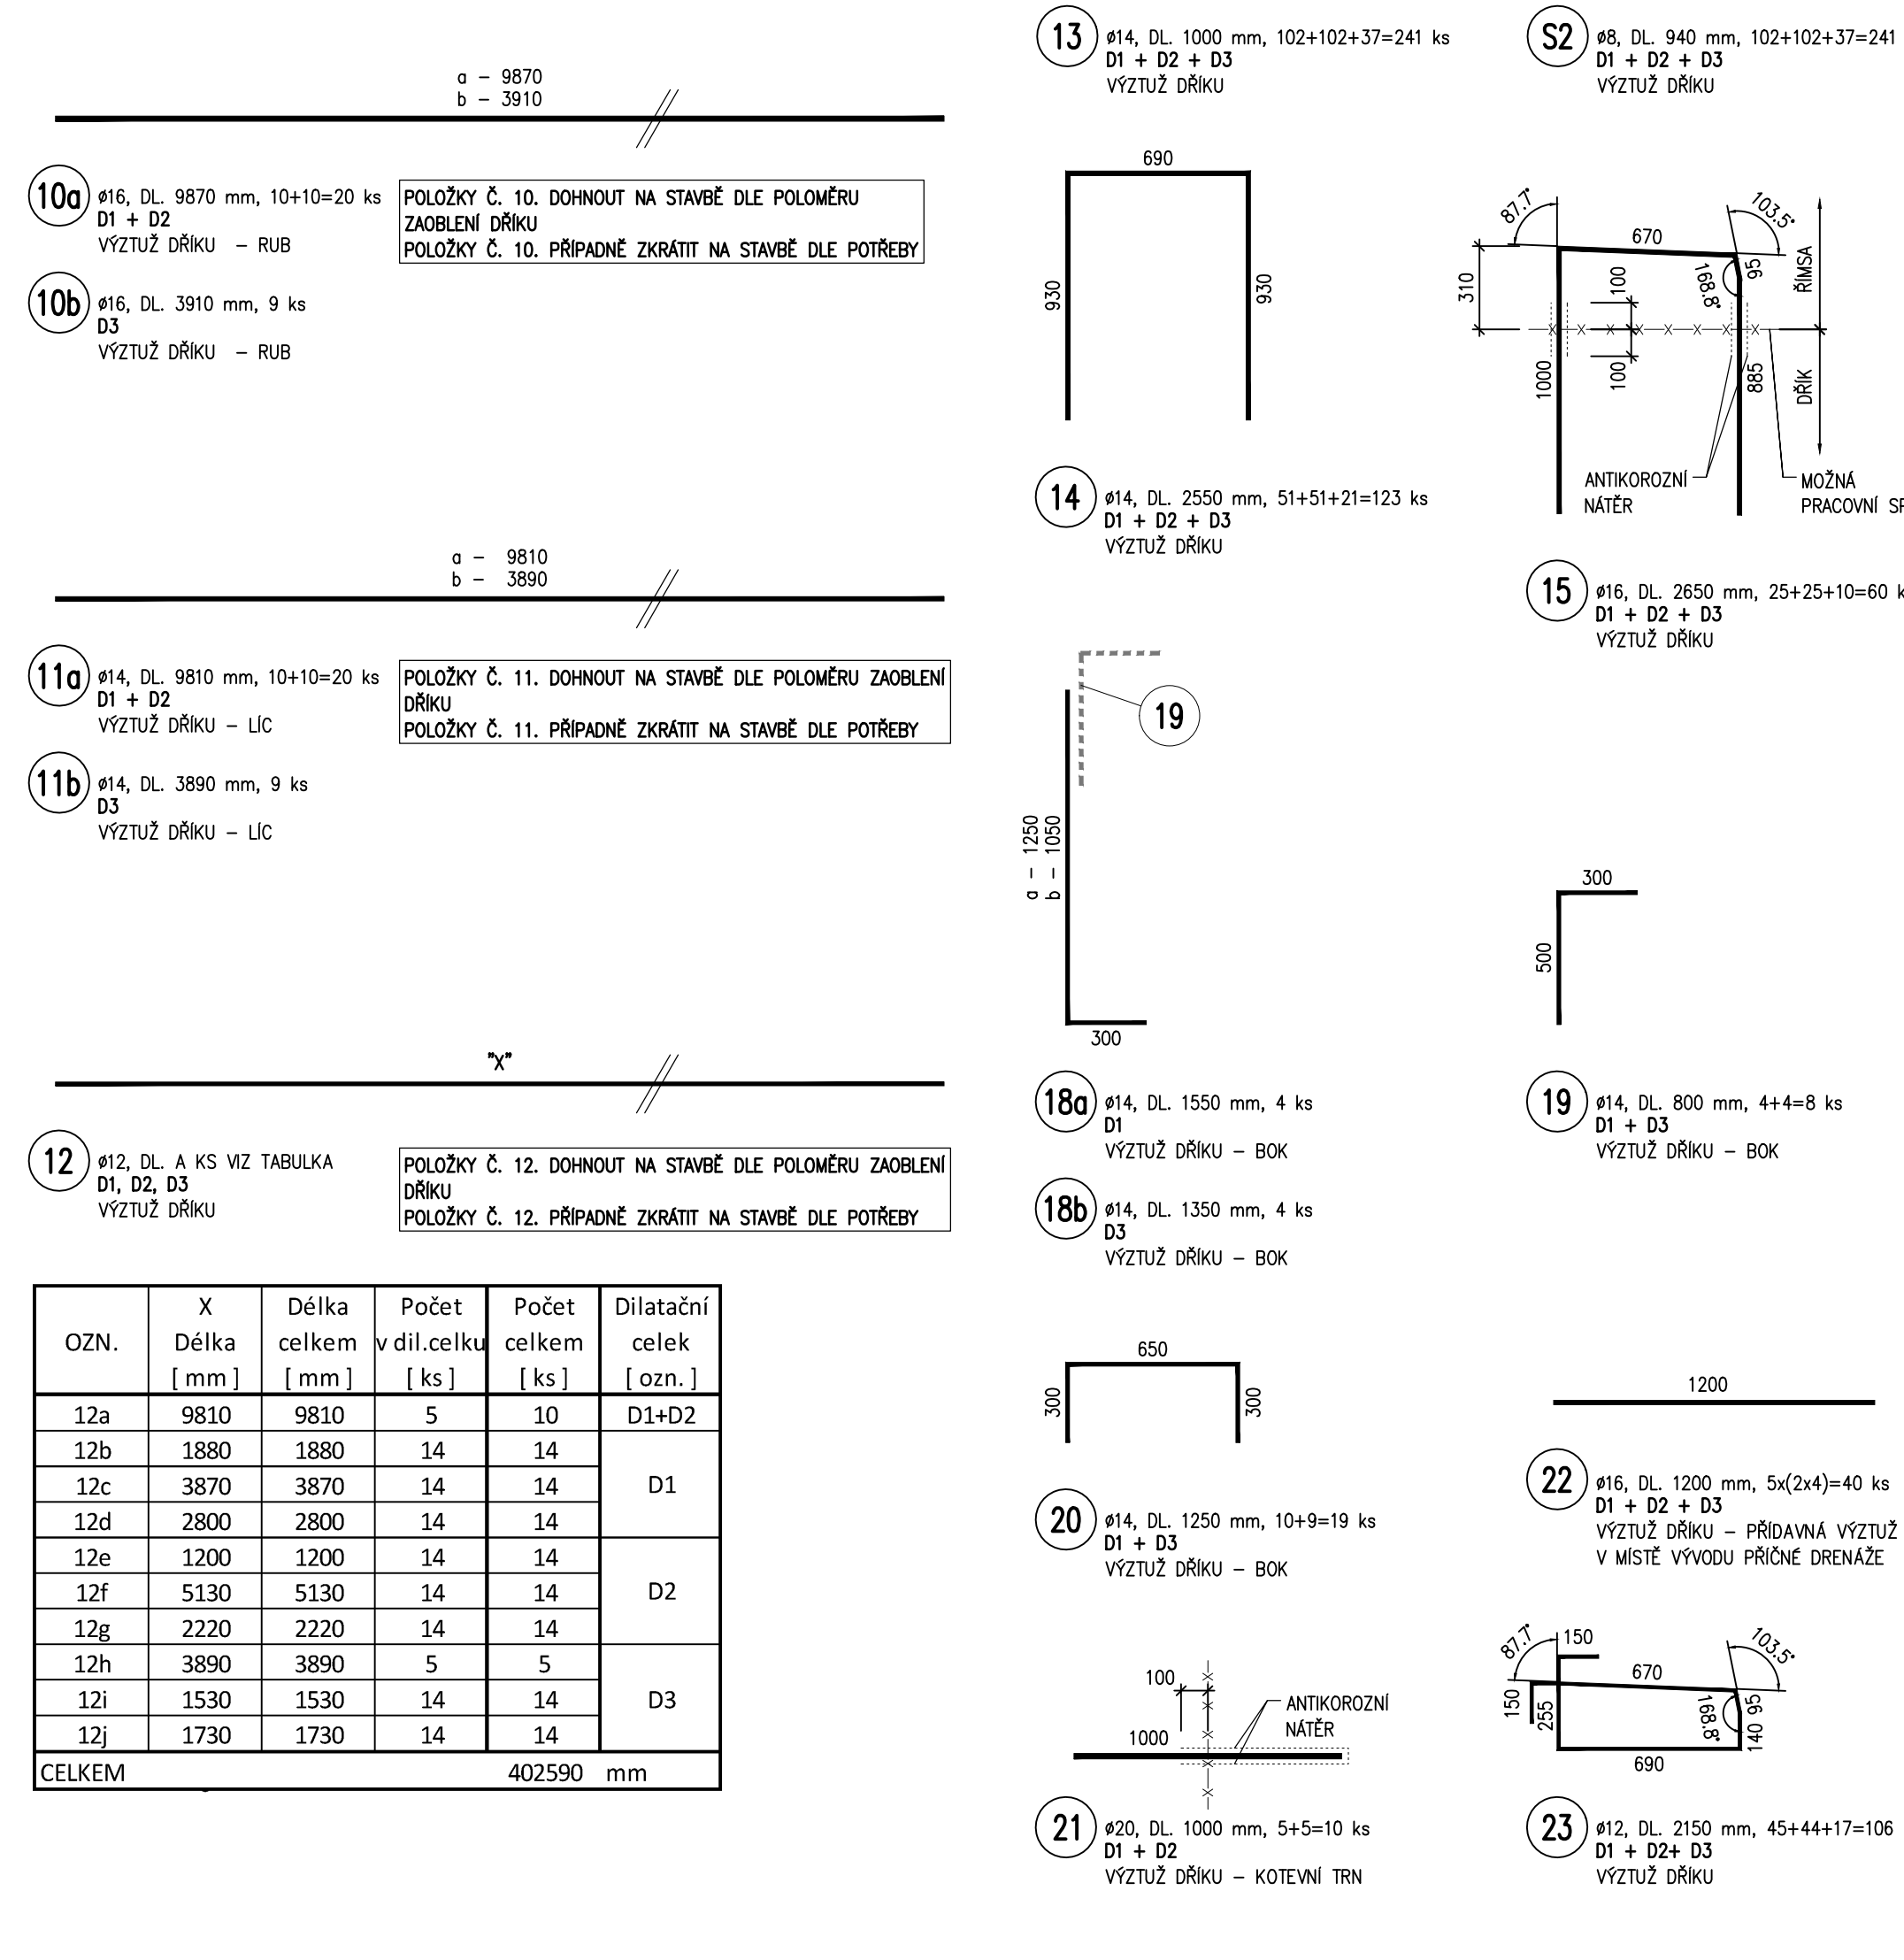


SCHÉMA VÝZTUŽE 1:25


POLOŽKA Č. 13, S2

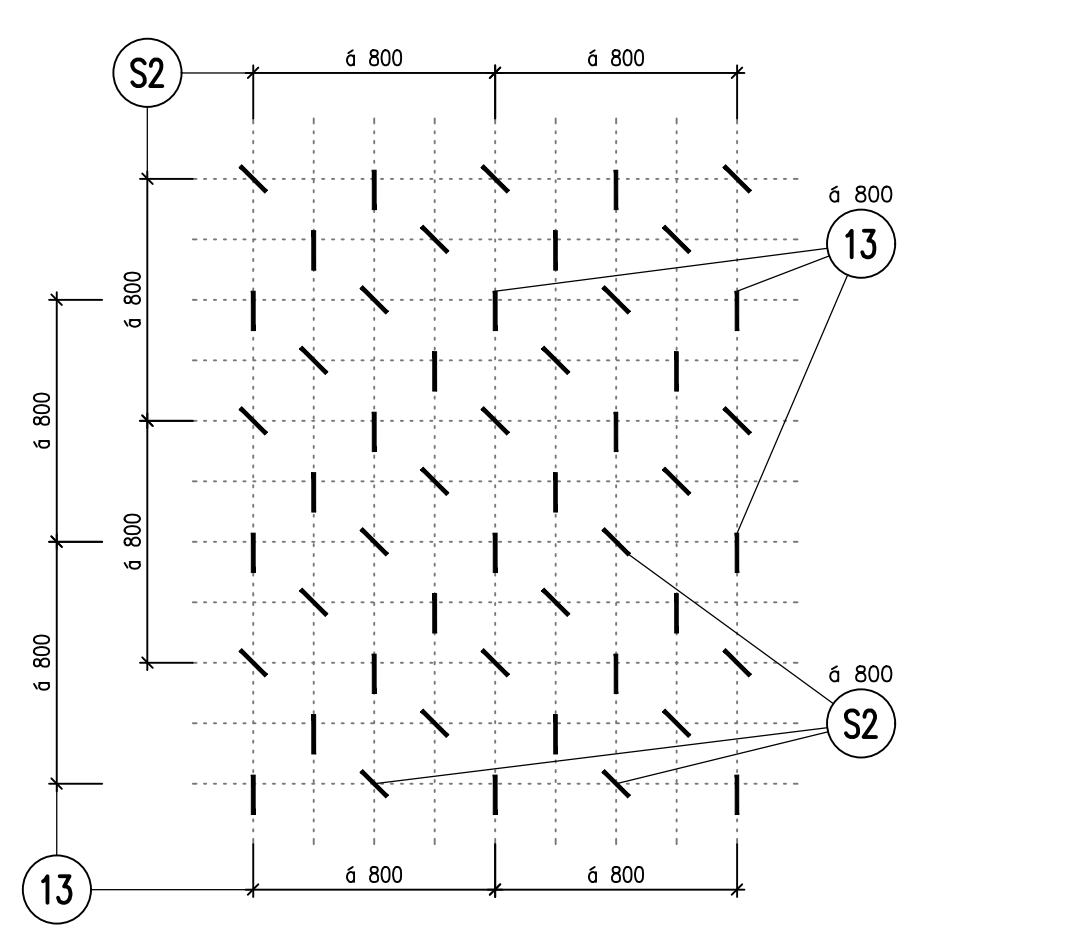

STAVEBNÍ MATERIÁLY

BETONY BUDOU PŘEVEDENY DLE ČSN EN 206	
KONSTRUKČNÍ BETONY:	
ZB ZÁKLAD	C30/37
ZB DŘÍK	C30/37
OSTATNÍ BETONY:	
PODKLADNÍ BETON	C12/15
BETONÁŘSKÁ VÝZTUŽ:	
OCEĽ	B500B

NEJMENŠÍ PRŮMĚR TRNU d, PRO OHÝBÁNÍ DLE ČSN EN 1992-1-1

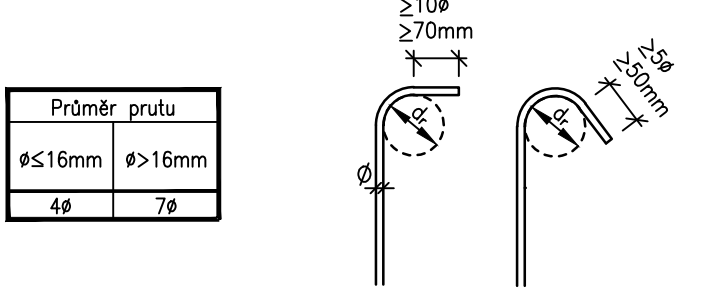

NOMINÁLNÍ KRYTÍ ZÁKLADŮ STĚNY 60 mm
MINIMÁLNÍ KRYTÍ ZÁKLADŮ STĚNY 50 mm
NOMINÁLNÍ KRYTÍ DŘÍKŮ STĚNY 55 mm
MINIMÁLNÍ KRYTÍ DŘÍKŮ STĚNY 45 mm

POZNÁMKY

- ZA OČELEM DOKONALÉHO PROBETONOVÁNÍ KONSTRUKCE NENÍ PŘÍPUSTNÉ, ABY MEZERA MEZI SOUBĚŽNÝMI POLOŽKAMI BYLA MENŠÍ NEŽ 35 mm.
- PRO PŘÍPADNÉ SVAŘOVÁNÍ VÝZTUŽE PLATÍ TP 193

PŘEDKONCEPT

Název stavby		OŠLO OBJEKTU	
II/101 Dolní Břežany - Zbraslav		SO 251.2	
Objednatel stavby		Krajská správa a údržba silnic Středočeského kraje, příspěvková organizace Zborovská 611/1, 150 21 Praha 5-Smíchov	
Autorský dozor		GeoTec-GS, a.s. Chmelová 2920/6, 106 00 Praha 10	
Technický dozor investora		TES + SGS + SGG TES Consulting, s.r.o. V Olšanské 2300/75, 100 00 Praha 10-Strašnice	
Zhotovitel stavby		M-SILNICE a.s. Husova 1697, 530 03 Pardubice www.msilnice.cz	
Koordinační RDS		M - PROJEKCE s. r. o. Restova 956/13, 500 02 Hradec Králové www.m-projeke.cz	
Souřadnicový systém: S-JTSK		Výškový systém: Bpv	
Zpracovatel stavebního objektu/části:		Projektční kancelář PRIS spol. s r. o. Osova 171/20, 625 00 Brno-Starý Lískovec www.pris.cz	
Výpracoval:		Hlavní inženýr projektu:	
Odpovědný projektant:		Kontroloval:	
Číslo zakázky:		Datum:	
Objekt/část:		Měřítko:	
SO 251.2 - OPĚRNÉ ZDI ZED č. 8		Stupeň: S RDS	
Příloha:		Číslo přílohy:	
VÝZTUŽ OPĚRNÉ ZDI		106_VOZ	