


MIKROPILOTY

PŘÍČNÝ ŘEZ P1-P1 km 1,520 000 1:25

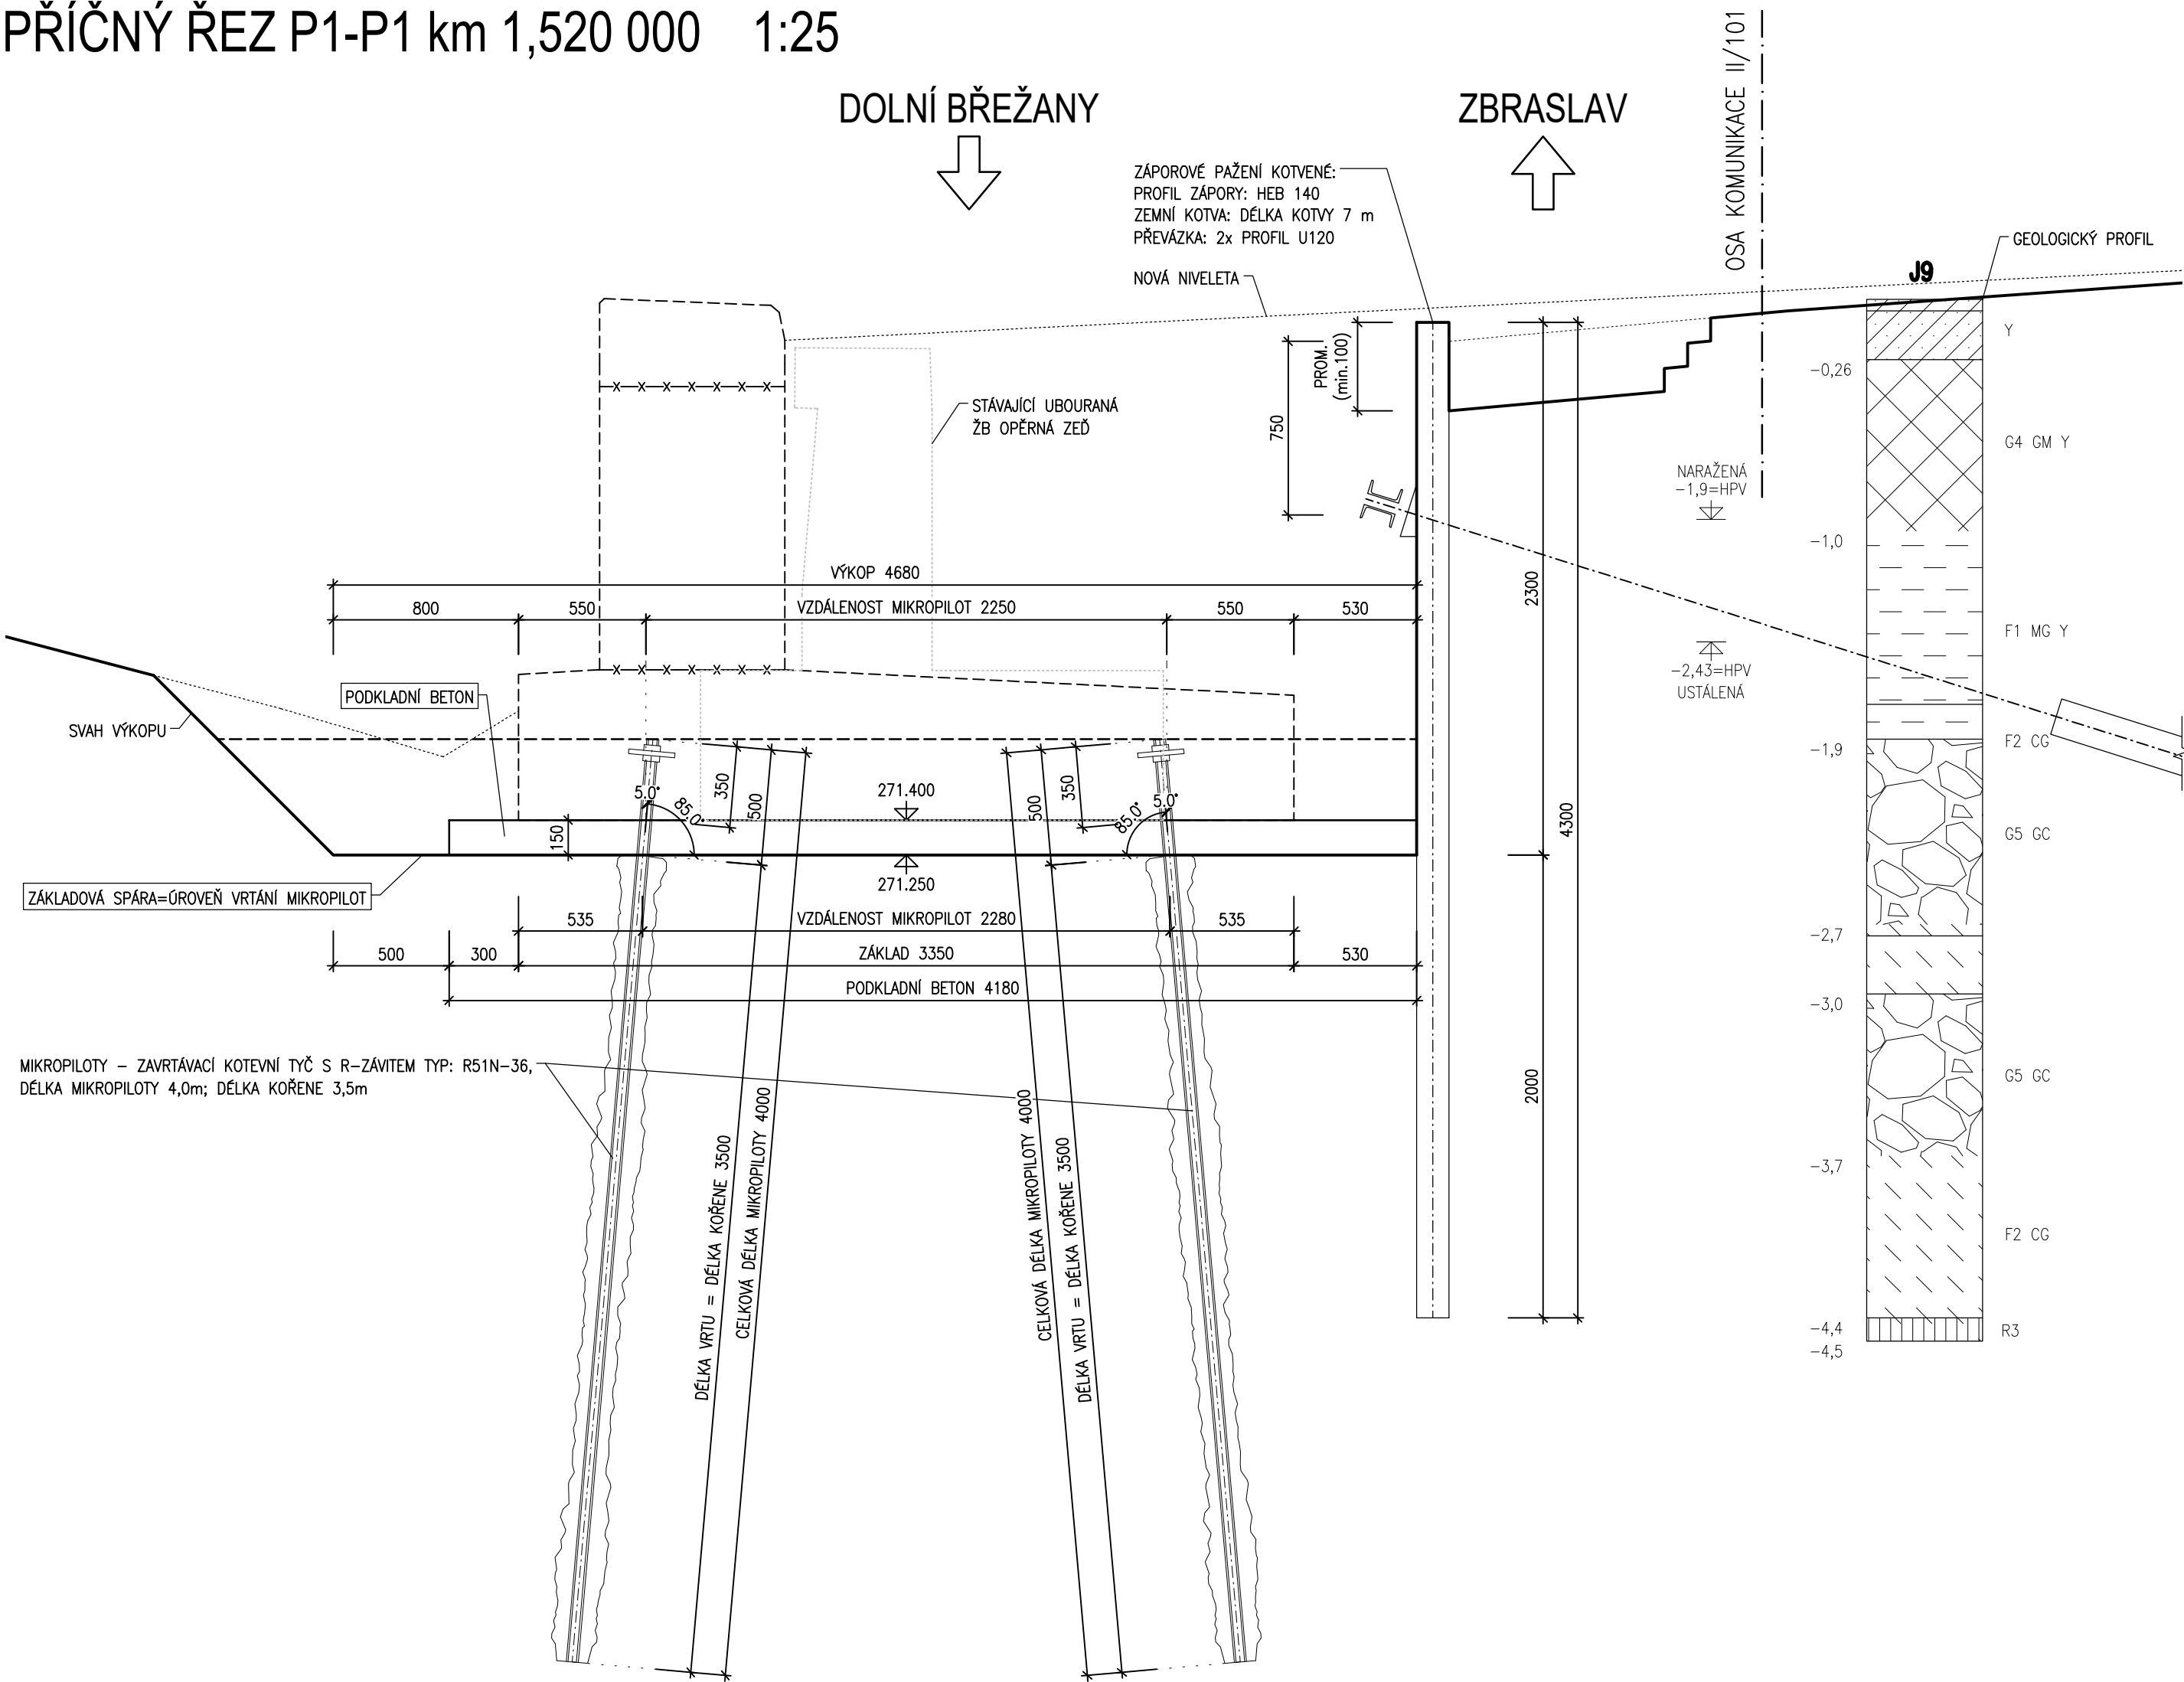

VÝKAZ MATERIÁLU

MIKROPILOTY OPĚRNÁ ZEĎ 08						
VÝKAZ MATERIÁLU						
OZN.	POPIS	DĚLKA [m]	HMOTNOST [kg/m]	POČET [ks]	DĚLKA CELKEM [m]	HMOTNOST [kg]
1	TYČ Ø51mm	4.00	7.7	1	4.000	30.80
3	PLECH 200/200,TL. 20mm	-	6.28	1	-	6.28
HMOTNOST CELKEM ... PRO 1 MIKROPILOTU DL. 4.0 m						37.08 kg
HMOTNOST CELKEM ... PRO VŠECH 40 MIKROPILOT						1483.20 kg

POZNÁMKY:
- JE VYKÁZÁNA CELKOVÁ DÉLKA TYČE 6,0 m VČETNĚ PŘESAHU 0,35 m DO ZÁKLADU

VÝKAZ MIKROPILOT

VÝKAZ VRTŮ PRO MIKROPILOTY			
OZN.	DĚLKA VRTU CELKEM [m]	POČET VRTŮ / [ks]	DĚLKA CELKEM [m]
ŠÍKMÉ	4.00	40	160.00
CELKEM DÉLKA VRTŮ CELKEM			160.00 m

VÝKAZ MIKROPILOT	
ŠÍKMÉ	40
CELKEM	40

MATERIÁL

CEMENTOVÁ SUSPENZE INJEKTAŽNÍ CEM 32,5R, C25/30


POZNÁMKY

- ZHOTOVITEL JE POVINEN PRO VŠECHNY ZEMĚMĚŘICKÉ PRÁCE POSTUPOVAT DLE TKP KAP. 1, ODS. 1.6.3.
- PRO MIKROPILOTY BUDOU POUŽITY INJEKČNÍ ZAVRTÁVACÍ KOTEVNÍ TYČE SDA, TYP R51N-36
- MIKROPILOTY JSOU VYTÝČENY V ÚROVNI ZÁKLADOVÉ SPÁRY, TZN. V DOLNÍ ÚROVNI PODKLADNÍHO BETONU.
- PRO PÍPADNÉ SPOJOVÁNÍ BUDOU POUŽITI ORIGINALNÍ SPOJNÍKY
- SAMOZAVRTÁVACÍ TYČ BUDE UKONČENÁ DESKOU 200x200x20 mm A Z OBOU STRAN STAŽENA MATICEMI
- VŠECHNY MIKROPILOTY JSOU ŠÍKMÉ 5°
- PROVÁDĚNÍ MIKROPILOT MUSÍ BÝT V SOULADU S ČSN EN 14199.
- CEMENTOVÁ SUSPENZE MUSÍ MÍT FINÁLNÍ PEVNOST MIN. C25/30
- PRO ČERPÁNÍ VODY ZE DNA ZÁKLADOVÉ SPÁRY BUDOU ZBUDOVÁNY JÍMKY.
- V MÍSTĚ NOVĚ NAVRŽENÉ ZDI BYLA ZJIŠTĚNA STÁVAJÍCÍ ŽELEZOBETONOVÁ OPĚRNÁ ZEĎ OPROTI ZADÁVACÍ DOKUMENTACI, KDE BYLA UVEDENÁ ZEĎ GABIONOVÁ

SEZNAM SOUŘADNIC


Vytýčení mikropilot										SO 251.2_08
Opěrná zeď č. 8 - mikropiloty										
RÁDA BODŮ 08										
ČÁST	Označ. bodu	Číslo bodu	SOURADNICE		VÝŠKA HLAVY MIKROPILOTY	CELKOVÁ DÉLKA MIKROPILOTY	VÝŠKA PATY MIKROPILOTY	VÝŠKA V ÚROVNI ZAKLADOVÉ SPÁRY	ODKLON	Poznámky
			PODKLADNÍ BETON							
			Y [m]	X [m]						
LÍCOVÁ STRANA	101	251 2 08 101	744015.485	1056774.282	271.750	4,00	267,77	271,250	5	DILATAČNÍ CELEK D1
	102	251 2 08 102	744016.571	1056773.802	271.750	4,00	267,77	271,250	5	
	103	251 2 08 103	744017.663	1056773.335	271.750	4,00	267,77	271,250	5	
	104	251 2 08 104	744018.759	1056772.880	271.750	4,00	267,77	271,250	5	
	105	251 2 08 105	744019.861	1056772.437	271.750	4,00	267,77	271,250	5	
	106	251 2 08 106	744020.967	1056772.007	271.750	4,00	267,77	271,250	5	
	107	251 2 08 107	744022.078	1056771.590	271.750	4,00	267,77	271,250	5	
	108	251 2 08 108	744023.194	1056771.185	271.750	4,00	267,77	271,250	5	
	109	251 2 08 109	744024.689	1056770.665	271.350	4,00	267,37	270,850	5	DILATAČNÍ CELEK D2
	110	251 2 08 110	744025.815	1056770.289	271.350	4,00	267,37	270,850	5	
	111	251 2 08 111	744026.946	1056769.927	271.350	4,00	267,37	270,850	5	
	112	251 2 08 112	744028.080	1056769.577	271.350	4,00	267,37	270,850	5	
	113	251 2 08 113	744029.218	1056769.240	271.350	4,00	267,37	270,850	5	
	114	251 2 08 114	744030.360	1056768.916	271.350	4,00	267,37	270,850	5	
	115	251 2 08 115	744031.506	1056768.605	271.350	4,00	267,37	270,850	5	
	116	251 2 08 116	744032.655	1056768.307	271.350	4,00	267,37	270,850	5	
	117	251 2 08 117	744033.904	1056767.999	271.150	4,00	267,17	270,650	5	DILATAČNÍ CELEK D3
	118	251 2 08 118	744034.915	1056767.761	271.150	4,00	267,17	270,650	5	
	119	251 2 08 119	744035.928	1056767.533	271.150	4,00	267,17	270,650	5	
	120	251 2 08 120	744036.944	1056767.316	271.150	4,00	267,17	270,650	5	
RUBOVÁ STRANA	501	251 2 08 501	744014.553	1056772.206	271.750	4,00	267,77	271,250	5	DILATAČNÍ CELEK D1
	502	251 2 08 502	744015.663	1056771.716	271.750	4,00	267,77	271,250	5	
	503	251 2 08 503	744016.777	1056771.238	271.750	4,00	267,77	271,250	5	
	504	251 2 08 504	744017.898	1056770.773	271.750	4,00	267,77	271,250	5	
	505	251 2 08 505	744019.023	1056770.321	271.750	4,00	267,77	271,250	5	
	506	251 2 08 506	744020.154	1056769.882	271.750	4,00	267,77	271,250	5	
	507	251 2 08 507	744021.289	1056769.455	271.750	4,00	267,77	271,250	5	
	508	251 2 08 508	744022.429	1056769.041	271.750	4,00	267,77	271,250	5	
	509	251 2 08 509	744023.956	1056768.510	271.350	4,00	267,37	270,850	5	DILATAČNÍ CELEK D2
	510	251 2 08 510	744025.107	1056768.126	271.350	4,00	267,37	270,850	5	
	511	251 2 08 511	744026.262	1056767.756	271.350	4,00	267,37	270,850	5	
	512	251 2 08 512	744027.421	1056767.398	271.350	4,00	267,37	270,850	5	
	513	251 2 08 513	744028.584	1056767.054	271.350	4,00	267,37	270,850	5	
	514	251 2 08 514	744029.751	1056766.723	271.350	4,00	267,37	270,850	5	
	515	251 2 08 515	744030.921	1056766.405	271.350	4,00	267,37	270,850	5	
	516	251 2 08 516	744032.095	1056766.101	271.350	4,00	267,37	270,850	5	
	517	251 2 08 517	744033.371	1056765.786	271.150	4,00	267,17	270,650	5	DILATAČNÍ CELEK D3
	518	251 2 08 518	744034.404	1056765.543	271.150	4,00	267,17	270,650	5	
	519	251 2 08 519	744035.440	1056765.311	271.150	4,00	267,17	270,650	5	
	520	251 2 08 520	744036.477	1056765.088	271.150	4,00	267,17	270,650	5	

PŮDORYS 1:100

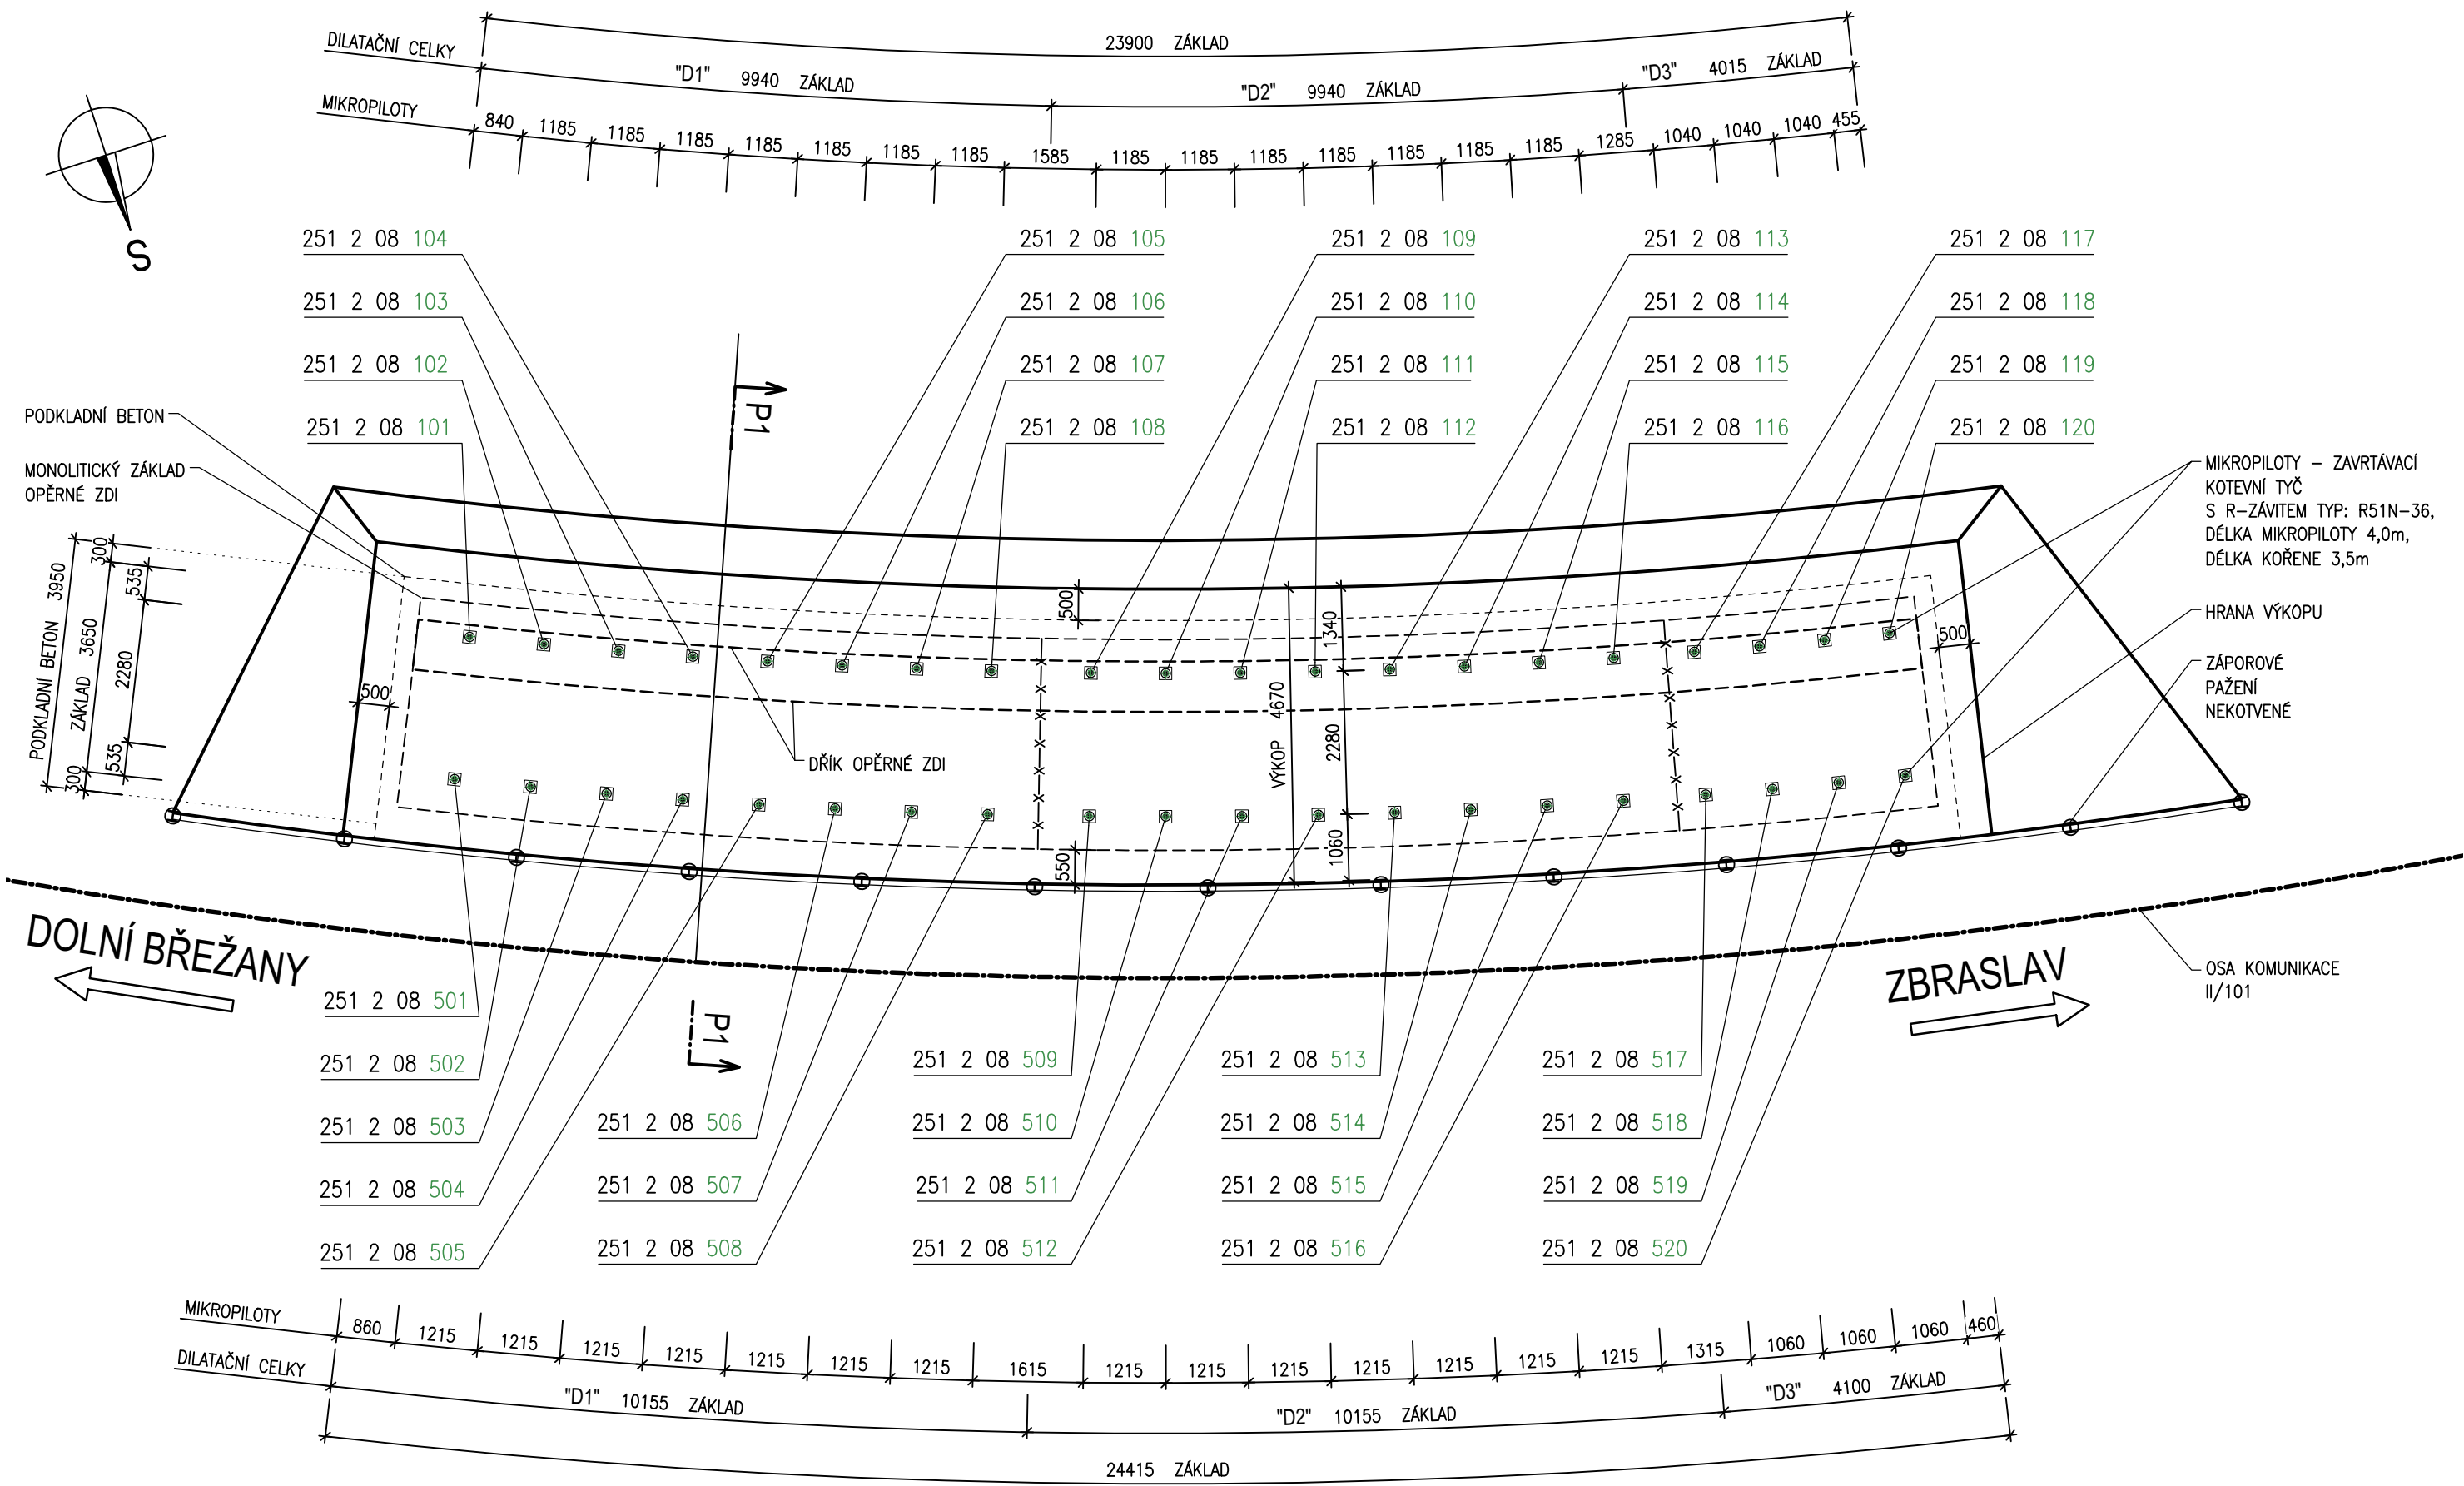


DETAIL UKONČENÍ MIKROPILOTY 1:5

POHLED

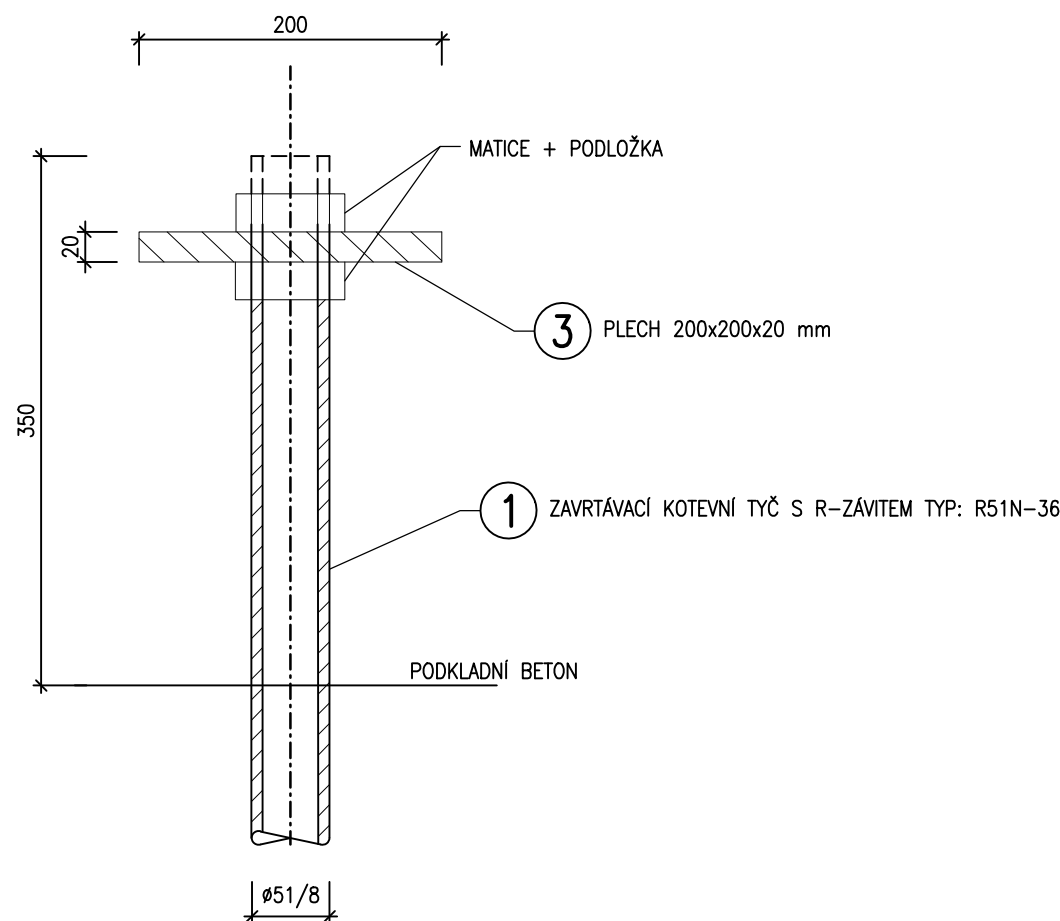

PŮDORYS

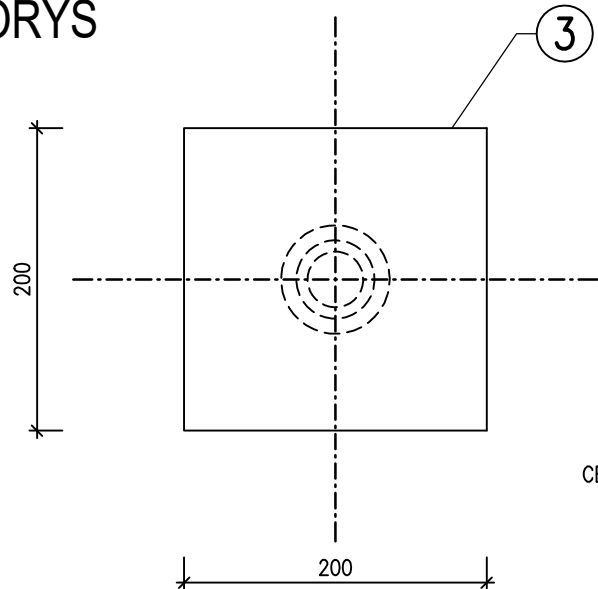

ŘEZ V KOŘENOVÉ ČÁSTI

