


VÝZTUŽ OPĚRNÉ ZDI

PŘÍČNÝ ŘEZ P1-P1 1:25

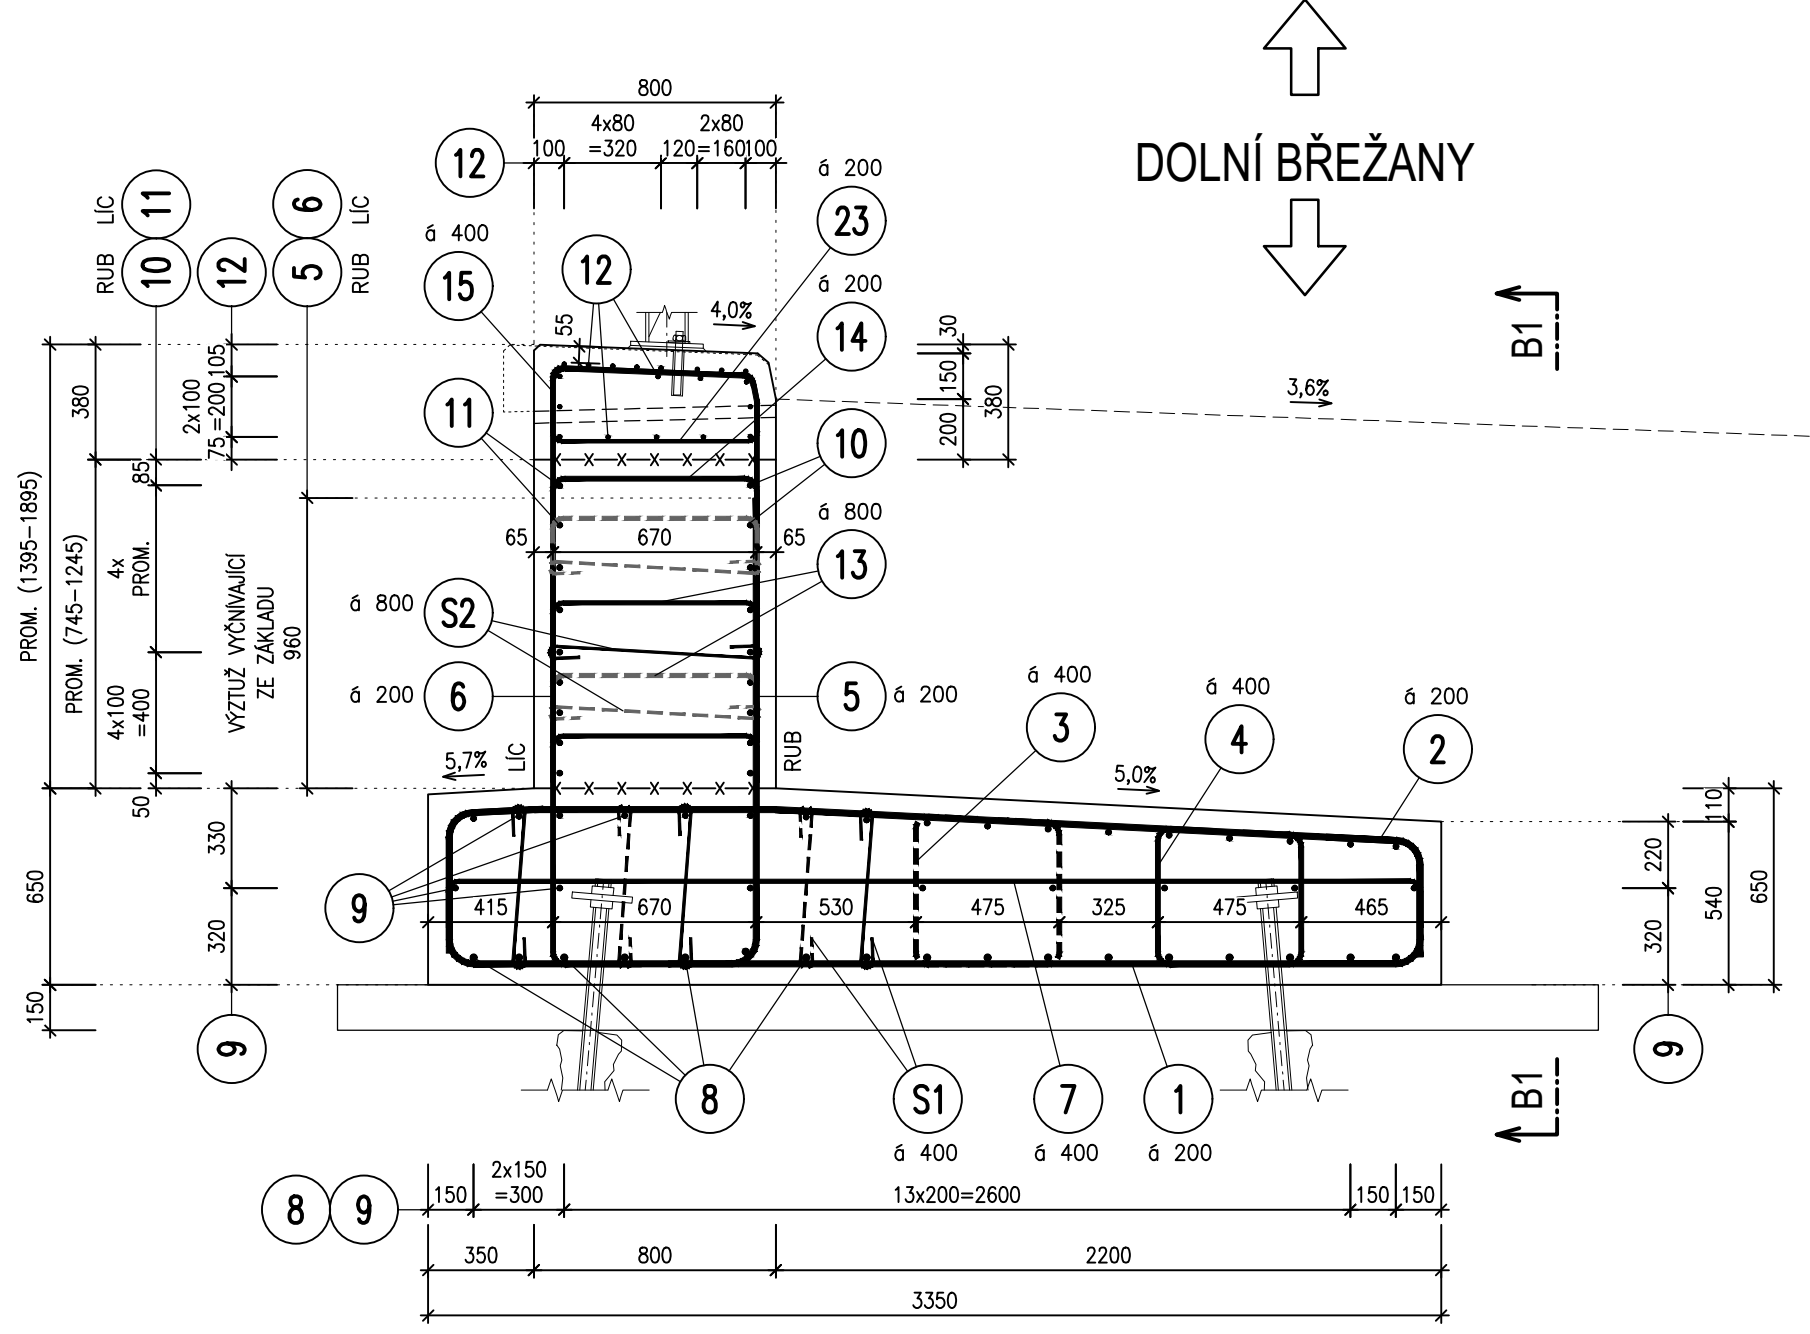

POHLED P2-P2 1:50



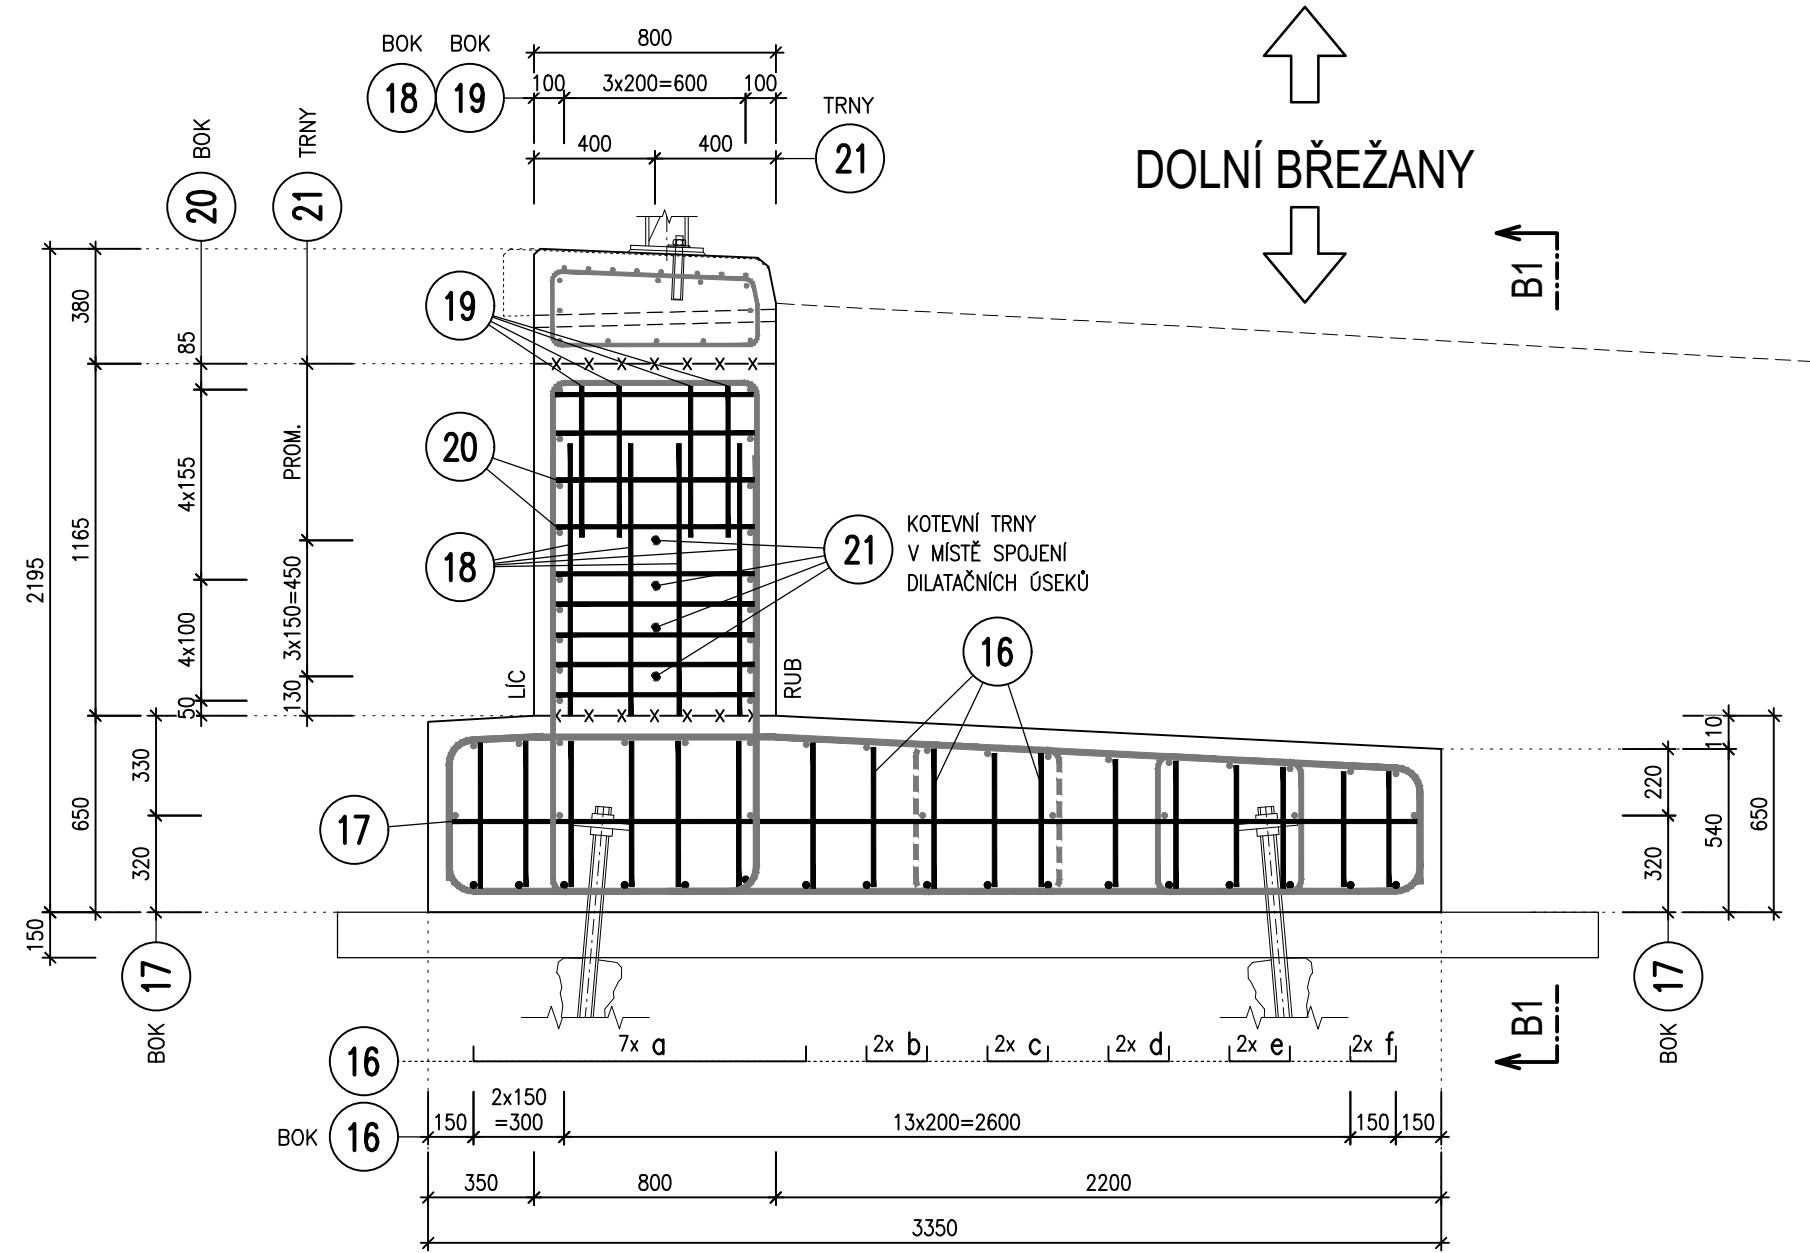



SCHÉMA VÝZTUŽE 1:25

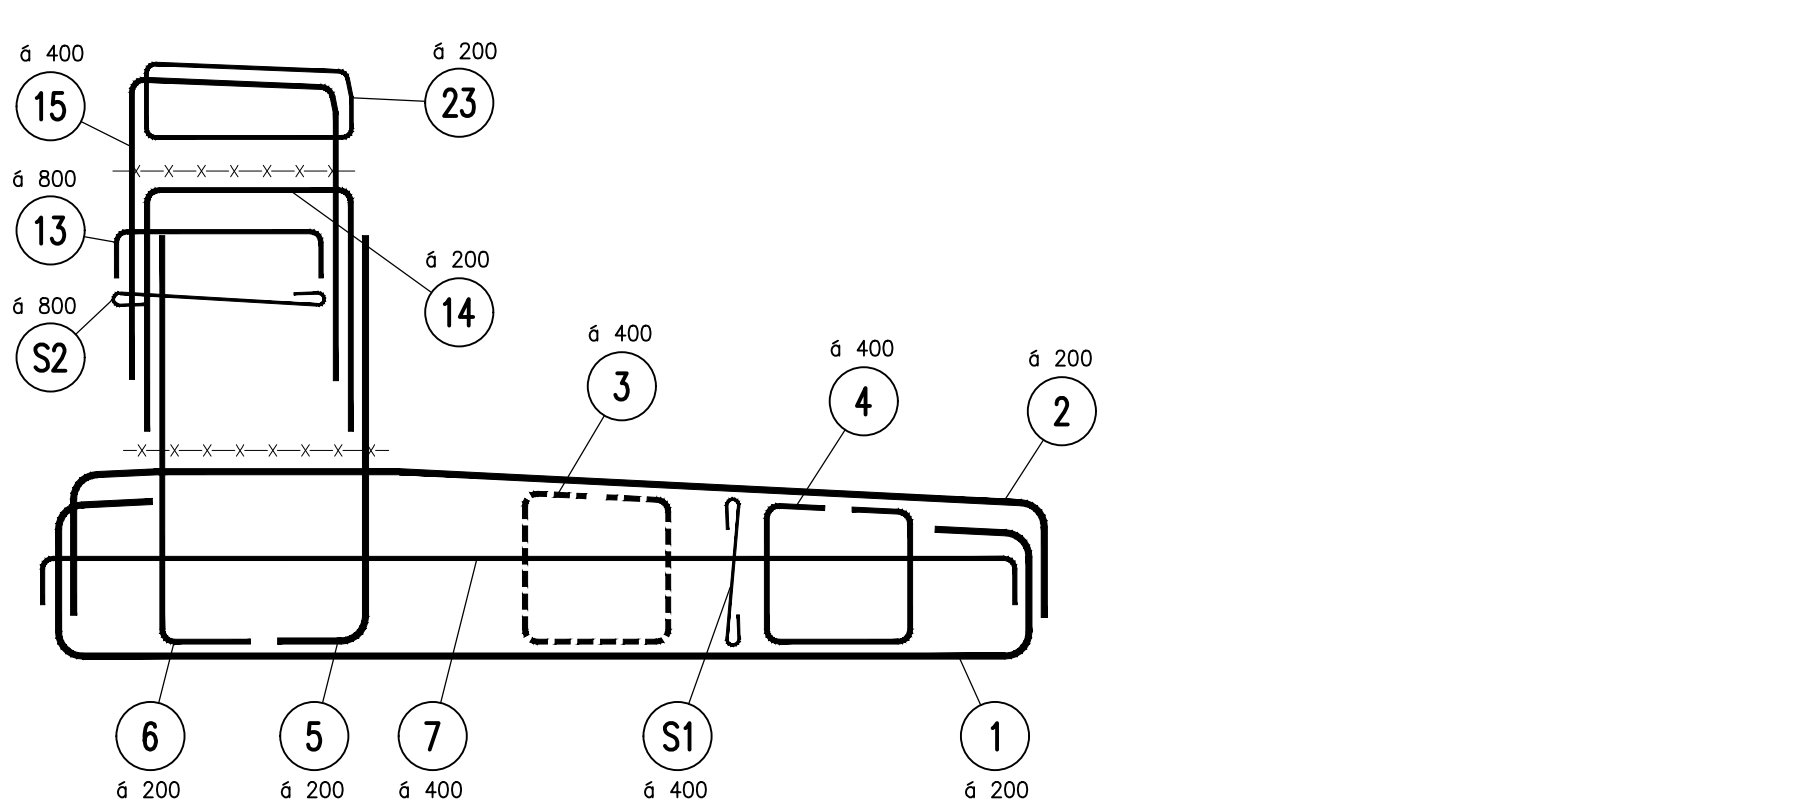


POHLED V LÍCI B1-B1 1:50

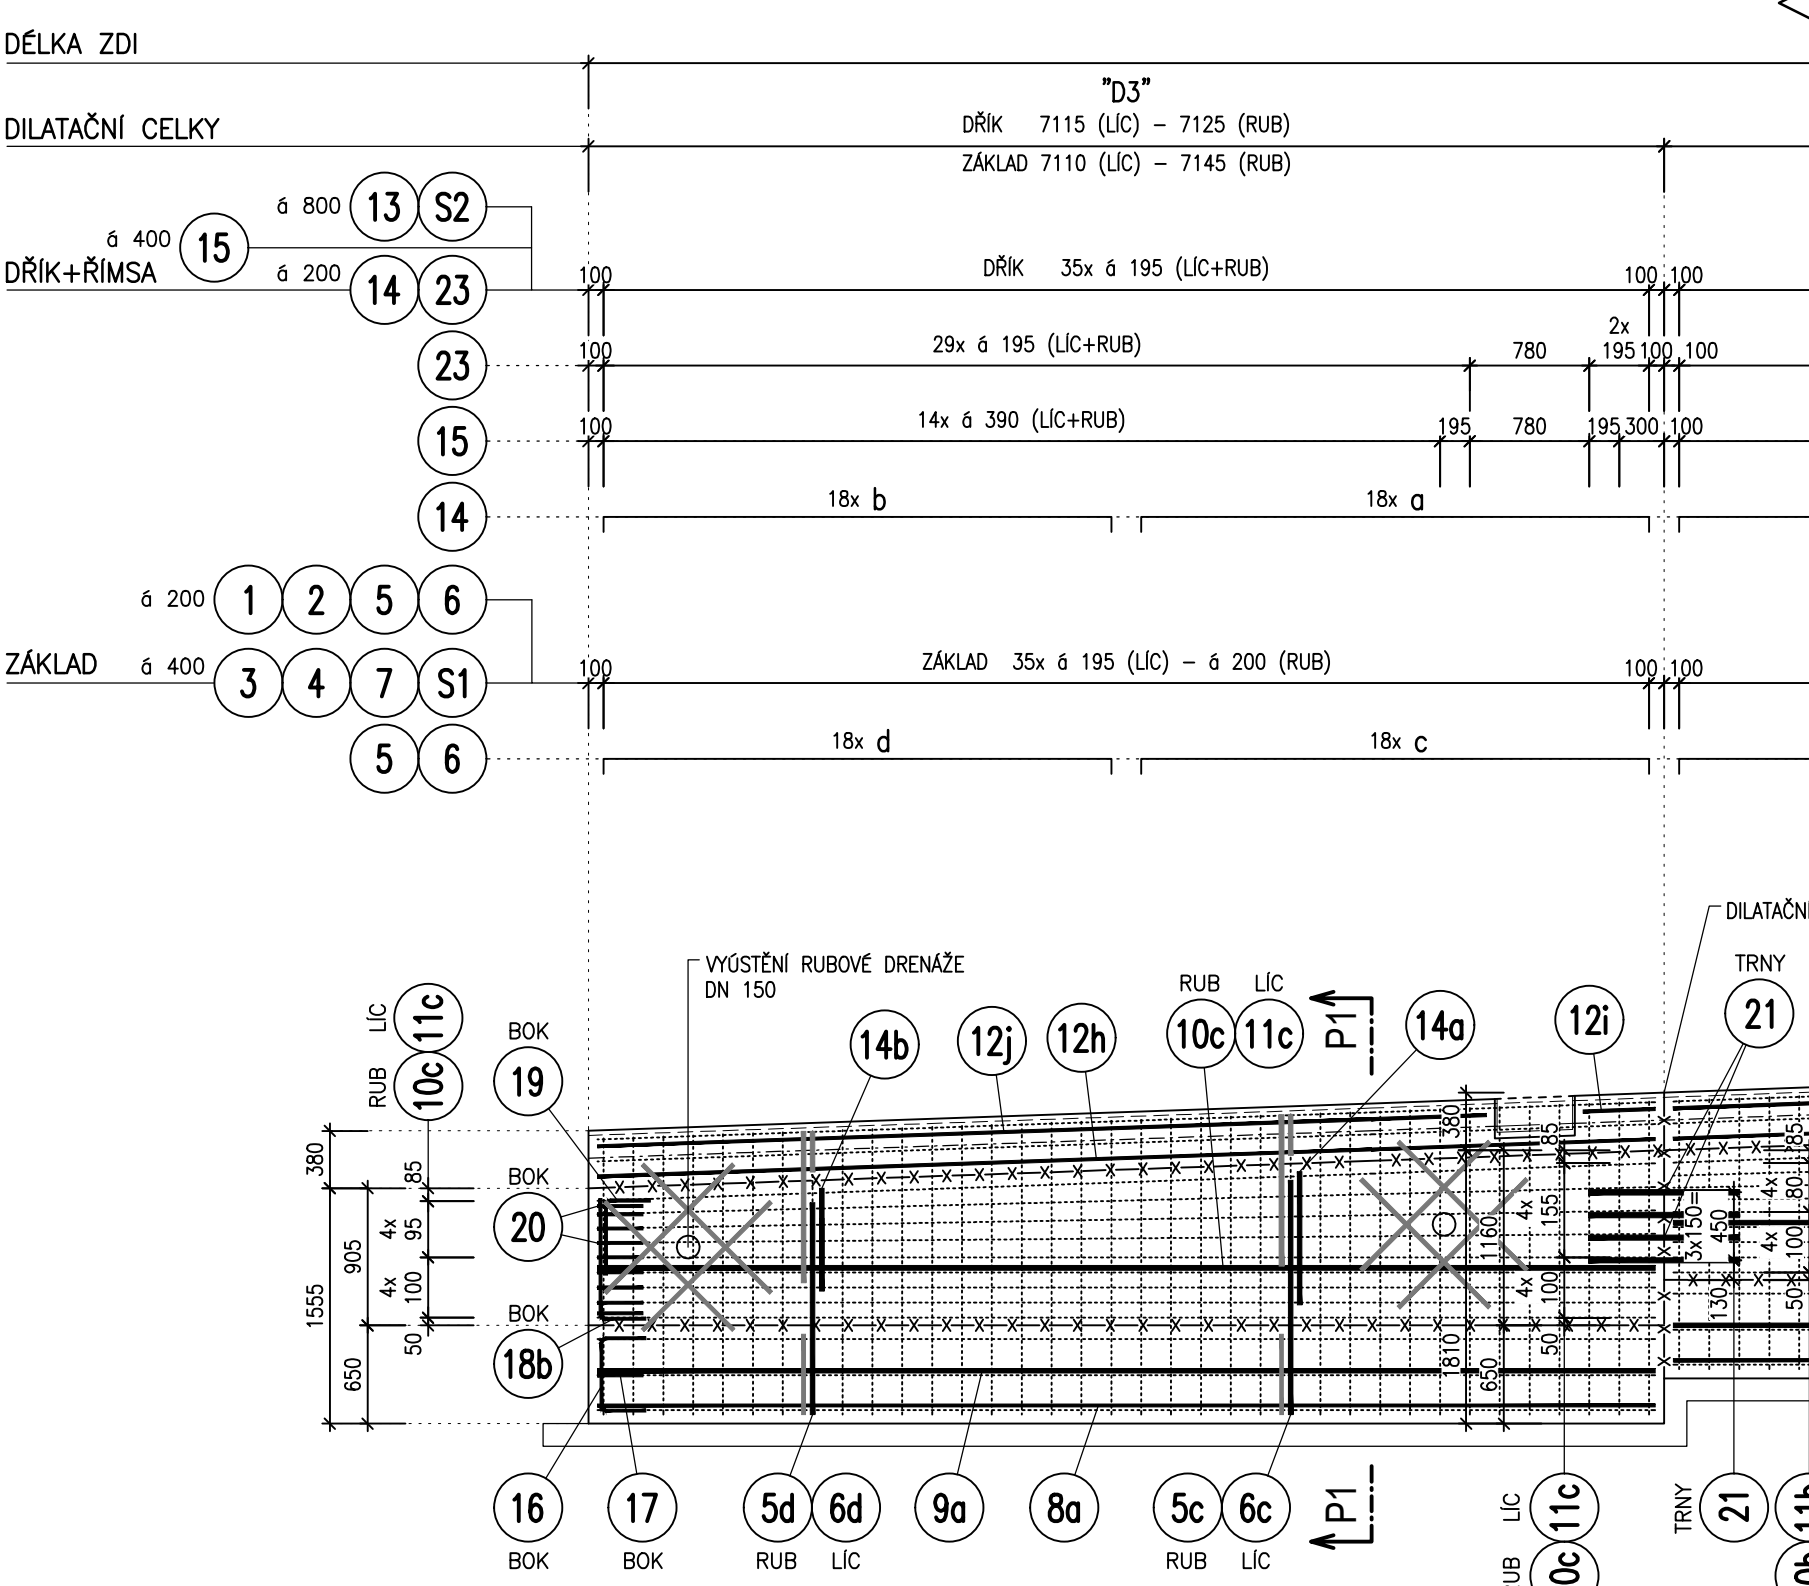


VÝTAH VÝZTUŽE - ZÁKLAD 1:25
VÝZTUŽ KÓTOVÁNA NA VNĚJŠÍ OBRYŠ

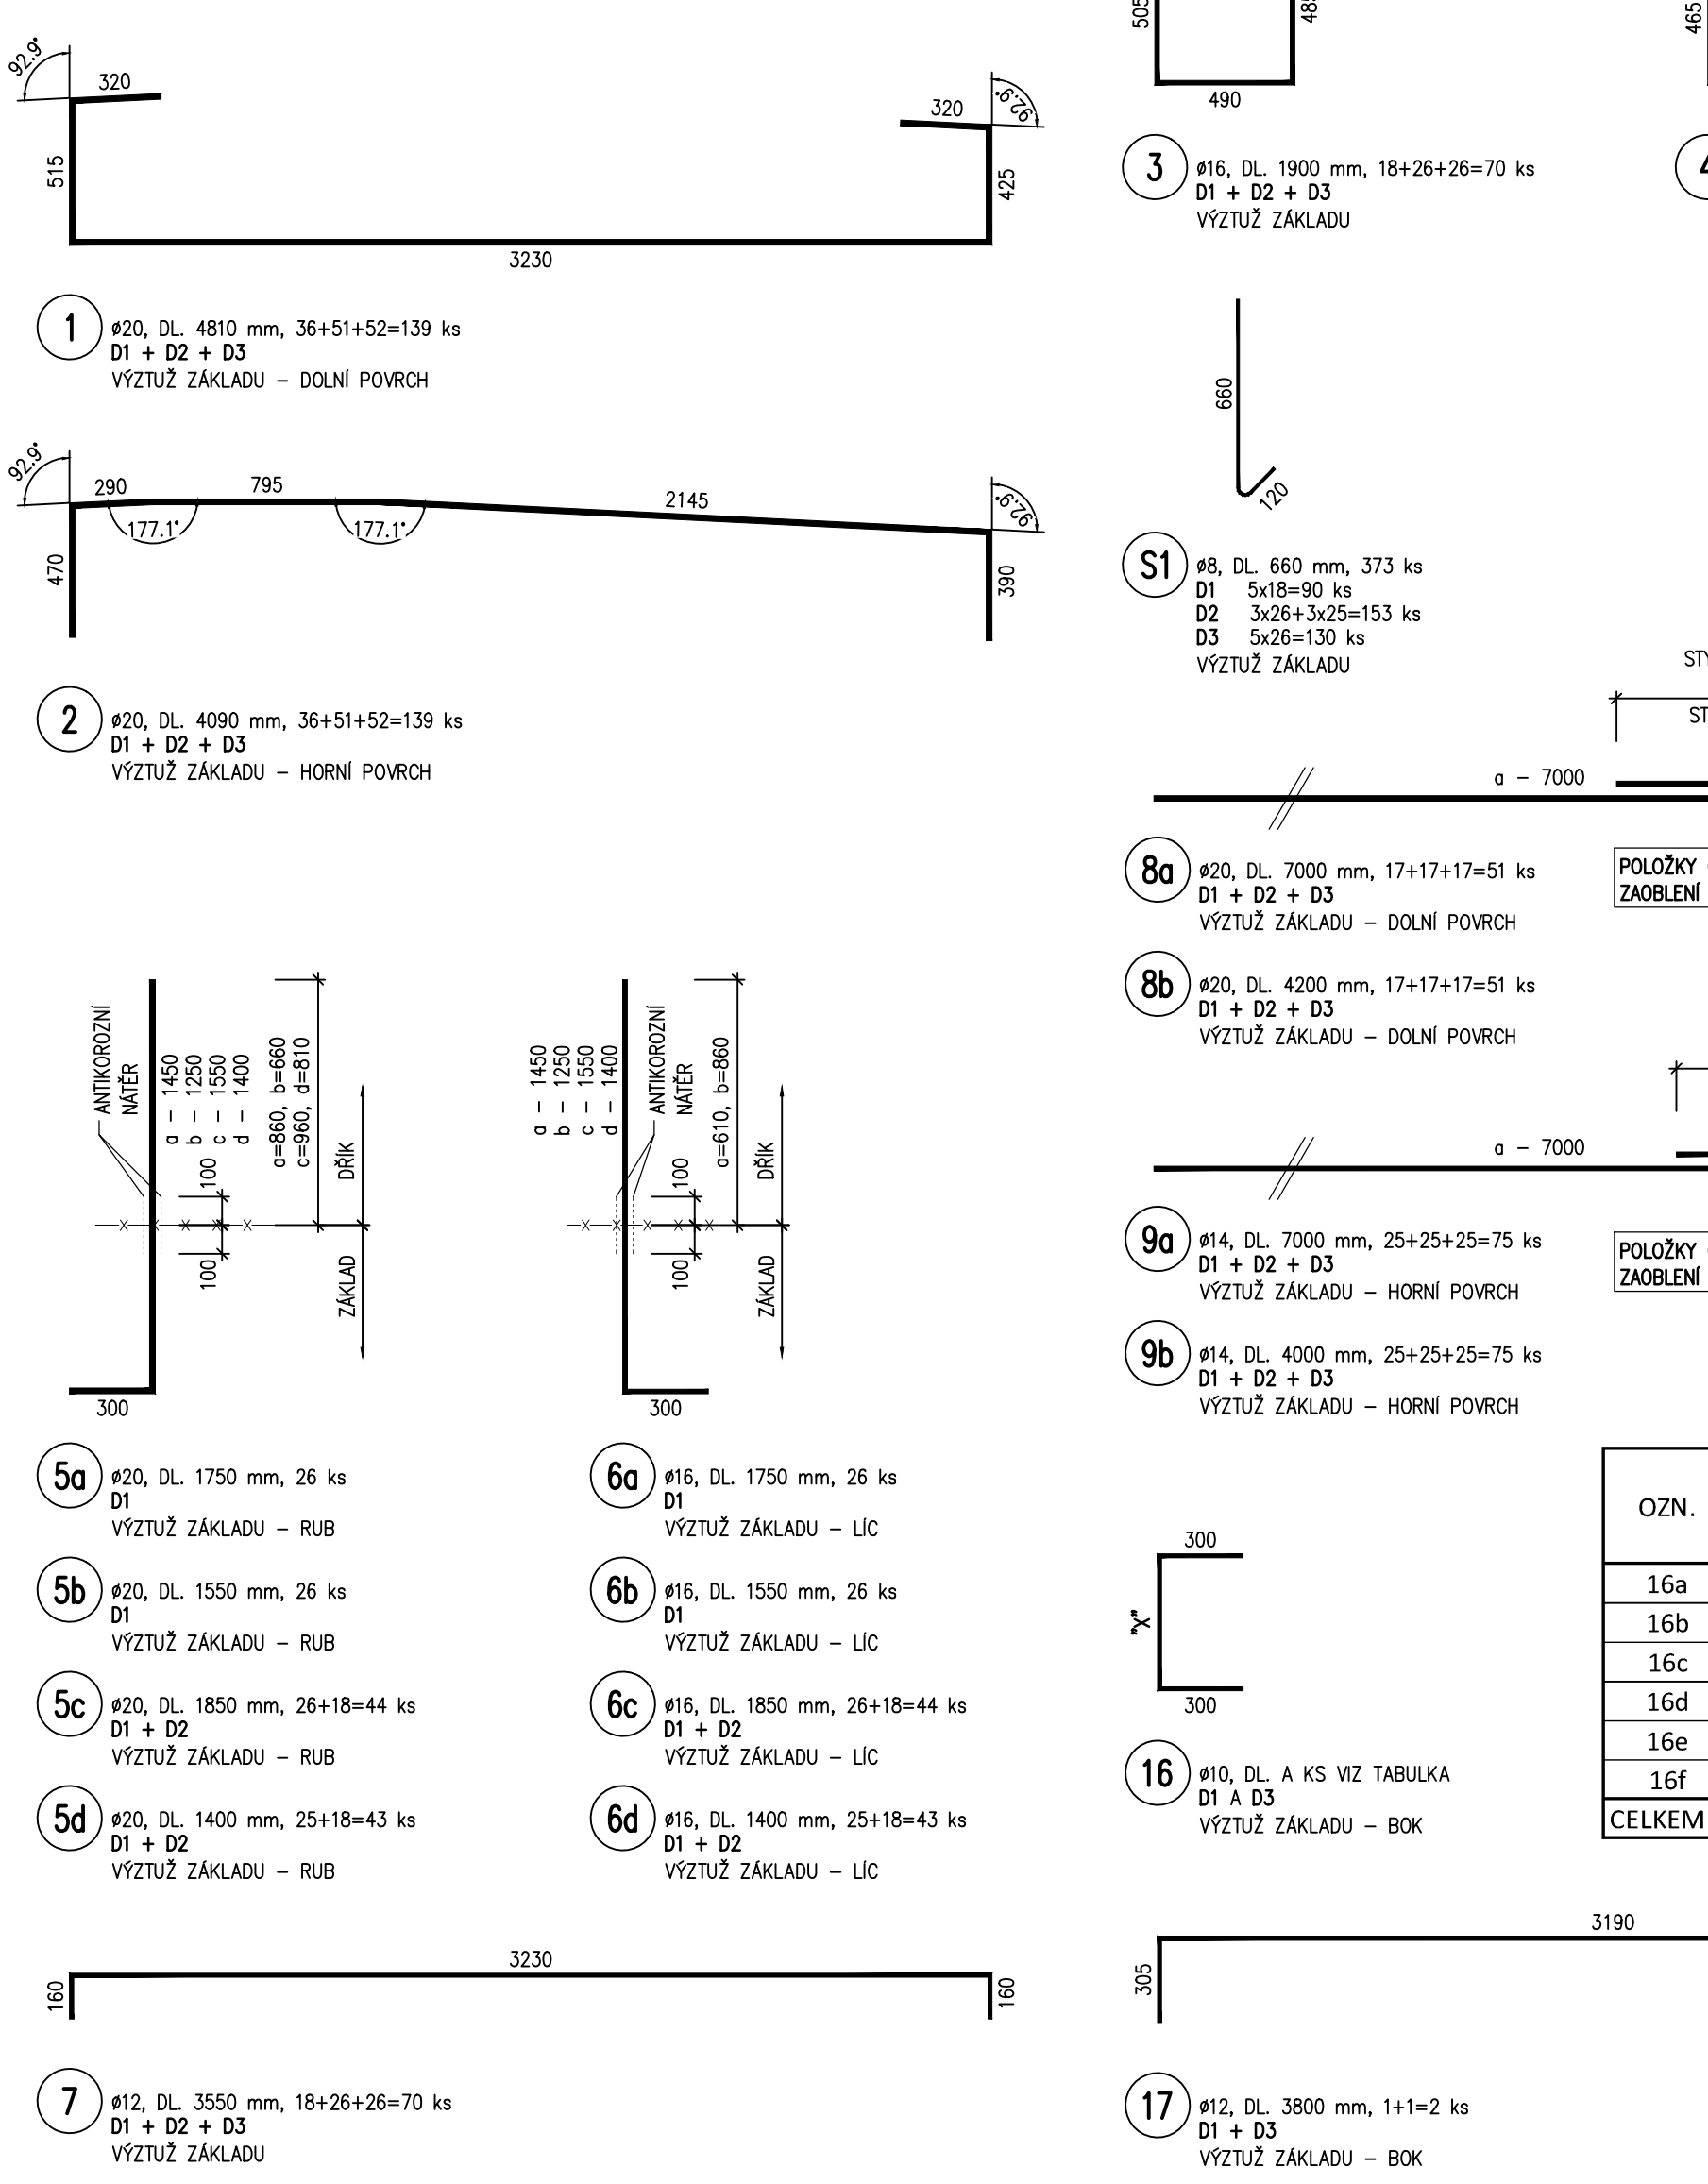


POHLED V LÍCI B1-B1 1:50

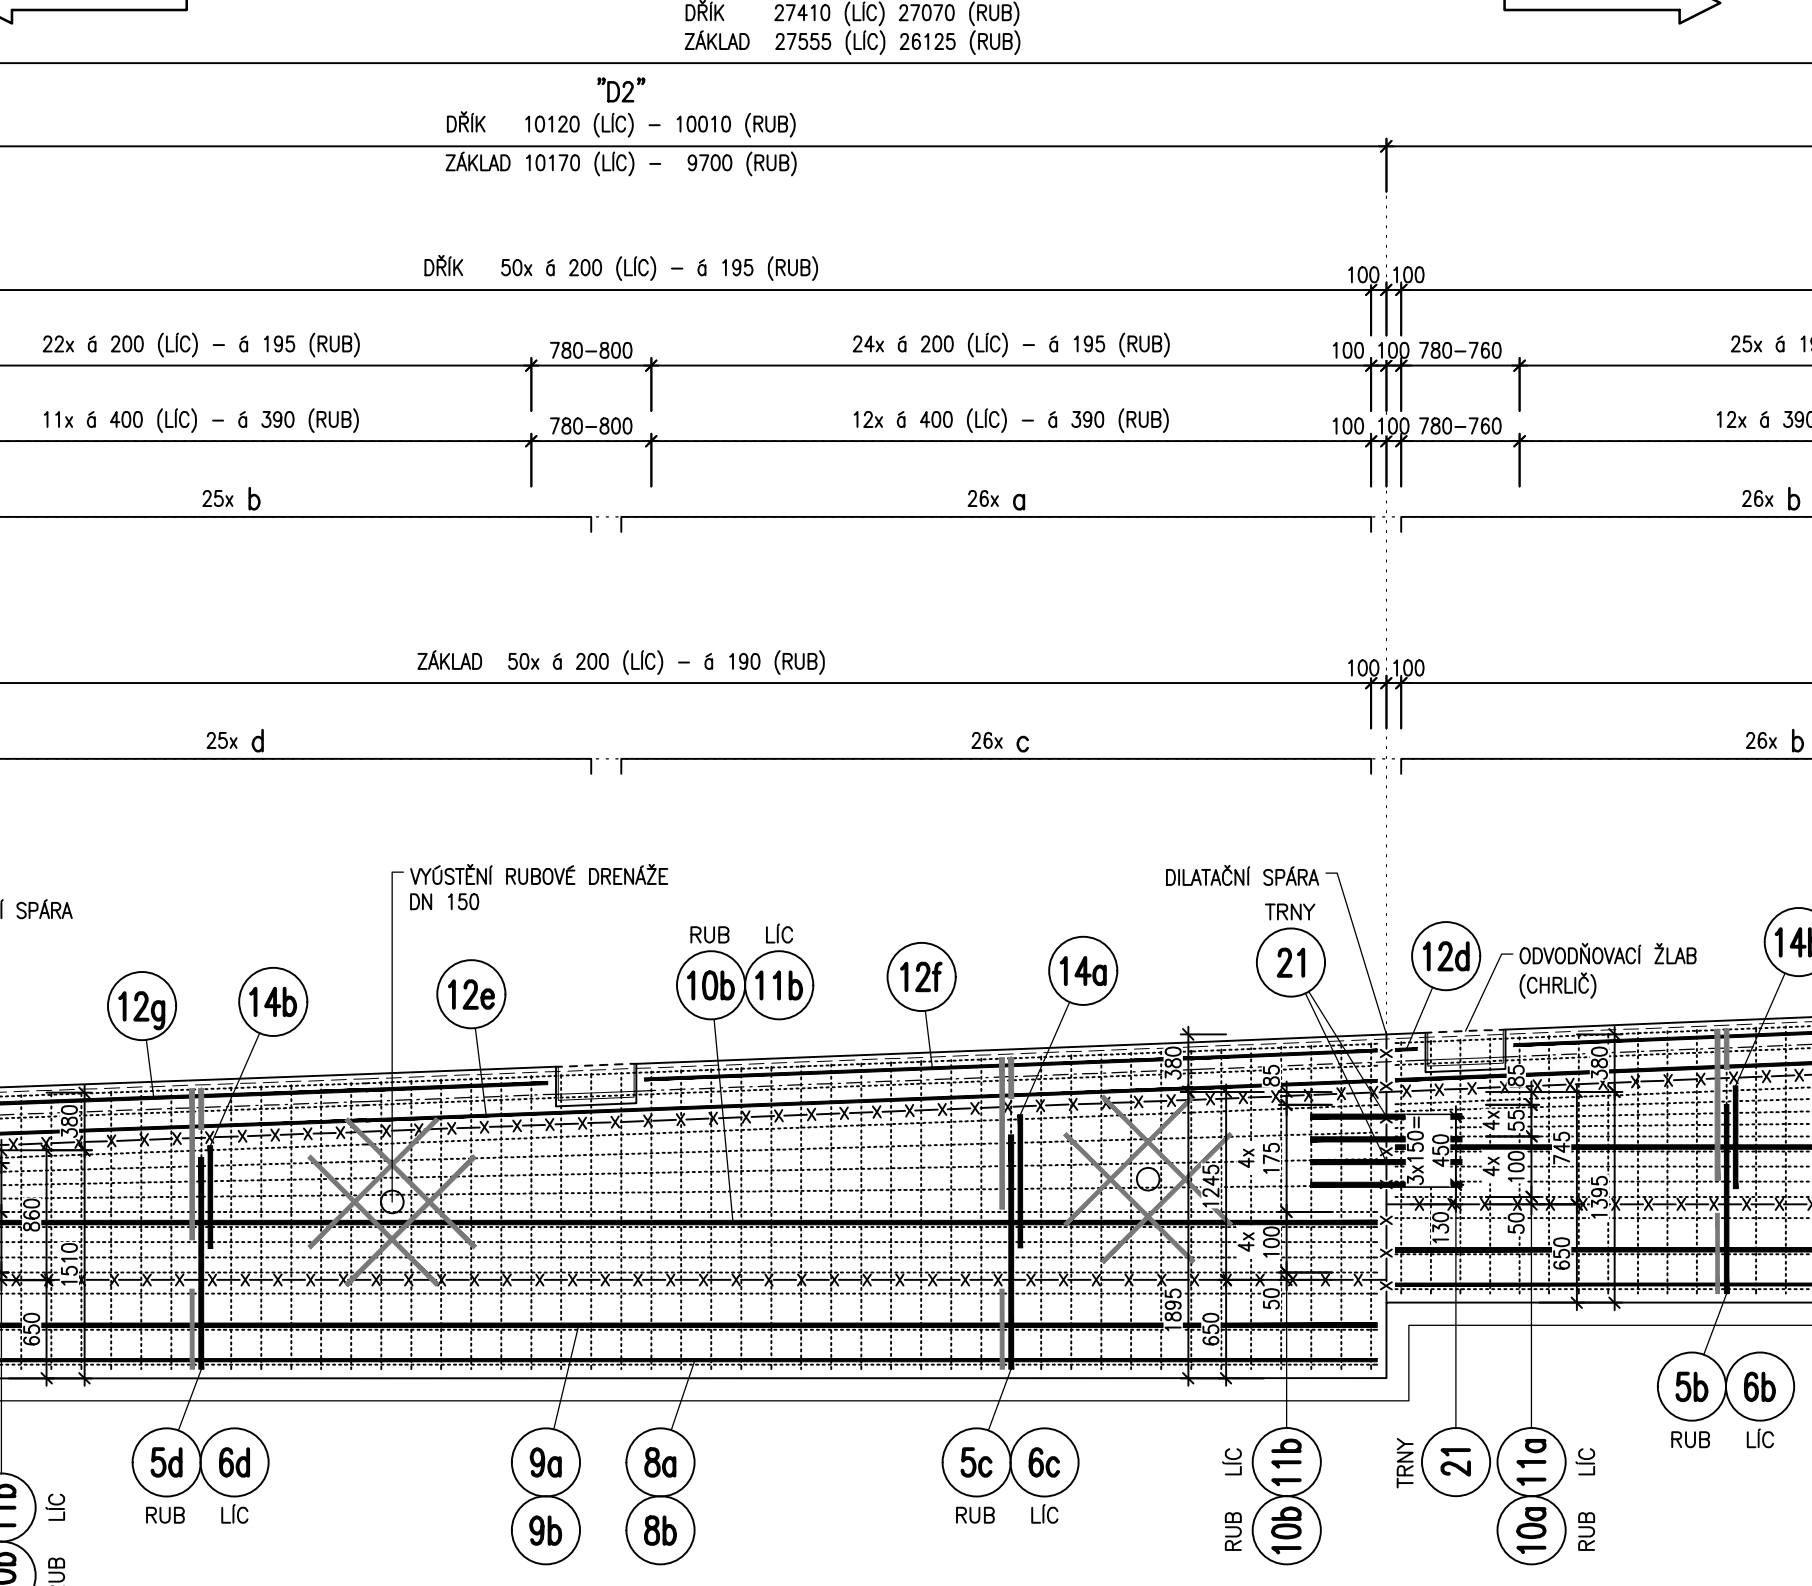

VÝTAH VÝZTUŽE - DŘÍK 1:25
VÝZTUŽ KÓTOVÁNA NA VNĚJŠÍ OBRYŠ

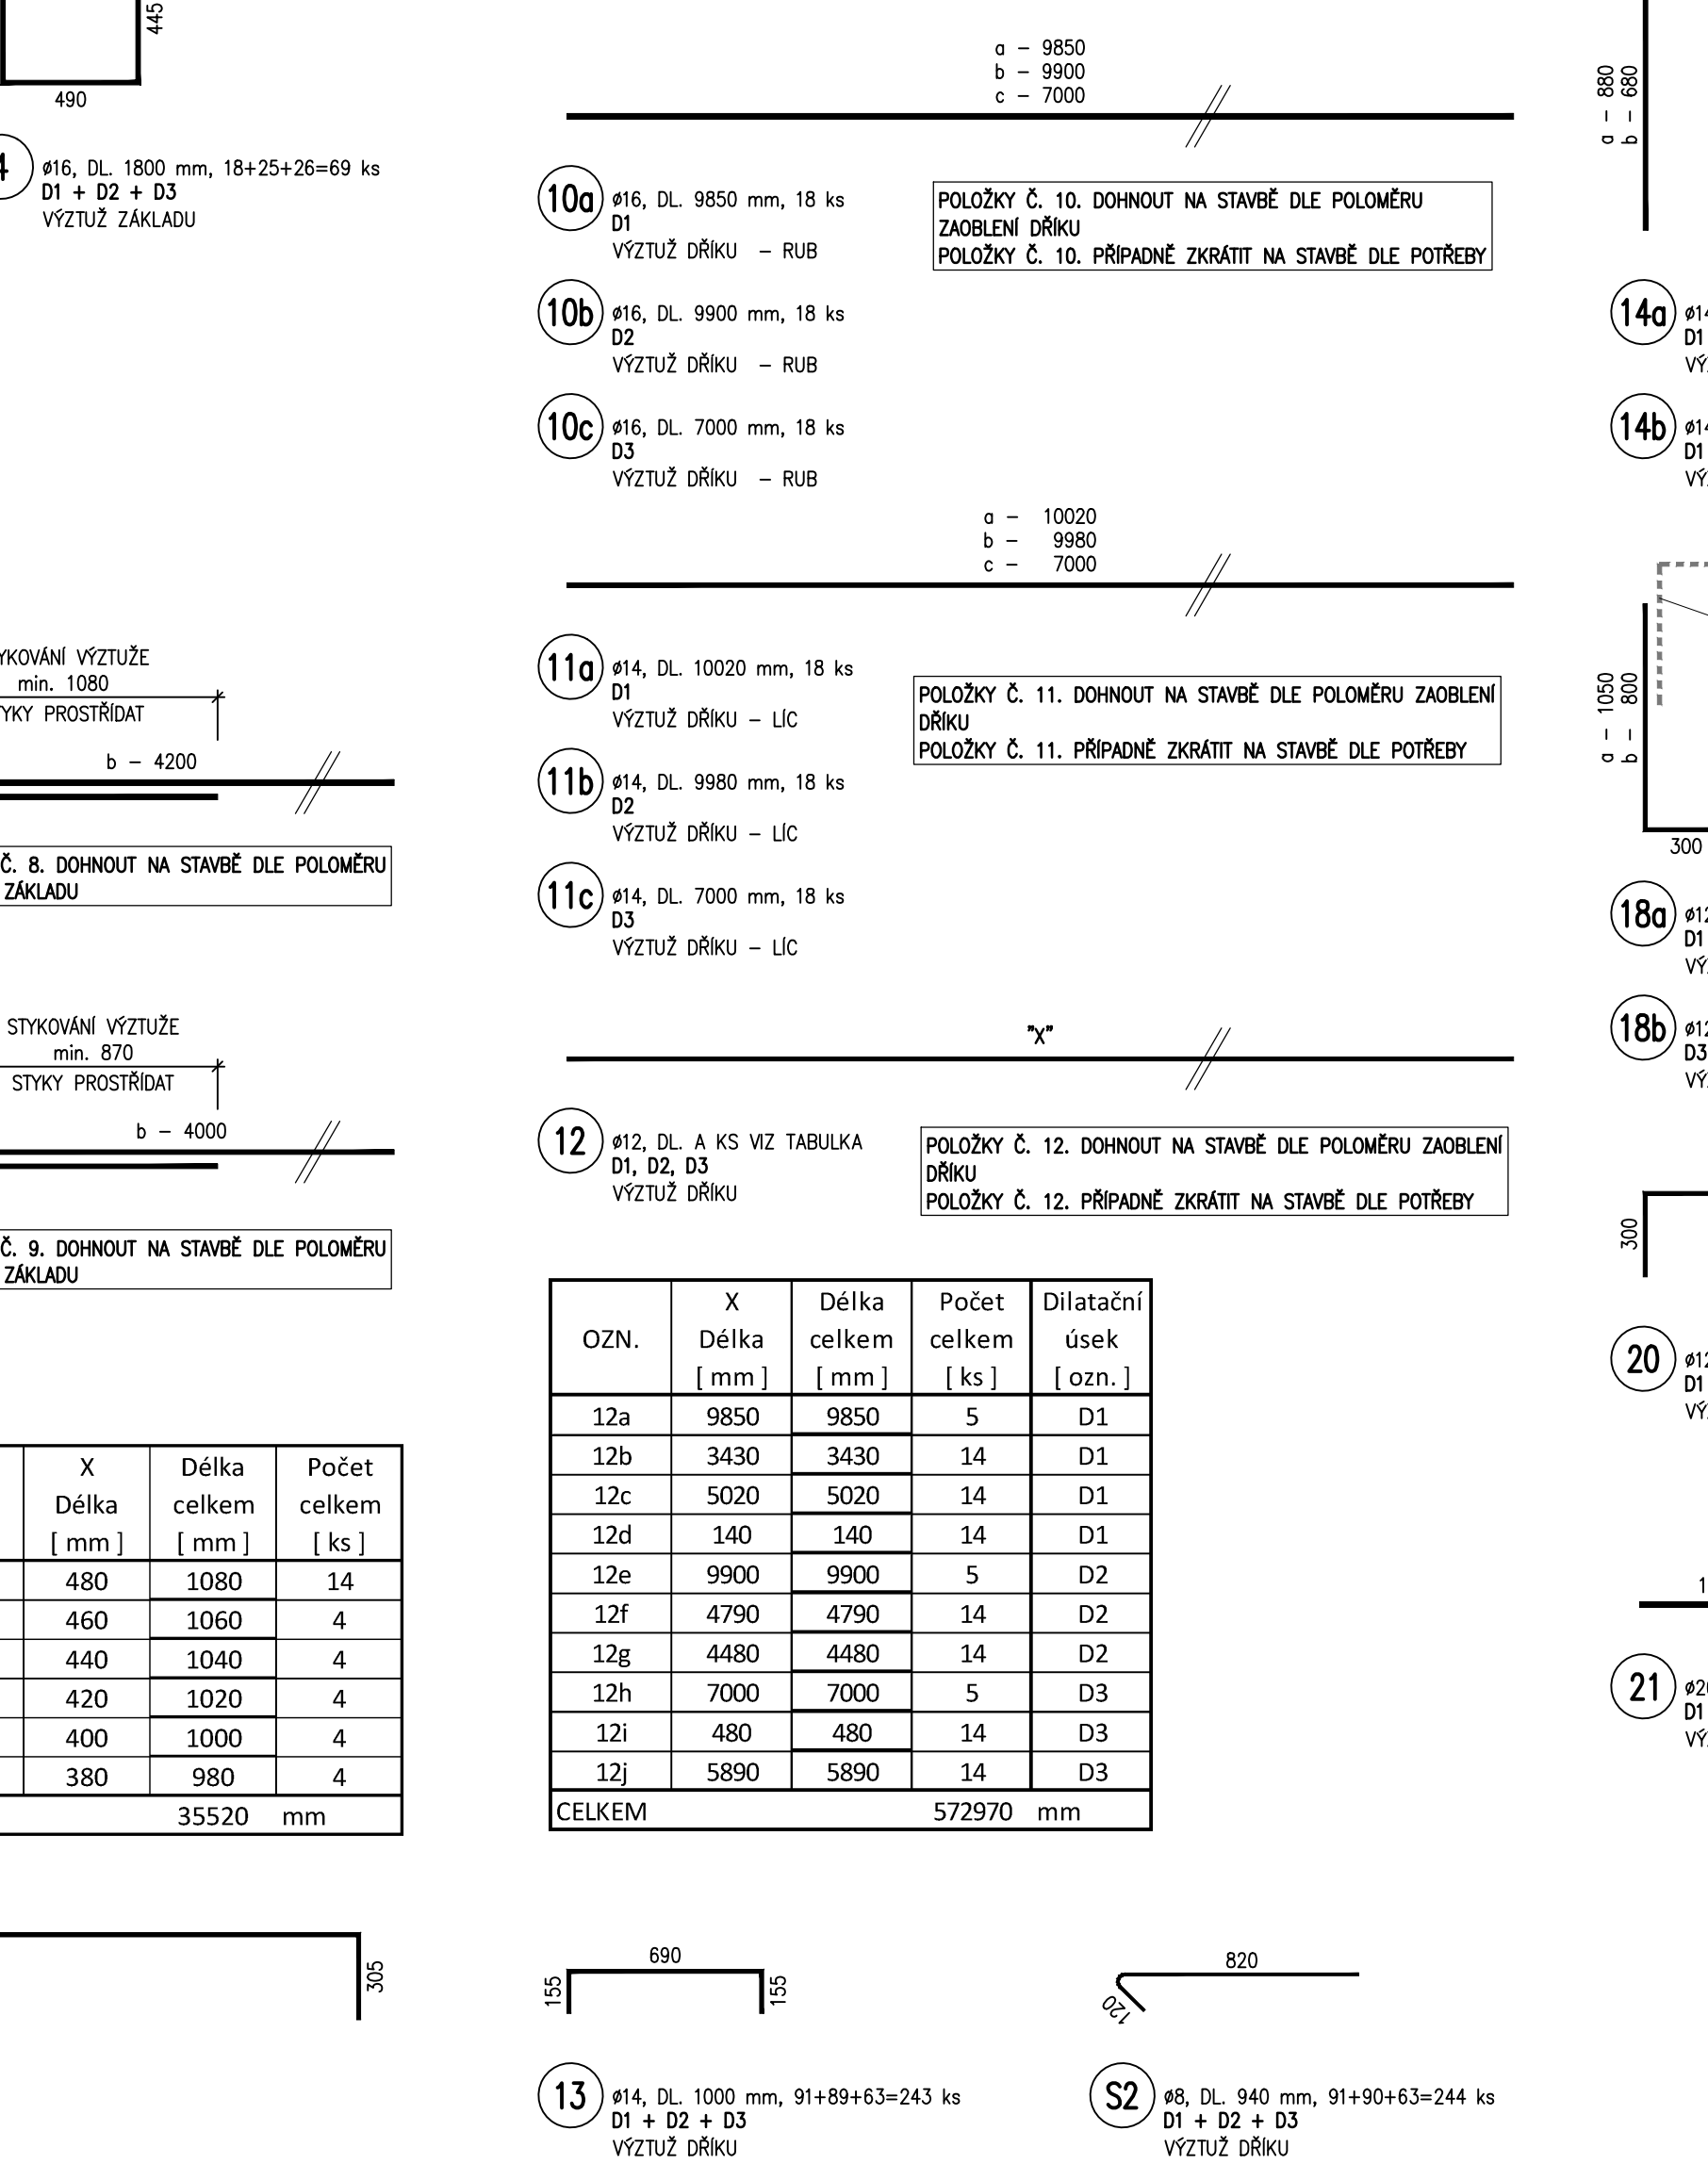

POHLED V LÍCI B1-B1 1:50

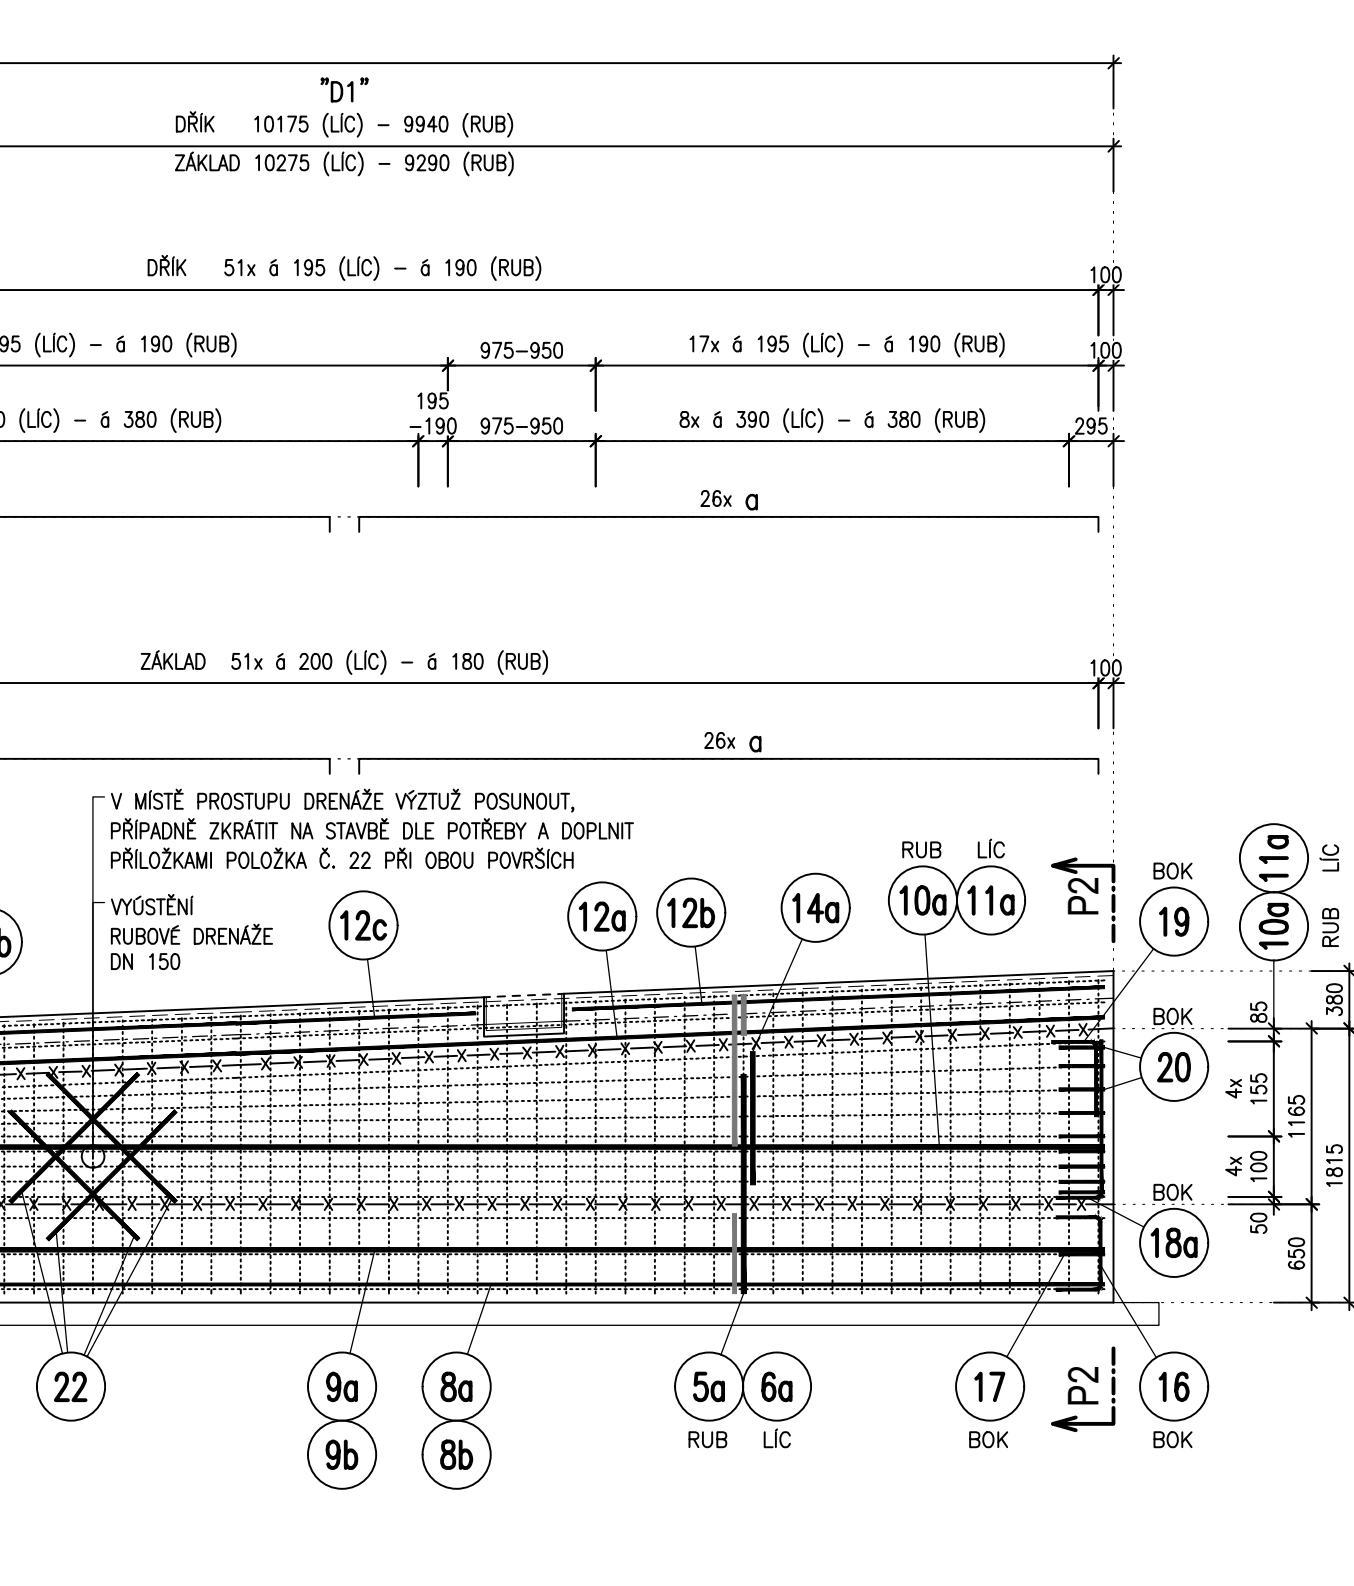

VÝTAH VÝZTUŽE - DŘÍK 1:25
VÝZTUŽ KÓTOVÁNA NA VNĚJŠÍ OBRYŠ


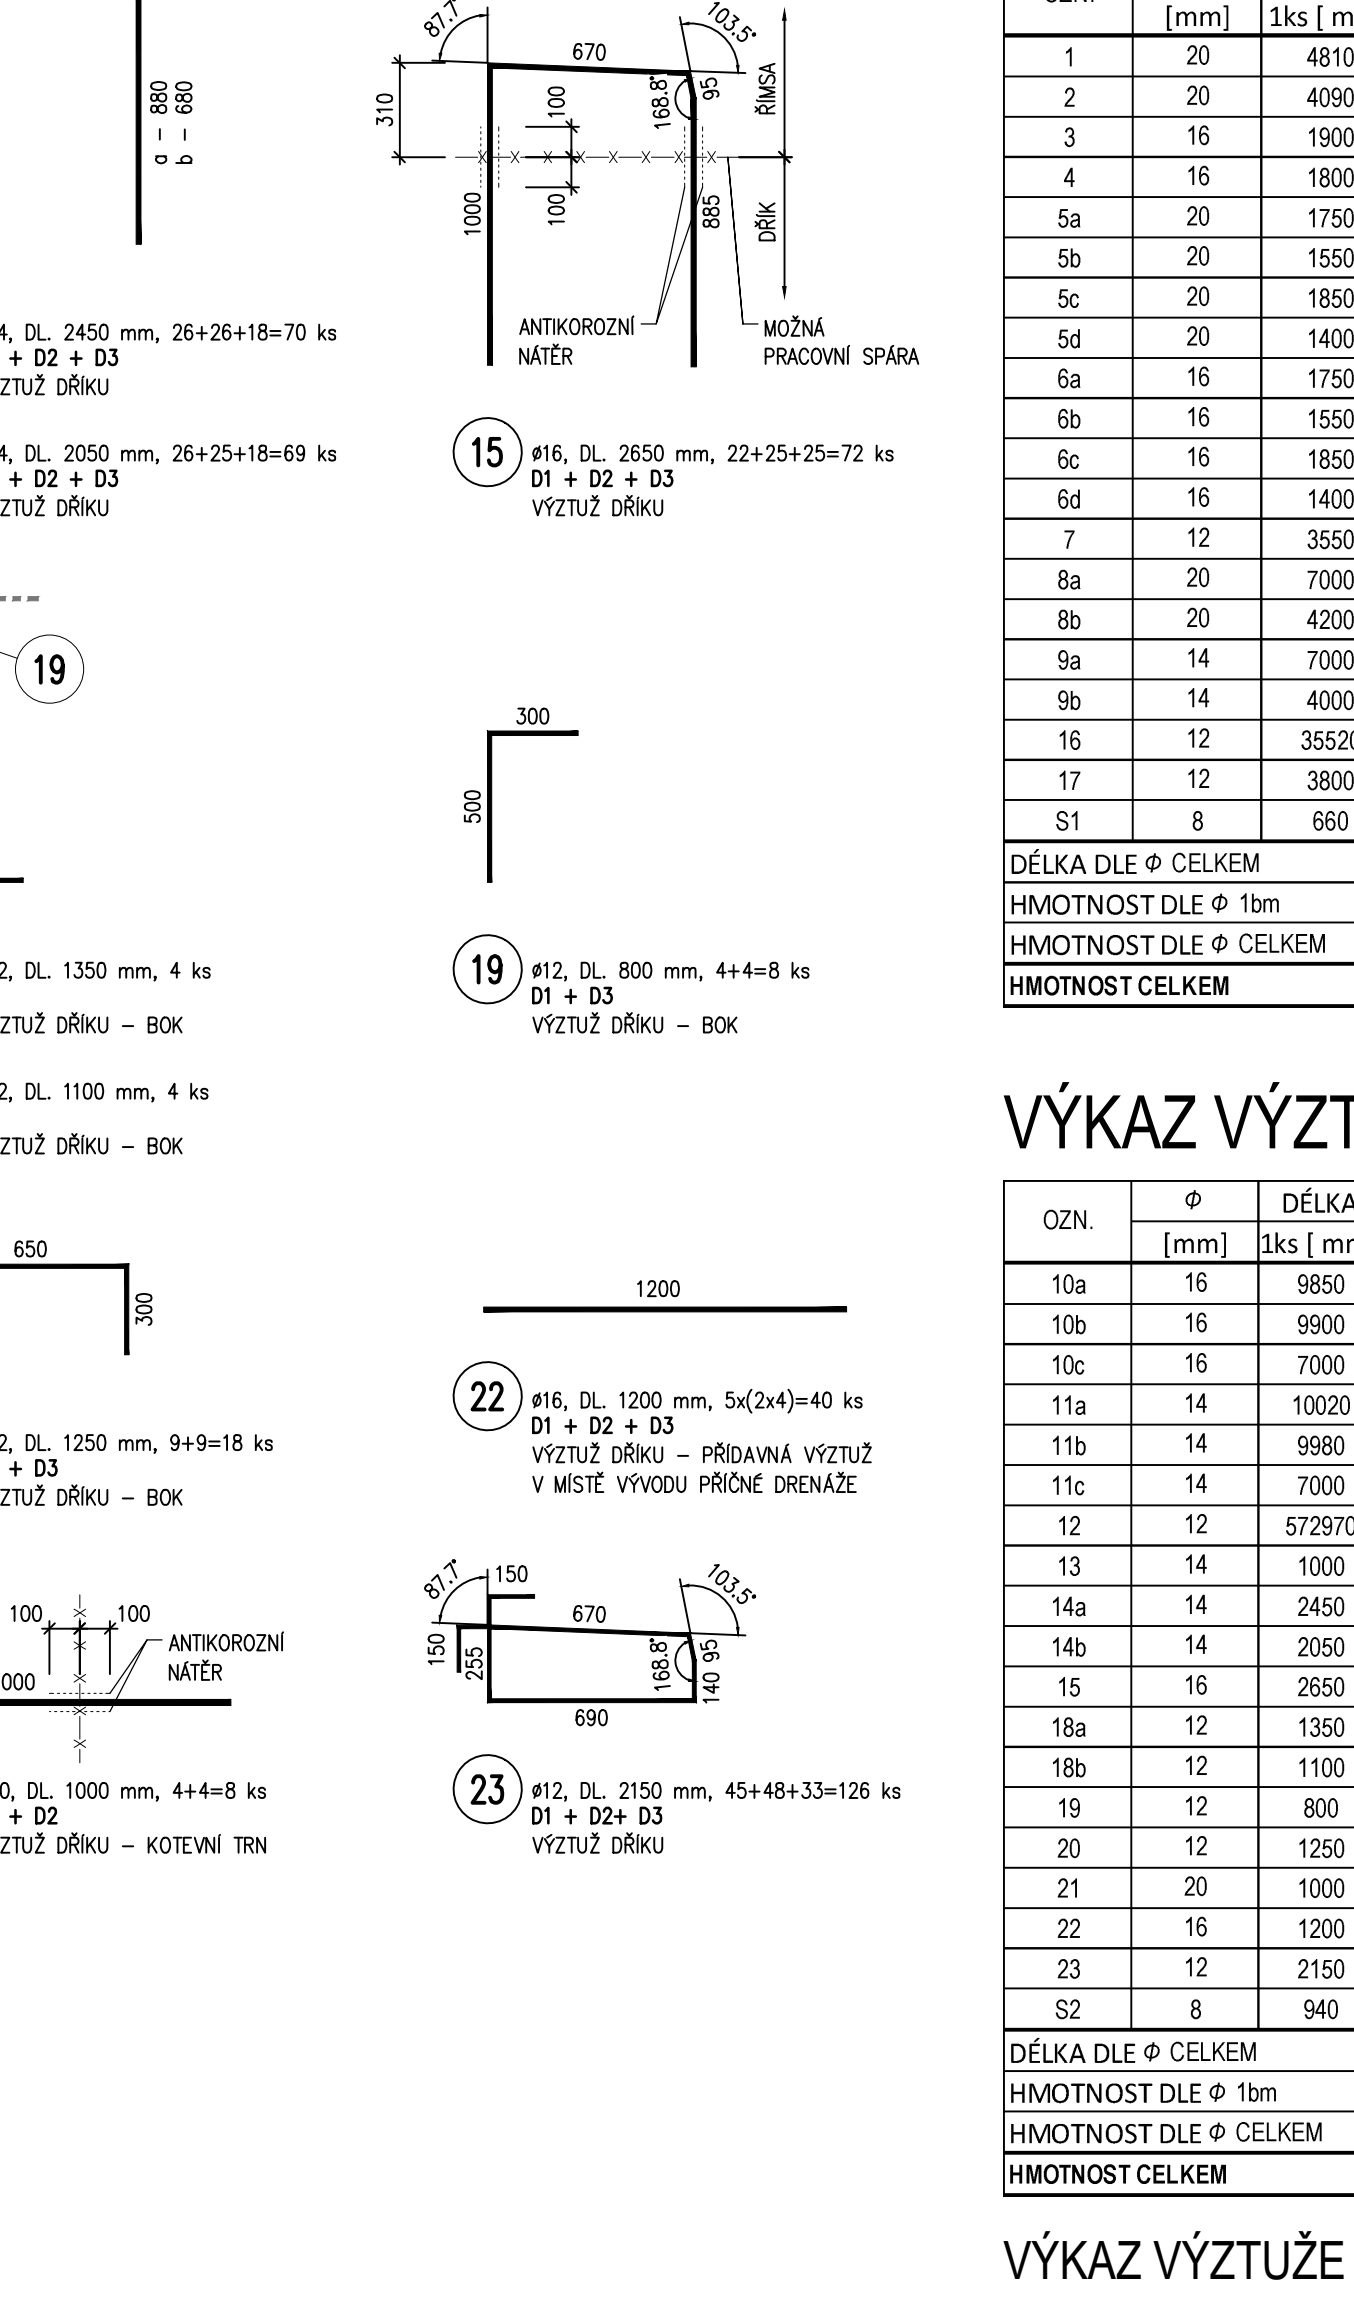


SCHÉMA VÝZTUŽE 1:25
POLOŽKA Č. 13, S2

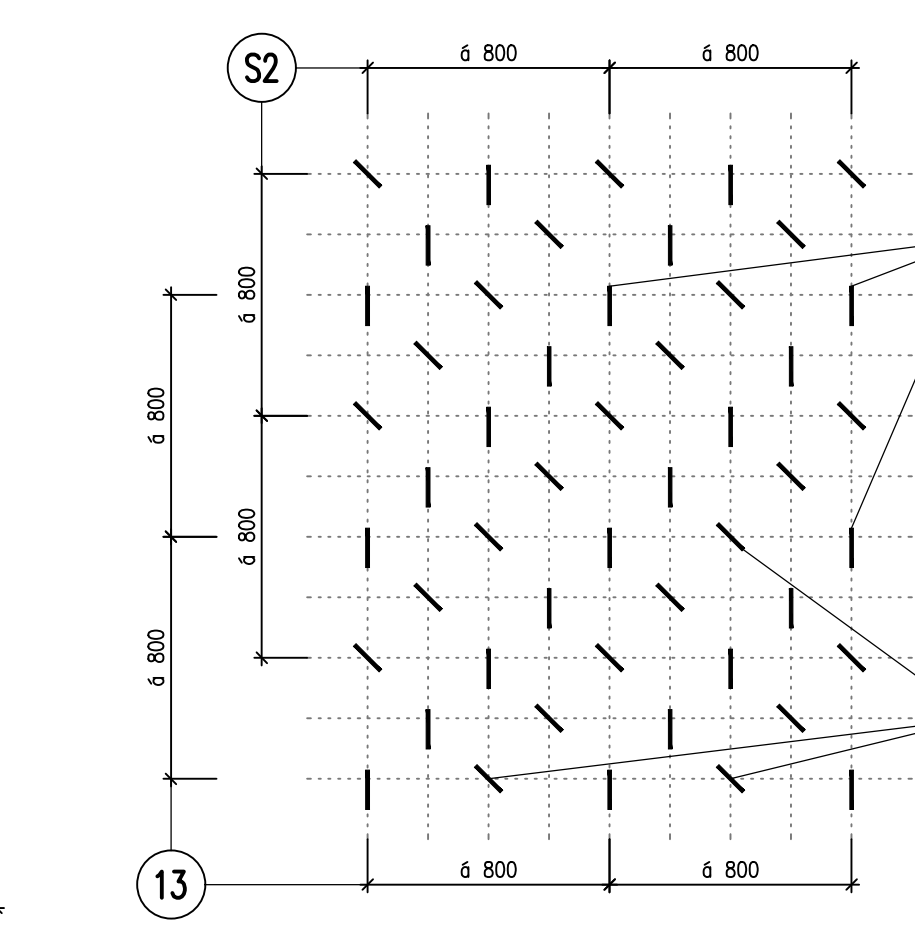


STAVEBNÍ MATERIÁLY

BETONY BUDOU PROVEDENY DLE ČSN EN 206
KONSTRUKČNÍ BETONY:
ZB ZÁKLAD
ZB DŘÍK
OSTATNÍ BETONY:
PODKLADNÍ BETON
BETONÁŘSKÁ VÝZTUŽ:
OCEL

C30/37 XD2, XF2, XC2 (CZ.F.1.2) – CI 0,2; D_{max} 22 – S3
C30/37 XD3, XF4, XC4 (CZ.F.1.2) – CI 0,2; D_{max} 22 – S3
C12/15 x0 (CZ.F.1.2) – CI 1,0; D_{max} 22 – S3
B500B

NEJMENŠÍ PRŮMĚR TRNU d, PRO OHÝBÁNÍ DLE ČSN EN 1992-1-1

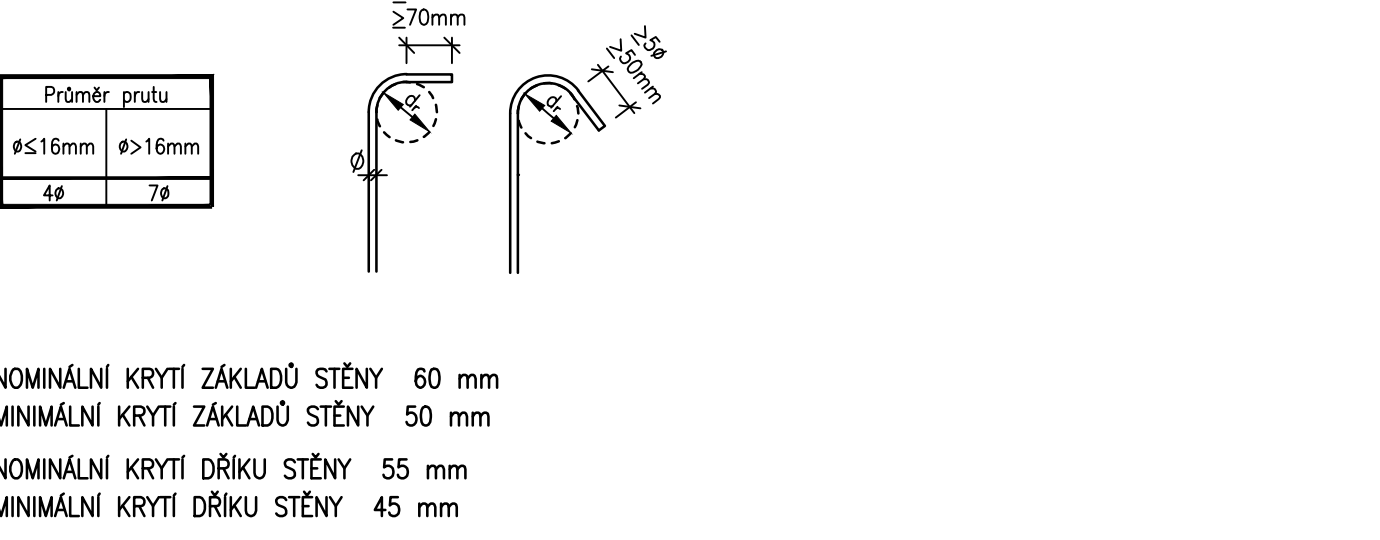

POZNÁMKY

- ZA ŮCELEM DOKONALÉHO PROBETONOVÁNÍ KONSTRUKCE NENÍ PŘÍPUSTNÉ, ABY MEZERA MEZI SOUBĚŽNÝMI POLOŽKAMI BYLA MENŠÍ NEŽ 35 mm.
- PRO PŘÍPADNÉ SVAŘOVÁNÍ VÝZTUŽE PLATÍ TP 193
- STYKOVANÁ VÝZTUŽ BUDE ULOŽENA NA SRÁZ

PŘEDKONCEPT

Název stavby		OBSLOUŽENOST	
II/101 Dolní Břežany - Zbraslav		SO 251.2	
Objednatel stavby		Krajská správa a údržba silnic Středočeského kraje, příspěvková organizace Zborovská 611/1, 150 21 Praha 5-Smíchov	
Autorský dozor		GeoTec-GS, a.s. Chmelová 2920/6, 106 00 Praha 10	
Technický dozor investora		TES + SGS + SGG vedoucí sdružení TES Consulting, s.r.o. V Olšanské 2300/75, 100 00 Praha 10-Strašnice	
Zhotovitel stavby		M-SILNICE a.s. Husova 1697, 530 03 Pardubice www.msilnice.cz	
Koordinační RDS		M - PROJEKCE s. r. o. Restova 956/13, 500 02 Hradec Králové www.m-projeke.cz	
Souřadnicový systém: S-JTSK		Výškový systém: Bpv	
Zpracovatel stavebního objektu/části:		Projektční kancelář PRIS spol. s r.o. Osova 717/20, 625 00 Brno-Starý Lysinec www.pris.cz	
Výpracoval: Iona Sýnková		Hlavní inženýr projektu: Ing. Jiří Ebenberger	
Odpovědný projektant: Ing. Martin Reutka		Kontroloval: Ing. Jiří ŠRUBAR	
Číslo zakázky: 25113		Datum: 06/2026	
Objekt/část: SO 251.2 - OPĚRNÉ ZDI ZED č. 09		Měřítko: 1:50; 1:25	
Příloha:		Číslo přílohy:	
VÝZTUŽ OPĚRNÉ ZDI		105_VOZ	