



MIKROPILOTY

PŘÍČNÝ ŘEZ P1-P1 km 1,660 000 1:25

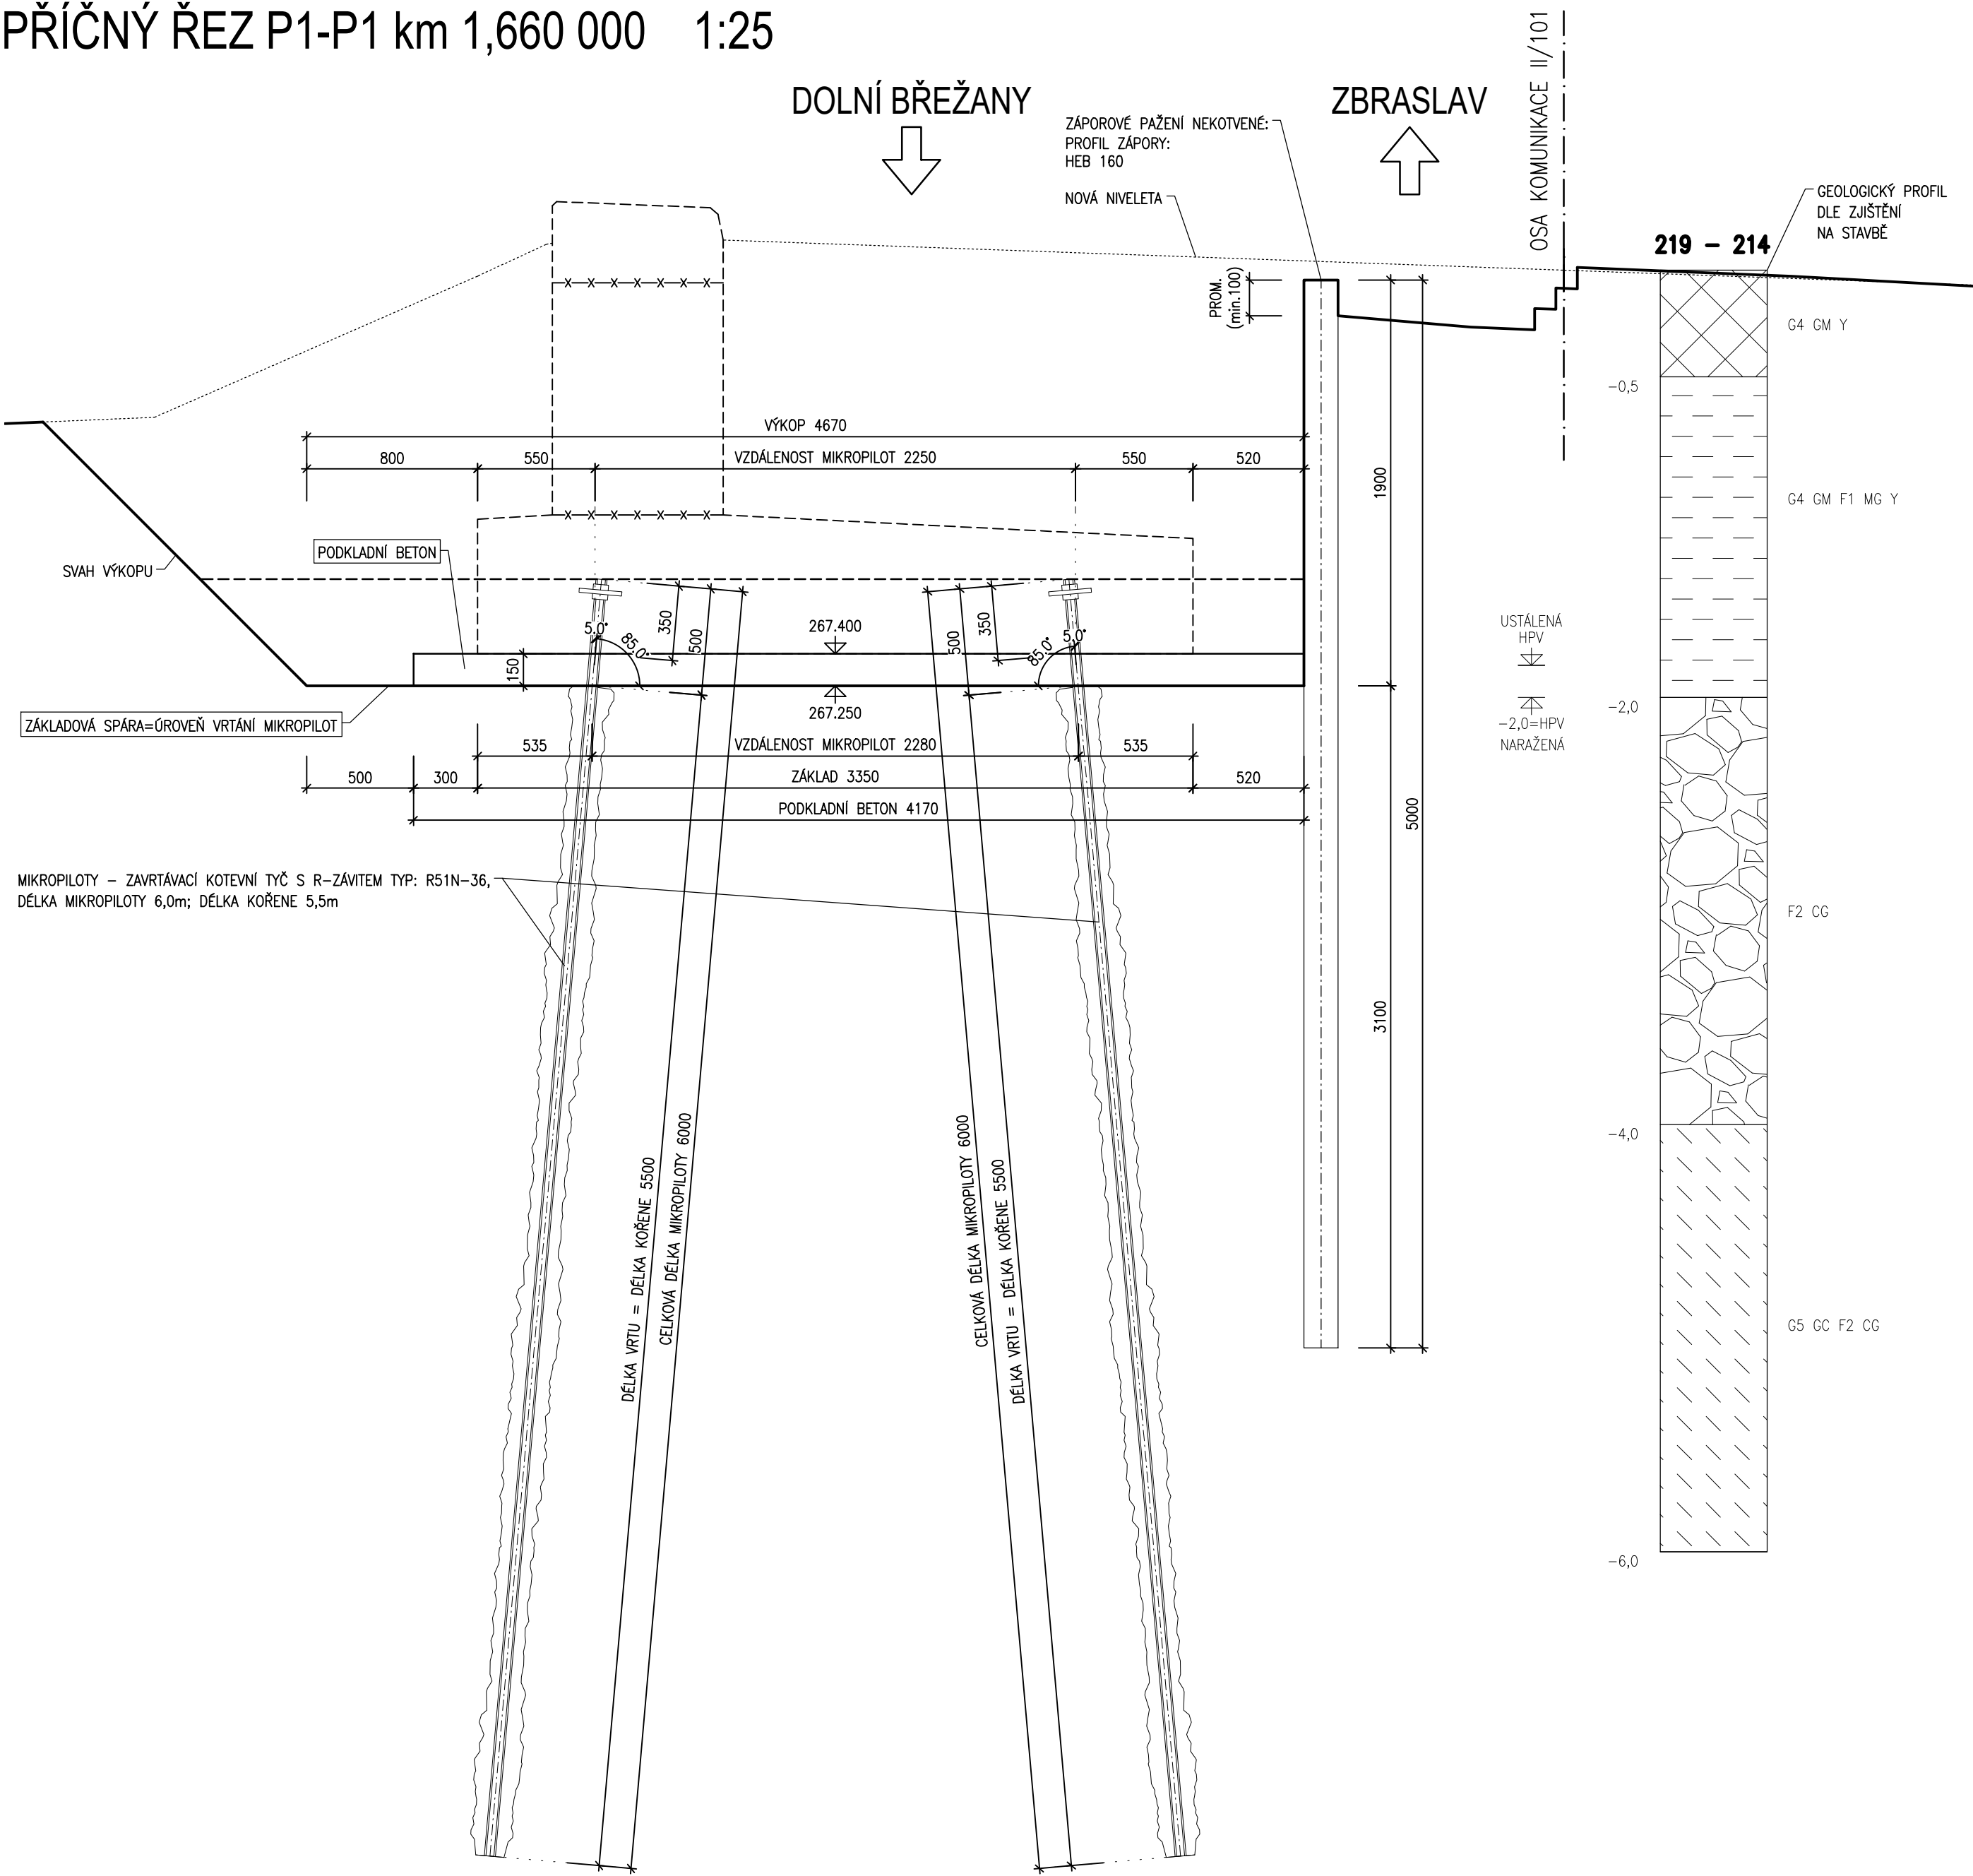


DETAIL UKONČENÍ MIKROPILOTY 1:5


POHLED

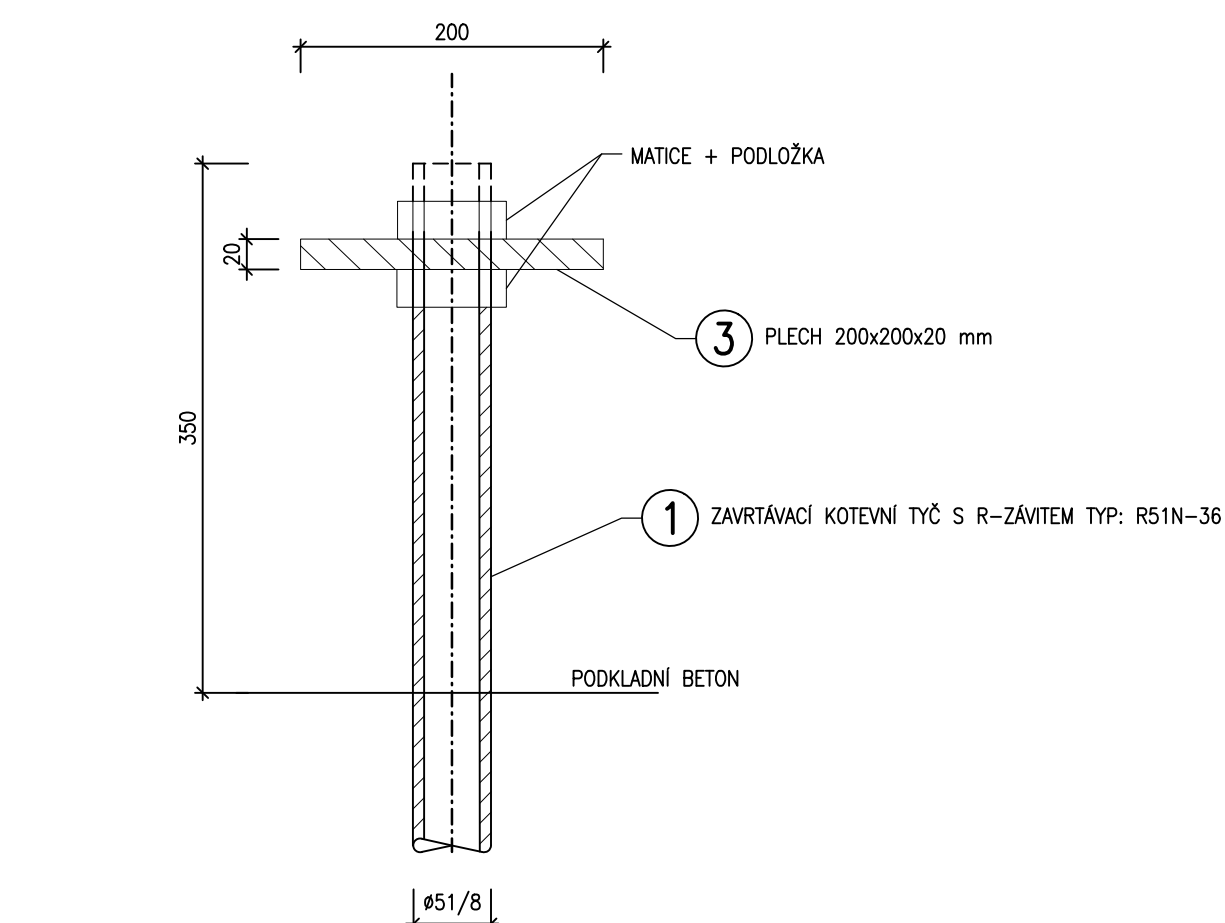


PŮDORYS

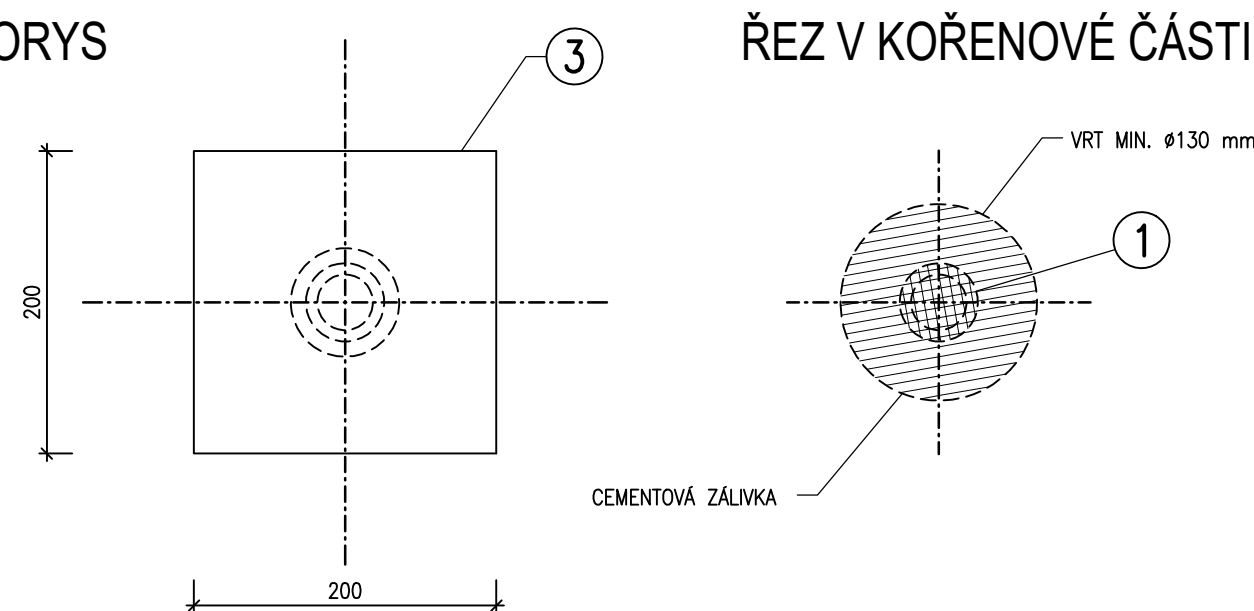

ŘEZ V KÖŘENOVÉ ČÁSTI

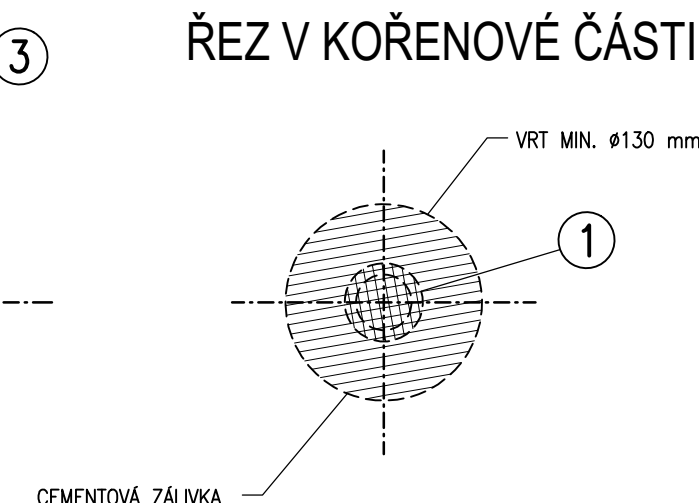

PŮDORYS 1:100

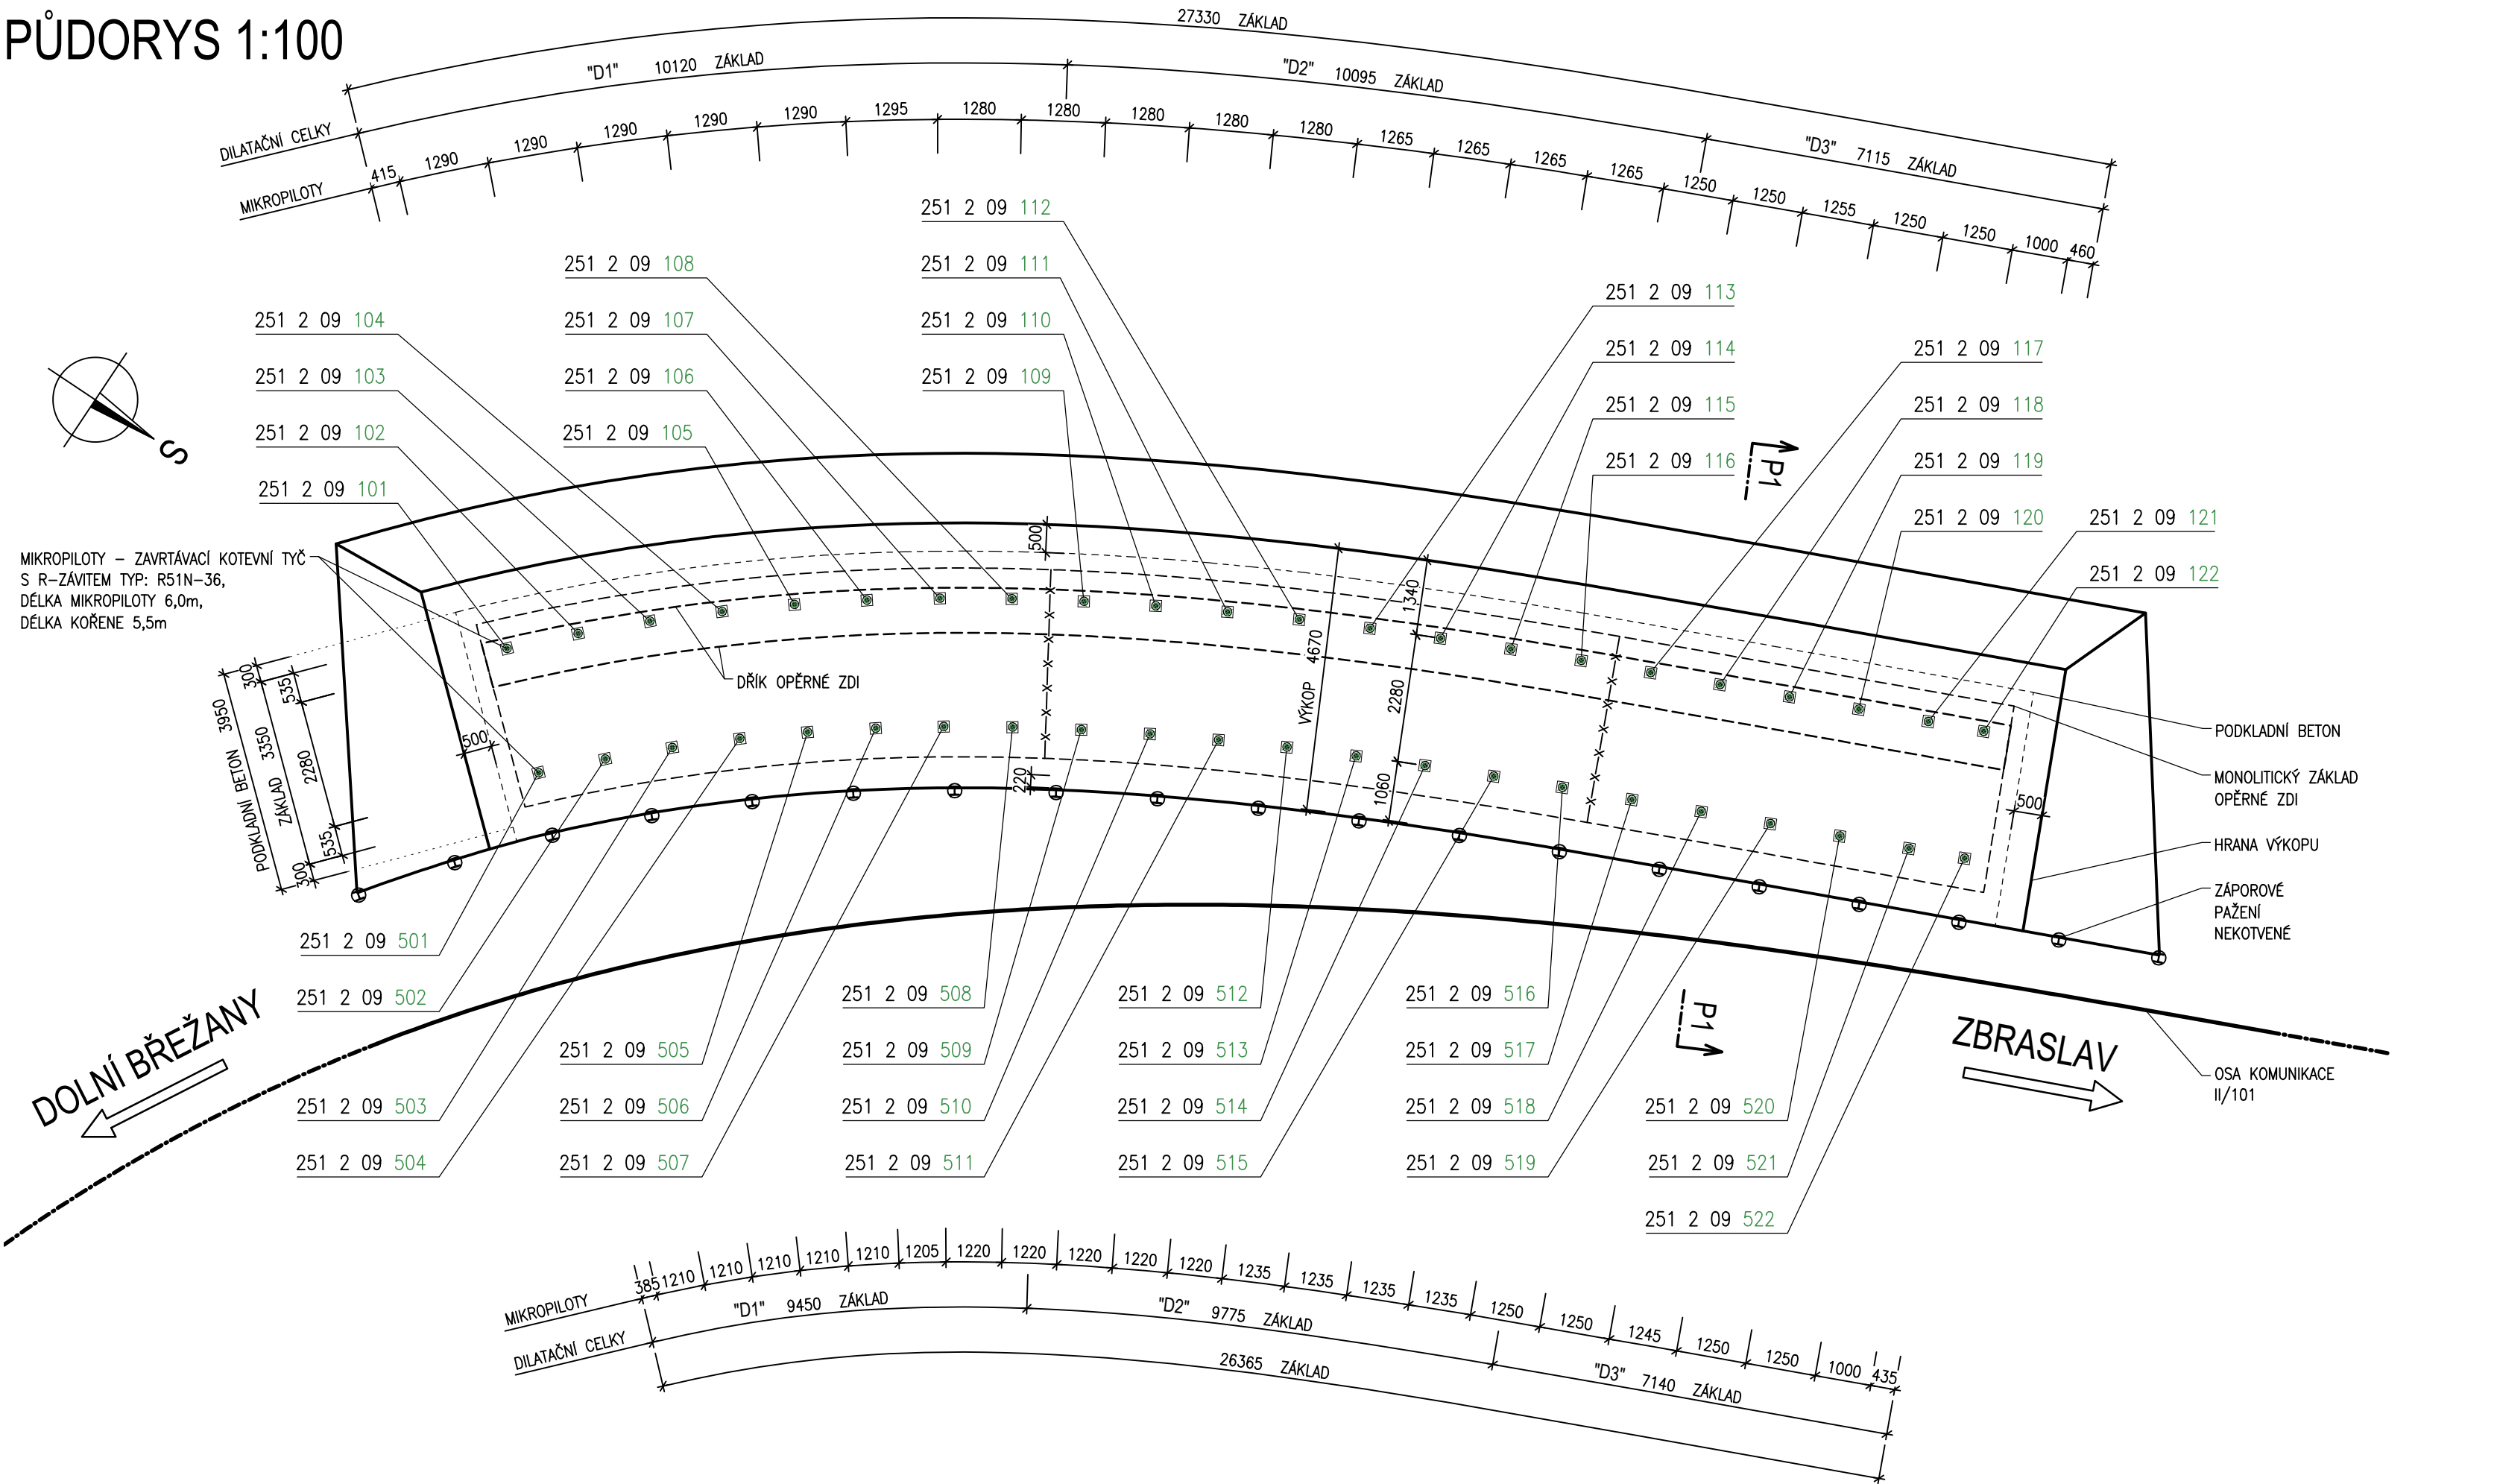

SEZNAM SOUŘADNIC

Vytčení mikropilot									
Opěrná zeď č. 9 - mikropiloty									
ŘADA BODŮ 09									
ČÁST	Označ. bodu	Číslo bodu	SOURADNICE		VÝSKA HLAVY MIKROPILOTY	CELKOVÁ DEŁKA MIKROPILOTY	VÝSKA PATY MIKROPILOTY	VÝSKA V ÜROVINI ZÁKLADOVÉ SPÁRY	ODKLON
			Y	X					
			[m]	[m]					
LICOVÁ STRANA	101	251 2 09 101	744138.143	1096762.928	268.550	6.00	262.57	268.050	5
	102	251 2 09 102	744139.065	1096762.023	268.550	6.00	262.57	268.050	5
	103	251 2 09 103	744139.953	1096761.086	268.550	6.00	262.57	268.050	5
	104	251 2 09 104	744140.807	1096760.116	268.550	6.00	262.57	268.050	5
	105	251 2 09 105	744141.624	1096759.116	268.550	6.00	262.57	268.050	5
	106	251 2 09 106	744142.401	1096758.089	268.550	6.00	262.57	268.050	5
	107	251 2 09 107	744143.147	1096757.031	268.550	6.00	262.57	268.050	5
	108	251 2 09 108	744143.850	1096755.963	268.550	6.00	262.57	268.050	5
	109	251 2 09 109	744144.522	1096754.975	268.050	6.00	262.07	267.550	5
	110	251 2 09 110	744145.165	1096753.770	268.050	6.00	262.07	267.550	5
	111	251 2 09 111	744145.782	1096752.650	268.050	6.00	262.07	267.550	5
	112	251 2 09 112	744146.377	1096751.518	268.050	6.00	262.07	267.550	5
	113	251 2 09 113	744146.942	1096750.387	268.050	6.00	262.07	267.550	5
	114	251 2 09 114	744147.491	1096749.248	268.050	6.00	262.07	267.550	5
	115	251 2 09 115	744148.025	1096748.101	268.050	6.00	262.07	267.550	5
	116	251 2 09 116	744148.550	1096746.950	268.050	6.00	262.07	267.550	5
	117	251 2 09 117	744149.055	1096745.807	267.750	6.00	261.77	267.250	5
	118	251 2 09 118	744149.580	1096744.664	267.750	6.00	261.77	267.250	5
RUBOVÁ STRANA	119	251 2 09 119	744150.085	1096743.516	267.750	6.00	261.77	267.250	5
	120	251 2 09 120	744150.566	1096742.371	267.750	6.00	261.77	267.250	5
	121	251 2 09 121	744151.067	1096741.226	267.750	6.00	261.77	267.250	5
	122	251 2 09 122	744151.458	1096740.310	267.750	6.00	261.77	267.250	5
	501	251 2 09 501	744136.620	1096761.235	268.550	6.00	262.57	268.050	5
	502	251 2 09 502	744137.481	1096760.388	268.550	6.00	262.57	268.050	5
	503	251 2 09 503	744138.311	1096759.510	268.550	6.00	262.57	268.050	5
	504	251 2 09 504	744139.107	1096758.601	268.550	6.00	262.57	268.050	5
	505	251 2 09 505	744139.870	1096757.664	268.550	6.00	262.57	268.050	5
	506	251 2 09 506	744140.600	1096756.697	268.550	6.00	262.57	268.050	5
	507	251 2 09 507	744141.292	1096755.711	268.550	6.00	262.57	268.050	5
	508	251 2 09 508	744141.963	1096754.689	268.550	6.00	262.57	268.050	5
	509	251 2 09 509	744142.604	1096753.650	268.050	6.00	262.07	267.550	5
	510	251 2 09 510	744143.217	1096752.593	268.050	6.00	262.07	267.550	5
DILATAČNÍ CELEK D1	511	251 2 09 511	744143.804	1096751.522	268.050	6.00	262.07	267.550	5
	512	251 2 09 512	744144.371	1096750.441	268.050	6.00	262.07	267.550	5
	513	251 2 09 513	744144.923	1096749.336	268.050	6.00	262.07	267.550	5
	514	251 2 09 514	744145.458	1096748.222	268.050	6.00	262.07	267.550	5
	515	251 2 09 515	744145.979	1096747.102	268.050	6.00	262.07	267.550	5
	516	251 2 09 516	744146.491	1096745.978	268.050	6.00	262.07	267.550	5
	517	251 2 09 517	744146.996	1096744.834	267.750	6.00	261.77	267.250	5
	518	251 2 09 518	744147.501	1096743.691	267.750	6.00	261.77	267.250	5
	519	251 2 09 519	744148.003	1096742.551	267.750	6.00	261.77	267.250	5
	520	251 2 09 520	744148.504	1096741.405	267.750	6.00	261.77	267.250	5
	521	251 2 09 521	744149.005	1096740.260	267.750	6.00	261.77	267.250	5
	522	251 2 09 522	744149.406	1096739.344	267.750	6.00	261.77	267.250	5

VÝKAZ MATERIÁLU

MIKROPILOTY OPĚRNÁ ZEĐ 09						
VÝKAZ MATERIÁLU						
OZN.	POPIS	DEŁKA [m]	HMOTNOST [kg/m]	POČET [ks]	DEŁKA CELKEM [m]	HMOTNOST [kg]
1	TYČ Ø51mm	6.00	7.7	1	6.000	46.20
3	PLECH 200/200,TL. 20mm	-	6.28	1	-	6.28
HMOTNOST CELKEM ... PRO 1 MIKROPILOTU DL. 6.0 m						52.48 kg
HMOTNOST CELKEM ... PRO VŠECH 44 MIKROPILOT						2309.12 kg
POZNÁMKA:						
- JE VÝKÁŽANA CELKOVÁ DEŁKA TYČE 6,0 m VČETNĚ PŘESAHU 0,35 m DO ZÁKLADU						

VÝKAZ MIKROPILOT

VÝKAZ VRTŮ PRO MIKROPILOTY			
OZN.	DEŁKA VRTU CELKEM [m]	POČET VRTŮ / [ks]	DEŁKA CELKEM [m]
ŠIKMÉ	6.00	44	264.00
CELKEM DEŁKA VRTŮ CELKEM			264.00 m

VÝKAZ MIKROPILOT	
ŠIKMÉ	44
CELKEM	44

MATERIÁL

CEMENTOVÁ SUSPENZE INJEKTAŽNÍ CEM 32,5R, C25/30

POZNÁMKY

- ZHOTOVITEL JE POVINEN PRO VŠECHNY ZEMĚMĚŘICKÉ PRÁCE POSTUPOVAT DLE TKP KAP. 1, ODS. 1.6.3.
- PRO MIKROPILOTY BUDOU POUŽITÝ INJEKČNÍ ZAVRTÁVACÍ KOTVENÍ TYČE SDA, TYP RS1N-36
- MIKROPILOTY JSOU VYTÝČENY V ÜROVINI ZÁKLADOVÉ SPÁRY, TZN. V DOLNÍ ÜROVINI PODKLADNÍHO BETONU.
- PRO PŘÍPADNÉ SPOJOVÁNÍ BUDOU POUŽITÝ ORIGINÁLNÍ SPOJUNKY
- SA MOZAVRTÁVACÍ TYČ BUDE UKONČENA DESKOU 200x200x20 mm A Z OBOU STRAN STAŽENA MATICEM
- VŠECHNY MIKROPILOTY JSOU ŠIKMÉ 5°
- PROVÁDĚNÍ MIKROPILOT MUSÍ BÝT V SOULADU S ČSN EN 14199.
- CEMENTOVÁ SUSPENZE MUSÍ MÍT FINÁLNÍ PEVNOST MIN. C25/30
- PRO ČERPÁNÍ VODY ZE DNA ZÁKLADOVÉ SPÁRY BUDOU ZBUDOVÁNY JIMKY.

PŘEDKONCEPT

OZNAČ.		TEXT ZMĚNY - ODŮVODNĚNÍ	DATUM
		TABULKA ZMĚN	PODPIS
Název stavby		II/101 Dolní Břežany - Zbraslav	
		SO 251.2	
Objednatel stavby		Krajská správa a údržba silnic Středočeského kraje, příspěvková organizace Zborovská 81/11, 150 21 Praha 5-Smíchov	
Autorský dozor		GeoTec GS® GeoTec-GS, a.s. Chmelová 2920/6, 106 00 Praha 10	
Technický dozor investora		TES + SGS + SGG vedoucí sdružení: TES Consulting, s.r.o. V Olšánách 2300/75, 100 00 Praha 10-Strašnice	
Zhotovitel stavby		M-SILNICE a.s. Husova 1697, 530 03 Pardubice www.msilnice.cz	
Koordínátor RDS		M - PROJEKCE s. r. o. Reslova 956/13, 500 02 Hradec Králové www.m-projekce.cz	
Souladnicový systém: S-JTSK		Výškový systém: Bpv	
Zpracovatel stavebního objektu/části:		Projekční kancelář PRIS spol. s r.o. Osová 717/20, 625 00 Brno-Starý Lískovec www.pris.cz	
Vypracoval: Iona Syrková		Hlavní inženýr projektu: Ing. Jiří Ehrenberger	
Odpovědný projektant: Ing. Martin Reuhka		Kontroloval: Ing. Jiří ŠRUBAR	
Číslo zadání: 25-122-02		Datum: 03/2026	
Objekt/část: SO 251.2 - OPĚRNÉ ZDI ZEĐ č. 09		Měřítko: 1:100; 1:25; 1:5	
Příloha: MIKROPILOTY		Stupeň: S RDS	
		Číslo přílohy: 104_MIK	