



TVAR OPĚRNÉ ZDI


POHLED V LÍCI B1-B1 1:50

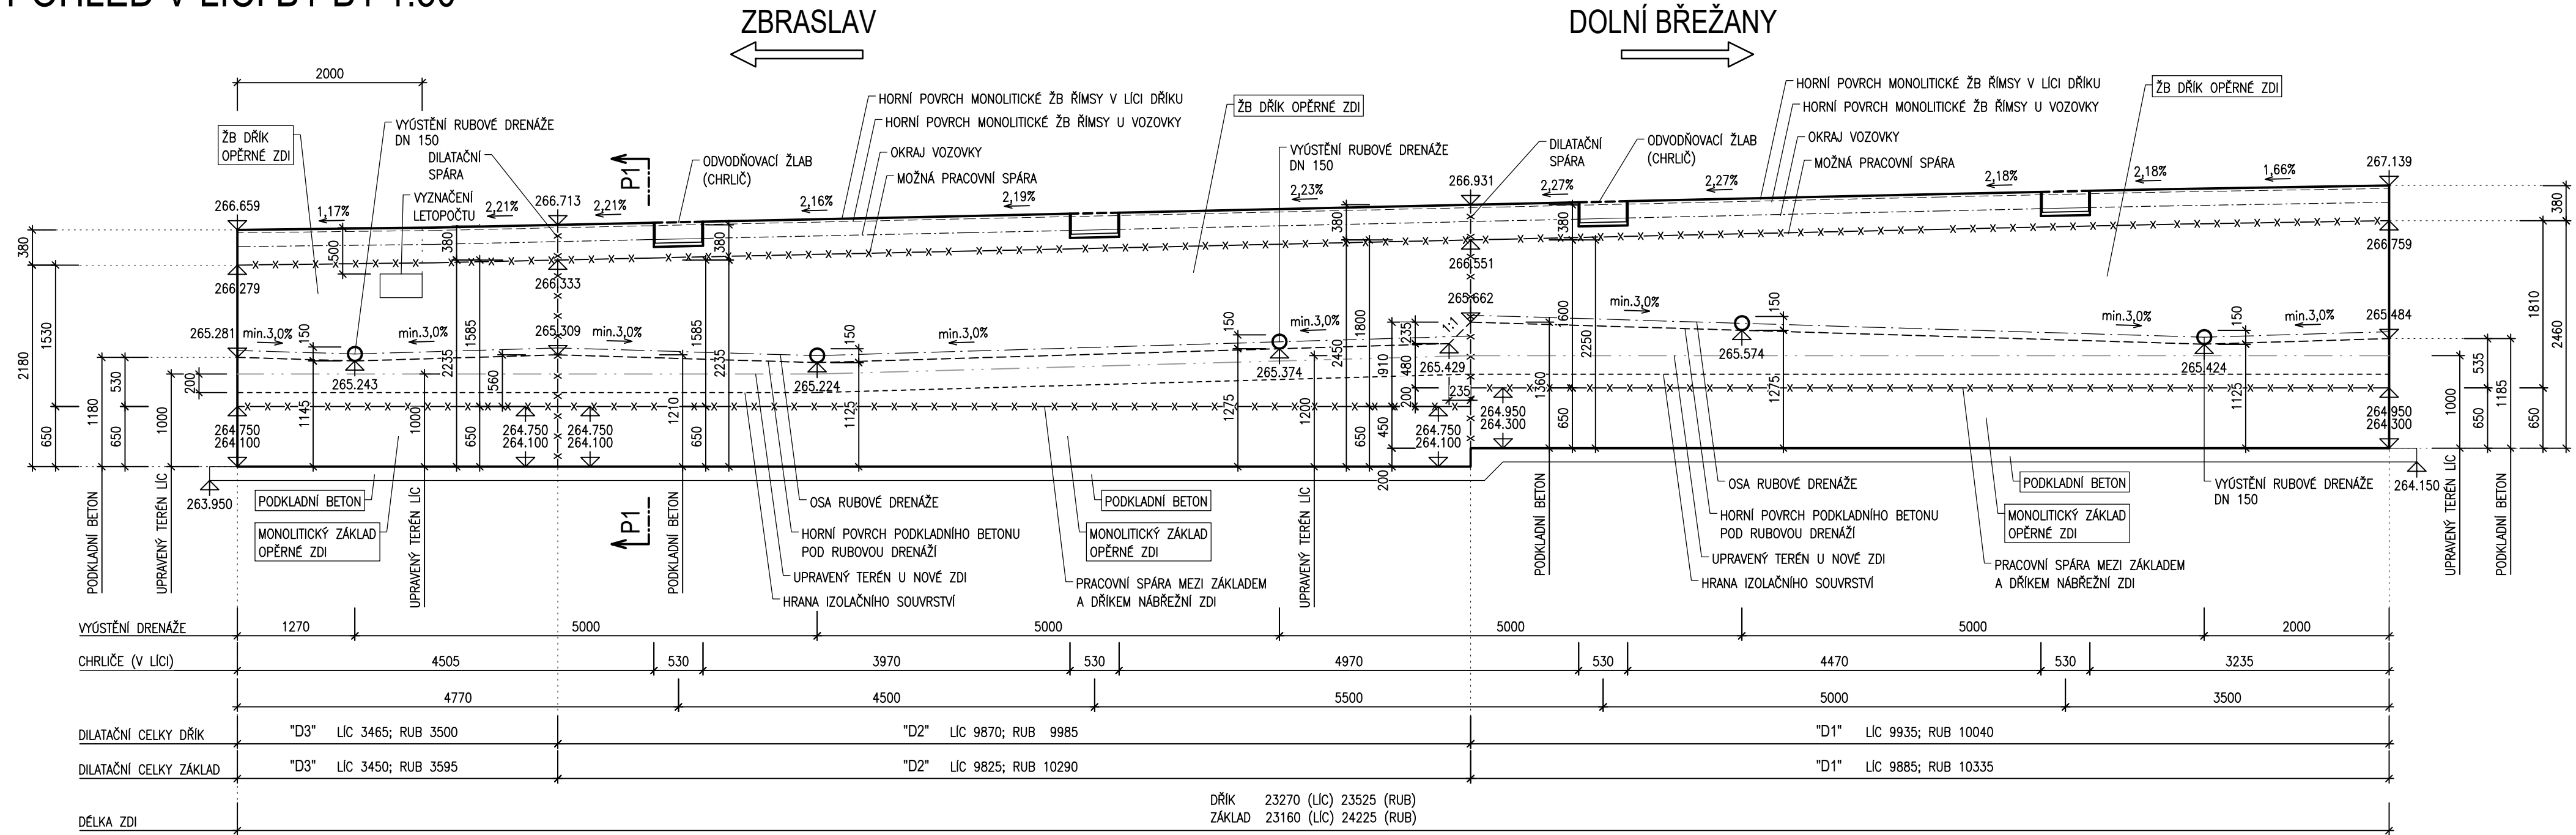

PŮDORYS 1:100

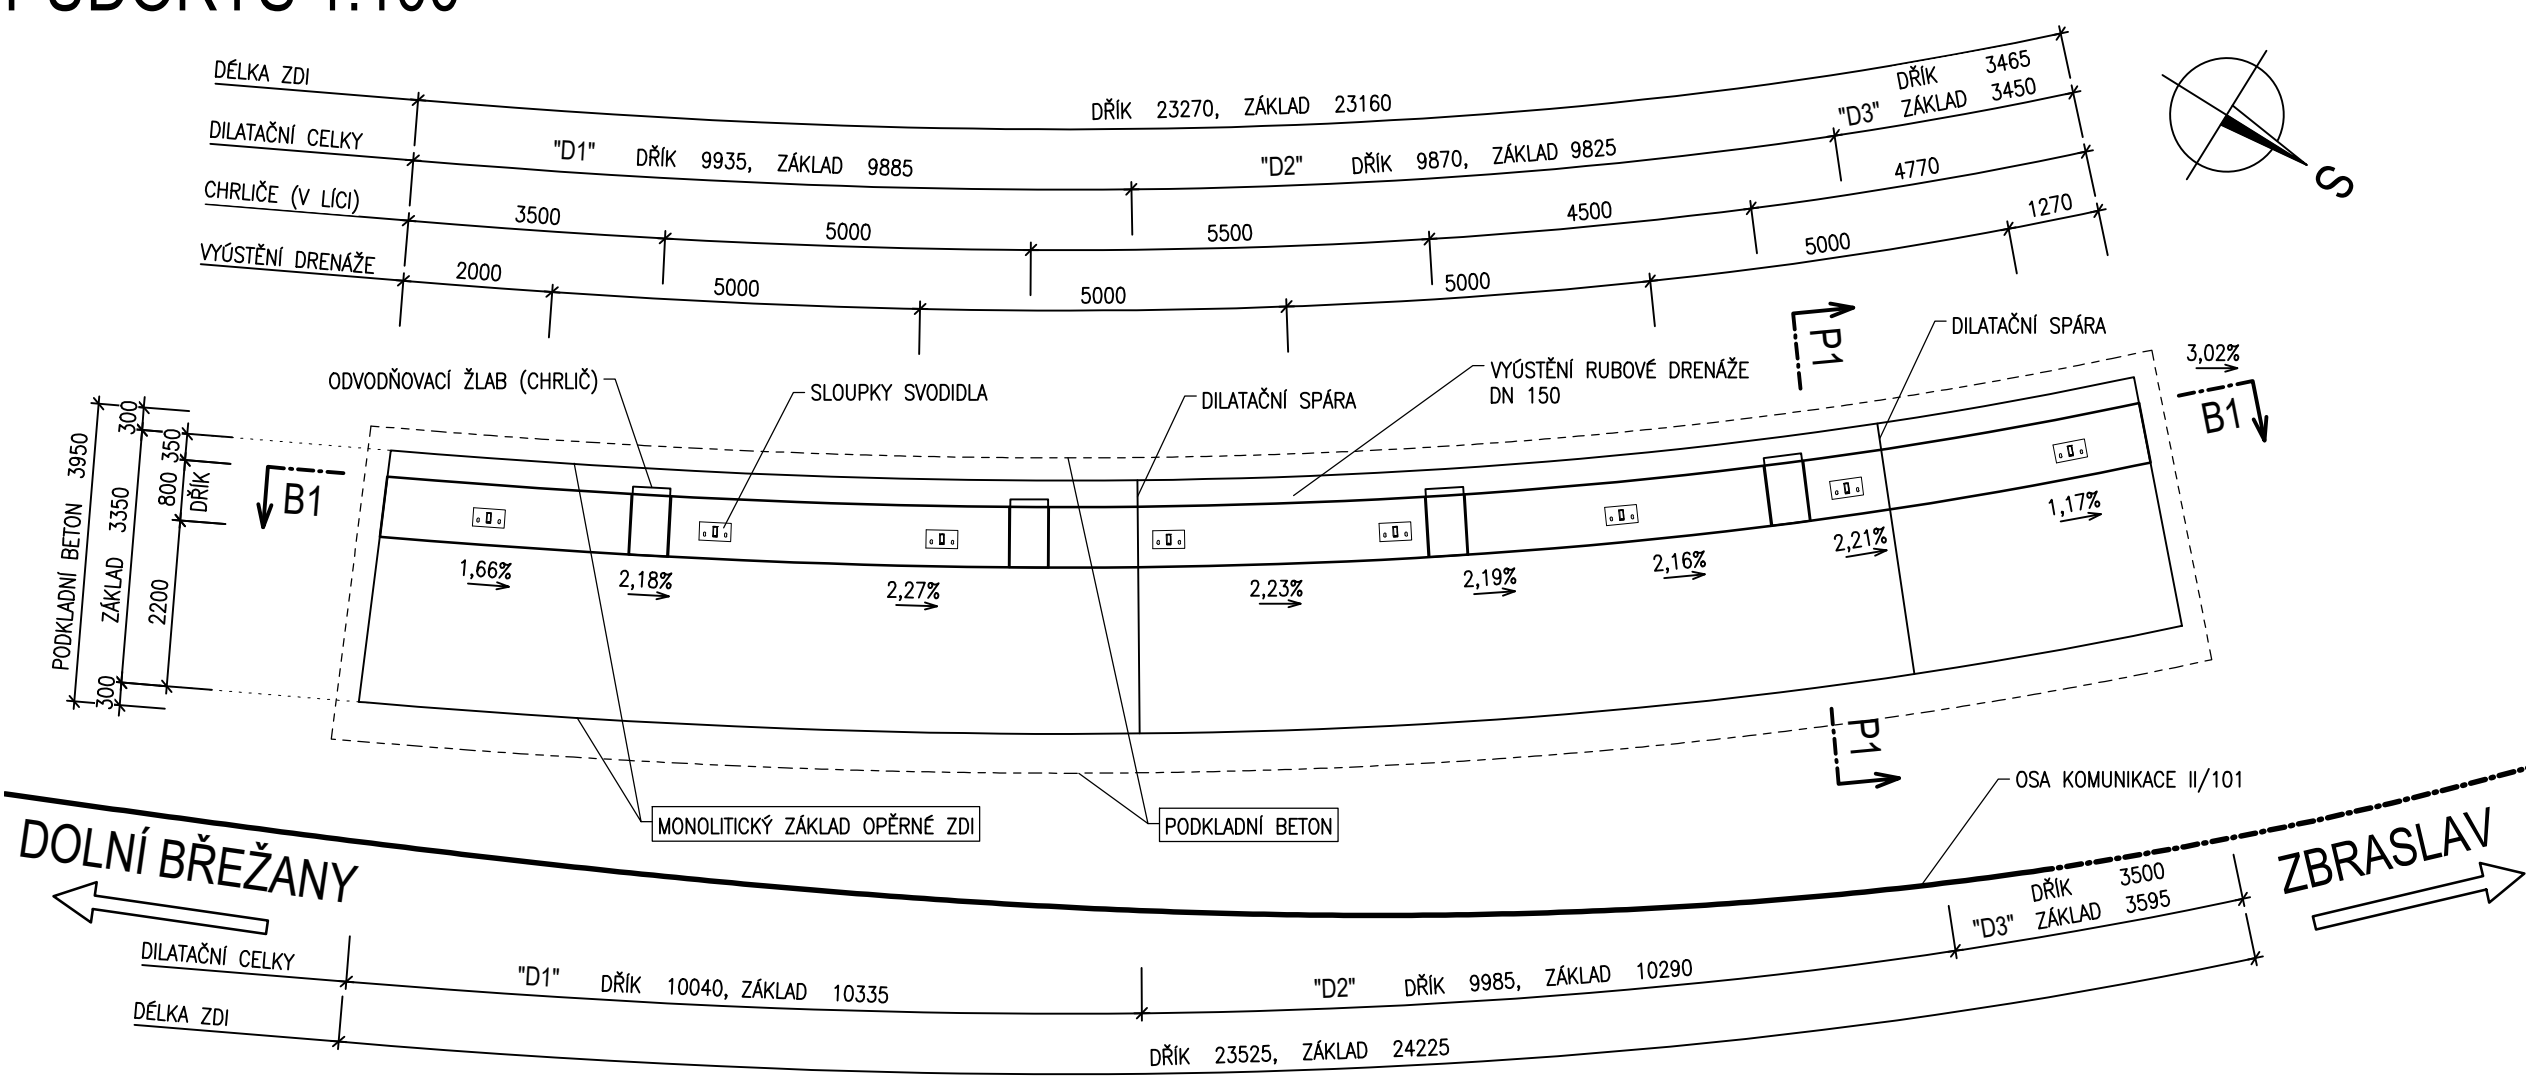

VYZNAČENÍ LETOPOČTU 1:5

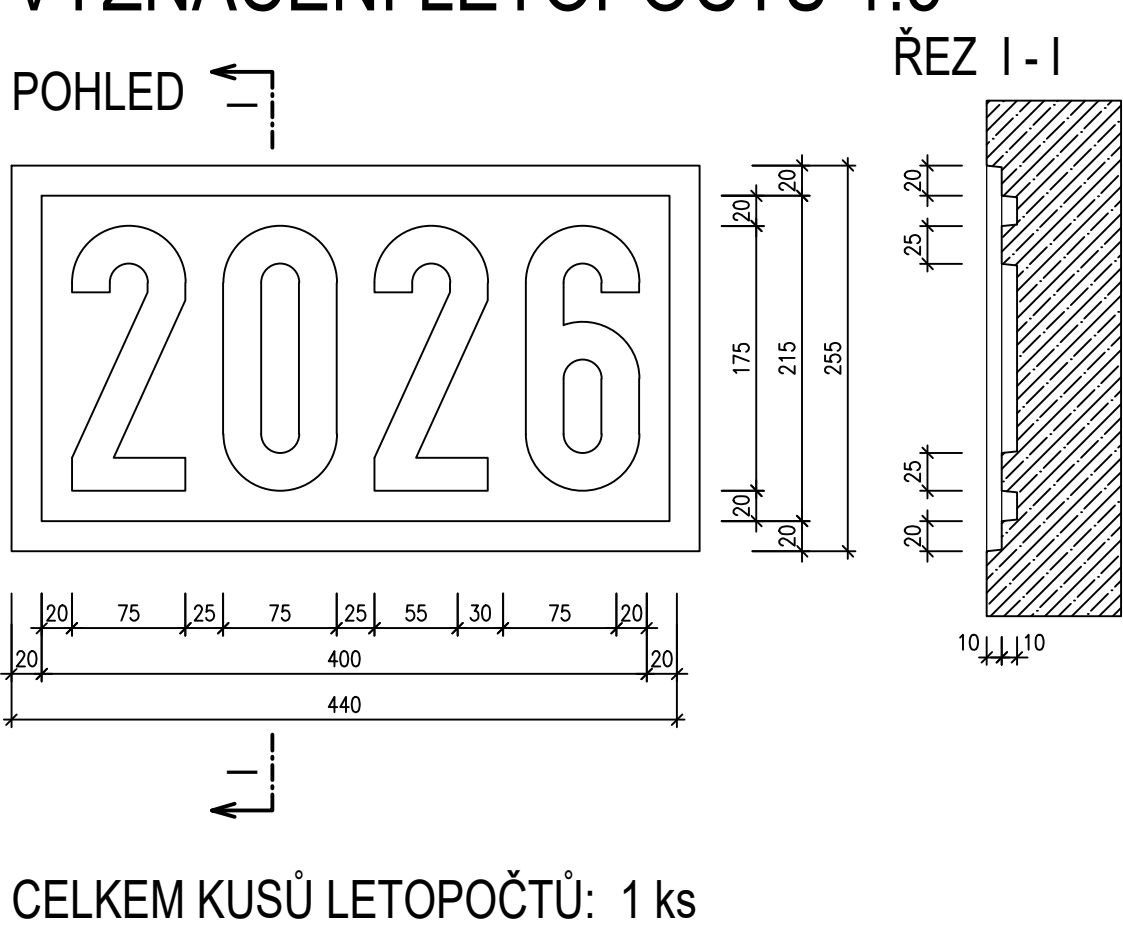

STAVEBNÍ MATERIÁLY

BETONOVÉ BUDOVY PROVEDENY DLE ČSN EN 206  
KONSTRUKCE BETONOVY:  
ZB ZÁKLAD  
ZB DŘÍK

**C30/37** XD2, XF2, XC2 (CZ.F.1.2) – CI 0,2; D<sub>max</sub> 22 – S3  
**C30/37** XD3, XF4, XC4 (CZ.F.1.2) – CI 0,2; D<sub>max</sub> 22 – S3

OSTATNÍ BETONOVY:  
PODKLADNÍ BETON  
PODKLADNÍ BETON – RUBOVÁ DRENÁŽ  
PODKLADNÍ BETON – SCHODIŠTĚ, DLAŽBY  
BETONOVÉ PRAHY

**C12/15** X0 (CZ.F.1.2) – CI 1,0; D<sub>max</sub> 22 – S3  
**C8/10** X0 (CZ.F.1.2) – CI 1,0; D<sub>max</sub> 22 – S3  
**C20/25** XF3, XD2 (CZ.F.1.2) – CI 0,2; D<sub>max</sub> 22 – S3  
**C30/37** XF4, XD3 (CZ.F.1.2) – CI 0,2; D<sub>max</sub> 22 – S3

BETONÁŘSKÁ VÝZTUŽ:  
OCEL

**B500B**

PRACOVNÍ, DILATAČNÍ SPÁRY A TĚSNĚNÍ

PENETRAČNÍ NÁTĚR

– KOMPONENTNÍ AKTIVNÍ NÁTĚR NA BÁZI EPOXIDU – POLYURETANOVÁ PRYSKYŘICE  
OBJEMOVÁ HMOTNOST 1,8 kg/l  
– VÍSKOŽITA 10–15 MPa.s  
– BOD VZPLAMUTÍ < 21 °C


TĚSNÍCÍ TMEL dle ČSN EN ISO 11600 (F-25-HM-M1p), barva šedá

– F – stavební (konstrukční) tmel  
– 25 – třída tmele dle tab.1  
– HM – die sekantového modulu tužnosti vysokomodulový  
– M1p – tmel zkoušen na podkladní maltě s penetrací

Tmel musí vyhovovat požadavkům dle ČSN EN ISO 11600 tab.3 a tab.4.


Pro těsnění je navržena elastická 1–komponentní tmeleci hmota:  
– báze tmele polyuretanová vytvrzující vzdušnou vlhkostí  
– objemová hmotnost ~1,3 kg/l  
– mez protažení cca. 400%  
– pevnost v tahu 1,5 N/mm2  
– pevnost v roztržení 7 N/mm2  
– modul pružnosti E ~0,6 N/mm2 (po 28 dnech) při teplotě –20 °C  
– tepelná odolnost – 40 °C až + 80 °C  
– tvrdost Shore A 35

PŘÍČNÝ ŘEZ P1-P1 km 1,760 000 1:25

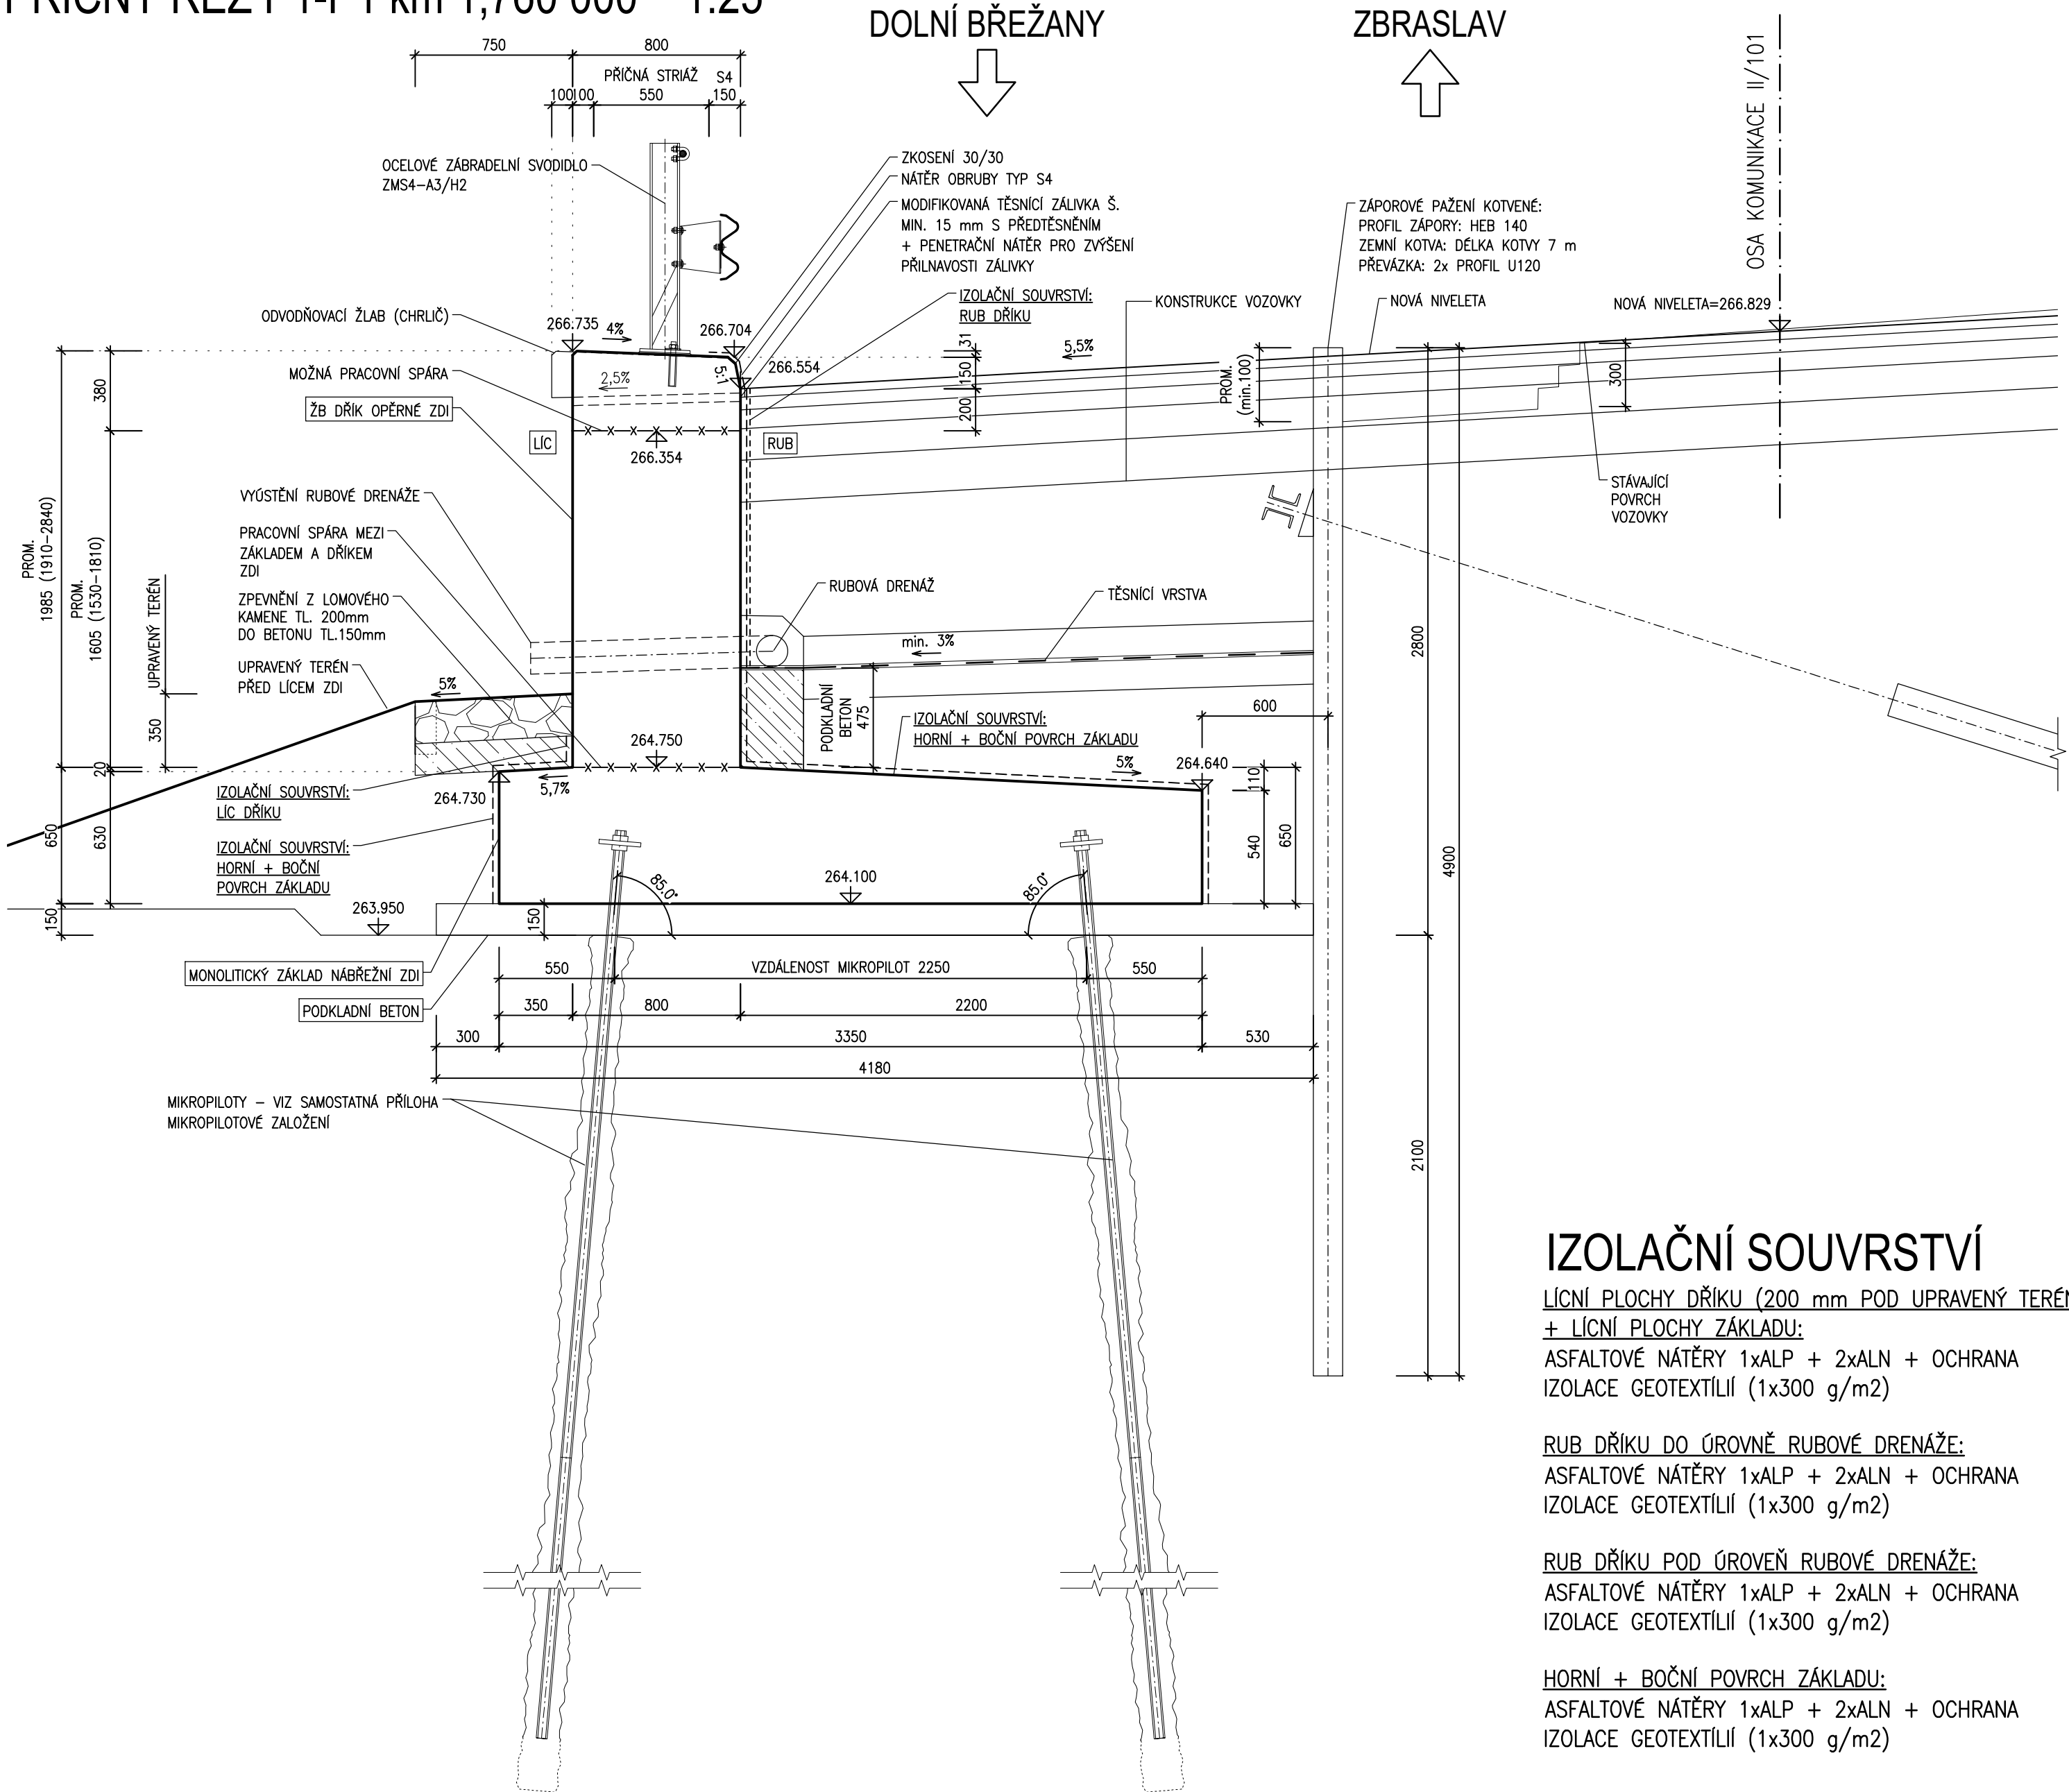


DETAIL PROSTUPU RUBOVÉ DRENÁŽE

ŘEZ DŘÍKEM ZDI 1:5

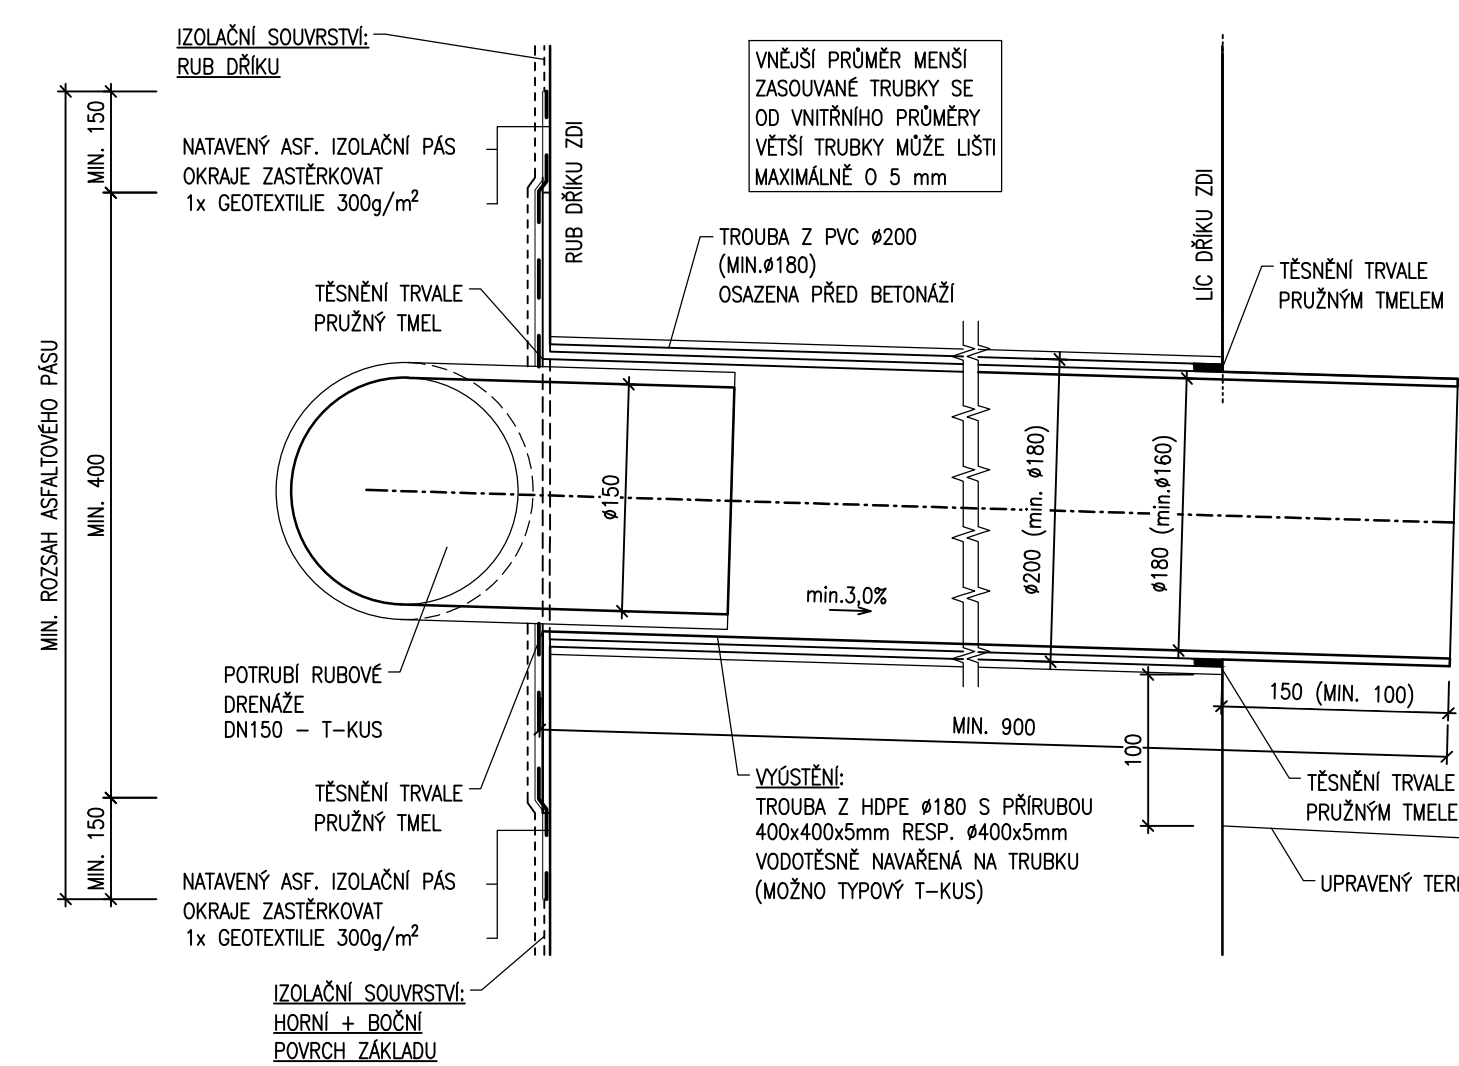


DETAIL ULOŽENÍ RUBOVÉ DRENÁŽE

ŘEZ RUBOVU DRENÁŽÍ ZA RUBEM 1:10

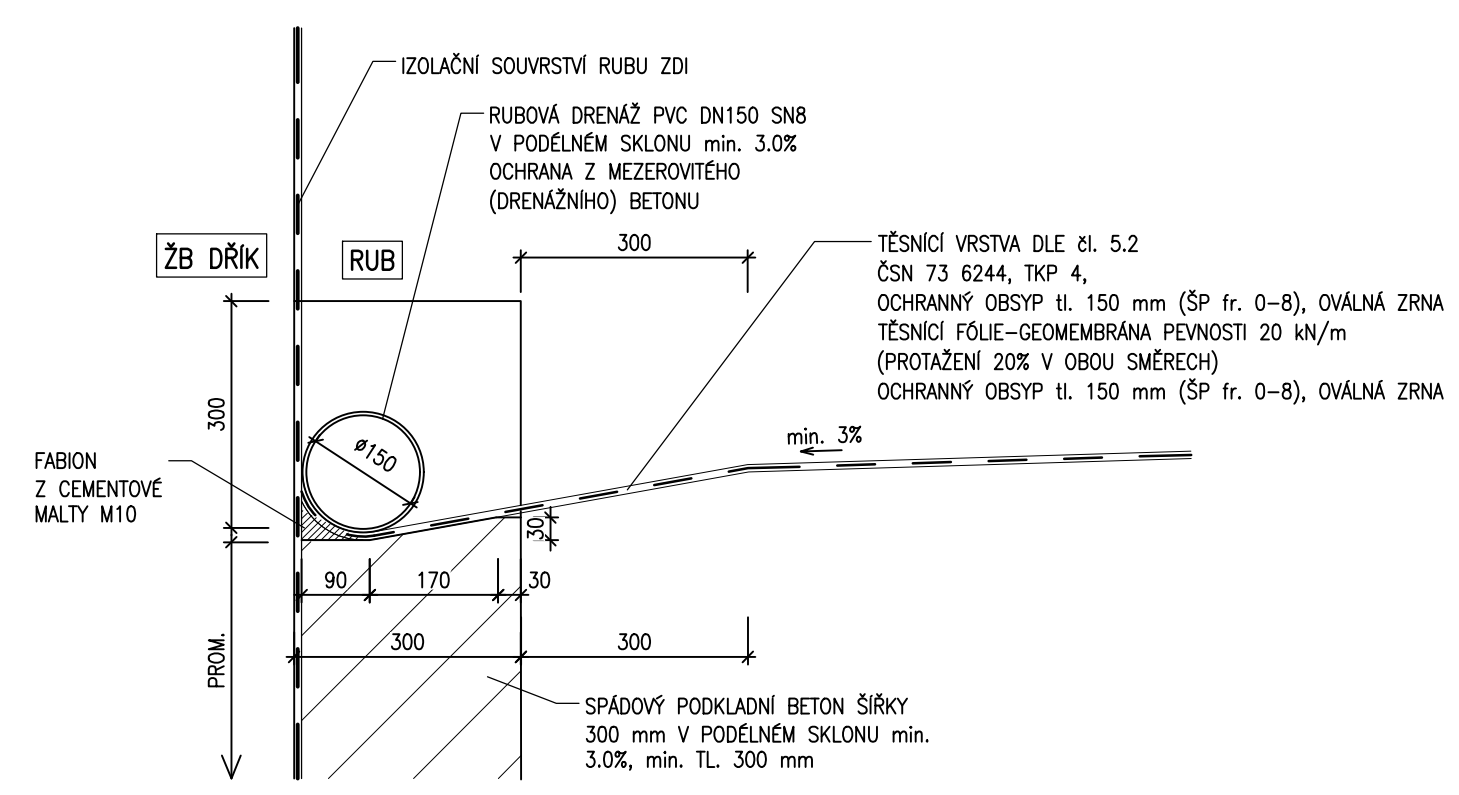


ODVODŇOVACÍ ŽLAB (CHRLIČ)

PŘÍČNÝ ŘEZ ŽLABEM 1:10

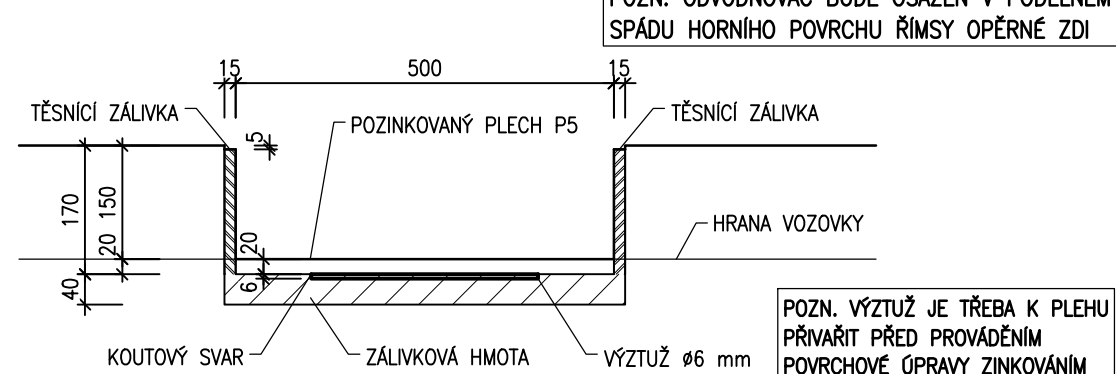


PODÉLNÝ ŘEZ ŽLABEM 1:10

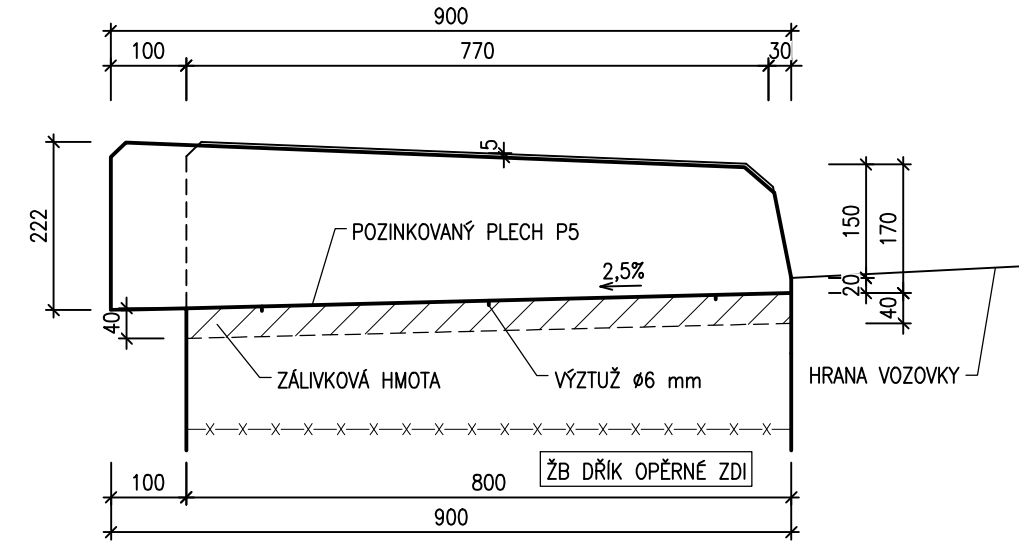

ODVODŇOVACÍ ŽLAB (CHRLIČ)

PŮDORYS ŽLABU 1:25

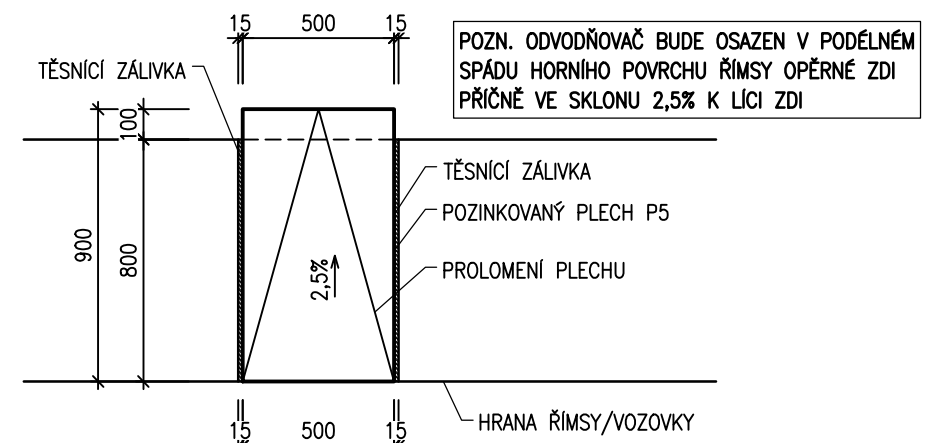

CELKEM KUSŮ CHRLIČŮ: 4 ks

PŘEDKONCEPT

|        |                         |       |        |
|--------|-------------------------|-------|--------|
|        |                         |       |        |
|        |                         |       |        |
| OZNAČ. | TEXT ZMĚNY – ODŮVODNĚNÍ | DATUM | PODPIS |

|              |                                 |               |          |
|--------------|---------------------------------|---------------|----------|
| Název stavby | II/101 Dolní Břežany - Zbraslav | ČÍSLO OBJEKTU | SO 251.2 |
|--------------|---------------------------------|---------------|----------|

|                   |   |
|-------------------|---|
| Objednatel stavby | Krajská správa a údržba silnic Středočeského kraje, příspěvková organizace Zborovská 811/11, 150 21 Praha 5-Smíchov |
|-------------------|---|

|                |                                                  |
|----------------|--------------------------------------------------|
| Autorský dozor | GeoTec-GS, a.s. Chmelová 2920/6, 106 00 Praha 10 |
|----------------|--------------------------------------------------|

|                           |   |         |       |        |
|---------------------------|---|---------|-------|--------|
| Technický dozor investora | TES + SGS + SGG vedoucí sdružení: TES Consulting, s.r.o. V Olšanské 2300/75, 100 00 Praha 10-Strašnice | RAZÍTKO | DATUM | PODPIS |
|---------------------------|---|---------|-------|--------|

|                   |                                                              |         |       |        |
|-------------------|--------------------------------------------------------------|---------|-------|--------|
| Zhotovitel stavby | M-SILNICE a.s. Husova 1697, 530 03 Pardubice www.msilnice.cz | RAZÍTKO | DATUM | PODPIS |
|-------------------|--------------------------------------------------------------|---------|-------|--------|

|                 |                                                                               |         |       |        |
|-----------------|-------------------------------------------------------------------------------|---------|-------|--------|
| Koordinator RDS | M - PROJEKCE s. r.o. Reslova 956/13, 500 02 Hradec Králové www.m-projeckce.cz | RAZÍTKO | DATUM | PODPIS |
|-----------------|-------------------------------------------------------------------------------|---------|-------|--------|

|                             |                     |
|-----------------------------|---------------------|
| Souřadnicový systém: S-JTSK | Výškový systém: Bpv |
|-----------------------------|---------------------|

|                                       |                                                                                            |
|---------------------------------------|--------------------------------------------------------------------------------------------|
| Zpracovatel stavebního objektu/části: | Projektční kancelář PRIS spol. s r.o. Osova 717/20, 625 00 Brno-Starý Lískovec www.pris.cz |
|---------------------------------------|--------------------------------------------------------------------------------------------|

|                                          |                                                |                                                             |
|------------------------------------------|------------------------------------------------|-------------------------------------------------------------|
| Vypracoval: Iona Sýnková                 | Hlavní inženýr projektu: Ing. Jiří Ehrenberger | Razítko: PRIS                                               |
| Odpovědný projektant: Ing. Martin Reuška | Kontroloval: Ing. Jiří ŠRUBAR                  | PROJEKČNÍ KANCELÁŘ PRIS spol. s r. o. OSOVA 20, 625 00 BRNO |
| Číslo zakázky: 25-122-02                 | Datum: 06/2026                                 |                                                             |

|                                              |                                 |           |
|----------------------------------------------|---------------------------------|-----------|
| Objekt/část: SO 251.2 - OPĚRNÉ ZDI ZED č. 10 | Měřítko: 1:100; 1:50; 1:25; 1:5 | Souprava: |
| Příloha: TVAR OPĚRNÉ ZDI                     | Stupeň: RDS                     |           |
|                                              | Číslo přílohy: 105_TV9          |           |