



TVAR ZDI – ZEĎ Č. 04


POHLED 1:200

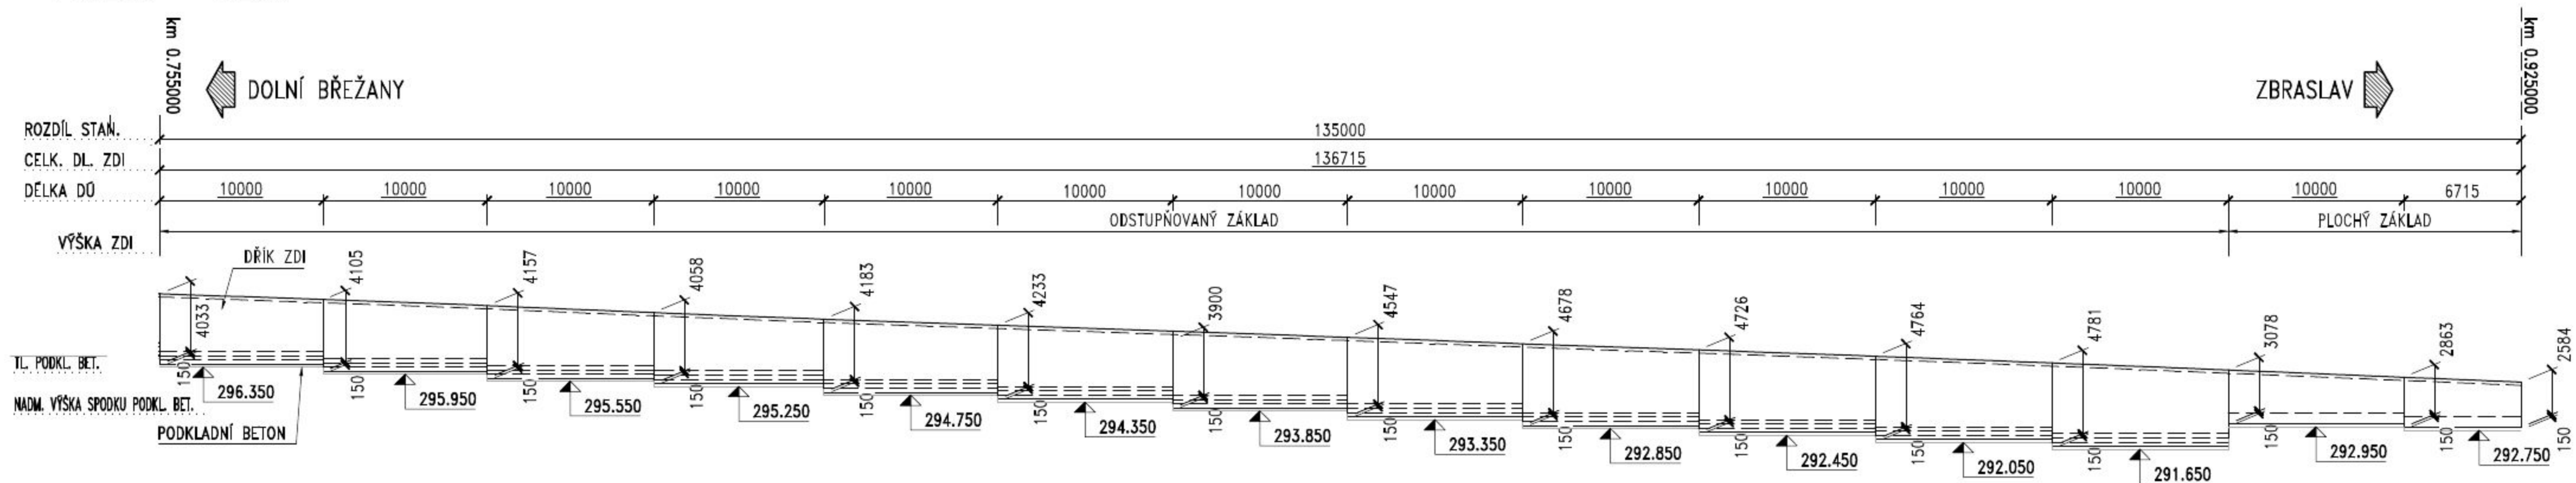


PŮDORYS 1:200

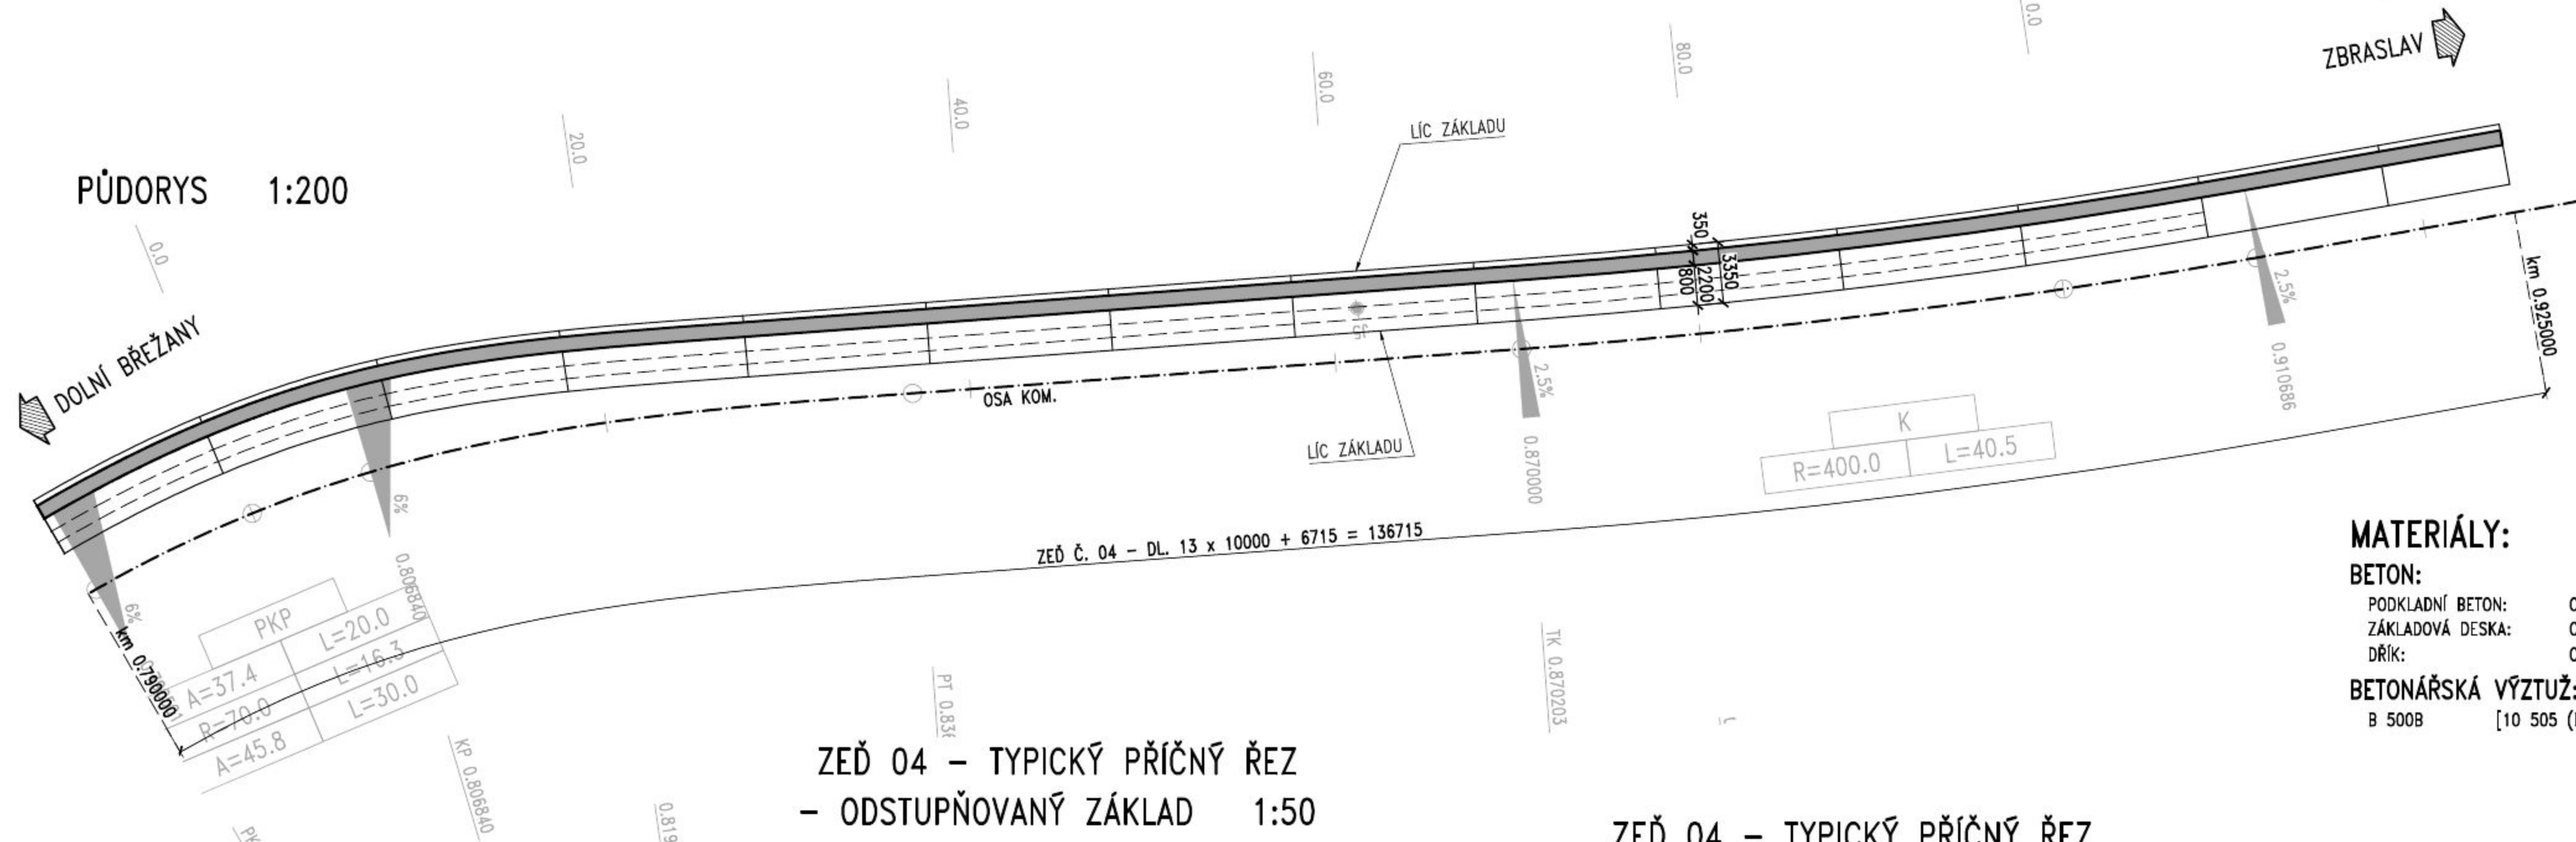

ZEĎ 04 – TYPICKÝ PŘÍČNÝ ŘEZ
– ODSTUPŇOVANÝ ZÁKLAD 1:50

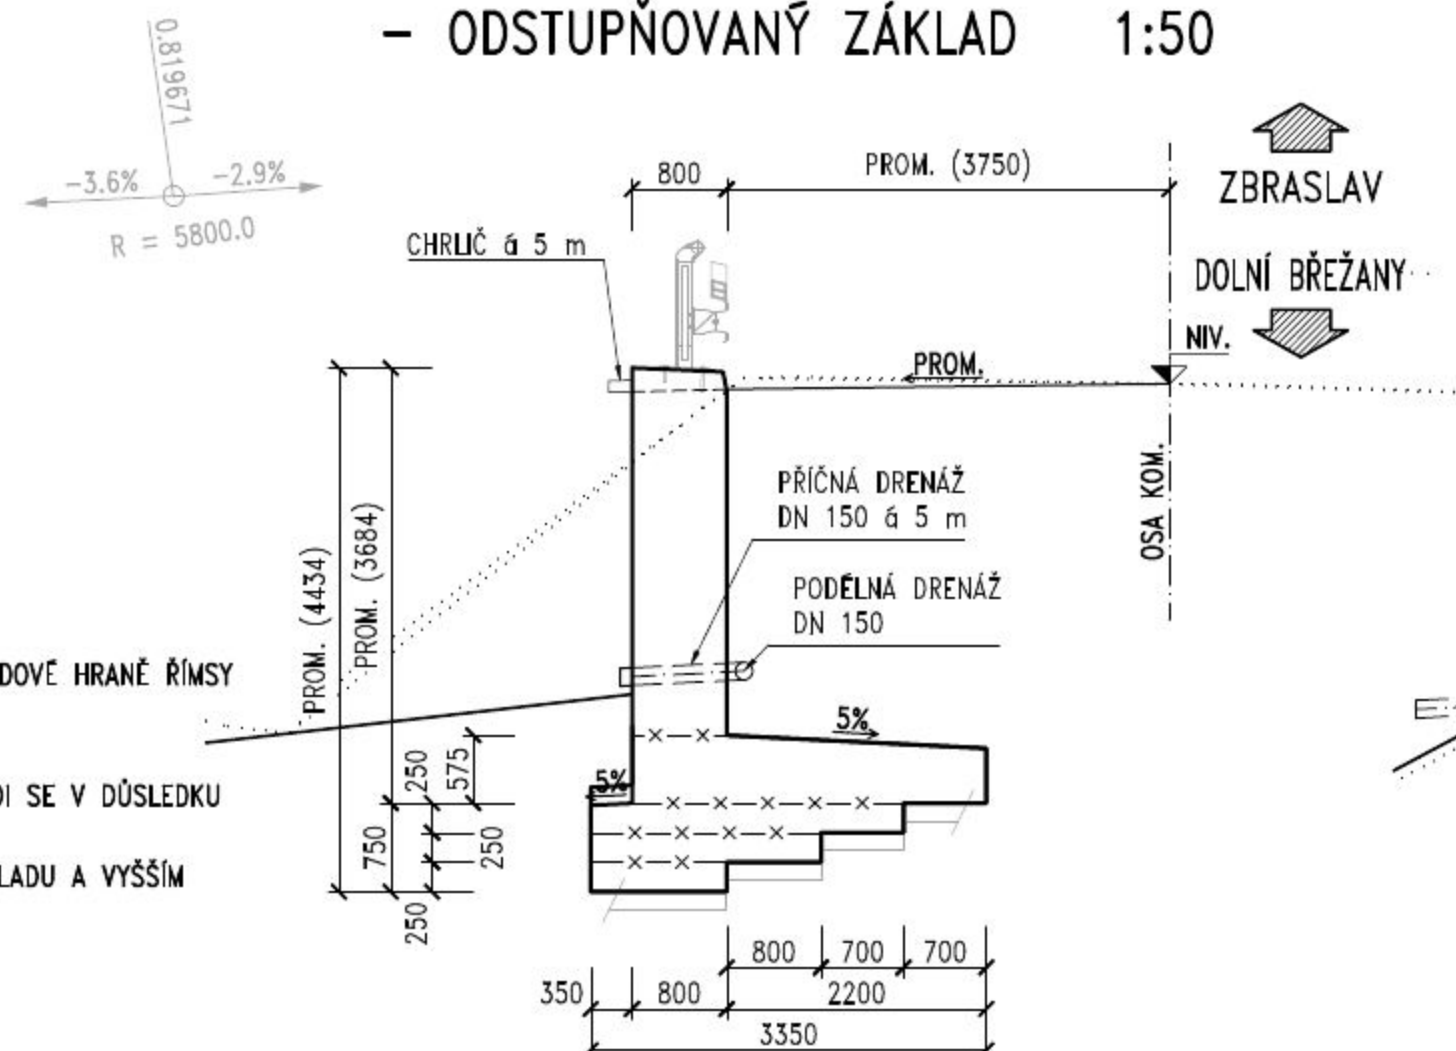

ZEĎ 04 – TYPICKÝ PŘÍČNÝ ŘEZ
– PLOCHÝ ZÁKLAD 1:50

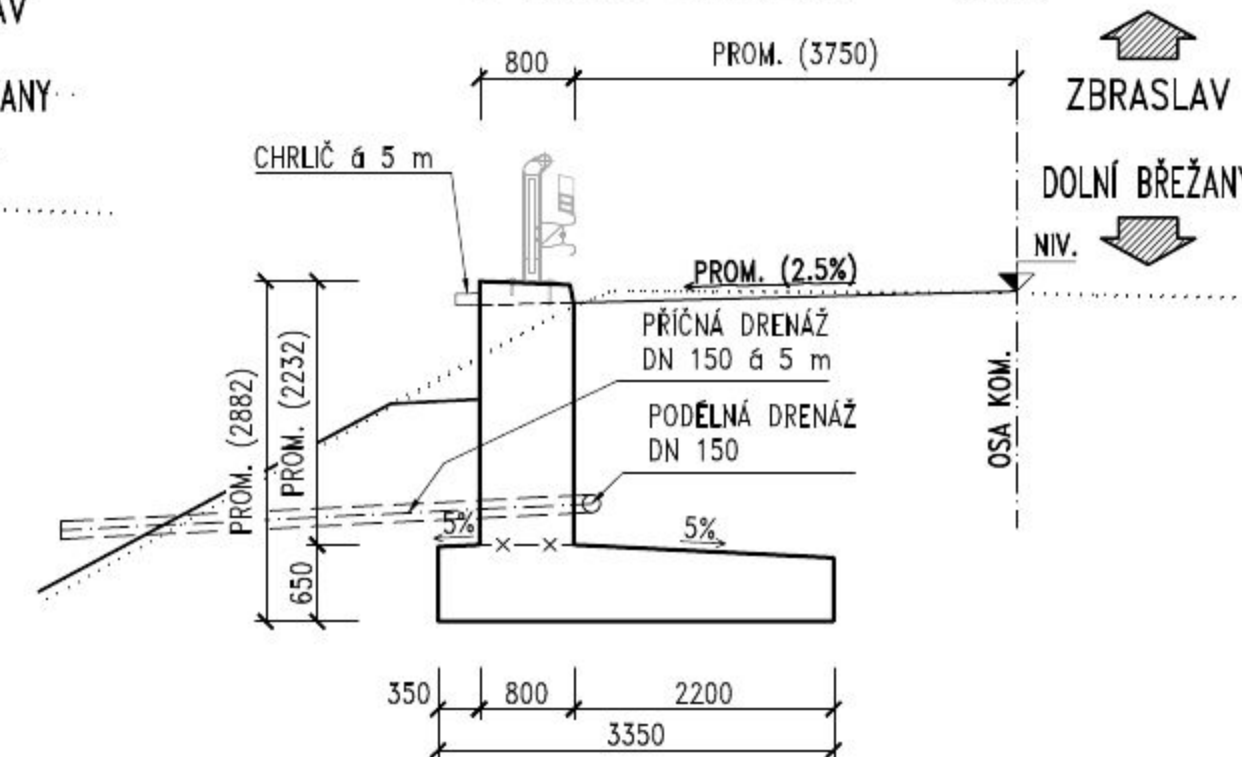

POZNÁMKY:

- 1) "D0" = DILATAČNÍ ÚSEK.
- 2) VODOROVNÉ DÉLKY (NAPŘ. "DÉLKA ZDI") MĚŘENY V NÁJEZDOVÉ HRANĚ ŘÍMSY (= V RUBU DŘÍKU) ZDI.
- 3) STANIČENÍ MĚŘENO V OSE KOMUNIKACE.
- 4) ROZDÍL STANIČENÍ A DÉLKY V NÁJEZDOVÉ HRANĚ ŘÍMSY ZDI SE V DŮSLEDKU PŮDORYSNÉHO ZAKRIVĚNÍ LIŠÍ.
- 5) KÓTY VÝŠKY ZDI VE VNĚJŠÍM LÍCI, T.J. MEZI SPODKEM ZÁKLADU A VYŠŠÍM OKRAJEM ŘÍMSOVÉ ČÁSTI.

MATERIÁLY:

BETON:

- PODKLADNÍ BETON: C 12/15 X0
ZÁKLADOVÁ DESKA: C 30/37 XF4/XD3/XC4
DŘÍK: C 30/37 XF4/XD3/XC4

BETONÁŘSKÁ VÝTUŽ:

- B 500B [10 505 (R)]

ZMENŠENO NA 50 %

ČÁST 2

VÝŠKOVÝ SYSTÉM Bpv SOUŘADNICOVÝ SYSTÉM S-JTSK

Ksús
KRAJSKÁ SPRÁVA A ÚDRŽBA SILNIC
Středočeského kraje, příspěvková organizace
Zborovská 81/11, 150 21 Praha 5 - Smíchov

GeoTec GS
Krajská správa a údržba silnic
Chmelová 2920/6, 106 00 Praha 10
tel.: +420 271 750 710
e-mail: praha@geotec-gs.cz

Vypracoval: Ing. Lukáš PROCHÁZKA
Odpovědný projektant: Ing. Pavel HRDINA
Schválil: Mgr. Filip DUDÍK
Číslo zakázky: 2017 - 395
Datum: 04/2024

Název akce: II/101 Dolní Břežany - Zbraslav
Objekt: TVAR ZDI – ZEĎ Č. 04
Měřítko: D.1.2.1
Formát: 7-04