TVAR ZDI – ZEĎ Č. 05

POHLED 1:200

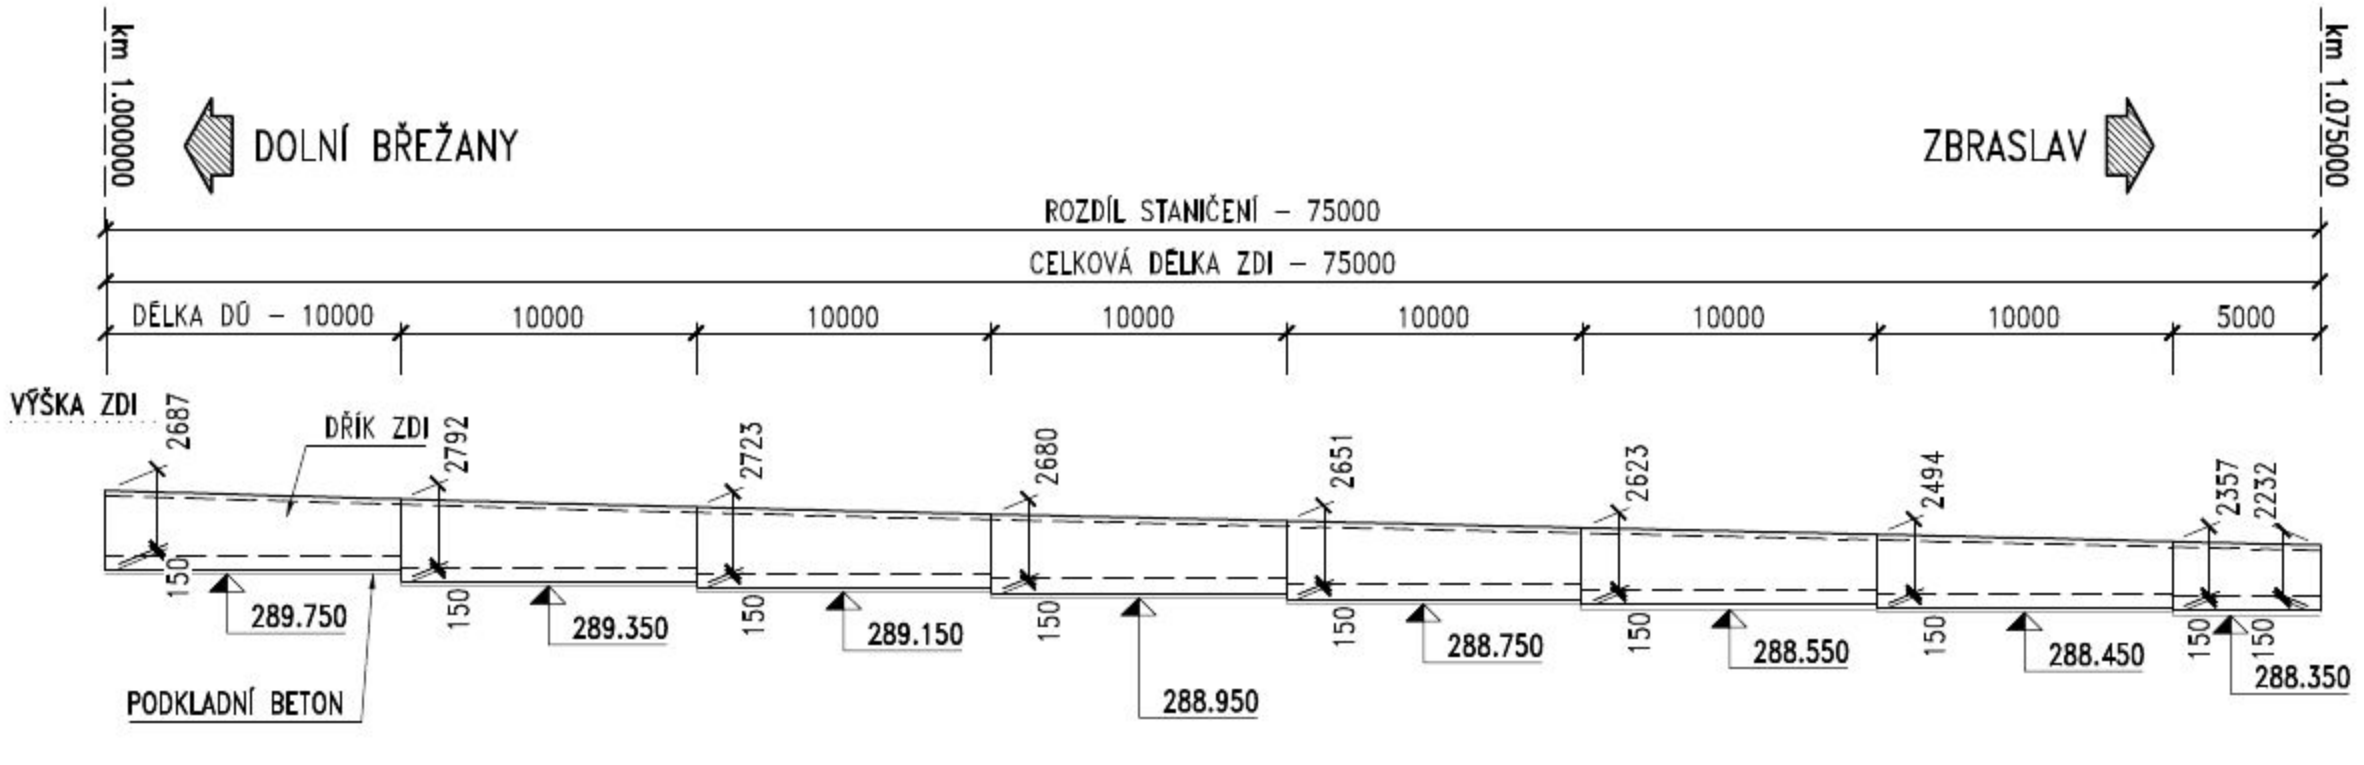

PŮDORYS 1:200

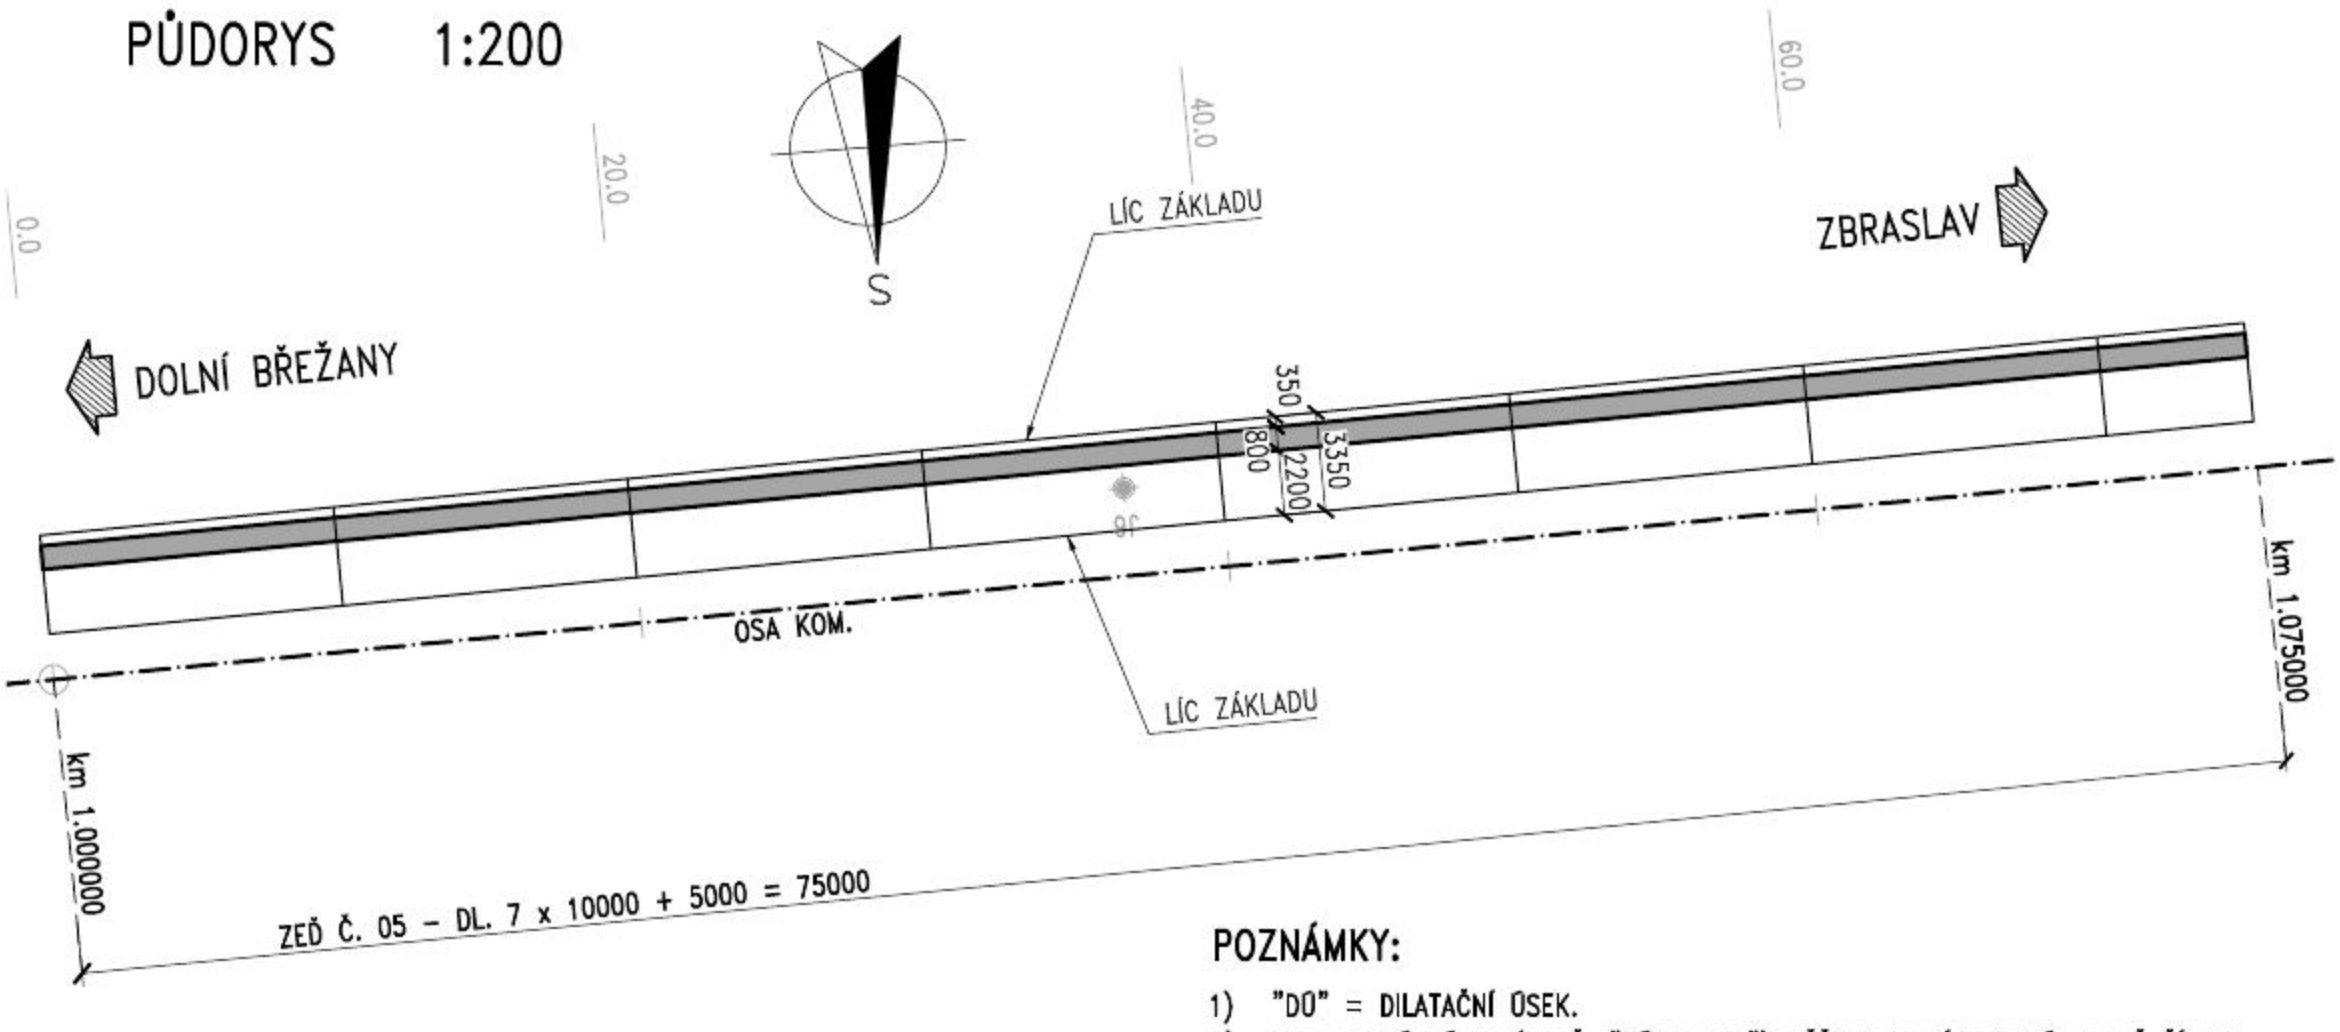

POZNÁMKY:

1) "DÚ" = DILATAČNÍ ÚSEK.
2) VODOROVNÉ DÉLKY (NAPŘ. "DÉLKA ZDI") MĚŘENY V NÁJEZDOVÉ HRANĚ ŘÍMSY (= V RUBU DŘÍKU) ZDI.
3) STANIČENÍ MĚŘENO V OSE KOMUNIKACE.
4) ROZDÍL STANIČENÍ A DÉLKY V NÁJEZDOVÉ HRANĚ ŘÍMSY ZDI SE V DŮSLEDKU PŮDORYSNÉHO ZAKŘIVENÍ LIŠÍ.
5) KÓTY VÝŠKY ZDI VE VNĚJŠÍM LÍCI, TJ. MEZI SPODKEM ZÁKLADU A VYŠŠÍM OKRAJEM ŘÍMSOVÉ ČÁSTI.

ZEĎ 05 – TYPICKÝ PŘÍČNÝ ŘEZ 1:50

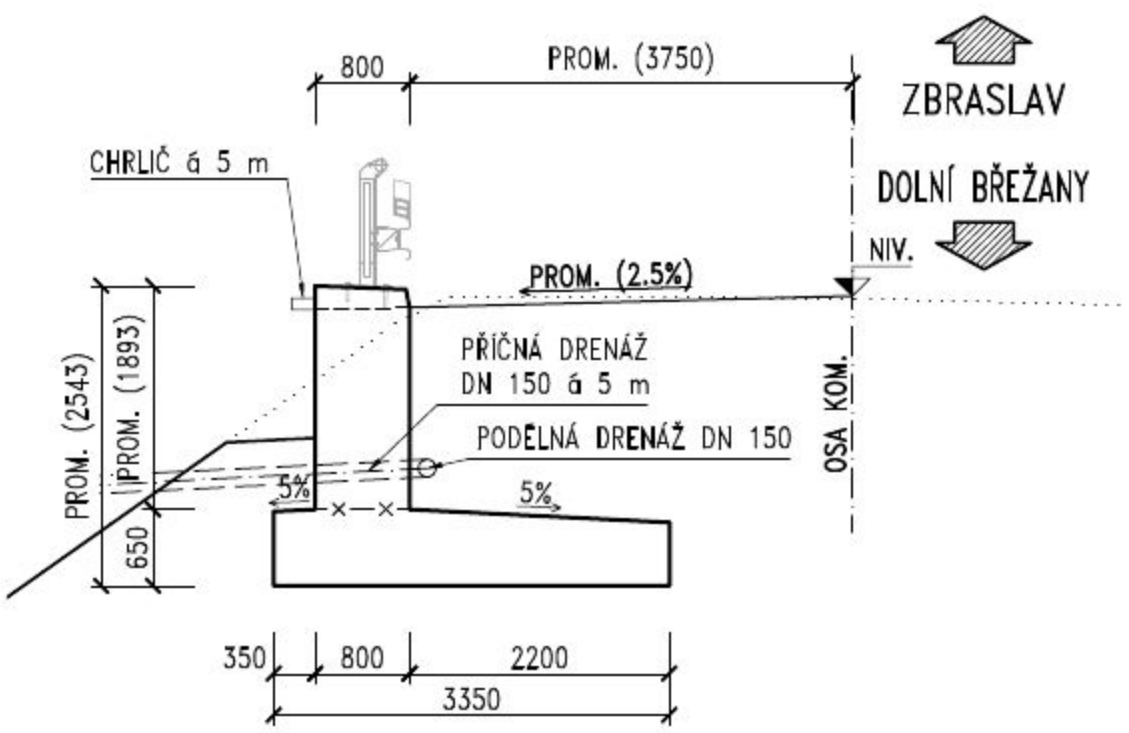

ZMENŠENO NA 50 %

ČÁST 2

VÝŠKOVÝ SYSTÉM Bpv SOUŘADNICOVÝ SYSTÉM S-JTSK

Objednatel:
SÚS KRAJSKÁ SPRÁVA A ÚDRŽBA SILNIC Středočeského kraje
Krajská správa a údržba silnic Středočeského kraje, příspěvková organizace
Zborovská 81/11, 150 21 Praha 5 - Smíchov

Zhotovitel:
GeoTec GS
GeoTec-GS, a.s.
Chmelová 2920/6, 106 00 Praha 10
tel.: +420 271 750 710
e-mail: praha@geotec-gs.cz

Vypracoval:	Odpovědný projektant:	Schválil:	Číslo zakázky:
Ing. Lukáš PROCHÁZKA	Ing. Pavel HRDINA	Mgr. Filip DUDÍK	2017 - 395
Podpis:	Podpis:	Podpis:	Datum: 04/2024

Název akce:	Měřítko:	Formát:
II/101 Dolní Břežany - Zbraslav	Stupeň: PDPS	Paré č.:
Objekt: TVAR ZDI – ZEĎ Č. 05	Příloha: D.1.2.1 7–05	