



POHLED 1:200


TVAR ZDI – ZEĎ Č. 06 – ČÁST 1

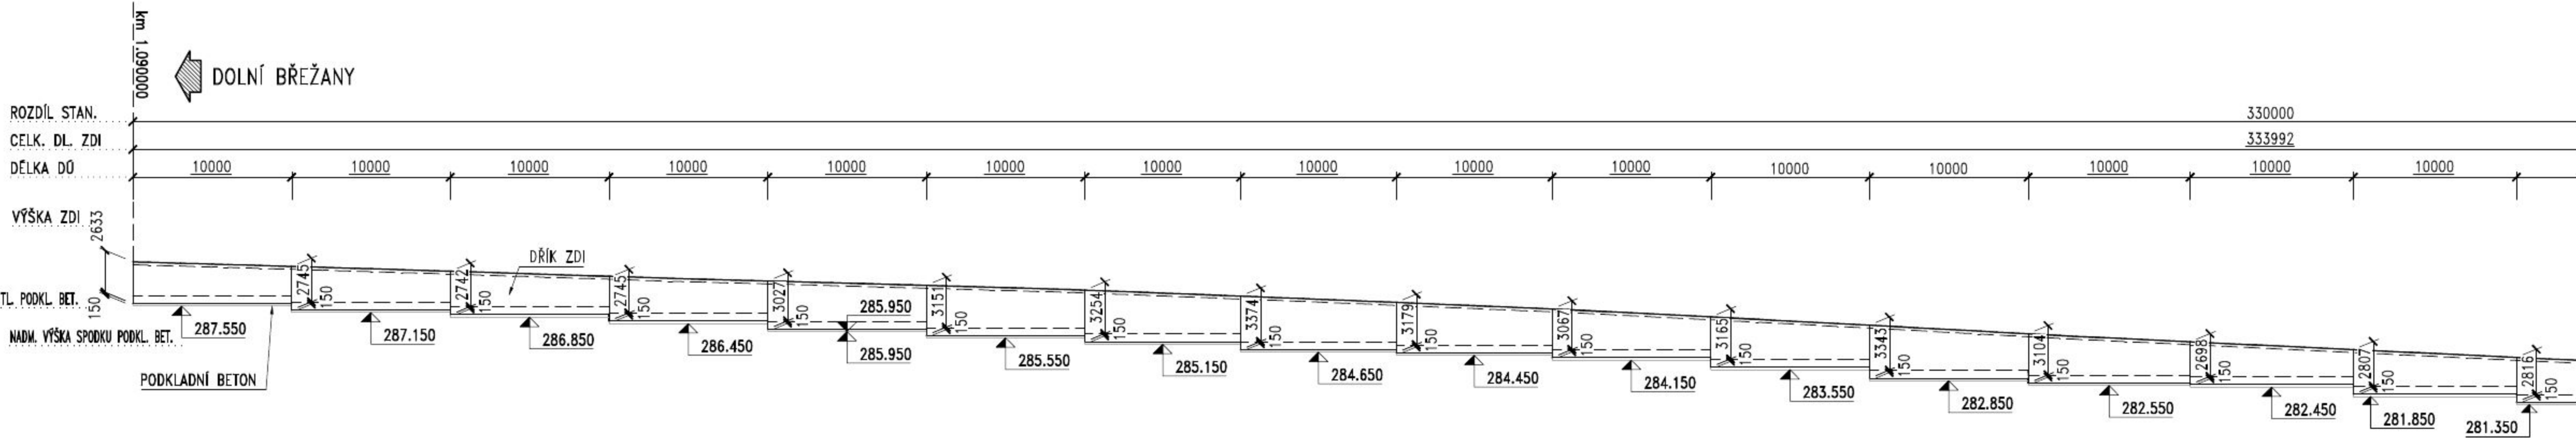

ZEĎ 06 – TYPICKÝ PŘÍČNÝ ŘEZ 1:50

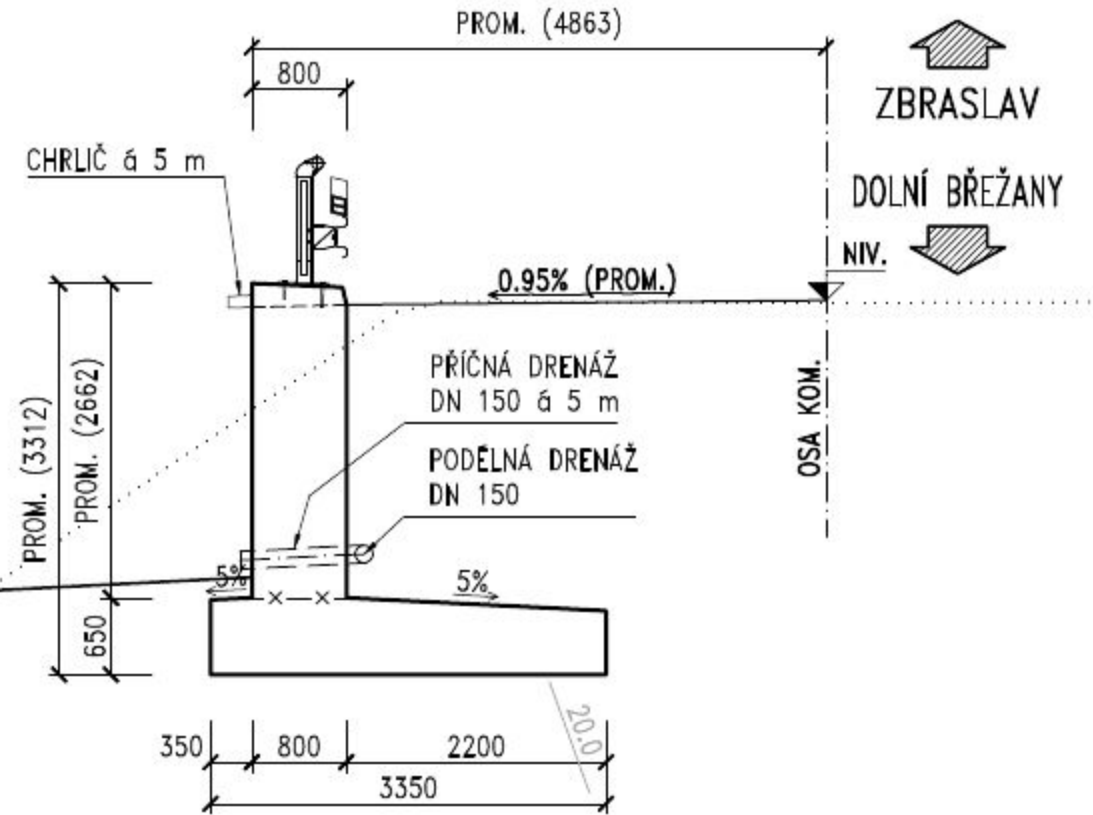

PŮDORYS 1:200

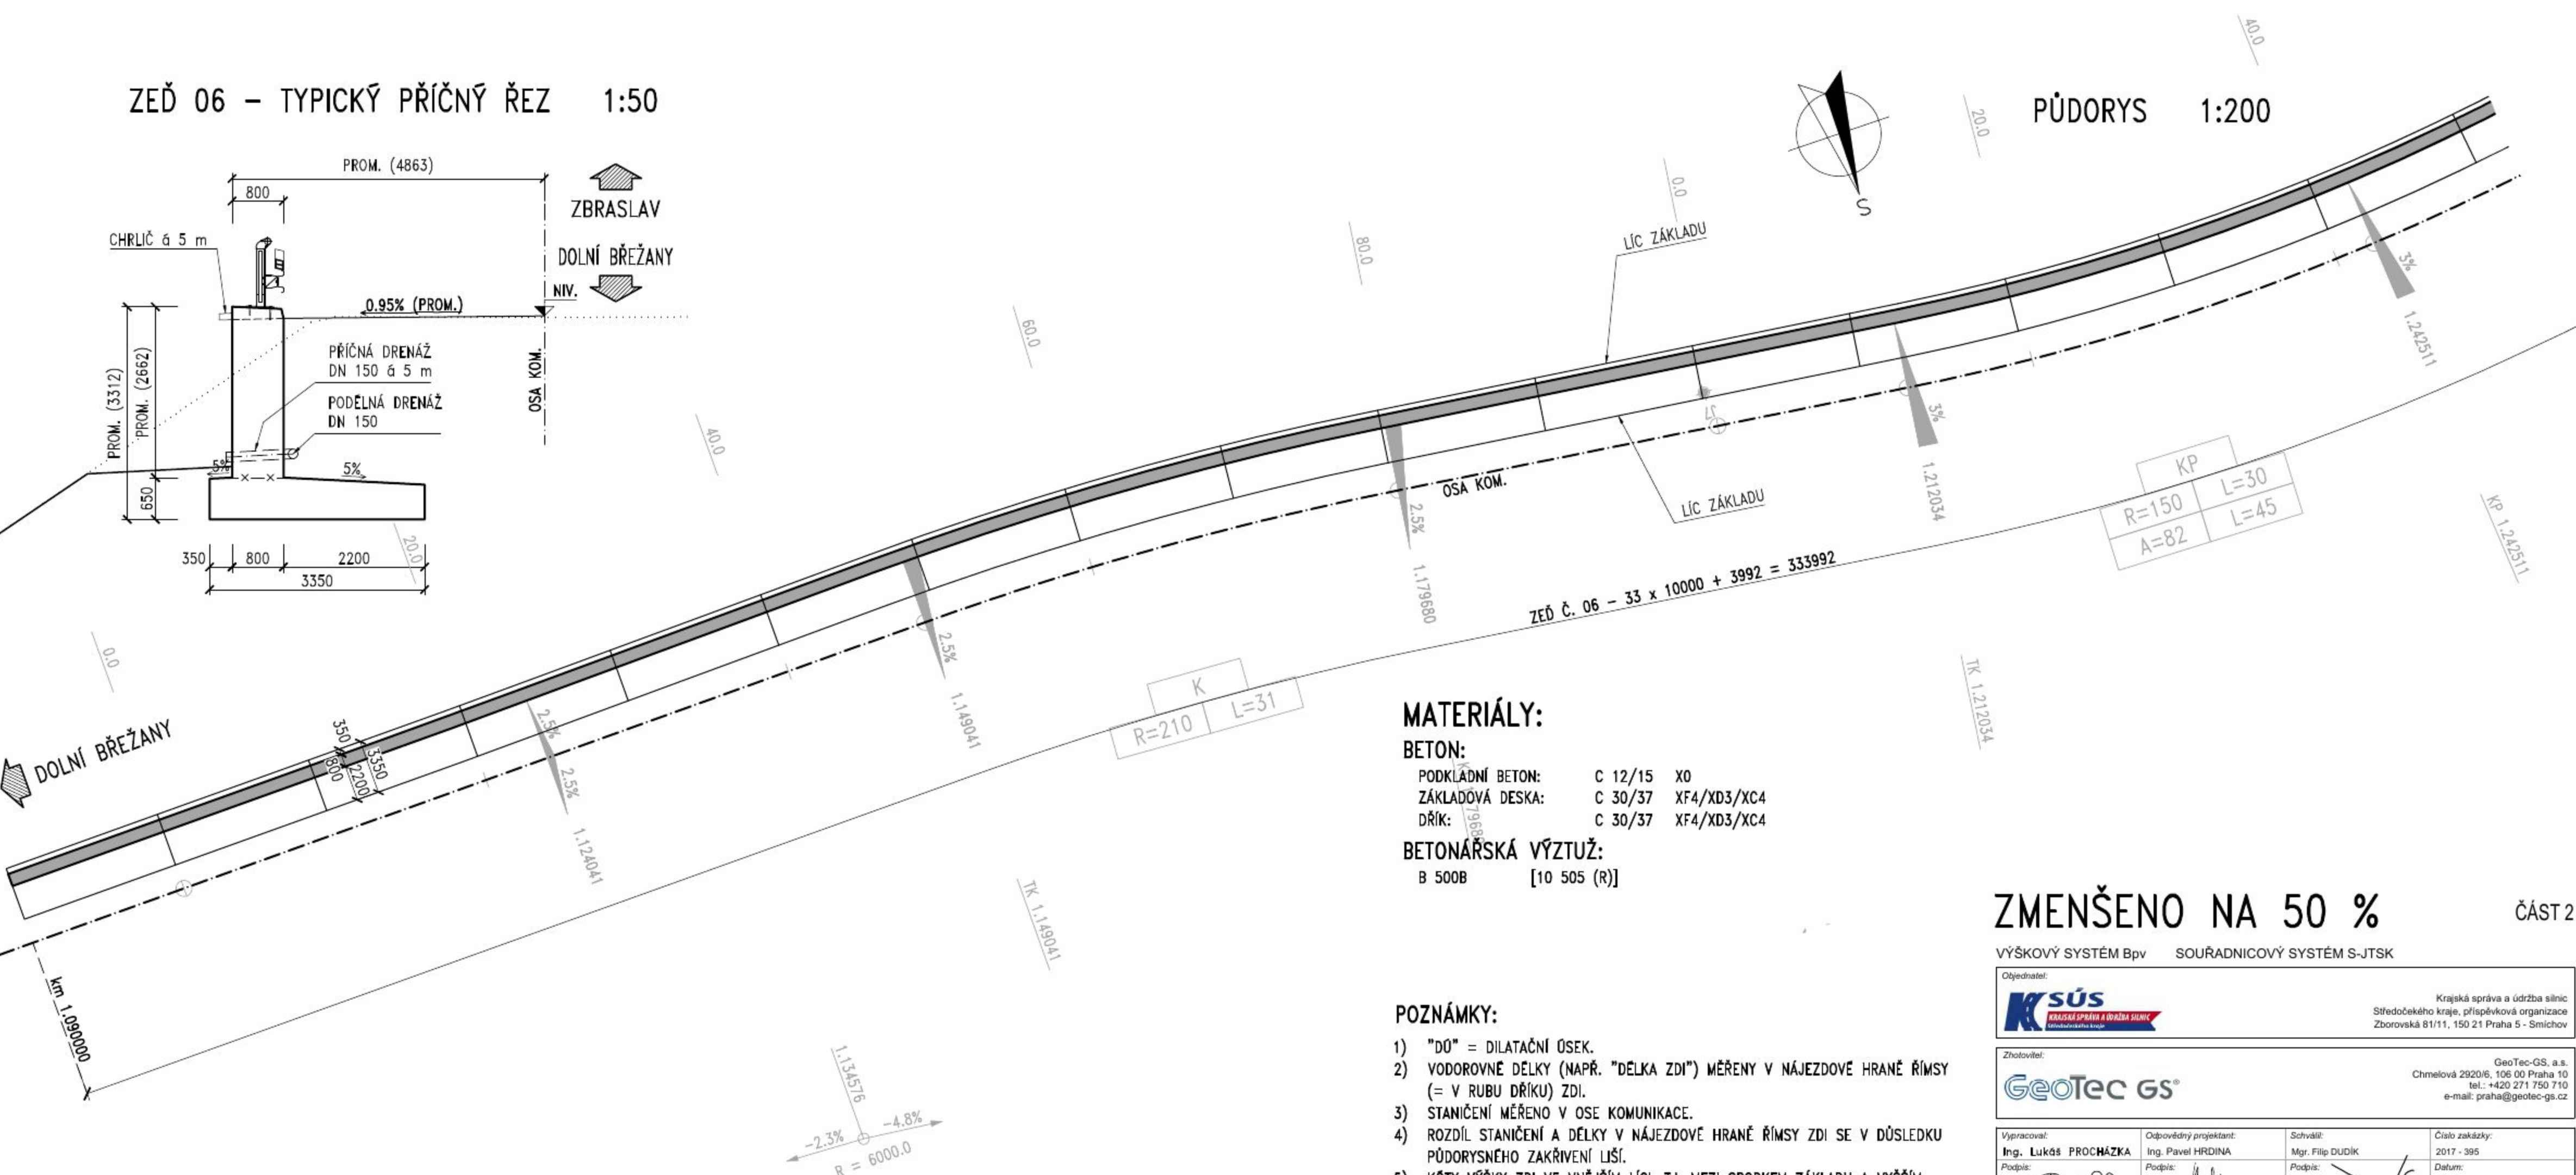

MATERIÁLY:

BETON:
PODKLADNÍ BETON: C 12/15 X0
ZÁKLADOVÁ DESKA: C 30/37 XF4/XD3/XC4
DŘÍK: C 30/37 XF4/XD3/XC4
BETONÁŘSKÁ VÝZTUŽ:
B 500B [10 505 (R)]

POZNÁMKY:

- "D0" = DILATAČNÍ OSEK.
- VODOROVNÉ DELKY (NAPŘ. "DELKA ZDI") MĚŘENY V NÁJEZDOVÉ HRANĚ ŘÍMSY (= V RUBU DŘÍKU) ZDI.
- STANIČNÍ MĚŘENO V OSE KOMUNIKACE.
- ROZDÍL STANIČNÍ A DELKY V NÁJEZDOVÉ HRANĚ ŘÍMSY ZDI SE V DŮSLEDKU PŮDORYSNEHO ZAKRÍVENÍ LIŠÍ.
- KÓTY VÝŠKY ZDI VE VNĚJŠÍM LÍCI, T.J. MEZI SPODKEM ZÁKLADU A VYŠŠÍM OKRAJEM ŘÍMSOVÉ ČÁSTI.


ZMENŠENO NA 50 %

ČÁST 2

VÝŠKOVÝ SYSTÉM BpV		SOUŘADNICOVÝ SYSTÉM S-JTSK	
Objednatel: K SÚS Krajská správa a údržba silnic Středočeského kraje, příspěvková organizace Zborovská 81/115, 150 21 Praha 5 - Smíchov		Zhotovitel: GeoTec GS Chmelová 2920/6, 106 00 Praha 10 tel.: +420 271 750 710 e-mail: praha@geotec-gs.cz	
Výpracovatel: Ing. Lukáš PROCHÁZKA Právník: Procházka		Odpovědný projektant: Ing. Pavel HRDINA Právník: Procházka	
Schválil: Mgr. Filip DUŠEK Právník: Procházka		Číslo zakázky: 2017 - 395 Datum: 04/2024	
Název akce: II/101 Dolní Břežany - Zbraslav		Měřítko: Státní: PDPS Přístroj: D 1.2.1 7-06-1	
Objekt: TVAR ZDI – ZEĎ Č. 06 – ČÁST 1		Formát: A4	

POHLED 1:225

TVAR ZDI – ZEĎ Č. 06 – ČÁST 2

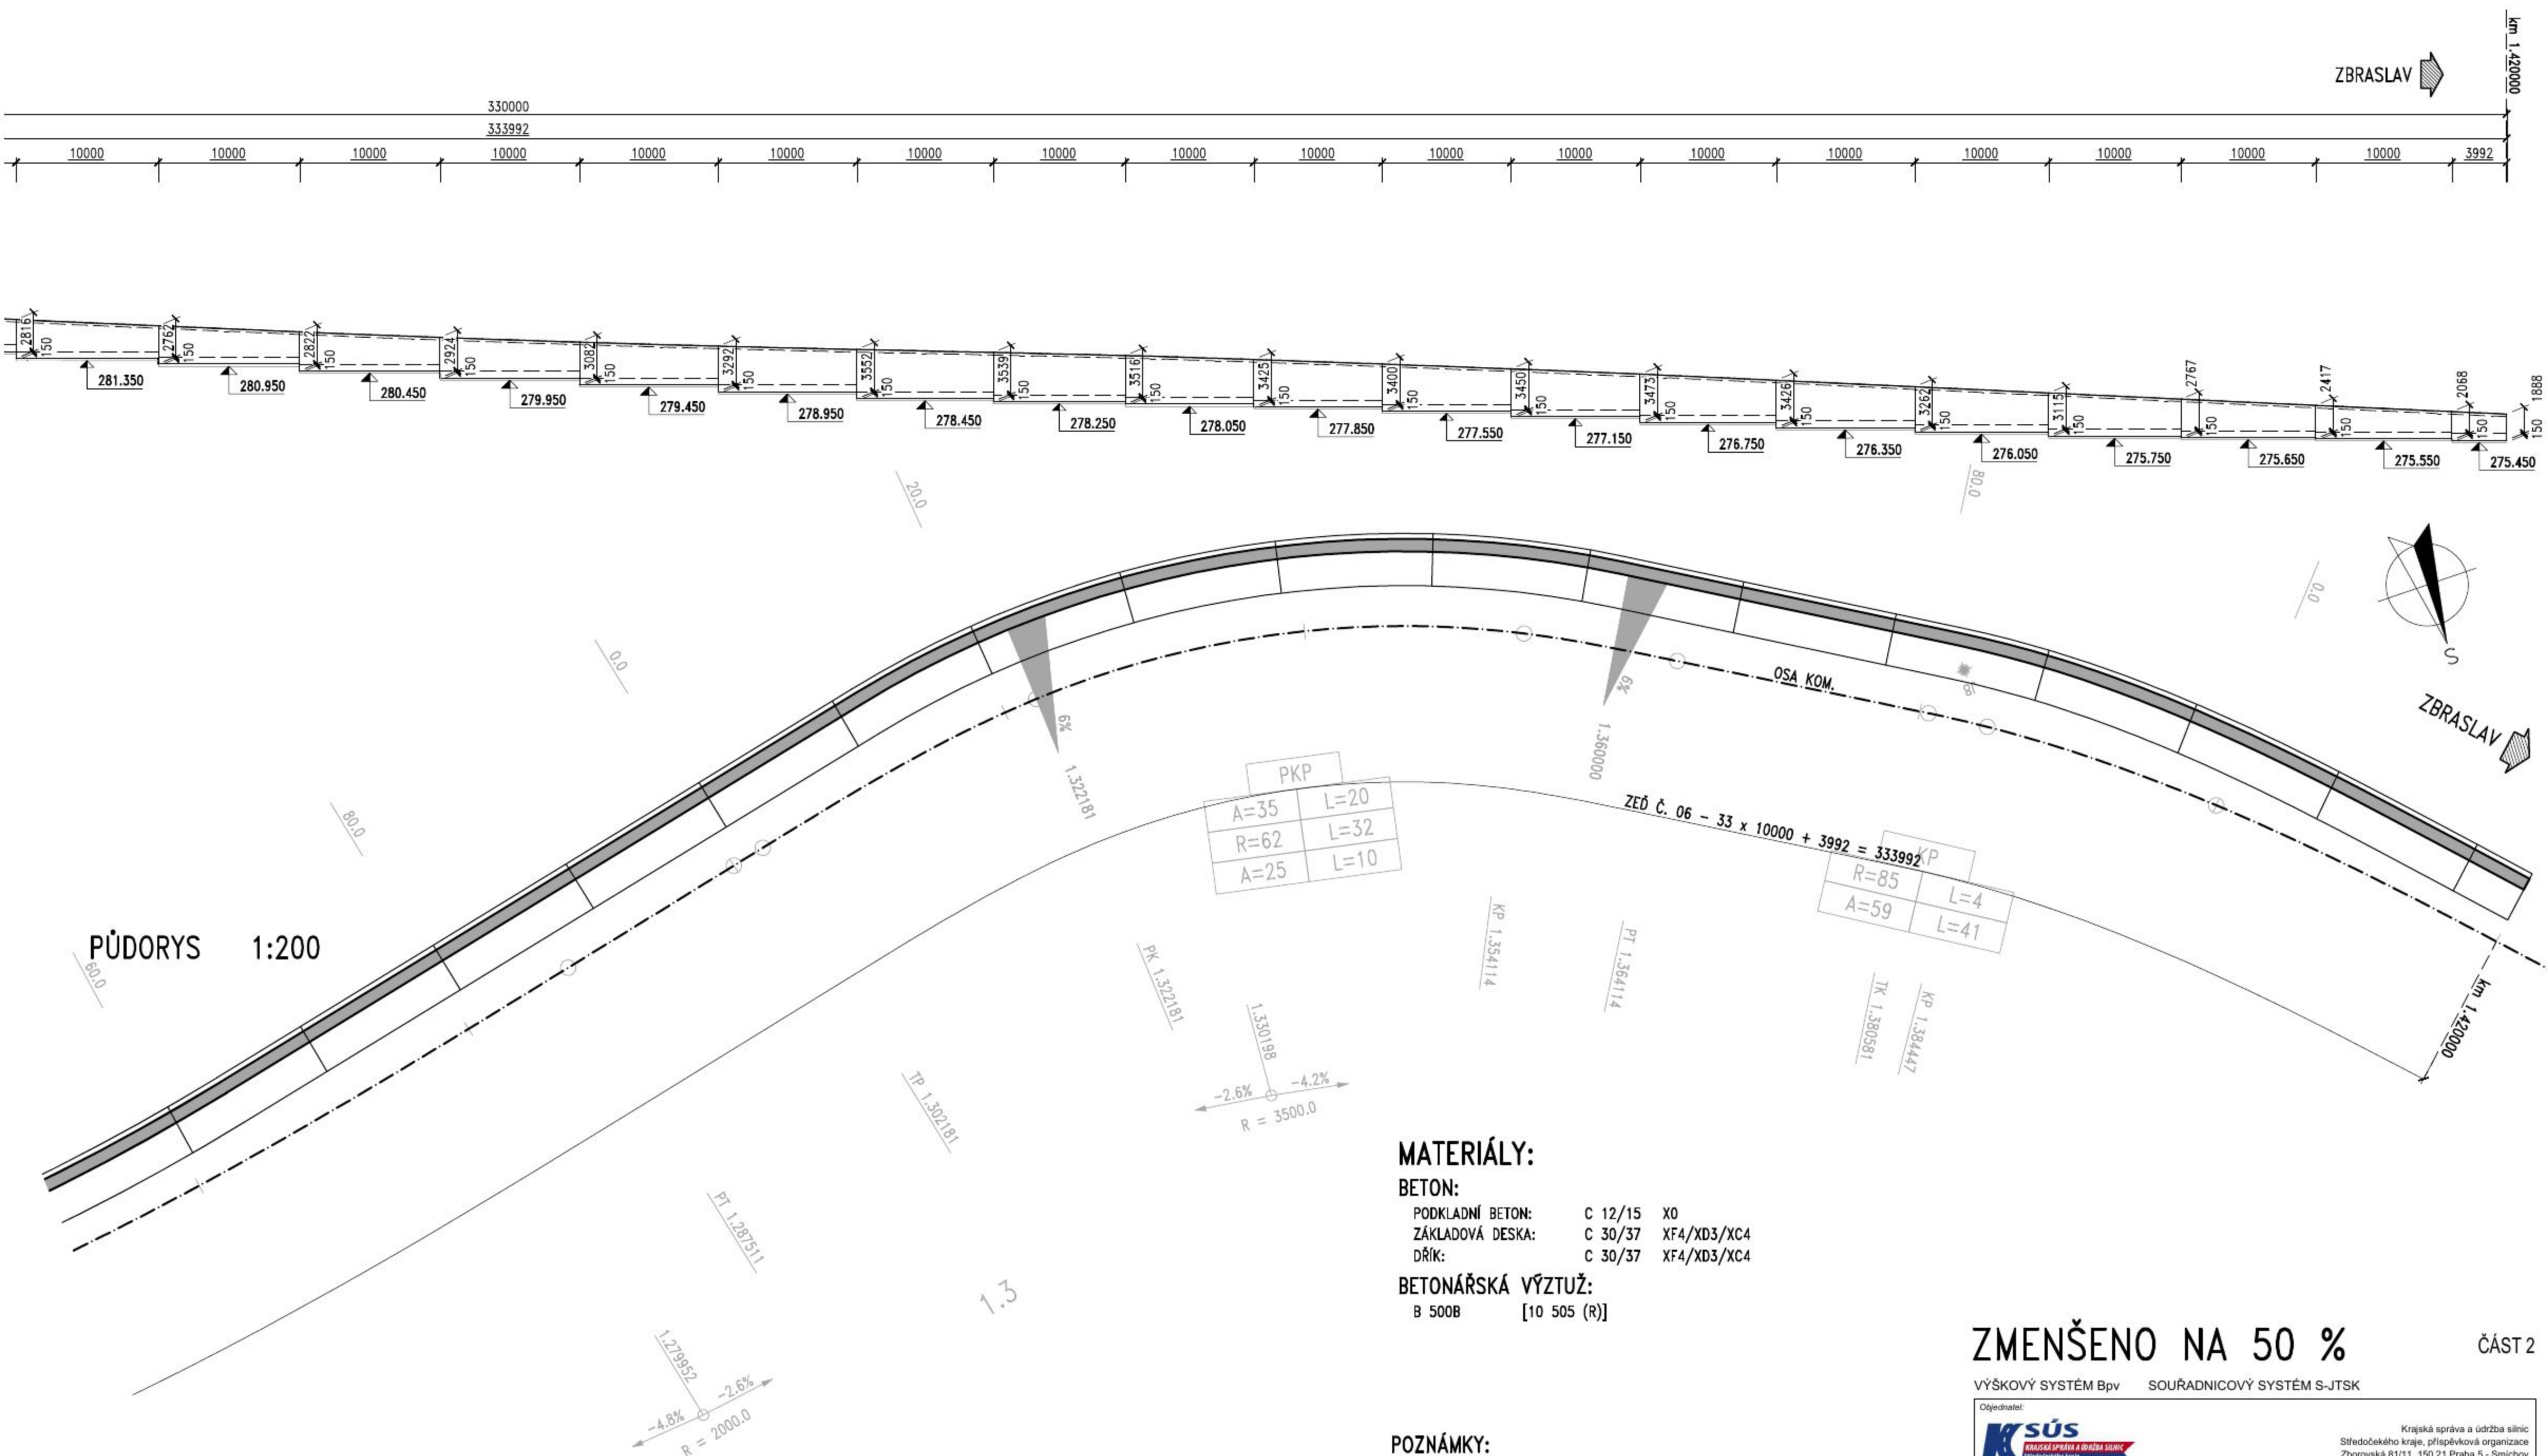

MATERIÁLY:

BETON:
PODKLADNÍ BETON: C 12/15 X0
ZÁKLADOVÁ DESKA: C 30/37 XF4/XD3/XC4
DŘÍK: C 30/37 XF4/XD3/XC4
BETONÁŘSKÁ VÝZTUŽ:
B 500B [10 505 (R)]

POZNÁMKY:

- "D0" = DILATAČNÍ OSEK.
- VODOROVNÉ DELKY (NAPŘ. "DELKA ZDI") MĚŘENY V NÁJEZDOVÉ HRANĚ ŘÍMSY (= V RUBU DŘÍKU) ZDI.
- STANIČNÍ MĚŘENO V OSE KOMUNIKACE.
- ROZDÍL STANIČNÍ A DELKY V NÁJEZDOVÉ HRANĚ ŘÍMSY ZDI SE V DŮSLEDKU PŮDORYSNEHO ZAKRÍVENÍ LIŠÍ.
- KÓTY VÝŠKY ZDI VE VNĚJŠÍM LÍCI, T.J. MEZI SPODKEM ZÁKLADU A VYŠŠÍM OKRAJEM ŘÍMSOVÉ ČÁSTI.

ZMENŠENO NA 50 %

ČÁST 2

VÝŠKOVÝ SYSTÉM BpV		SOUŘADNICOVÝ SYSTÉM S-JTSK	
Objednatel: K SÚS Krajská správa a údržba silnic Středočeského kraje, příspěvková organizace Zborovská 81/115, 150 21 Praha 5 - Smíchov		Zhotovitel: GeoTec GS Chmelová 2920/6, 106 00 Praha 10 tel.: +420 271 750 710 e-mail: praha@geotec-gs.cz	
Výpracovatel: Ing. Lukáš PROCHÁZKA Právník: Procházka		Odpovědný projektant: Ing. Pavel HRDINA Právník: Procházka	
Schválil: Mgr. Filip DUŠEK Právník: Procházka		Číslo zakázky: 2017 - 395 Datum: 04/2024	
Název akce: II/101 Dolní Břežany - Zbraslav		Měřítko: Státní: PDPS Přístroj: D 1.2.1 7-06-2	
Objekt: TVAR ZDI – ZEĎ Č. 06 – ČÁST 2		Formát: A4	