


TVAR ZDI – ZEĎ Č. 13

POHLED 1:200

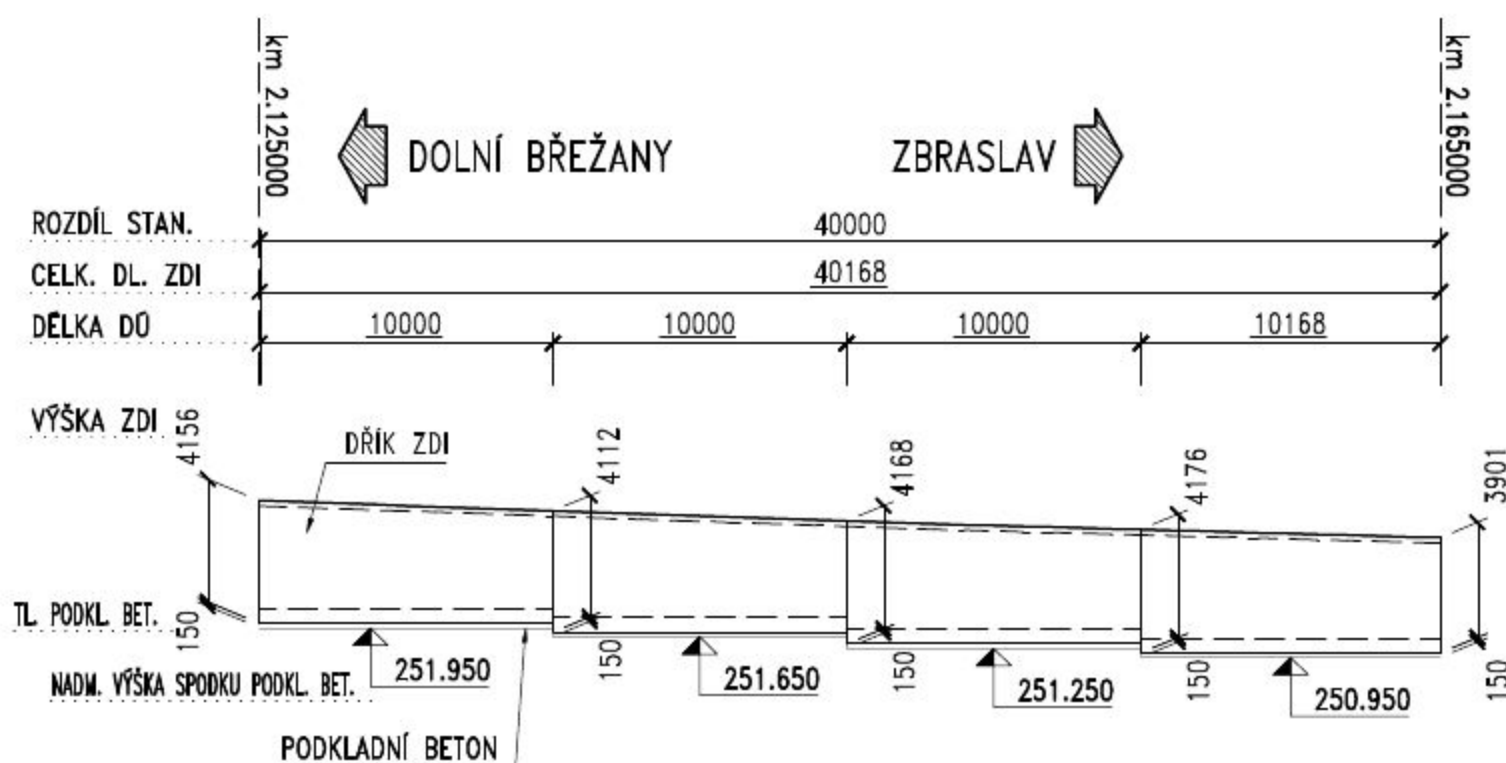

MATERIÁLY:


BETON:

PODKLADNÍ BETON:	C 12/15	X0
ZÁKLADOVÁ DESKA:	C 30/37	XF4/XD3/XC4
DŘÍK:	C 30/37	XF4/XD3/XC4

BETONÁŘSKÁ VÝZTUŽ:

B 500B [10 505 (R)]


PŮDORYS 1:200

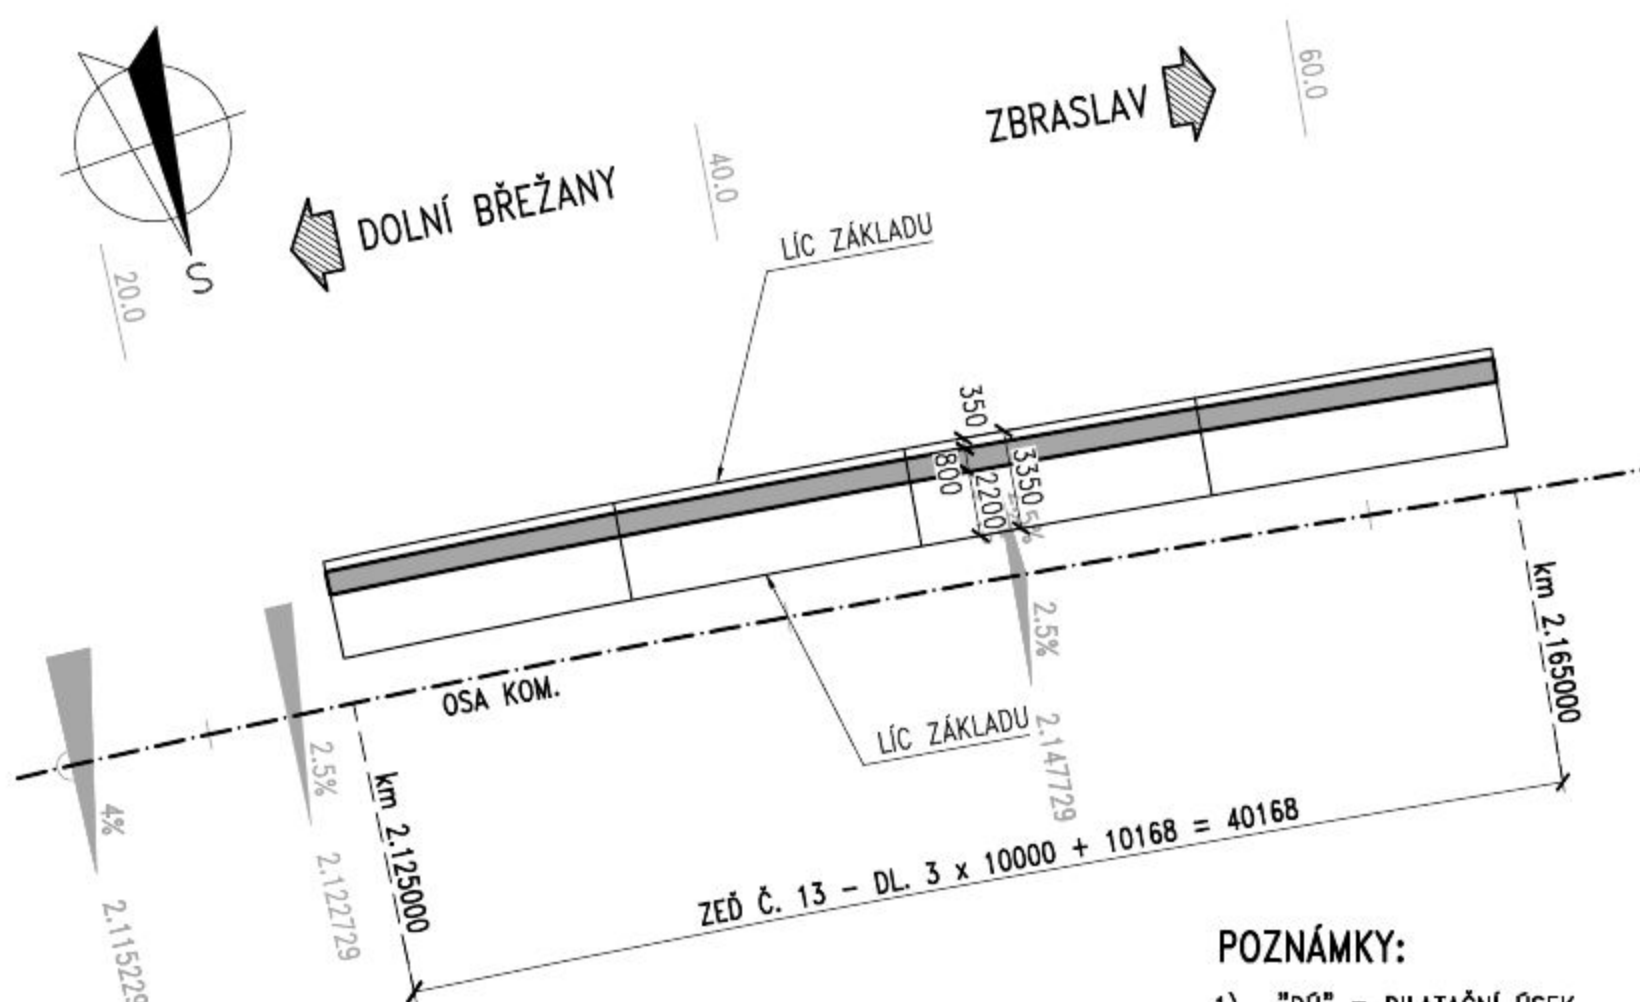

POZNÁMKY:

- 1) "DŮ" = DILATAČNÍ ÚSEK.
- 2) VODOROVNÉ DÉLKY (NAPŘ. "DÉLKA ZDI") MĚŘENY V NÁJEZDOVÉ HRANĚ ŘÍMSY (= V RUBU DŘÍKU) ZDI.
- 3) STANIČENÍ MĚŘENO V OSE KOMUNIKACE.
- 4) ROZDÍL STANIČENÍ A DÉLKY V NÁJEZDOVÉ HRANĚ ŘÍMSY ZDI SE V DŮSLEDKU PŮDORYSNÉHO ZAKŘIVENÍ LIŠÍ.
- 5) KÓTY VÝŠKY ZDI VE VNĚJŠÍM LÍCI, T.J. MEZI SPODKEM ZÁKLADU A VYŠŠÍM OKRAJEM ŘÍMSOVÉ ČÁSTI.

ZEĎ 13 – TYPICKÝ PŘÍČNÝ ŘEZ 1:50

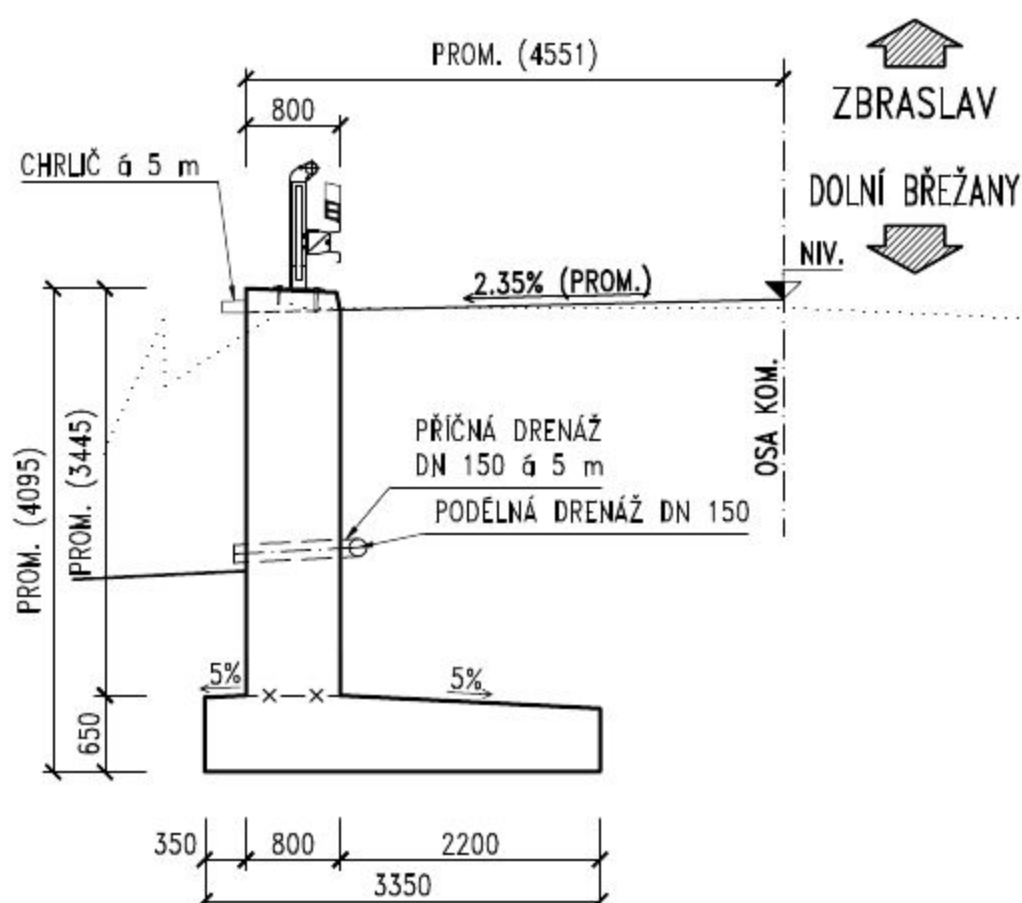

ZMENŠENO NA 50 %

ČÁST 2

VÝŠKOVÝ SYSTÉM BpV SOUŘADNICOVÝ SYSTÉM S-JTSK

Objednatel:



Krajská správa a údržba silnic
Středočeského kraje, příspěvková organizace
Zborovská 81/11, 150 21 Praha 5 - Smíchov

Zhotovitel:



GeoTec-GS, a.s.
Chmelová 2920/6, 106 00 Praha 10
tel.: +420 271 750 710
e-mail: praha@geotec-gs.cz

Vypracoval:

Ing. Lukáš PROCHÁZKA

Odpovědný projektant:

Ing. Pavel HRDINA

Schválil:

Mgr. Filip DUDÍK

Číslo zakázky:

2017 - 395

Podpis:

Procházka

Podpis:

Hrdina

Podpis:

Dudík

Datum:

04/2024

Název akce:

II/101 Dolní Břežany - Zbraslav

Měřítko:

Stupeň:

Paré č.:

Objekt:

TVAR ZDI – ZEĎ Č. 13

Příloha:

D.1.2.1

7-13