


TVAR ZDI – ZEĎ Č. 14

POHLED 1:200

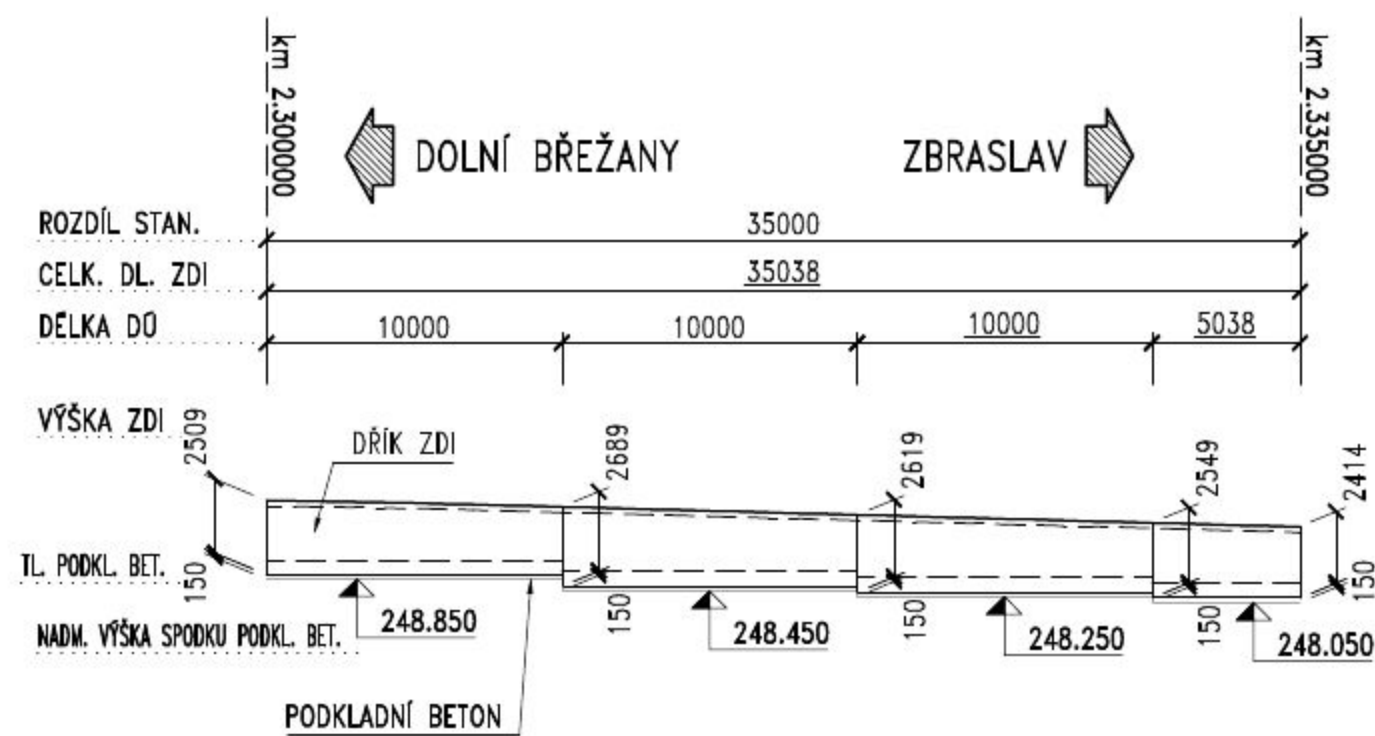

MATERIÁLY:


BETON:

PODKLADNÍ BETON:	C 12/15	X0
ZÁKLADOVÁ DESKA:	C 30/37	XF4/XD3/XC4
DŘÍK:	C 30/37	XF4/XD3/XC4

BETONÁŘSKÁ VÝZTUŽ:

B 500B [10 505 (R)]


PŮDORYS 1:200

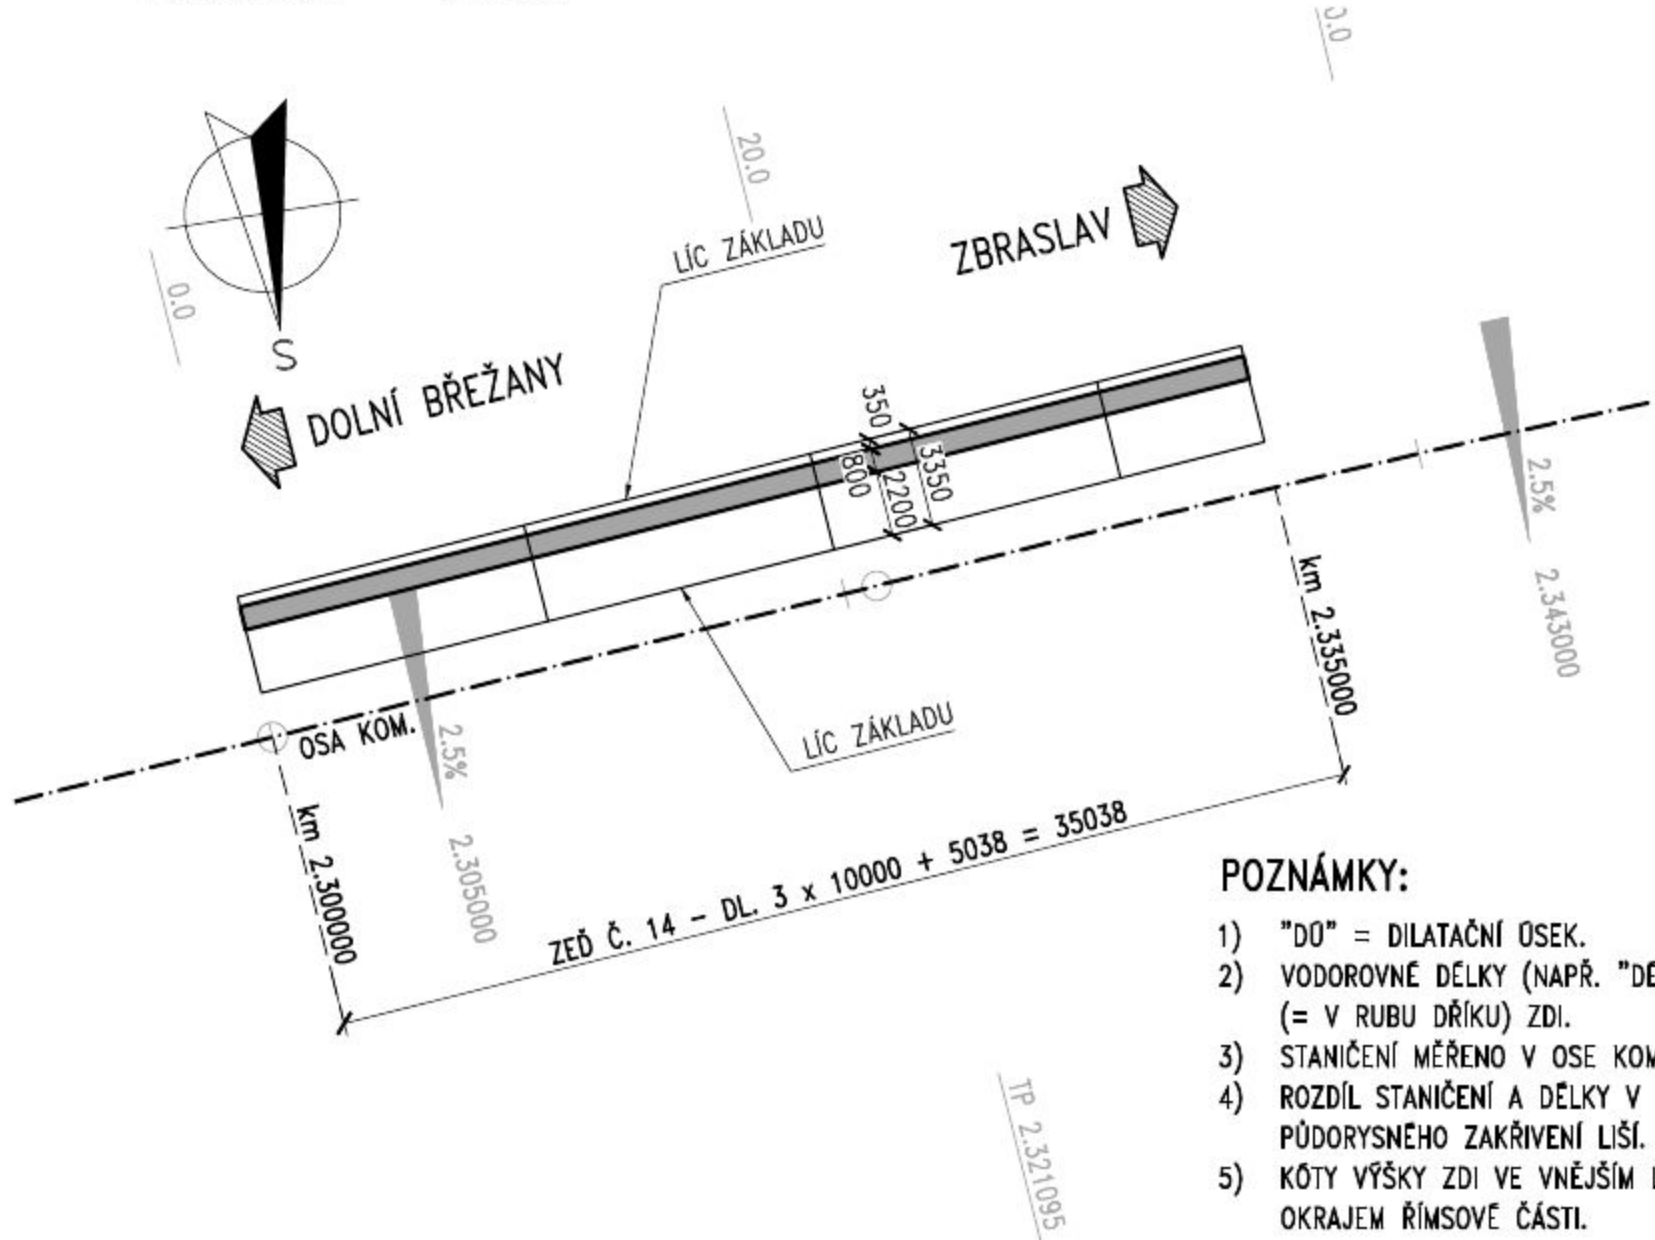

POZNÁMKY:

- 1) "DŮ" = DILATAČNÍ OSEK.
- 2) VODOROVNÉ DÉLKY (NAPŘ. "DÉLKA ZDI") MĚŘENY V NÁJEZDOVÉ HRANĚ ŘÍMSY (= V RUBU DŘÍKU) ZDI.
- 3) STANIČENÍ MĚŘENO V OSE KOMUNIKACE.
- 4) ROZDÍL STANIČENÍ A DÉLKY V NÁJEZDOVÉ HRANĚ ŘÍMSY ZDI SE V DŮSLEDKU PŮDORYSNÉHO ZAKŘIVENÍ LIŠÍ.
- 5) KÓTY VÝŠKY ZDI VE VNĚJŠÍM LÍCI, T.J. MEZI SPODKEM ZÁKLADU A VYŠŠÍM OKRAJEM ŘÍMSOVÉ ČÁSTI.

ZEĎ 14 – TYPICKÝ PŘÍČNÝ ŘEZ 1:50

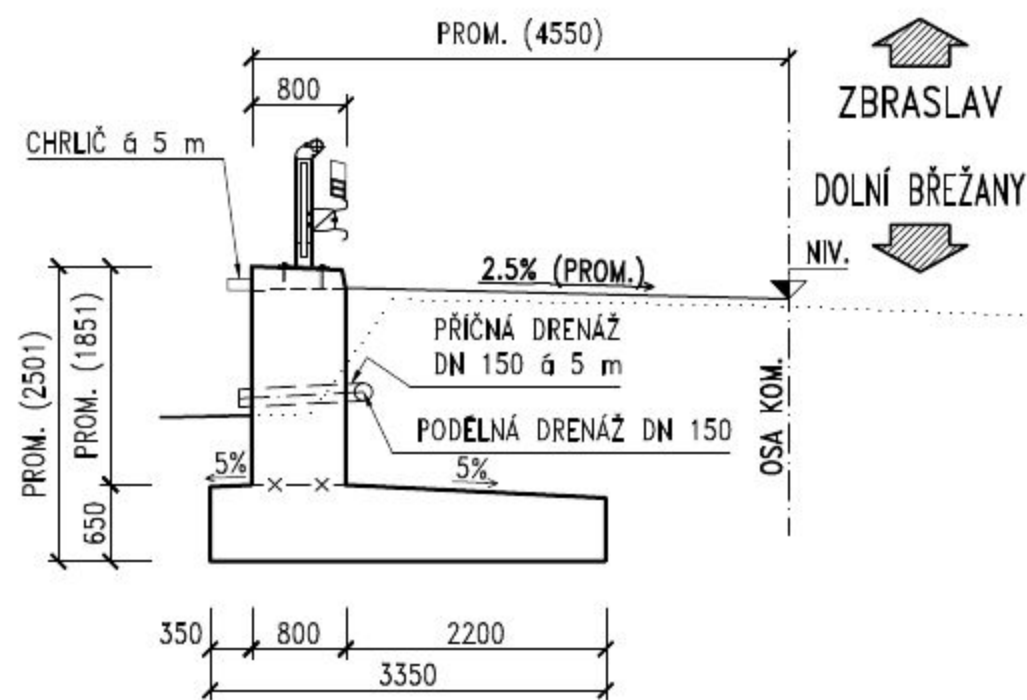

ZMENŠENO NA 50 %

ČÁST 2

VÝŠKOVÝ SYSTÉM BpV SOUŘADNICOVÝ SYSTÉM S-JTSK

Objednatel:	Krajská správa a údržba silnic Středočeského kraje, příspěvková organizace Zborovská 81/11, 150 21 Praha 5 - Smíchov
Zhotovitel:	GeoTec GS, a.s. Chmelová 2920/6, 106 00 Praha 10 tel.: +420 271 750 710 e-mail: praha@geotec-gs.cz

Vypracoval:	Odpovědný projektant:	Schválil:	Číslo zakázky:
Ing. Lukáš PROCHÁZKA	Ing. Pavel HRDINA	Mgr. Filip DUDÍK	2017 - 395
Podpis:	Podpis:	Podpis:	Datum:
			04/2024
Název akce:	II/101 Dolní Břežany - Zbraslav		Měřítko:
			Formát:
			Stupeň: PDPS
			Paré č.:
Objekt:	TVAR ZDI – ZEĎ Č. 14		Příloha: D.1.2.1 7-14