




POHLED 1:200

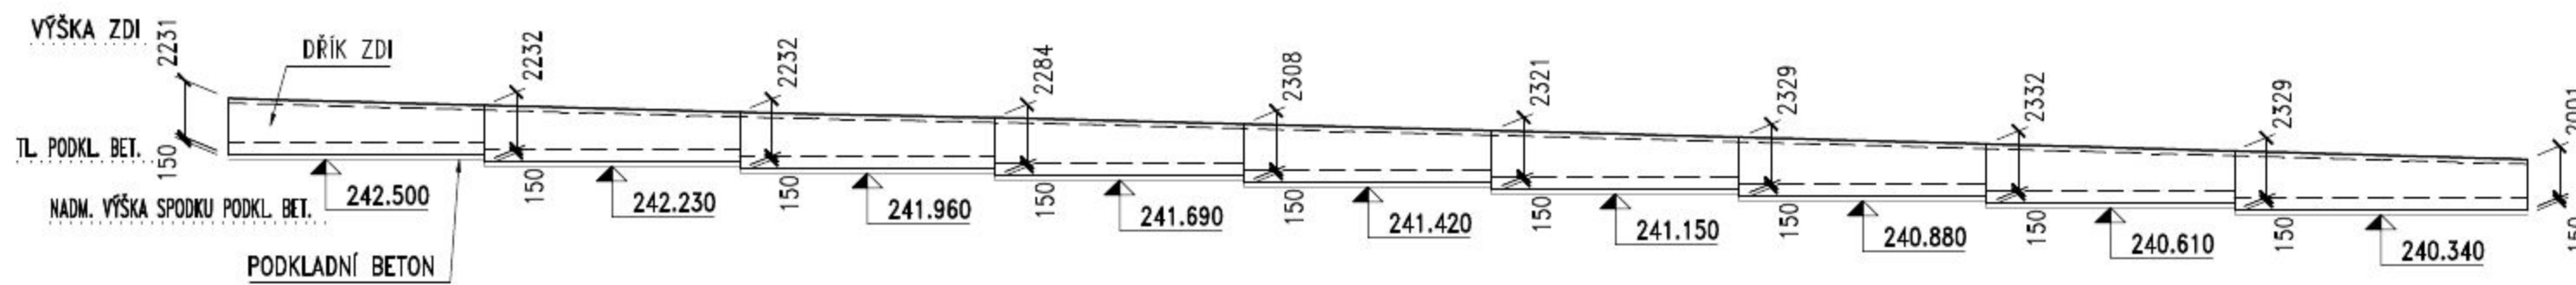

PŪDORYS 1:200

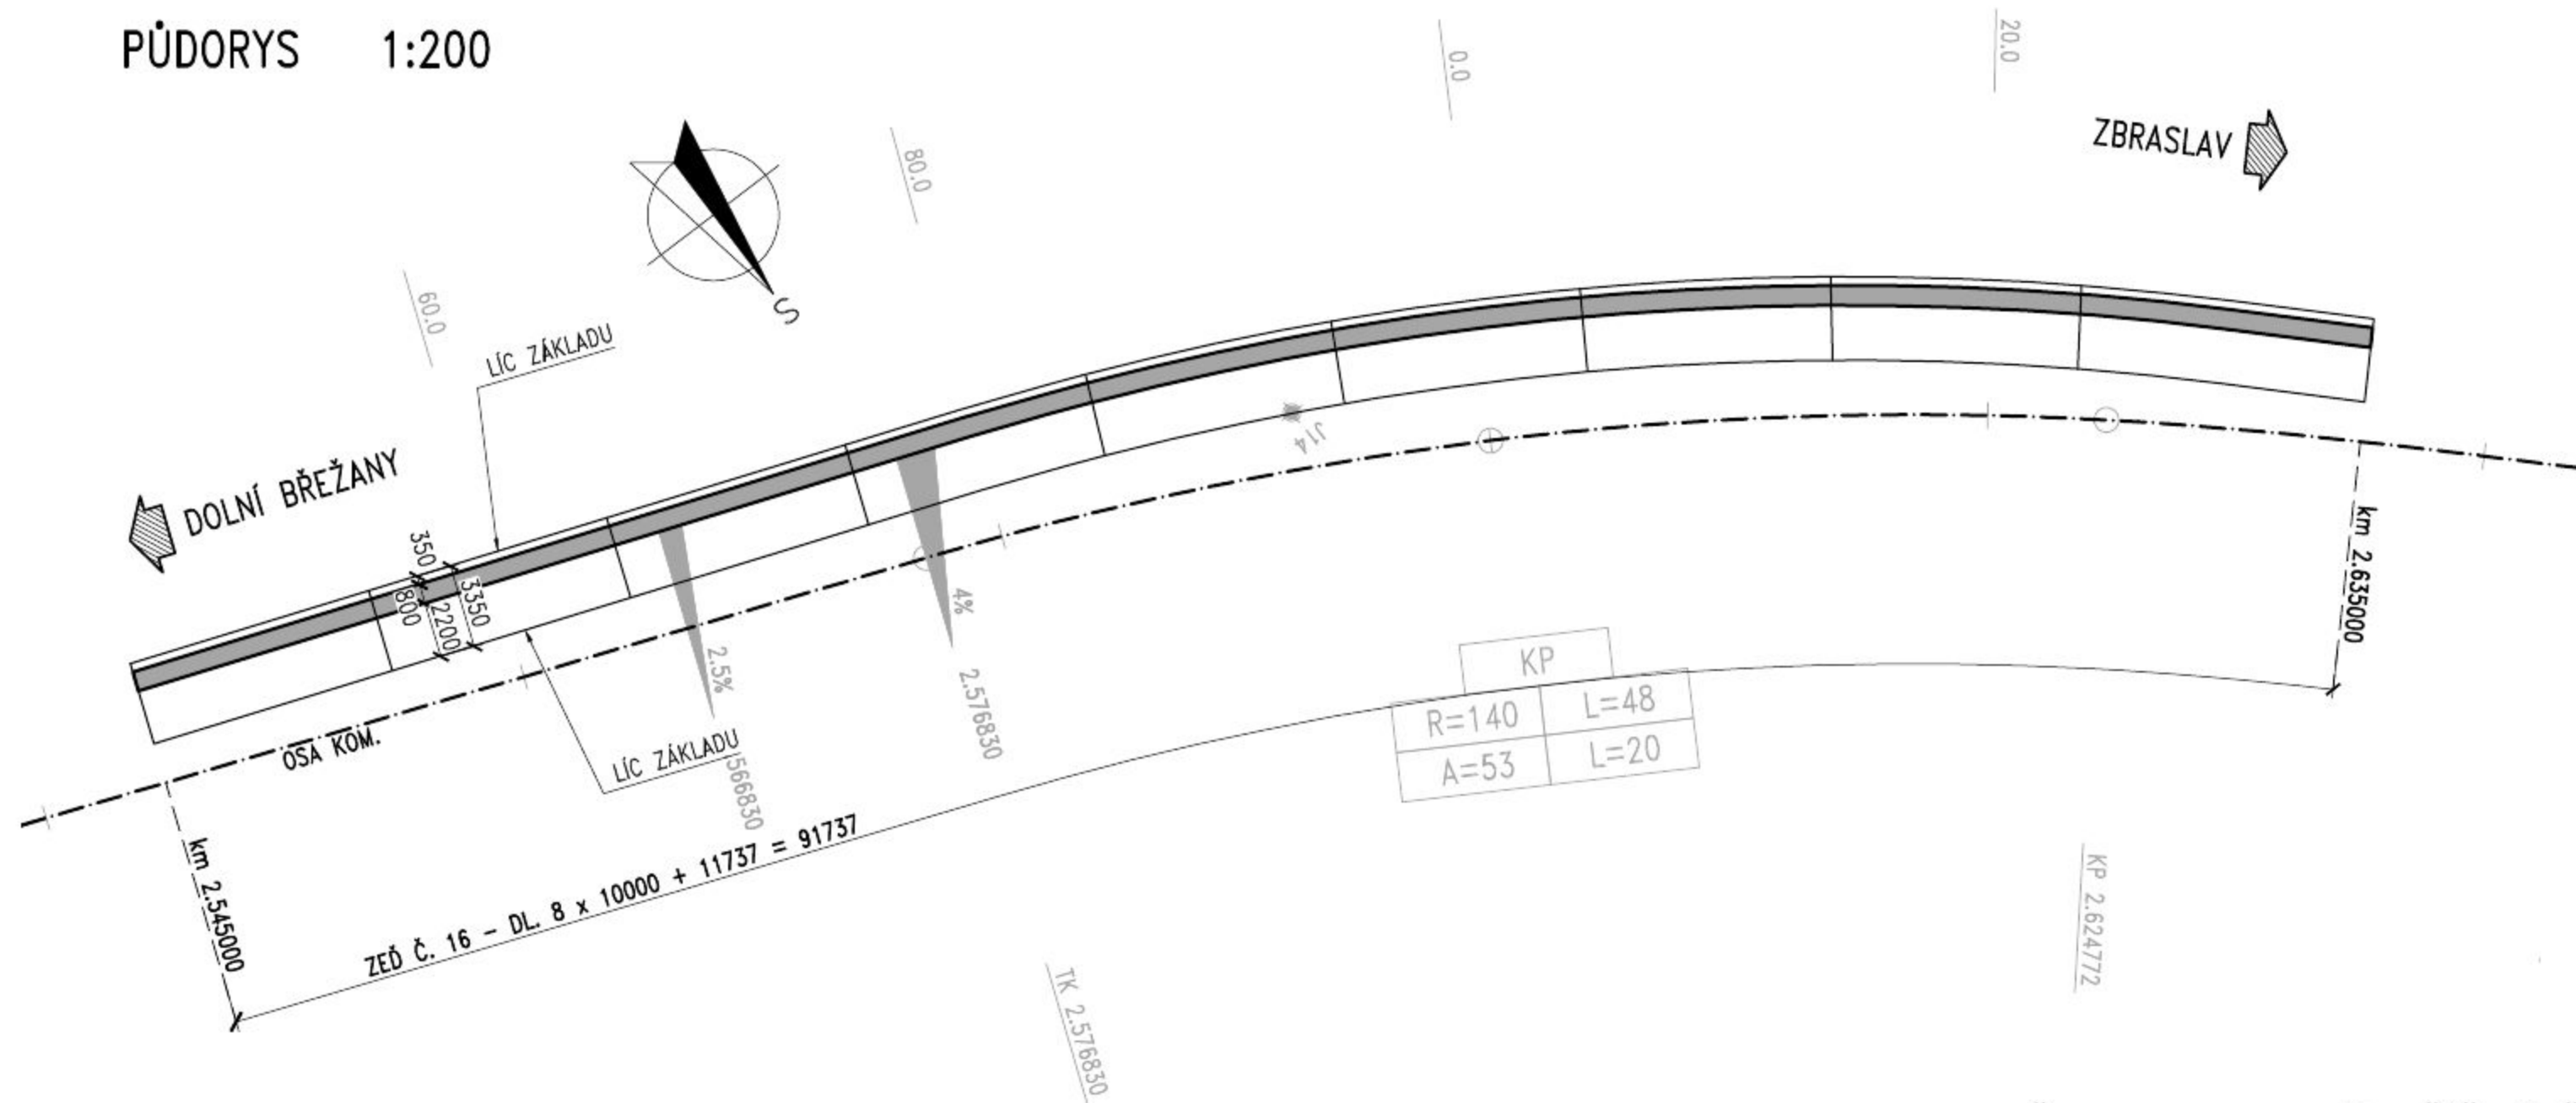

ZED 16 – TYPICKÝ PŘÍČNÝ ŘEZ 1:50

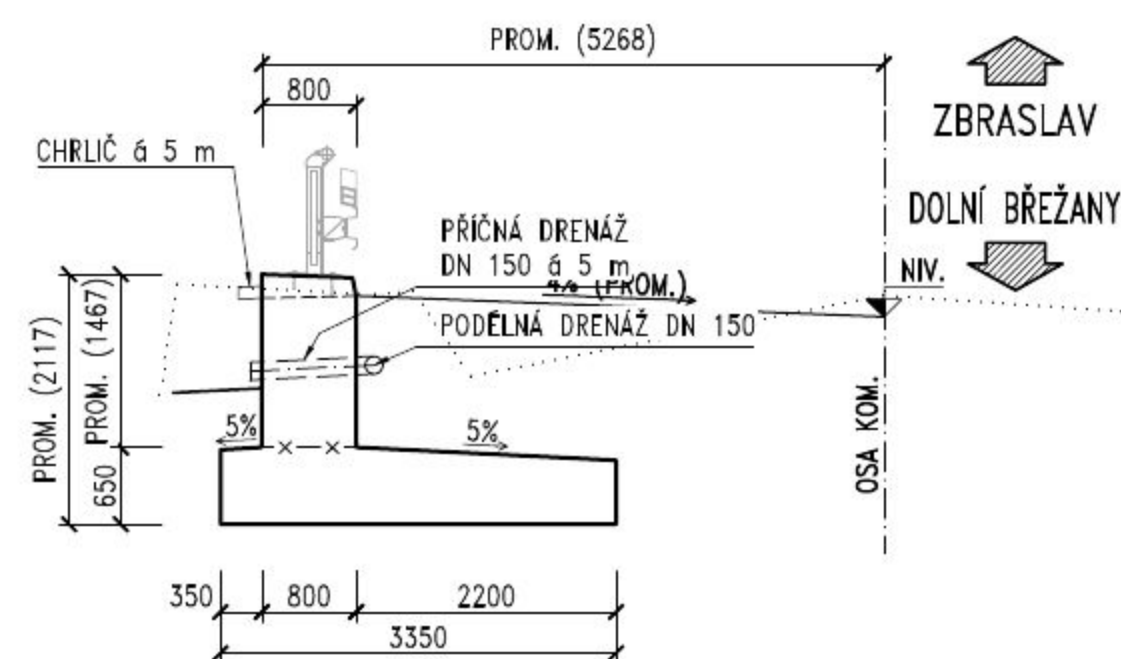

B 500B [10 505 (R)]

- 1) "DÚ" = DILATAČNÍ ÚSEK.
- 2) VODOROVNÉ DÉLKY (NAPŘ. "DĚLKA ZDI") MĚŘENY V NÁJEZDOVÉ HRANĚ ŘÍMSY (= V RUBU DŘÍKU) ZDI.
- 3) STANIČENÍ MĚŘENO V OSE KOMUNIKACE.
- 4) ROZDÍL STANIČENÍ A DÉLKY V NÁJEZDOVÉ HRANĚ ŘÍMSY ZDI SE V DŮSLEDKU PŮDORYSNÉHO ZAKŘIVĚNÍ LÍŠÍ.
- 5) KÓTY VÝŠKY ZDI VE VNĚJŠÍM LÍCI, TJ. MEZI SPODKEM ZÁKLADU A VYŠŠÍM OKRAJEM ŘÍMSOVÉ ČÁSTI.

ZMENŠENO NA 50 %

ČÁST 2

VÝŠKOVÝ SYSTÉM Bpv SOUŘADNICOVÝ SYSTÉM S-JTSK

Objednatel:



Krajská správa a údržba silnic
Středočeského kraje, příspěvková organizace
Zborovská 81/11, 150 21 Praha 5 - Smíchov

Zhotovitel:

Geotec GS®

GeoTec-GS, a.s.
Chmelová 2920/6, 106 00 Praha 10
tel.: +420 271 750 710
e-mail: praha@geotec-gs.cz

Vypracovať:

Ing. Lukáš PROCHÁZKA

Odpovědný projektant:

A	Ing. Pavel HRDINA
---	-------------------

Schválil:

Mgr. Filip DUDÍK

Podpis: _____

Mázev akce

II/101 Dolní Břežany - Zbraslav

Měřítka:	Formát:
----------	---------

Stungh	Paré A
--------	--------

Objekt:

TVAR ZDI – ZEDĚ Č. 16

Priloha:
D.1.2.1

D.1.2.1	7-16
---------	------