



TVAR ZDI – ZEĎ Č. 23


POHLED 1:225

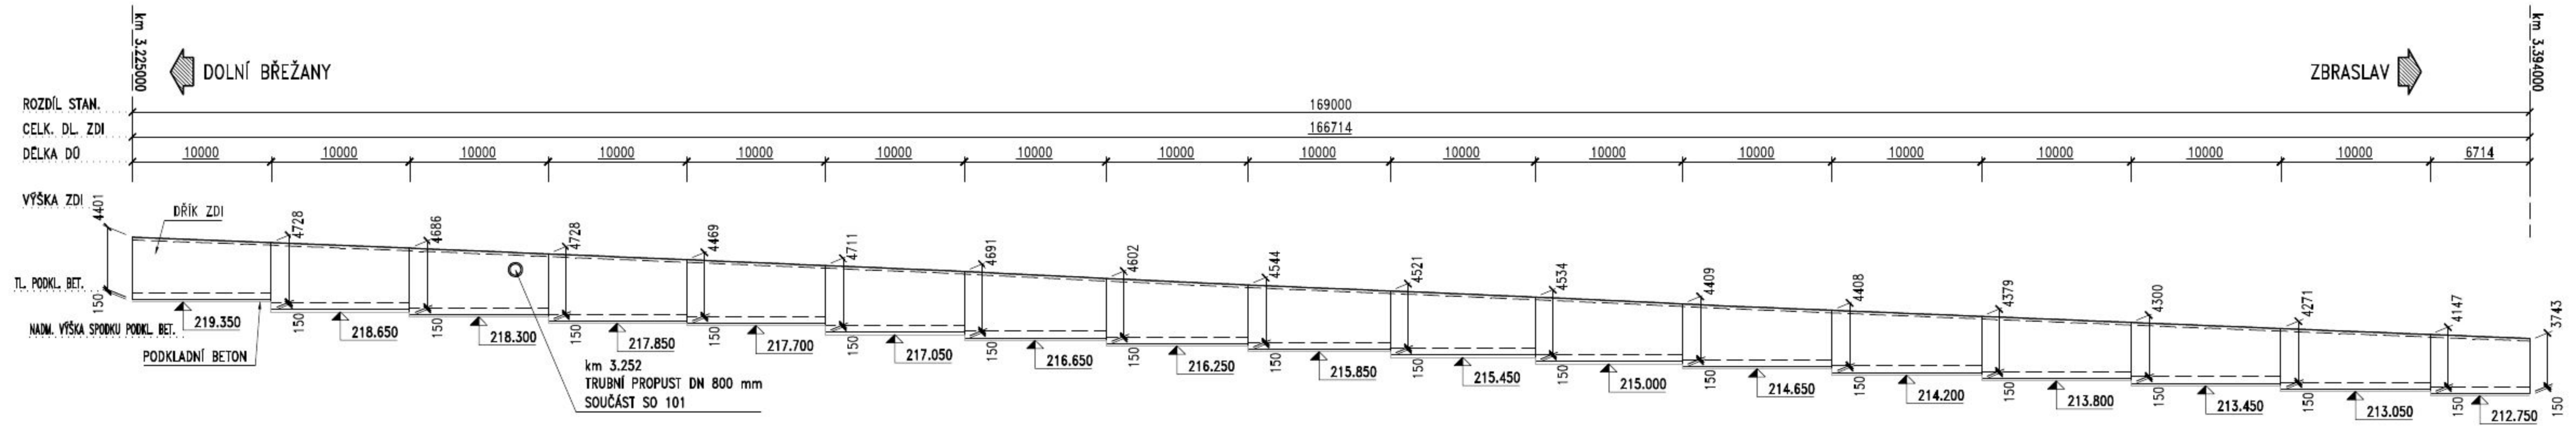

PŮDORYS 1:200

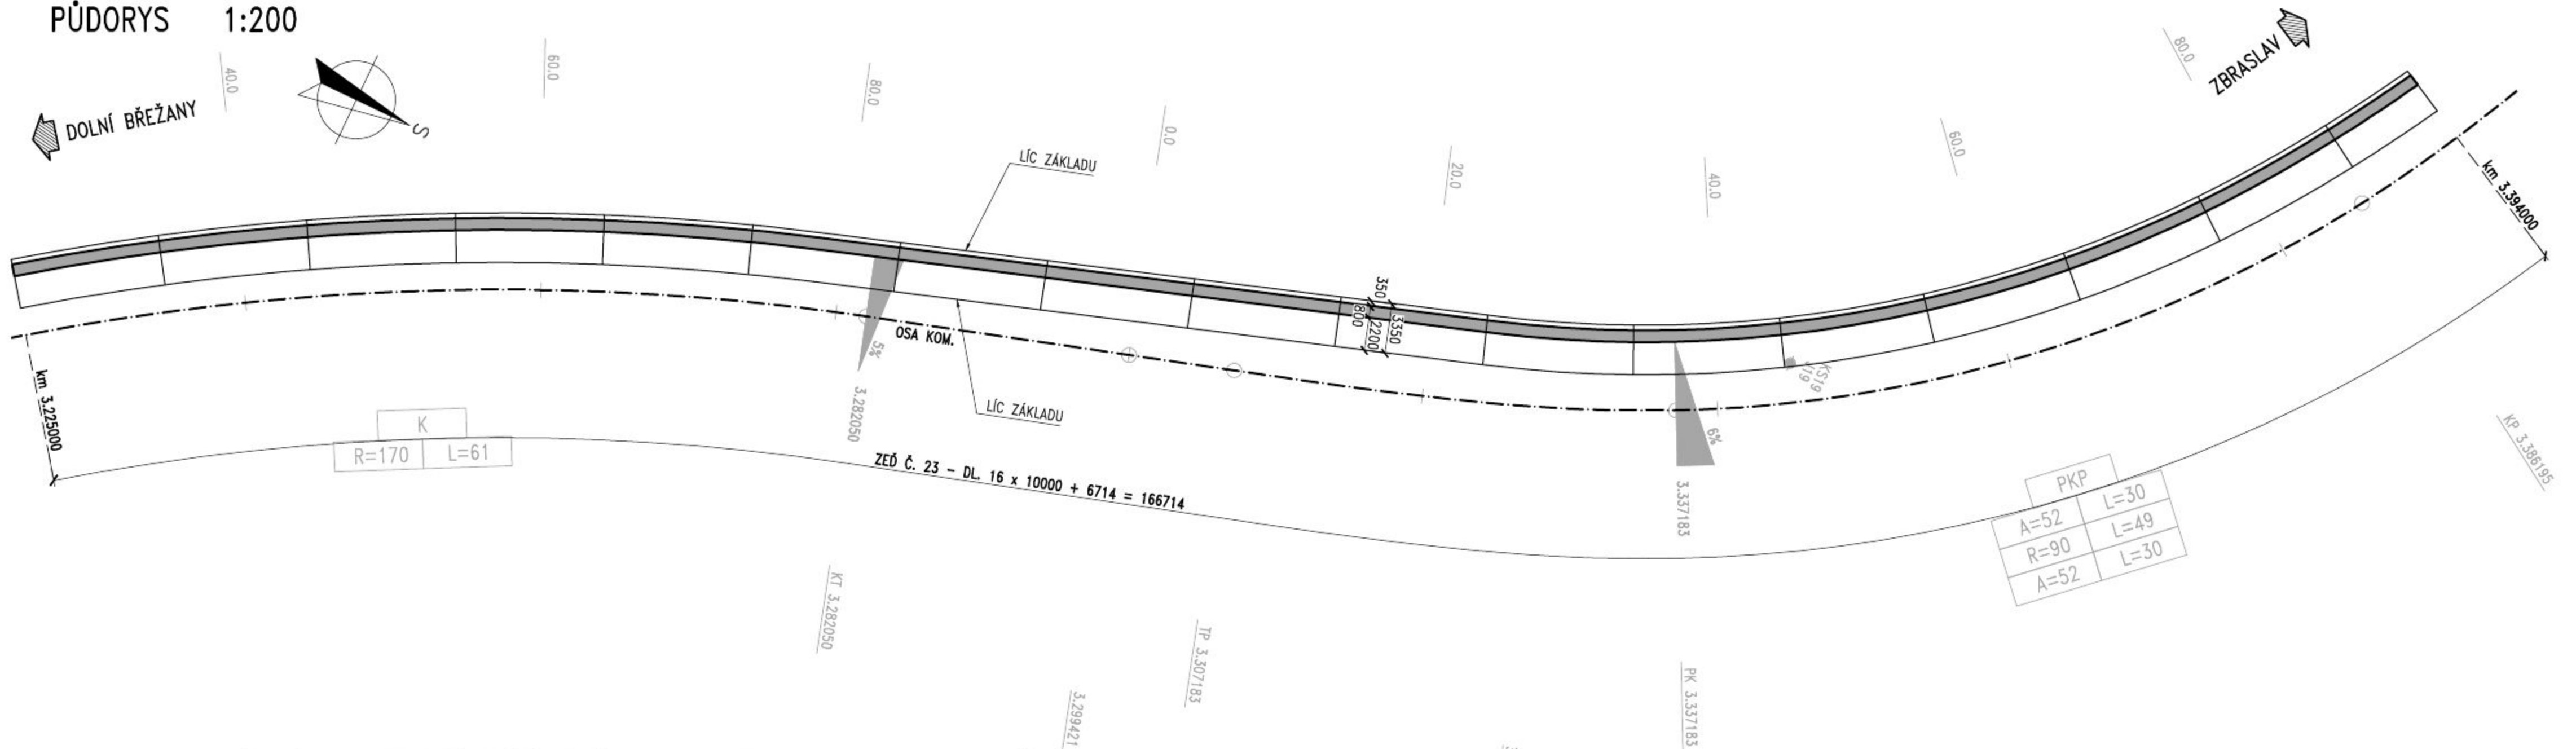

ZEĎ 23 – TYPICKÝ PŘÍČNÝ ŘEZ 1:50

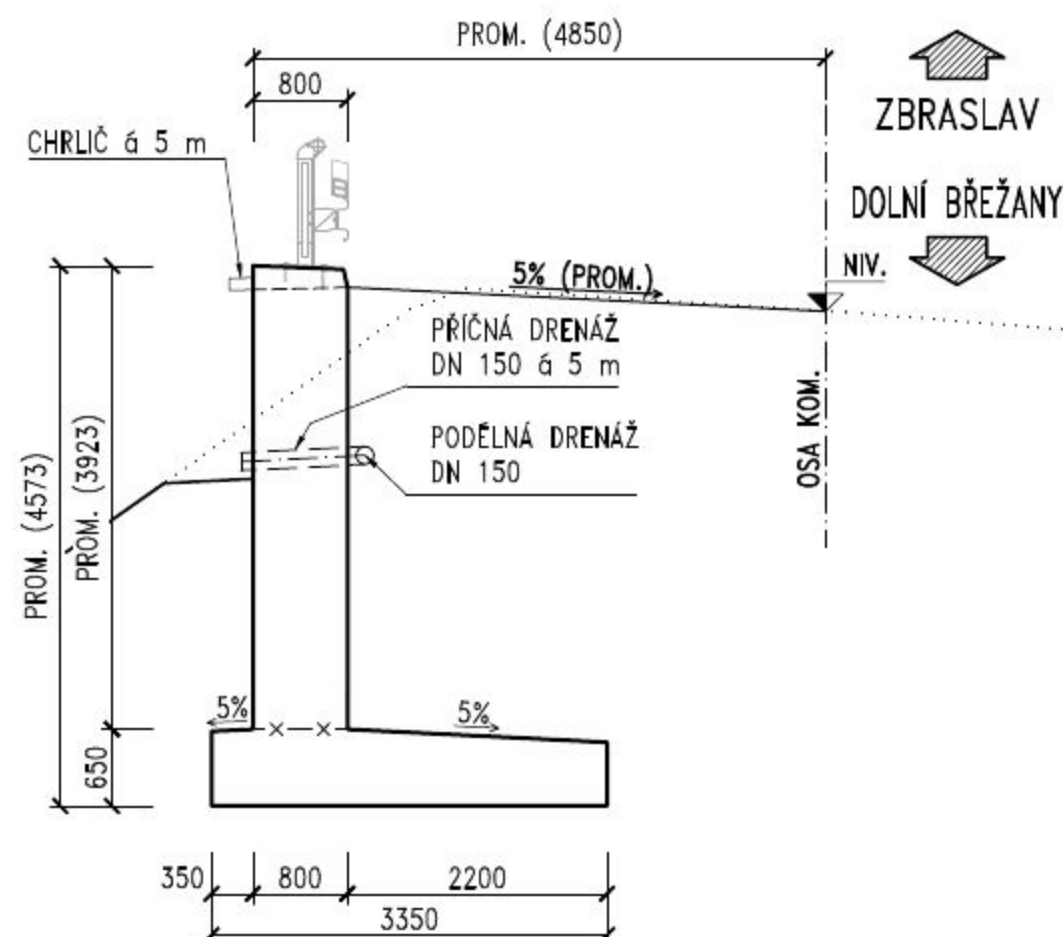

MATERIÁLY:

BETON:

PODKLADNÍ BETON: C 12/15 XO
ZÁKLADOVÁ DESKA: C 30/37 XF4/XD3/XC4
DŘÍK: C 30/37 XF4/XD3/XC4

BETONÁŘSKÁ VÝZTUŽ:
B 500B [10 505 (R)]

POZNÁMKY:

- "DÚ" = DILATAČNÍ ÚSEK.
- VODOROVNÉ DÉLKY (NAPŘ. "DÉLKA ZDI") MĚŘENY V NÁJEZDOVÉ HRANĚ ŘÍMSY (= V RUBU DŘÍKU) ZDI.
- STANIČENÍ MĚŘENO V OSE KOMUNIKACE.
- ROZDÍL STANIČENÍ A DÉLKY V NÁJEZDOVÉ HRANĚ ŘÍMSY ZDI SE V DŮSLEDKU PŮDORYSNEHO ZAKRÍVENÍ LIŠÍ.
- KÓTY VÝŠKY ZDI VE VNĚJŠÍM LÍCI, T.J. MEZI SPODKEM ZÁKLADU A VYŠŠÍM OKRAJEM ŘÍMSOVÉ ČÁSTI.

ZMENŠENO NA 50 %

ČÁST 2

VÝŠKOVÝ SYSTÉM BpV SOUŘADNICOVÝ SYSTÉM S-JTSK

Ověřeno: **Ksús** KRAJSKÁ SPRÁVA A ÚDRŽBA SILNIC Středočeského kraje, příspěvková organizace Zborovská 81/11, 150 21 Praha 5 - Smíchov

Zhotovitel: GeoTec GS, a.s. Chmelová 2920/6, 106 00 Praha 10 tel.: +420 271 750 710 e-mail: praha@geotec-gs.cz

Vypracoval: Ing. Lukáš PROCHÁZKA Odpovědný projektant: Ing. Pavel HRDINA Schválil: Mgr. Filip DUDÍK Číslo zakázky: 2017 - 395 Datum: 04/2024

Název akce: II/101 Dolní Břežany - Zbraslav Měřítko: Formát: Stupeň: Paré č.: Příloha: D.1.2.1 7-23