



TVAR ZDI – ZEĎ Č. 25

POHLED 1:200

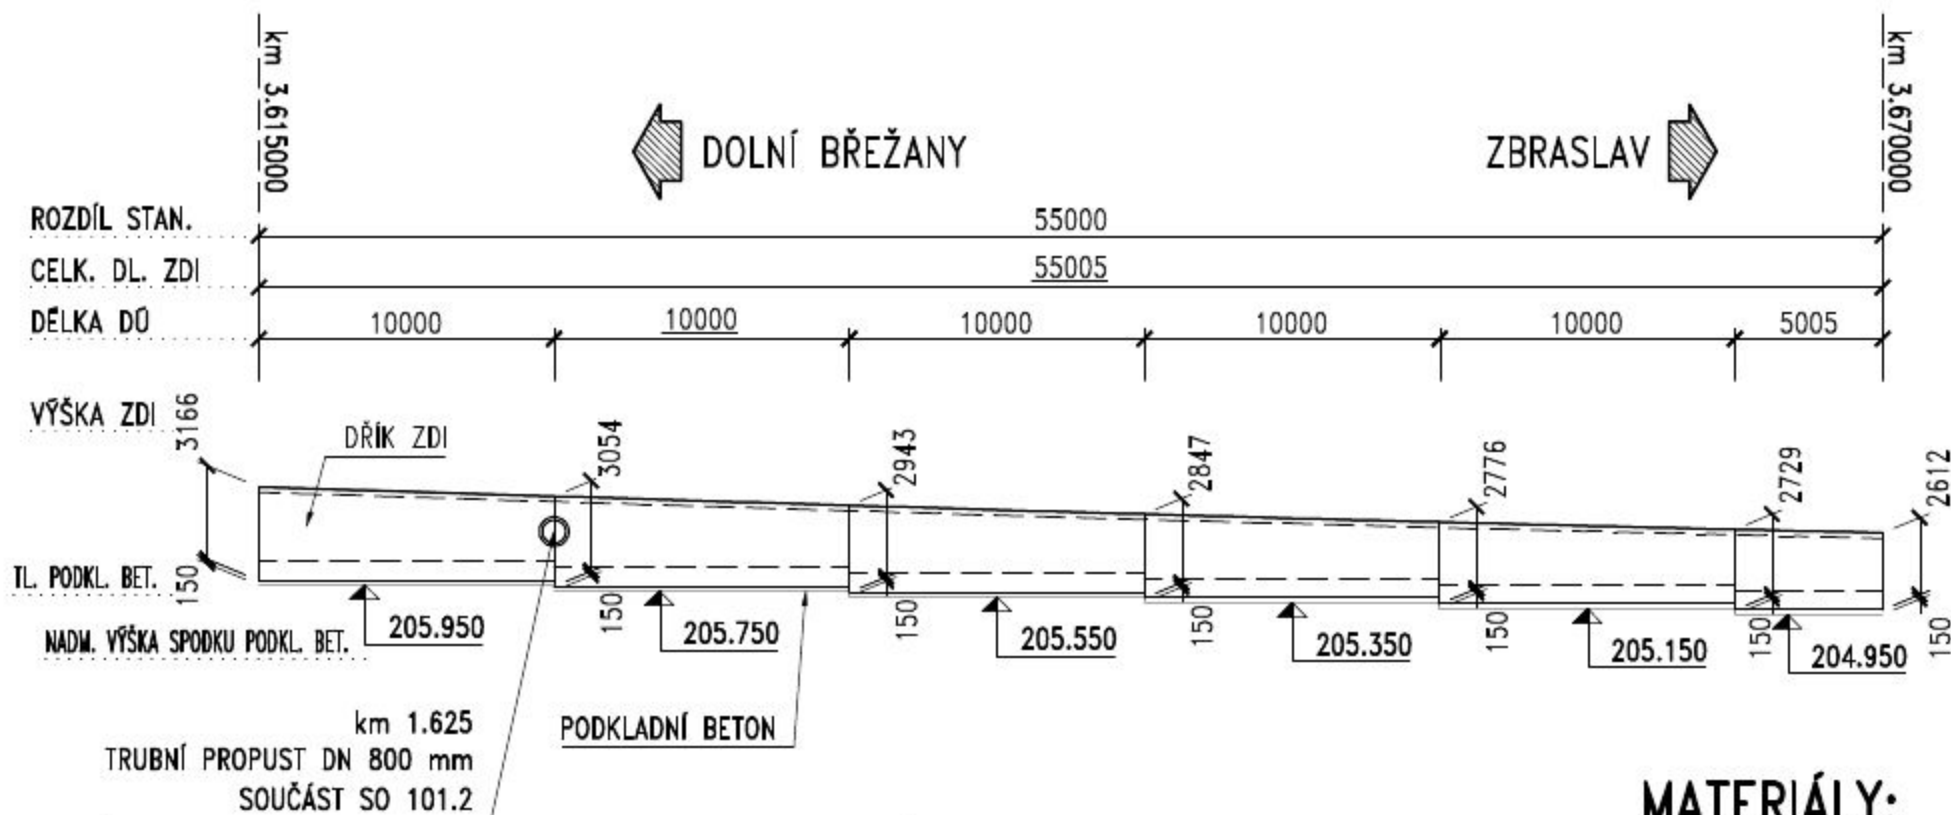

PŮDORYS 1:200

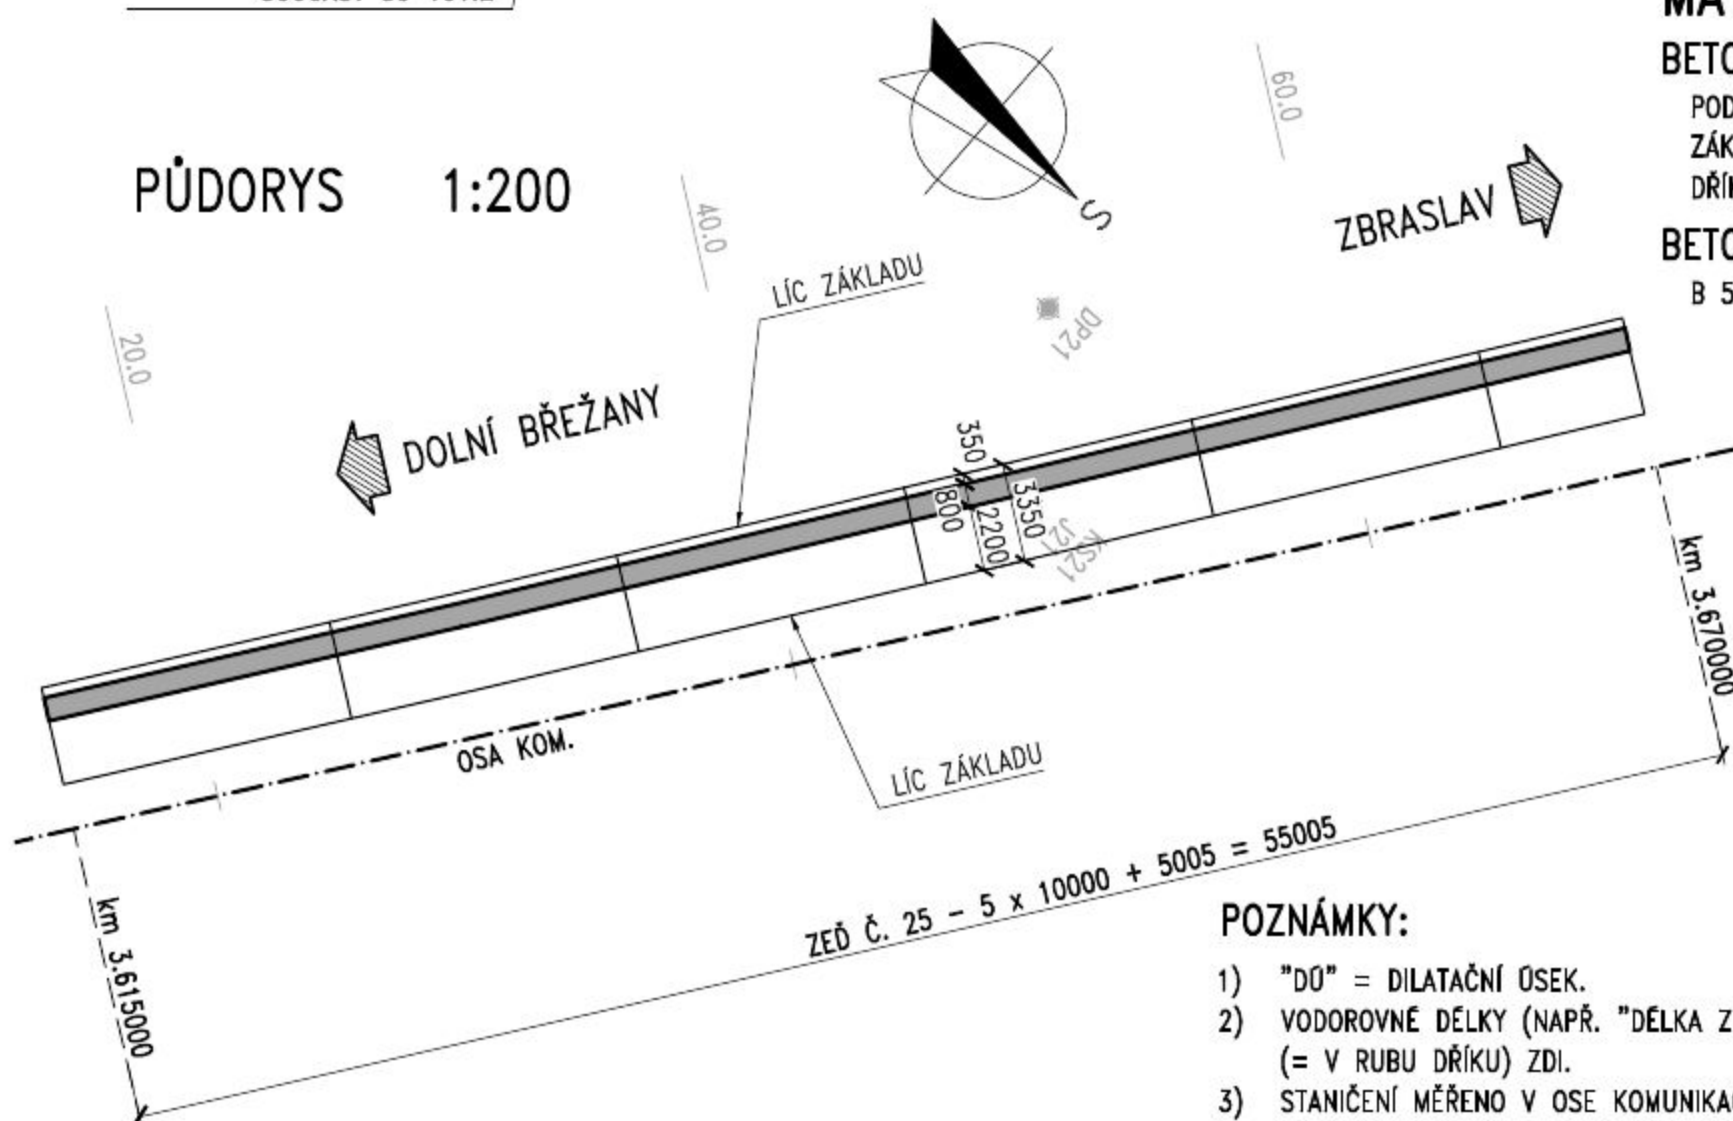

MATERIÁLY:

BETON:

PODKLADNÍ BETON: C 12/15 X0
ZÁKLADOVÁ DESKA: C 30/37 XF4/XD3/XC4
DŘÍK: C 30/37 XF4/XD3/XC4


BETONÁŘSKÁ VÝZTUŽ:

B 500B [10 505 (R)]

POZNÁMKY:

- 1) "DŮ" = DILATAČNÍ ŮSEK.
- 2) VODOROVNÉ DÉLKY (NAPŘ. "DÉLKA ZDI") MĚŘENY V NÁJEZDOVÉ HRANĚ ŘÍMSY (= V RUBU DŘÍKU) ZDI.
- 3) STANIČENÍ MĚŘENO V OSE KOMUNIKACE.
- 4) ROZDÍL STANIČENÍ A DÉLKY V NÁJEZDOVÉ HRANĚ ŘÍMSY ZDI SE V DŮSLEDKU PŮDORYSNÉHO ZAKŘIVENÍ LIŠÍ.
- 5) KÓTY VÝŠKY ZDI VE VNĚJŠÍM LÍCI, T.J. MEZI SPODKEM ZÁKLADU A VYŠŠÍM OKRAJEM ŘÍMSOVÉ ČÁSTI.

ZEĎ 25 – TYPICKÝ PŘÍČNÝ ŘEZ 1:50

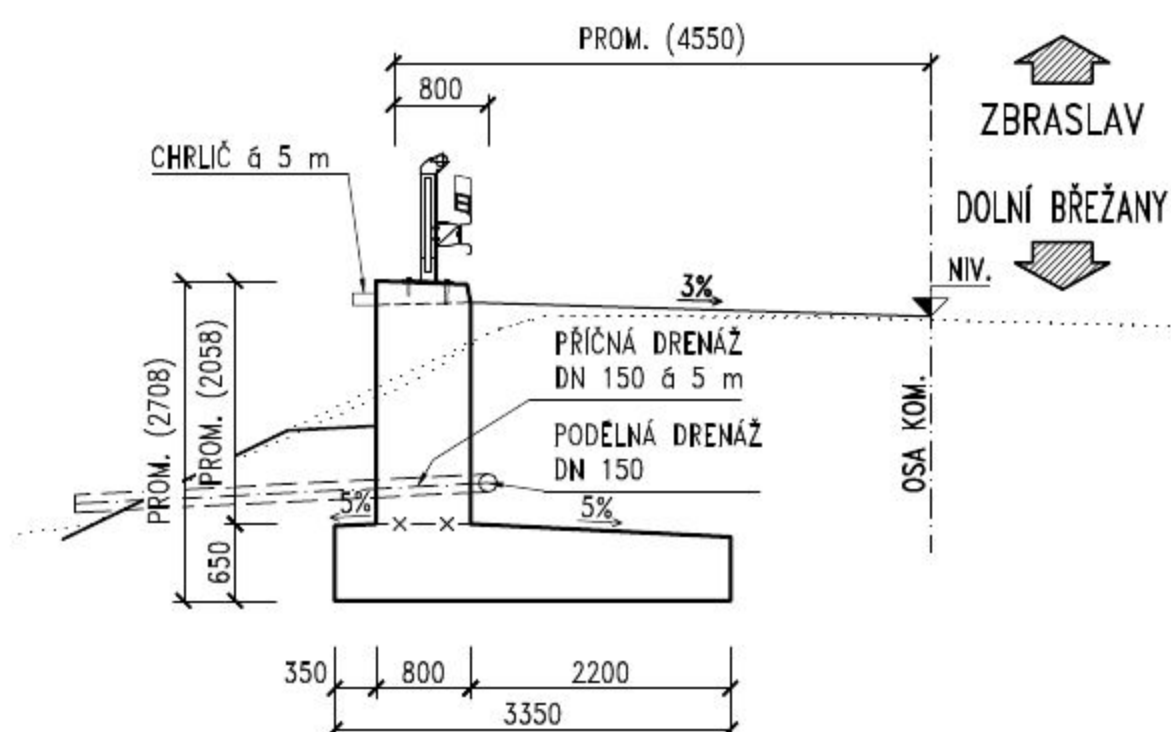

ZMENŠENO NA 50 %

ČÁST 2

VÝŠKOVÝ SYSTÉM BpV SOUŘADNICOVÝ SYSTÉM S-JTSK

Objednatel:

K SÚS
KRAJSKÁ SPRÁVA A ÚDRŽBA SILNIC
Středočeský územní úřad

Krajská správa a údržba silnic
Středočeského kraje, příspěvková organizace
Zborovská 81/11, 150 21 Praha 5 - Smíchov

Zhotovitel:

GeoTec GS

GeoTec-GS, a.s.
Chmelová 2920/6, 106 00 Praha 10
tel.: +420 271 750 710
e-mail: praha@geotec-gs.cz

Vypracoval: Ing. Lukáš PROCHÁZKA	Odpovědný projektant: Ing. Pavel HRDINA	Schválil: Mgr. Filip DUDÍK	Číslo zakázky: 2017 - 395
Podpis: <i>Procházka</i>	Podpis: <i>Hrdina</i>	Podpis: <i>Dudík</i>	Datum: 04/2024

Název akce: II/101 Dolní Břežany - Zbraslav	Měřítko: Stupeň: PDPS	Formát: Paré č.:
Objekt: TVAR ZDI – ZEĎ Č. 25	Příloha: D.1.2.1 7-25	