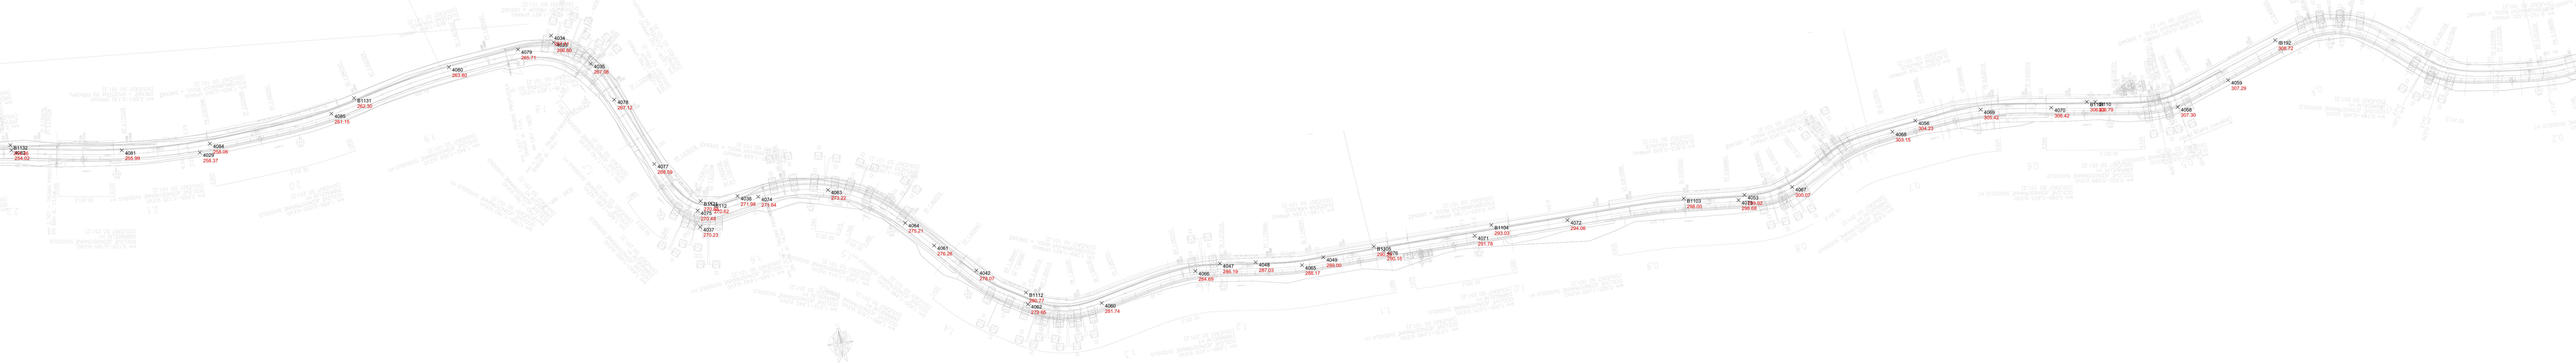

4001
0.00
4002
203.08
4003
203.96
B1161
207.12
4004
209.18
4005
211.43
4099
211.25
4098
214.32
4007
B1175
215.88
4008
218.81
4097
218.62
4009
221.16
4096
221.63
4010
223.27
4095
224.37
4011
225.41
4012
4094
227.36
4093
229.69
B1141
232.90
4014
233.83
4015
235.91
B114
4016
0.00
237.69
4017
237.62
4091
237.72
4018
239.85
4090
239.65
4020
241.75
5089
241.85
4022
244.27
4088
245.14
B1133
4086
247.52
4024
249.31
4087
249.53
4025
250.22
4026
251.10
4027
4083
253.00
B1132
4082
254.02
4081
255.99
4029
258.37
4084
258.06
3,8
3,6
3,5
3,4
3,3
3,2
3,1
3,0
2,9
2,8
2,7
2,5
2,3
2,2
2,1
2,0
SO 251.2
km 3,625–3,736 VPRAVO DRENÁŽ – VYÚSTĚNÍ DO UV (SOUČÁST SO 101.2)
km 3,447–3,736 VPRAVO PODOBRUBNÍKOVÝ RIGOL (SOUČÁST SO 101.2)
km 3,446–3,625 VPRAVO DRENÁŽ – VYÚSTĚNÍ DO HV (SOUČÁST SO 101.2)
km 3,331–3,446 VPRAVO ZPEVNĚNÝ PŘÍKOP (SOUČÁST SO 101.2)
km 3,670–3,753 VLEVO OCELOVÉ JEDNOSTRANNÉ SVODIDLO H1 (SOUČÁST SO 101.2)
km 3,625–3,670 VLEVO OCELOVÉ JEDNOSTRANNÉ SVODIDLO ZÁBRADELNÍ H1 (SOUČÁST SO 251.2)
km 3,445–3,625 VLEVO OCELOVÉ JEDNOSTRANNÉ SVODIDLO H1 (SOUČÁST SO 101.2)
km 3,625 – TRUBNÍ PROPUSTEK DN600 dl. 9m
km 3,446 – TRUBNÍ PROPUSTEK DN600 dl. 11m
km 3,252 – TRUBNÍ PROPUSTEK DN600 dl. 9,5m
km 2,855 – TRUBNÍ PROPUSTEK DN 800 dl. 17,5m
km 2,835 – SJEZD (S TP 1/400)
km 2,167 – TRUBNÍ PROPUSTEK DN 600 dl. 15,5m

B1132
254.26
4082
254.02
4081
255.99
4029
258.37
4084
258.06
4085
261.15
B1131
262.30
4080
263.80
4079
265.71
4034
267.41
4033
266.60
4035
267.08
4078
267.12
4077
268.59
B1121
270.89
IB112
270.62
4075
270.48
4037
270.23
4038
271.98
4074
271.64
4063
273.22
4064
275.21
4061
276.26
4042
278.07
B1112
280.77
4062
279.65
4060
281.74
4066
284.69
4047
286.19
4048
287.03
4065
288.17
4049
289.00
B1105
290.2
4076
290.15
4071
291.78
B1104
293.03
4072
294.06
B1103
298.00
4053
299.02
4073
298.68
4067
300.07
4068
303.15
4056
304.23
4069
305.42
4070
306.42
B1108
IB110
306.79
4058
307.30
4059
307.29
IB192
308.72