




**TRUBNÍ PROPUSTEK DN600
V KM 1,579135**

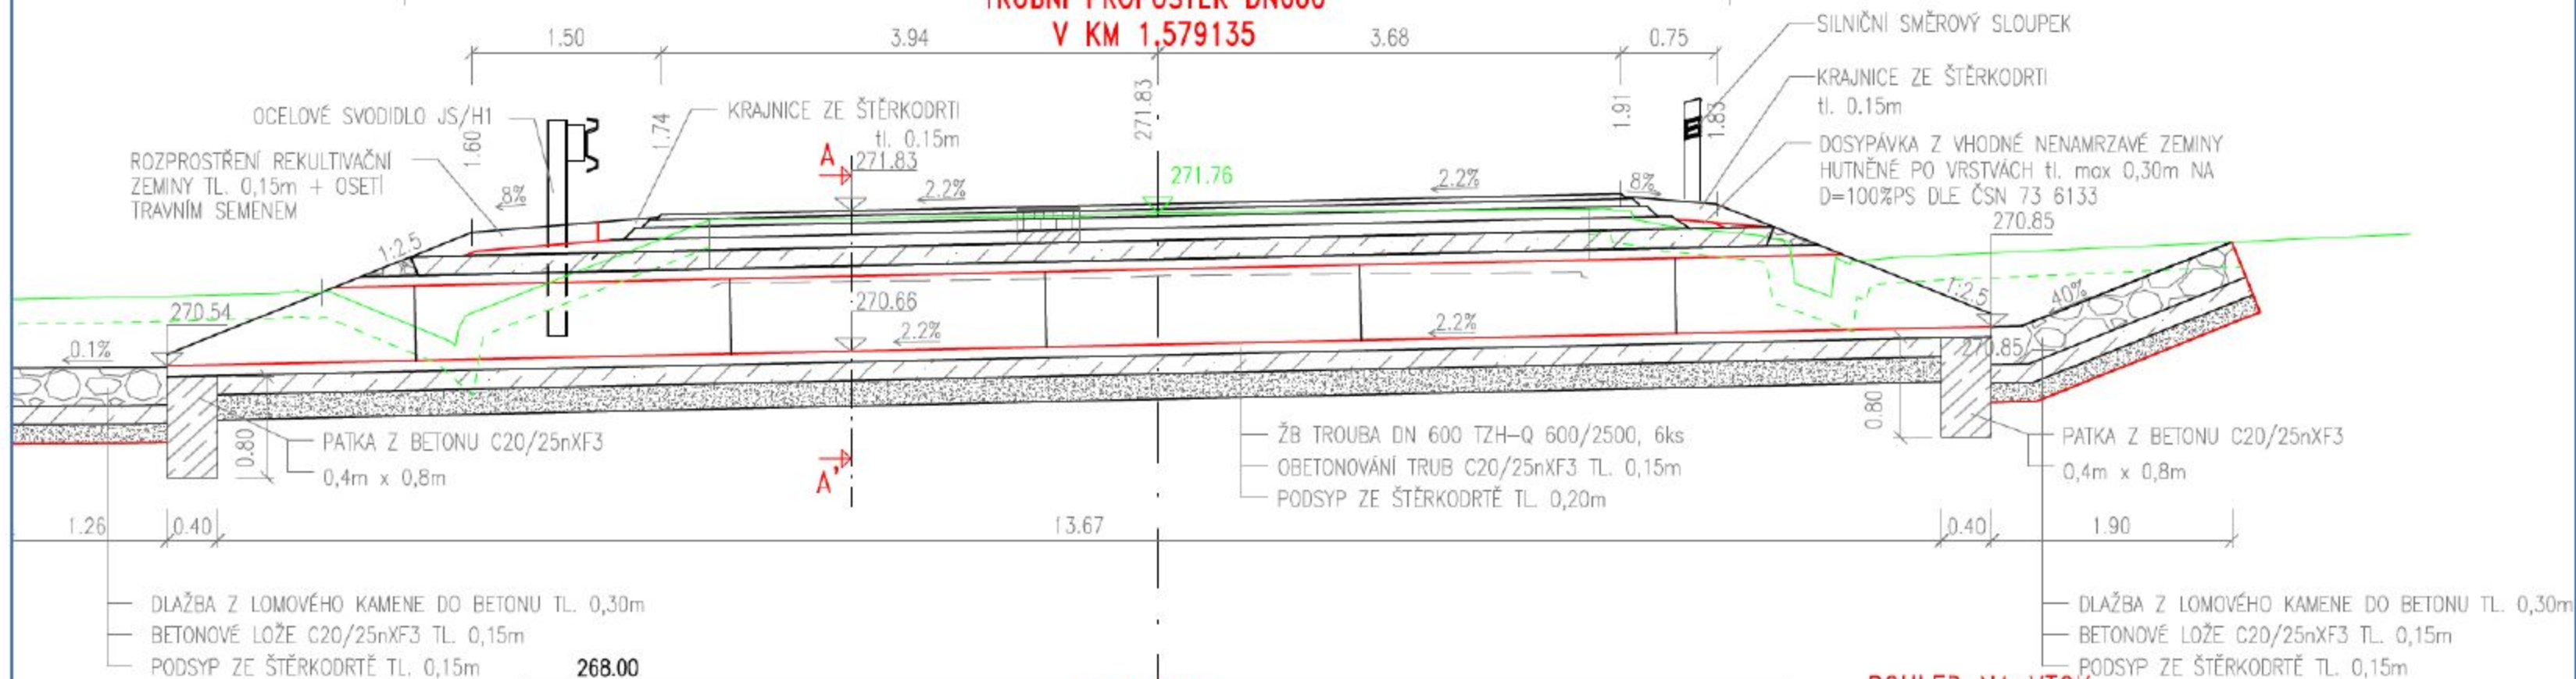

POHLED NA VÝTOK

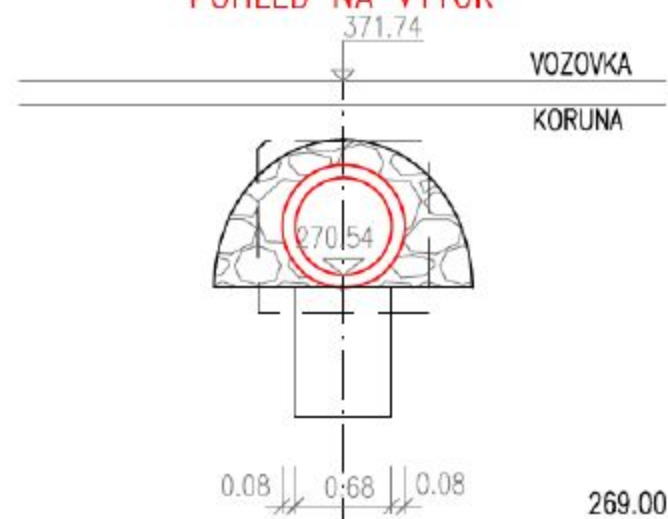

ŘEZ A-A'

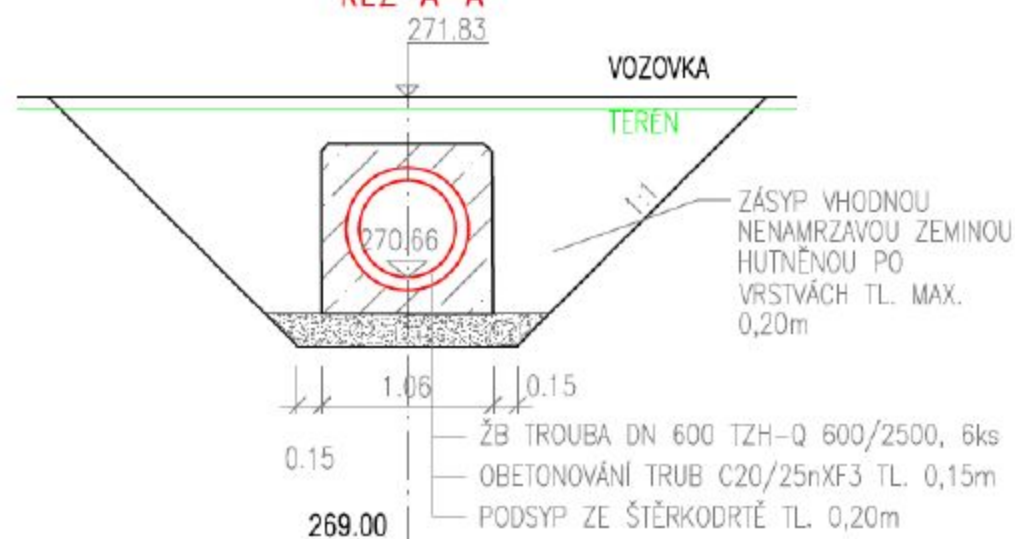

POHLED NA VTOK

