




**TRUBNÍ PROPUSTEK DN600
V KM 2.166836**

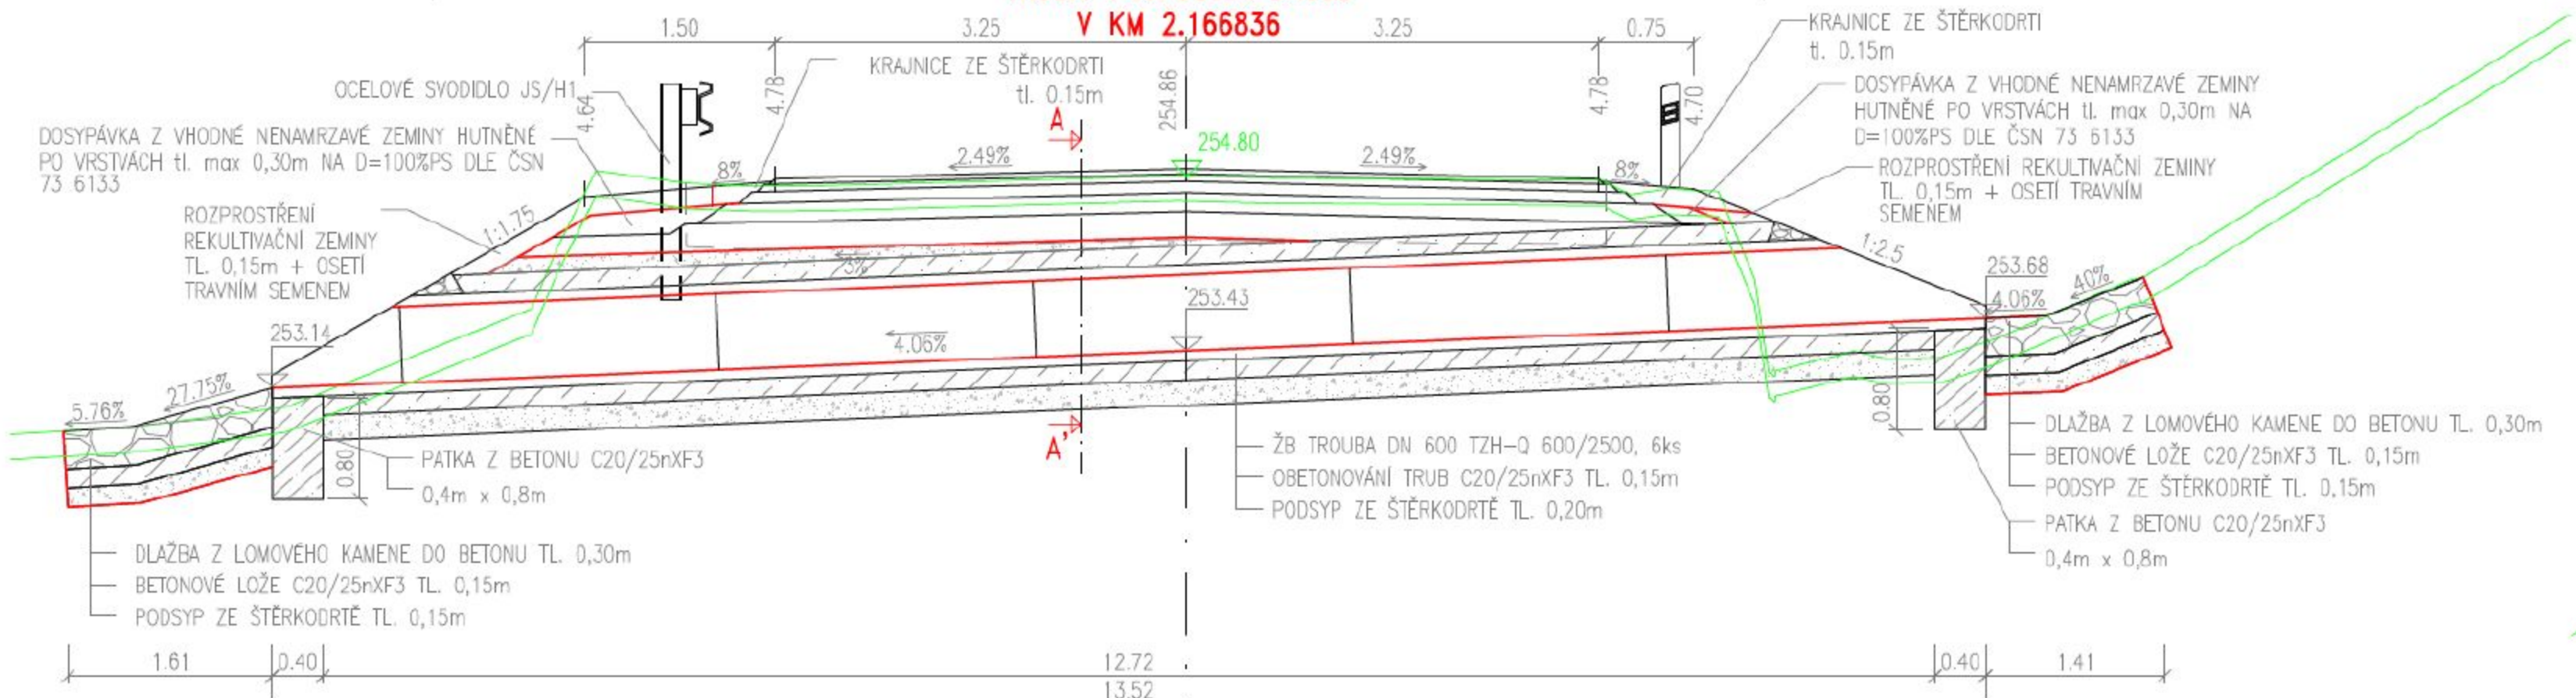

POHLED NA VÝTOK

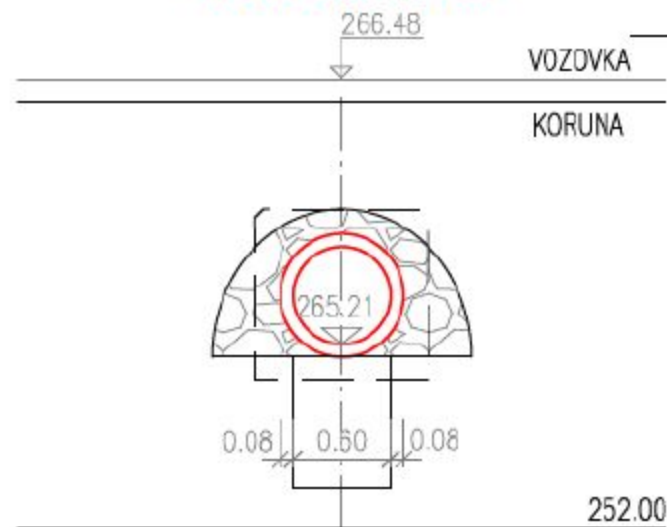

ŘEZ A-A'

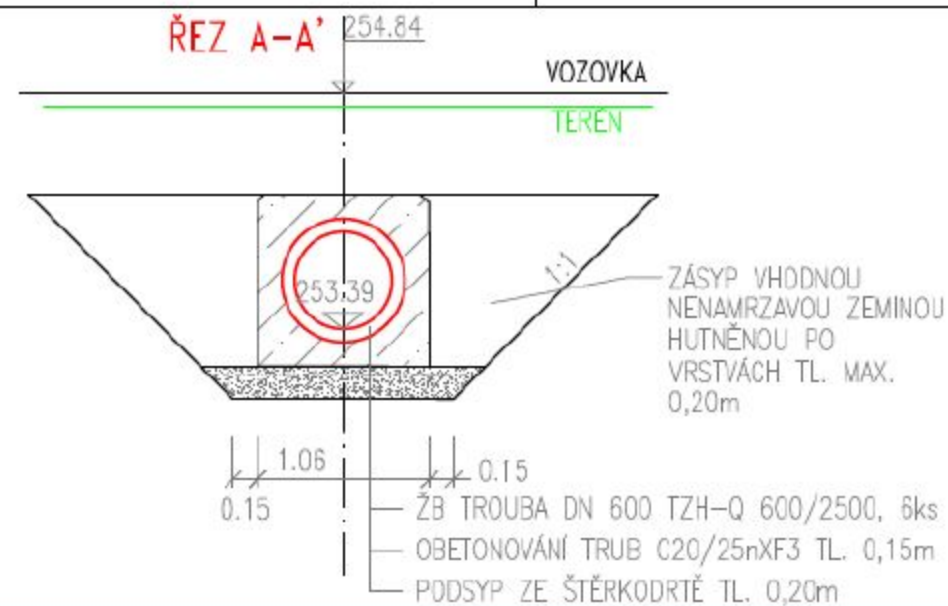

POHLED NA VTOK

